



UNION PACIFIC RAILROAD STRUCTURES SUBMITTAL



VICINITY MAP
NOT TO SCALE

PROJECT LOCATION



PROJECT LOCATION MAP
NOT TO SCALE



IN ASSOCIATION WITH:



383 4th St. Ste. 201
Oakland, CA 94607
T: 925.400.4356
www.jmacivil.com

INDEX TO PLANS


- S-1 RAISED PLATFORM GP No. 1
- S-2 RAISED PLATFORM GP No. 2
- S-3 PEDESTRIAN OVERCROSSING GP
- S-4 PARKING LOT PLATFORM GP
- S-5 INDEX TO PLANS

ELK GROVE, CALIFORNIA SACRAMENTO SUBDIVISION MILE POST 126.87 TO 128.51 ACE TRACK IMPROVEMENT AND ELK GROVE STATION PROJECT

WORK ORDER:
PROJECT NUMBER:
BUDGET REFERENCE:



30% DESIGN
NOT FOR CONSTRUCTION

LAST REVISED
January 10, 2022

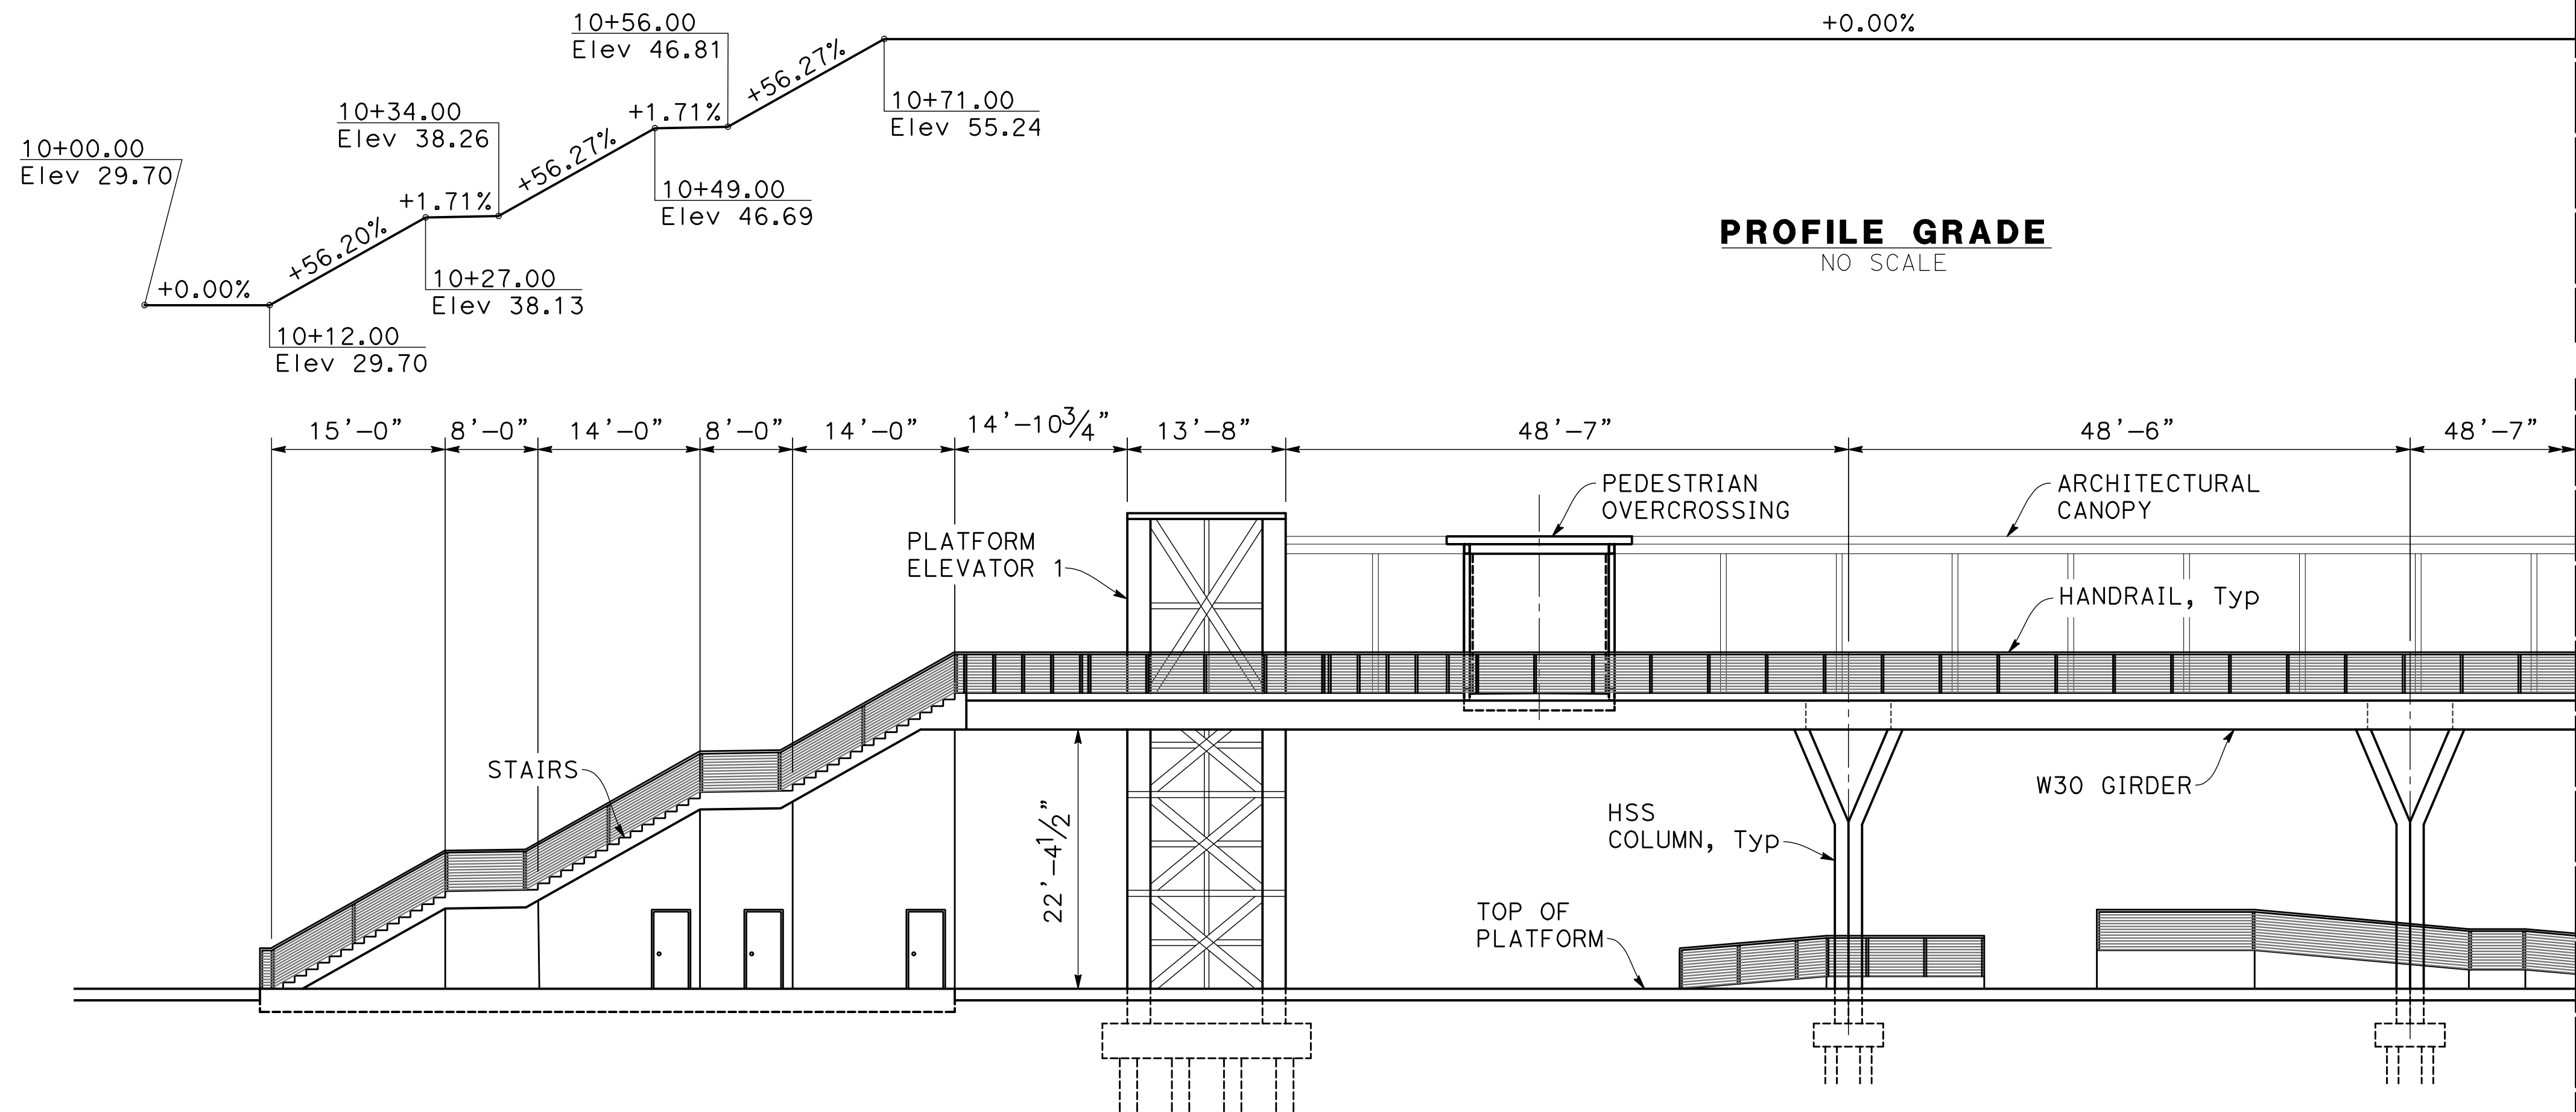

MATCHLINE Sta 12+10.00
SEE SHEET 2 OF 5

MATCHLINE Sta 12+10.00
SEE SHEET 2 OF 5

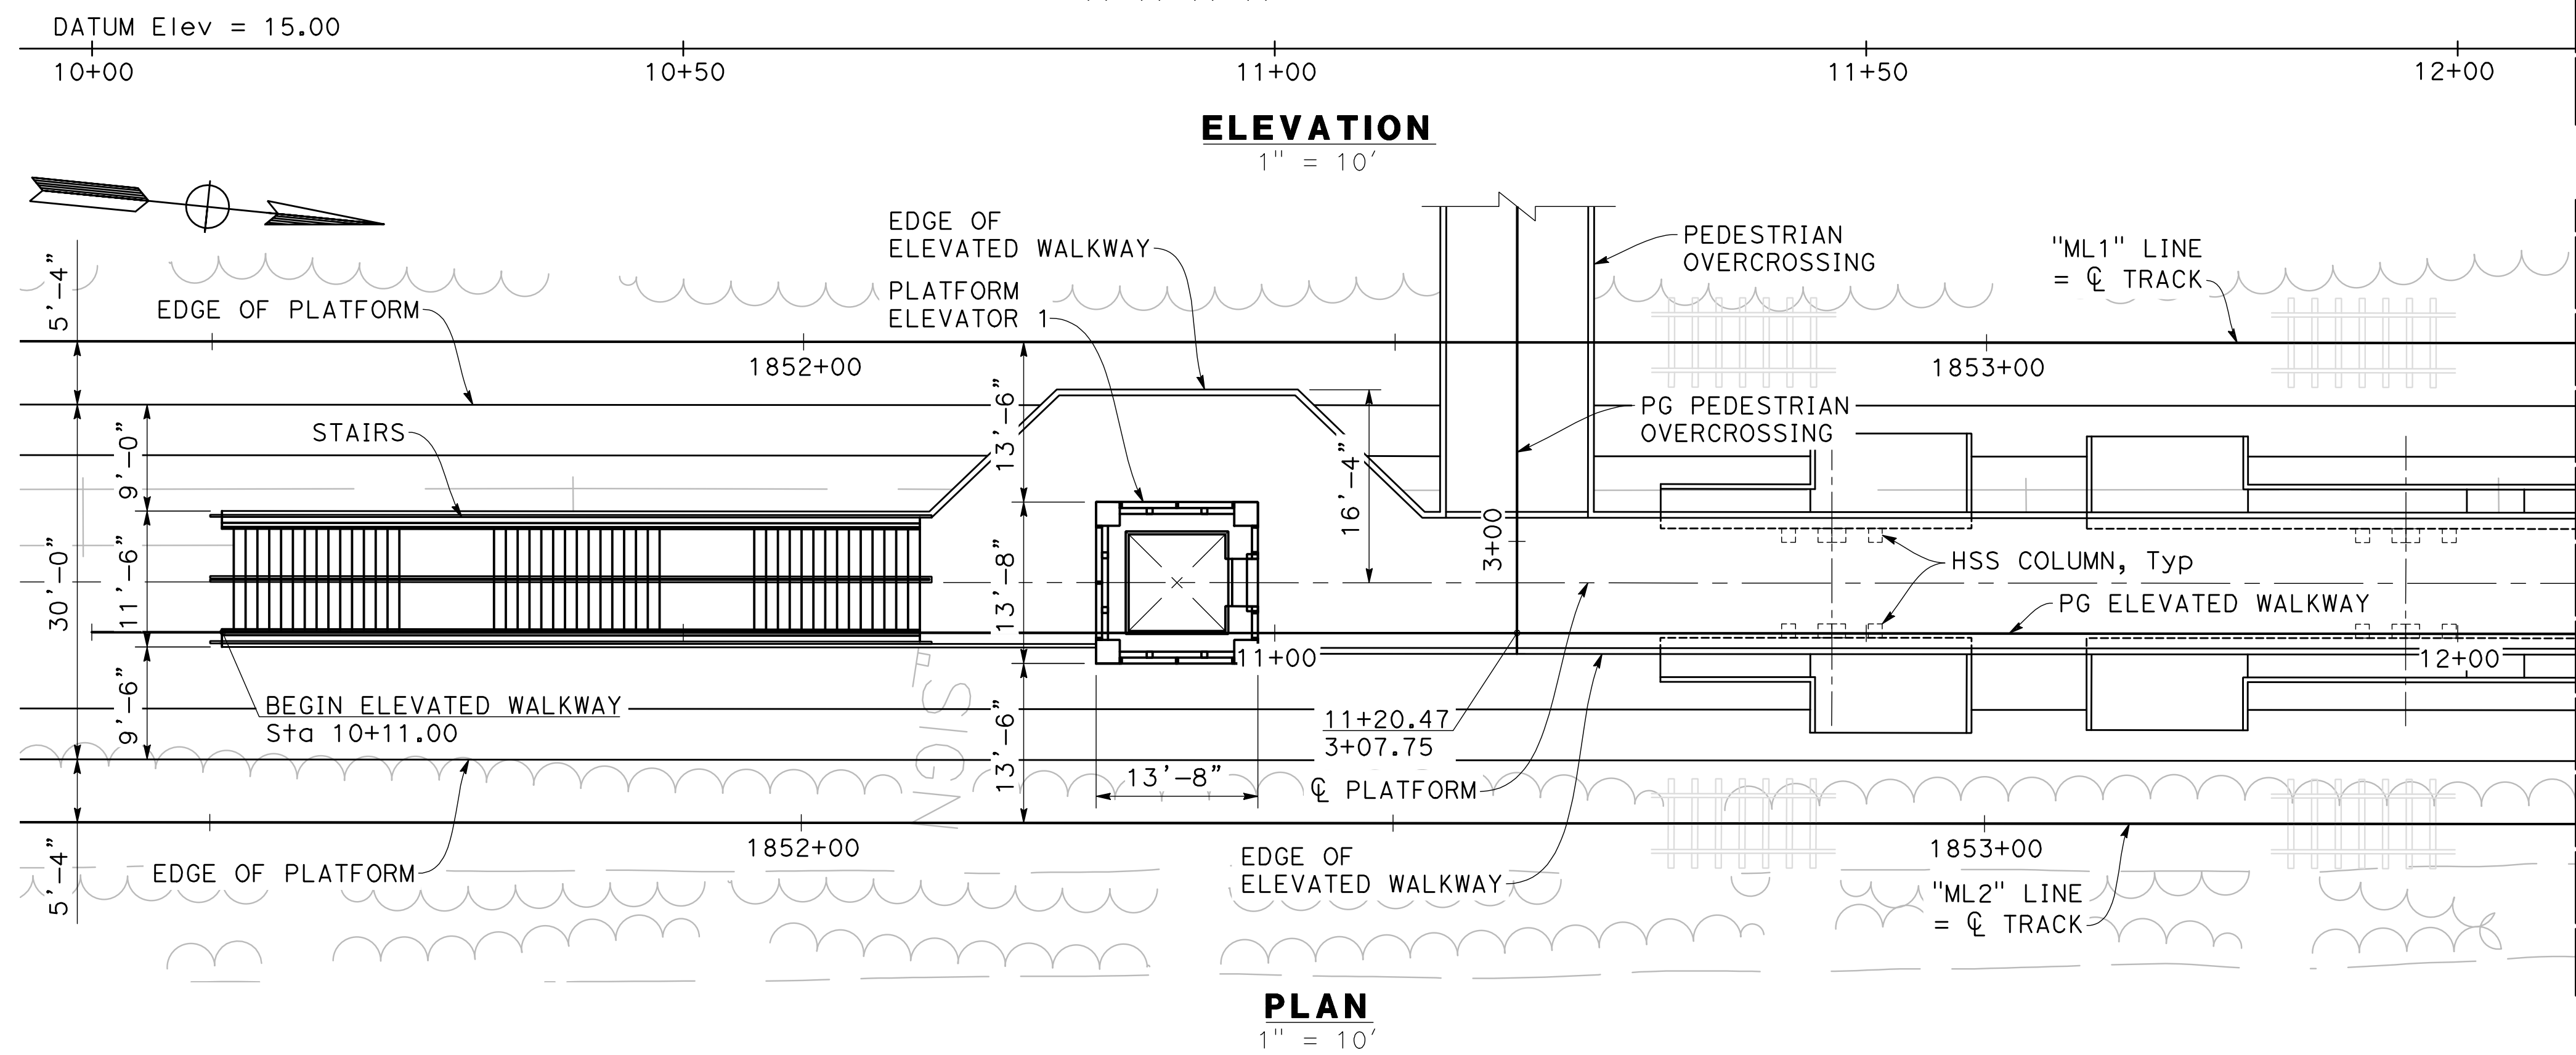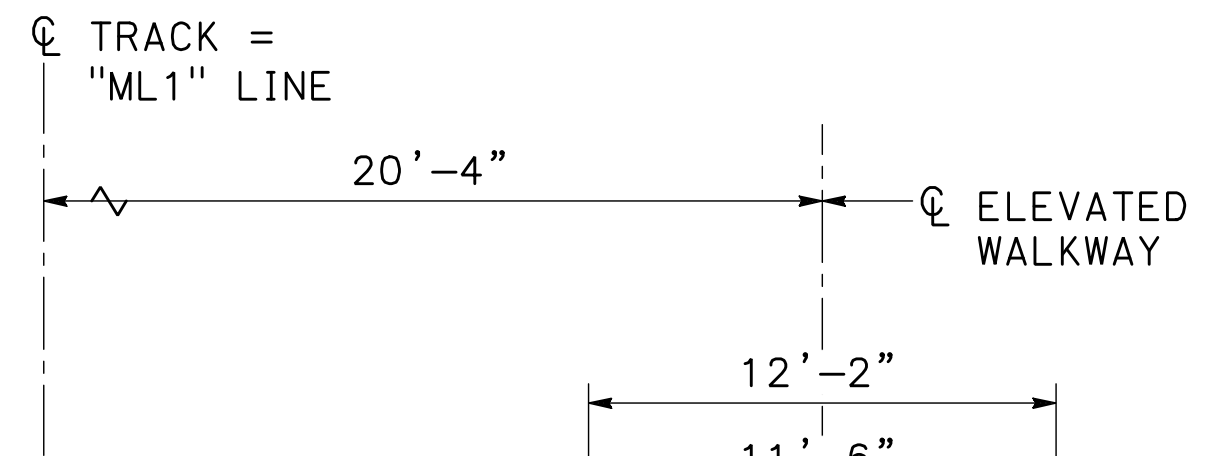


MATCHLINE Sta 12+10.00
SEE SHEET 2 OF 5


**ELEVATED WALKWAY
ALONG PLATFORM
TYPICAL SECTION**
1" = 5'


1 OF 5




REV. #	BY	DATE	DESCRIPTION

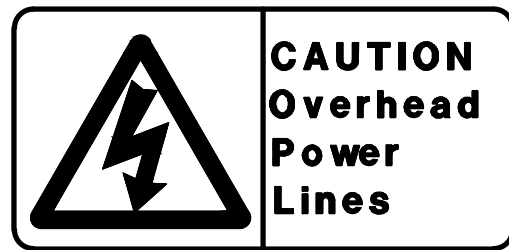

SHEET #: S-1	DOCUMENT TYPE: 30% DESIGN
DRAWN BY: JV	UNION PACIFIC RAILROAD For Use in Agreement with: ACE
CHECKED BY: YR	LOCATION & DESCRIPTION: Elk Grove, CA - Elk Grove Station Project Latitude: 38°25'34"N : Longitude: 121°27'24"W
DATE: 01/07/22	SHEET TITLE: RAISED PLATFORM - GP No. 1
PAGE NUMBER of XX	


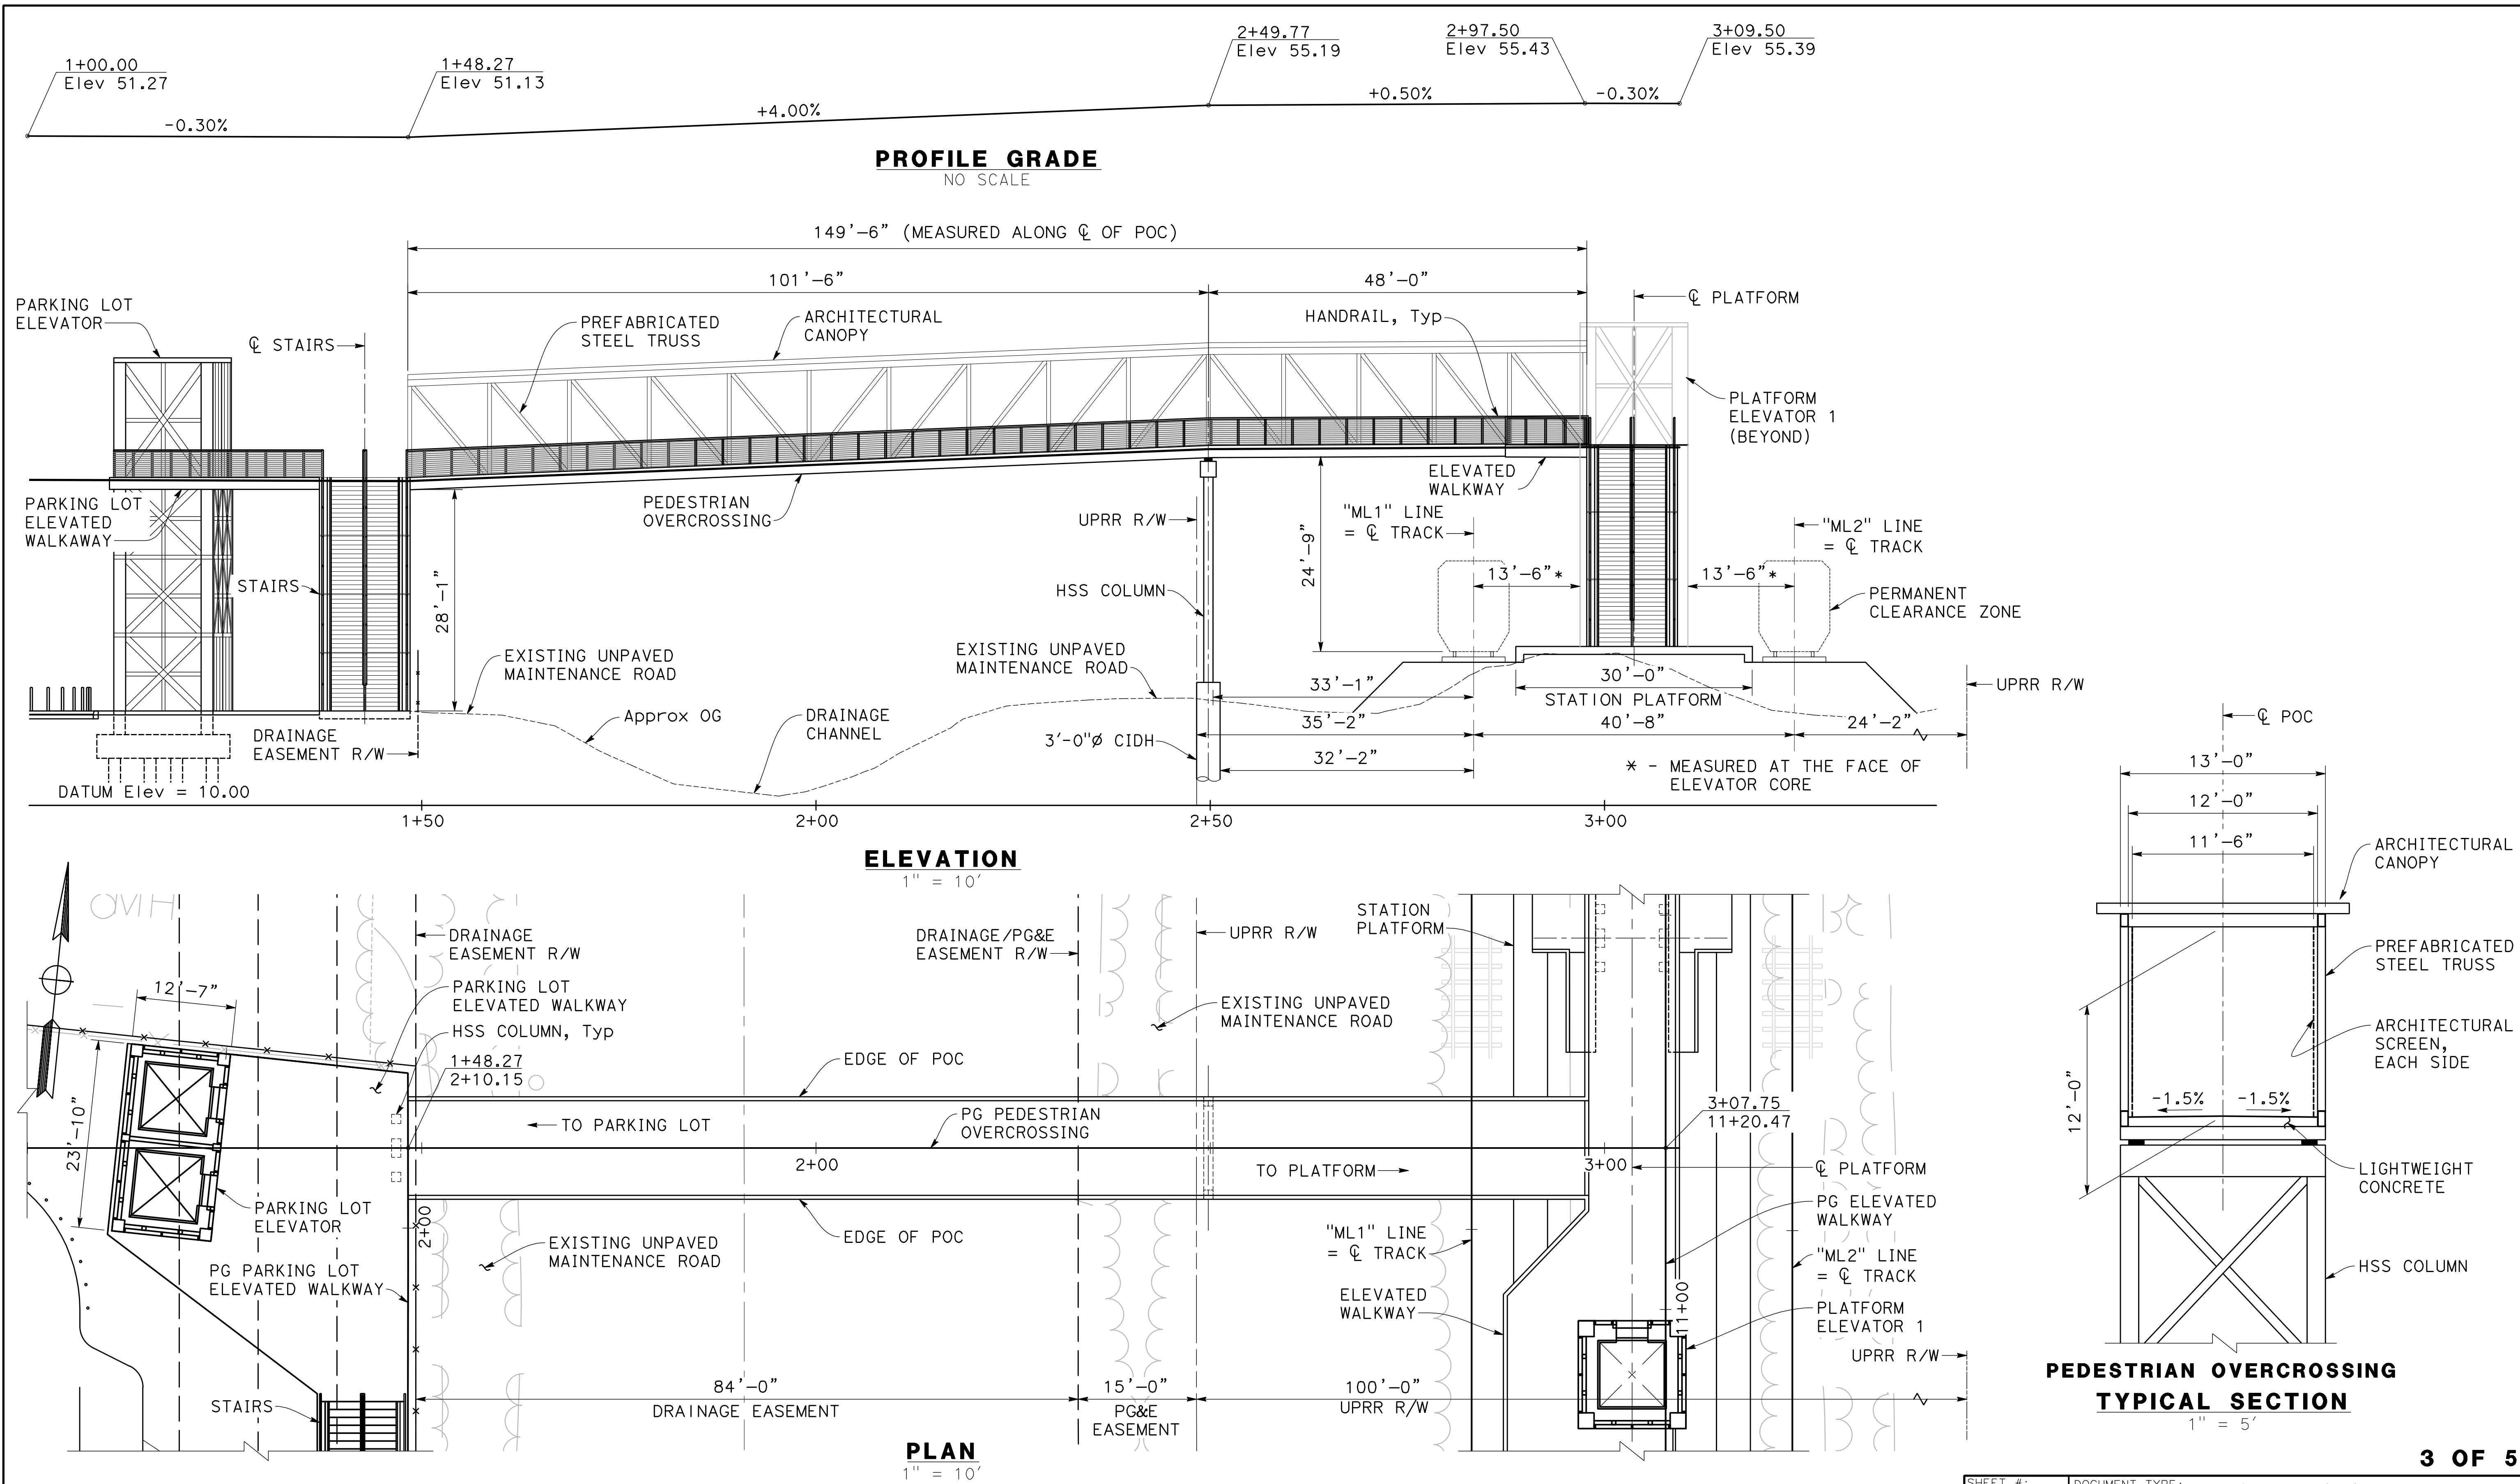


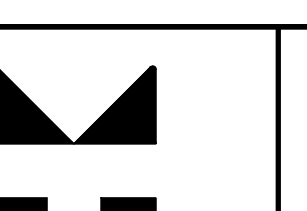				 CALL BEFORE YOU DIG				 ALTAMONT CORRIDOR EXPRESS						SHEET #: S-3		DOCUMENT TYPE: 30% DESIGN	
REV. #	BY	DATE	DESCRIPTION									DRAWN BY: JV		UNION PACIFIC RAILROAD For Use in Agreement with ACE			
												CHECKED BY: YR					
												DATE: 01/11/22		LOCATION & DESCRIPTION: Elk Grove, CA – Elk Grove Station Project Latitude: 38°25'34"N : Longitude: 121°27'24"W			
												PAGE NUMBER 1 of 1					
														SHEET TITLE: PEDESTRIAN OC - GENERAL PLAN			

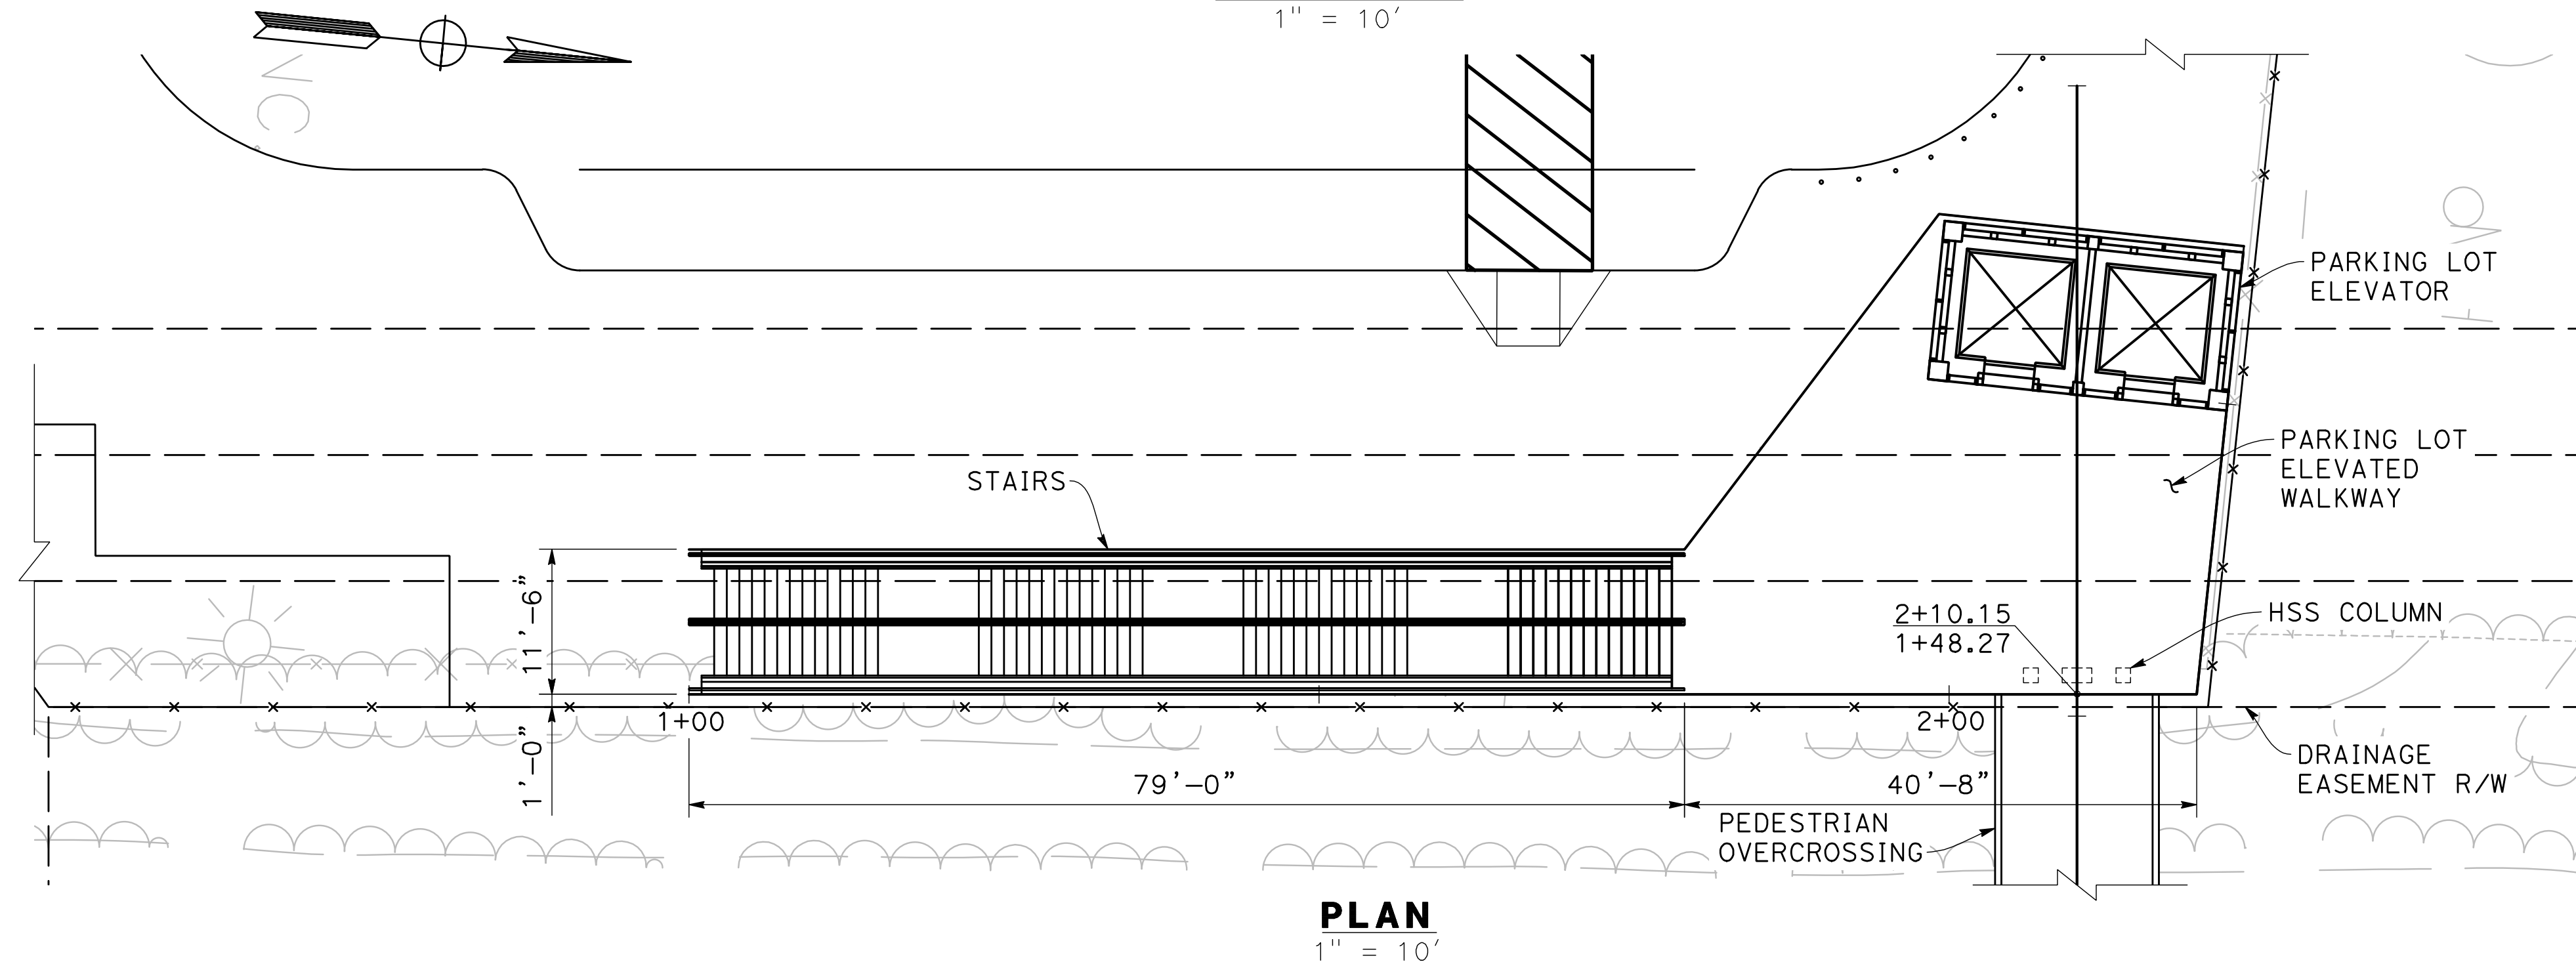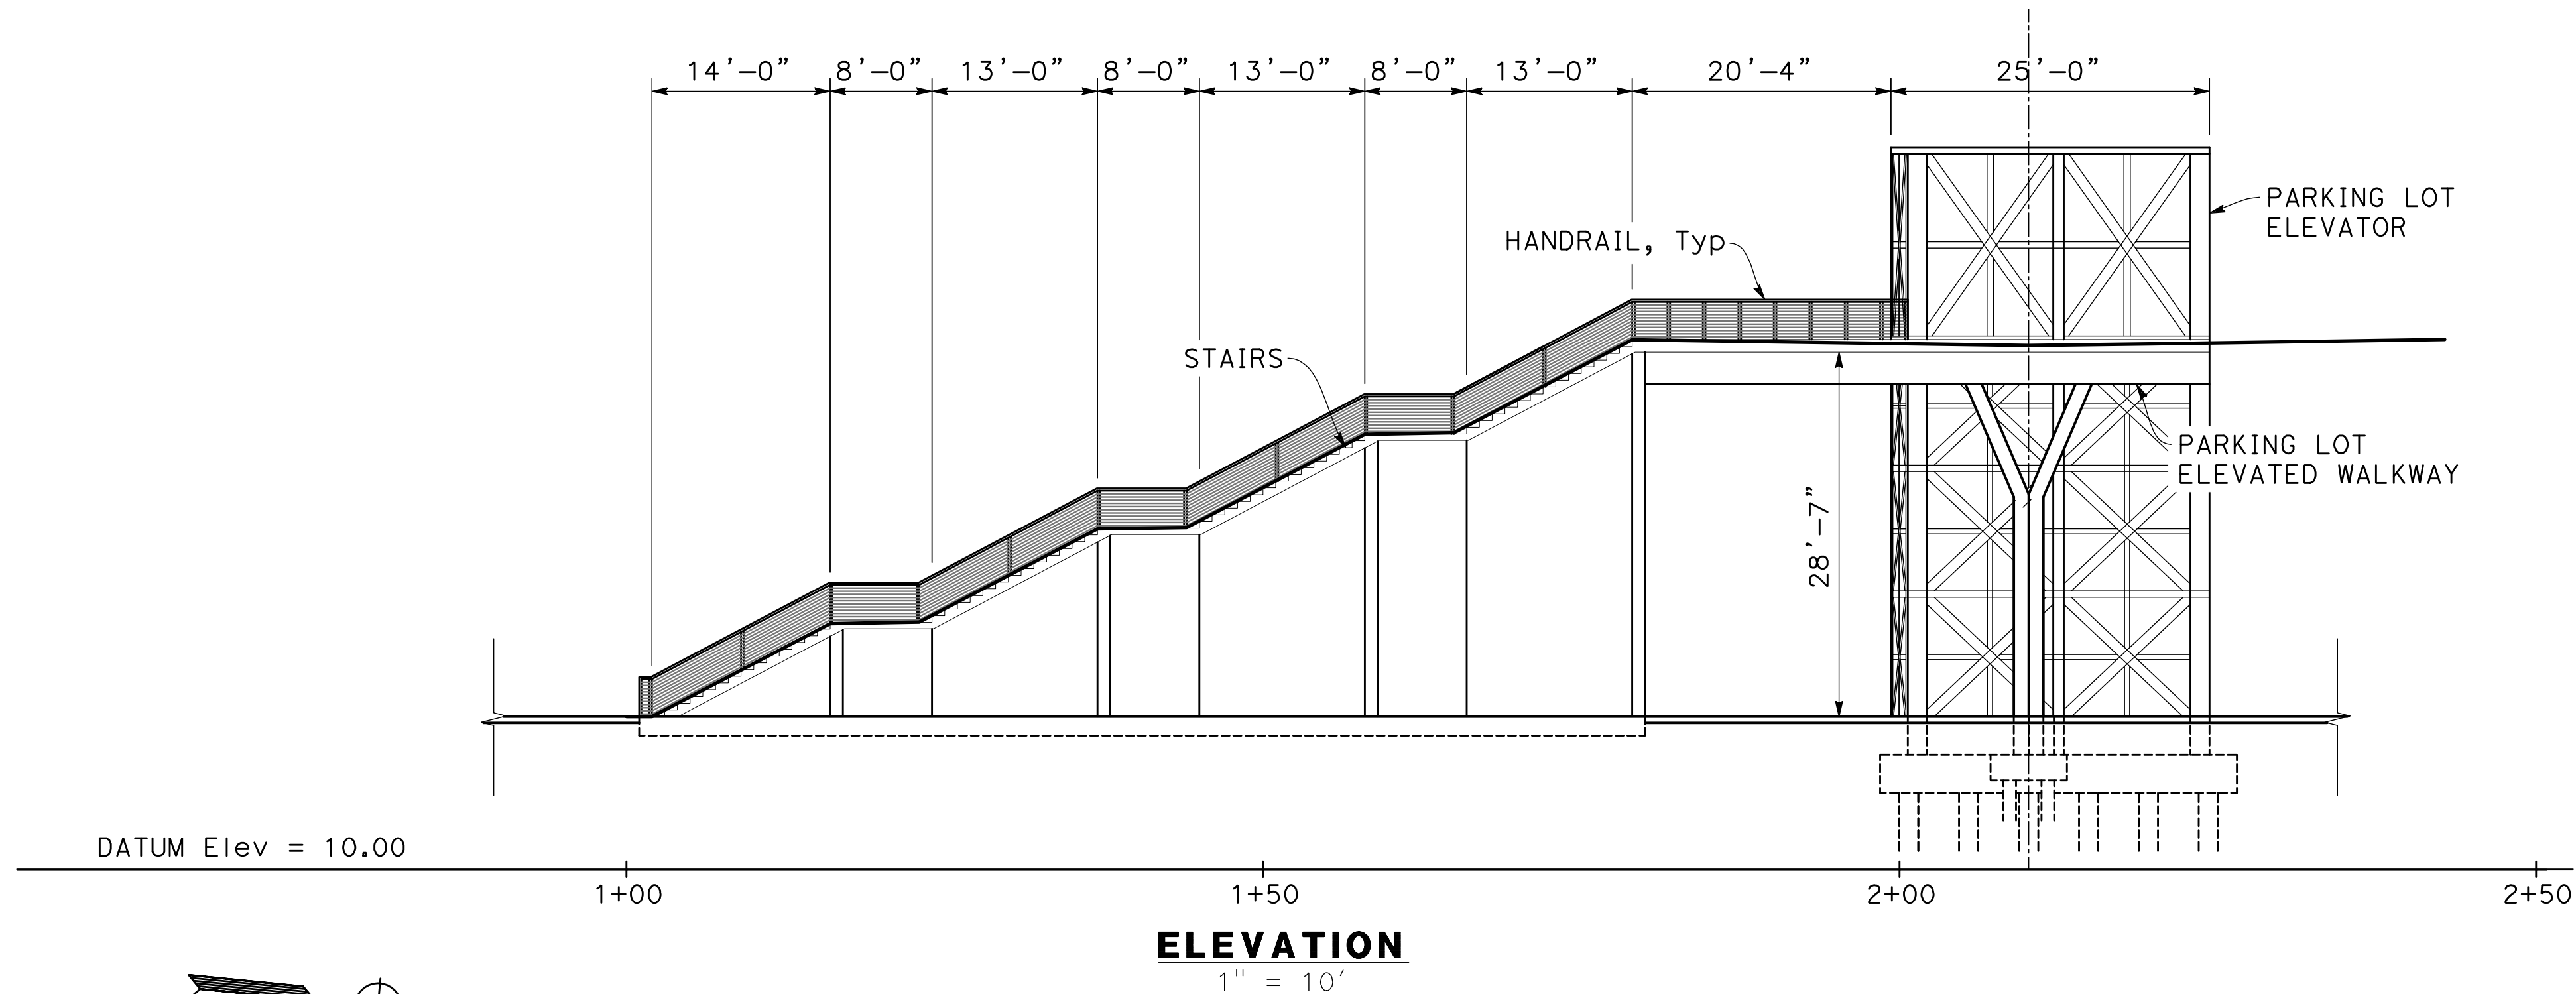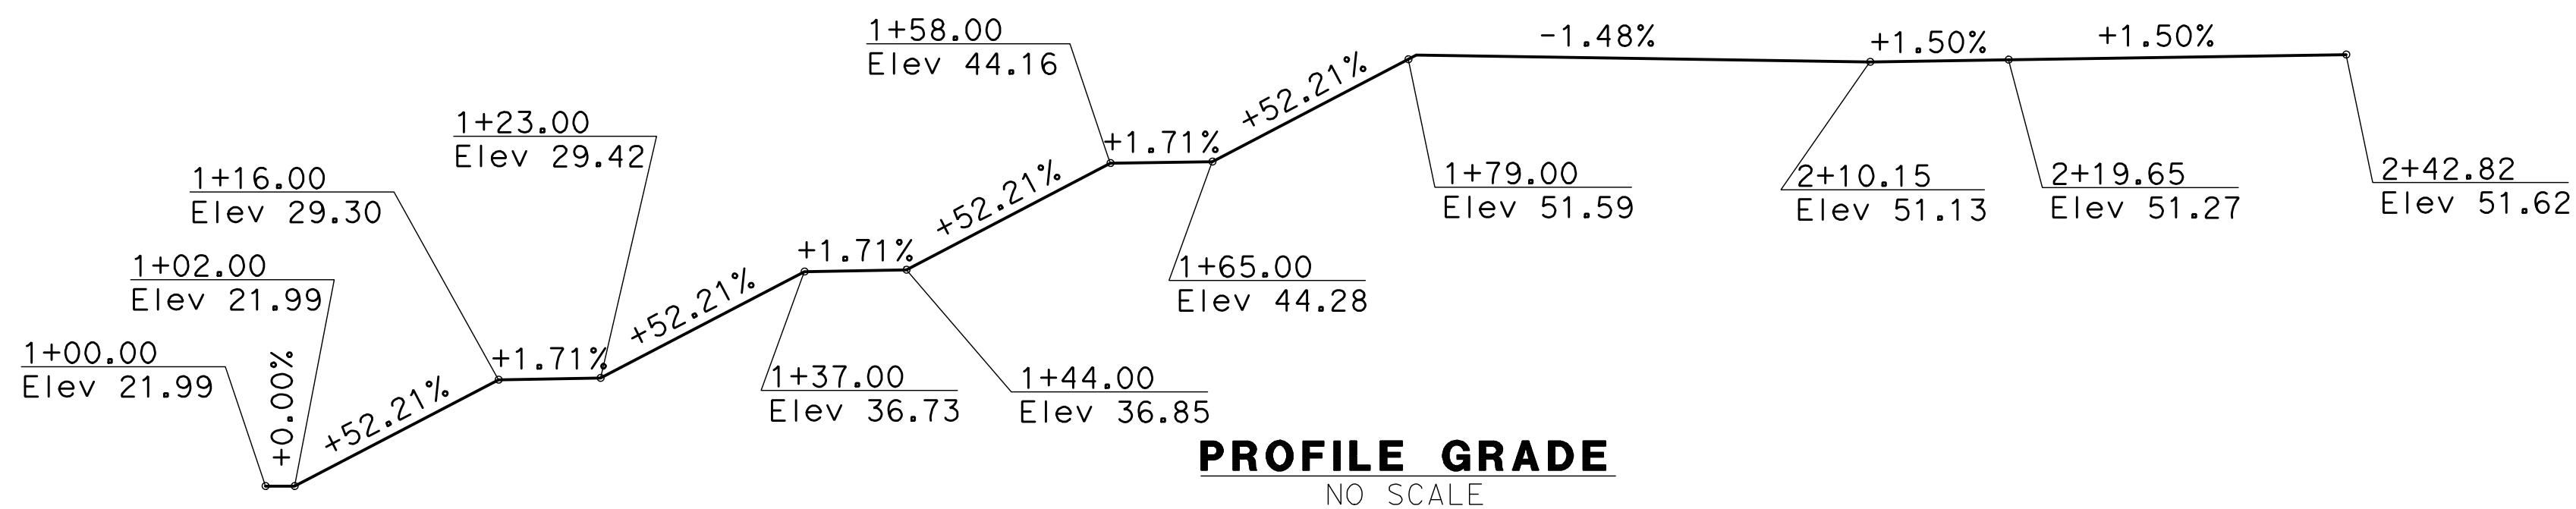

4 OF 5

REV. #	BY	DATE	DESCRIPTION

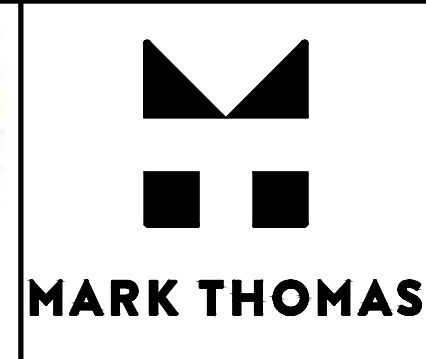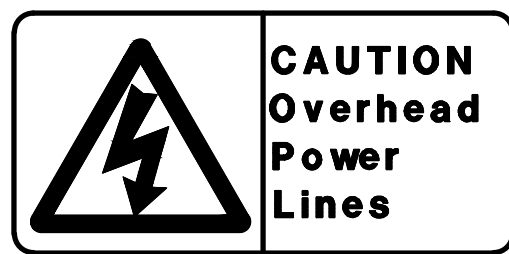

SHEET #: S-4	DOCUMENT TYPE: 30% DESIGN
DRAWN BY: JV	UNION PACIFIC RAILROAD For Use in Agreement with: ACE
CHECKED BY: YR	
DATE: 01/07/22	LOCATION & DESCRIPTION: Elk Grove, CA – Elk Grove Station Project Latitude: 38°25'34"N : Longitude: 121°27'24"W
PAGE NUMBER of XX	SHEET TITLE: PARKING LOT PLATFORM - GP

GENERAL NOTES

1. Railroad requires review and approval of all submittals for shoring, demolition, erection and falsework. No work shall be allowed prior to written railroad approval. Allow a minimum of 45 days for the review and approval of each submittal unless specified otherwise in the contract special provisions.
2. The elevation of the existing top-of-rail profile shall be verified before beginning construction. All discrepancies shall be brought to the railroad authority for approval prior to beginning any construction activities.
3. The contractor must submit a proposed method of erosion and sediment control within the railroad Right-Of-Way and have the method approved by the railroad.
4. All shoring systems that impact the Railroad's operations and/or support the railroad's embankment shall be designed and constructed per current Railroad Guidelines for Temporary shoring.
5. All demolitions within the railroad Right-Of-Way and/or demolition that may impact the railroad's tracks or operations shall be in compliance wit the Railroad's Demolition Guidelines.
6. All construction phases that may impact the railroad's normal operation shall be designed to cause no interruption to the railroad operation. Any train traffic interruption closure shall require prior railroad approval in writing.
7. All permanent clearances shall be verified prior to completion of the project.
8. For all railroad coordination during construction refer to the railroad's special provisions within the Contract Special Provisions documents and the approved Construction and Maintenance (C & M) Agreement.
9. Railroad requirements do not allow work within 50 feet of track centerline when a train passes the work site and all personnel must clear the area within 25 feet of the track centerline and secure all equipment.
10. UPRR Monitoring Program and Contingency Plans must be submitted and approved prior to work.

CALTRANS STANDARD PLANS DATED 2018 EDITION

TBD

STANDARD PLAN SHEET No.

DETAIL No.

PLAN SYMBOLS

A

Indicates Section Identification

Indicates Temporary Shoring

ABBREVIATIONS

- Embed – Embedment
- UPRR – Union Pacific Railroad
- T/R – Top of Rail
- TOC – Top of Curb

GENERAL NOTES
LOAD AND RESISTANCE FACTOR DESIGN

DESIGN: AREMA Manual for Railway Engineering, 2019
UPRR-BNSF Guidelines for Railroad Grade Separation Projects, 2015
UPRR-BNSF Guidelines for Temporary Shoring, 2004

AASHTO LRFD Bridge Design Specifications, 8th Edition with California Amendments, preface dated April 2019.

LIVE LOADING: 90 PSF pedestrian live load
REINFORCED CONCRETE: fy = 60 ksi
 f'c = 4.0 ksi


STRUCTUAL STEEL (new construction):
ASTM A709 Grade 50
A325 HS bolts
All bolted connections are slip
critical unless otherwise noted.
Class B faying surfaces.

SHORING: Temporary shoring shall be in compliance with UPRR-BNSF Guidelines for Temporary Shoring, 2021, with updated shoring zone diagram including design variance.

TOP OF RAIL ELEVATIONS

TBD

STATION	ELEVATIONS	
	JMA ML1	JMA ML2

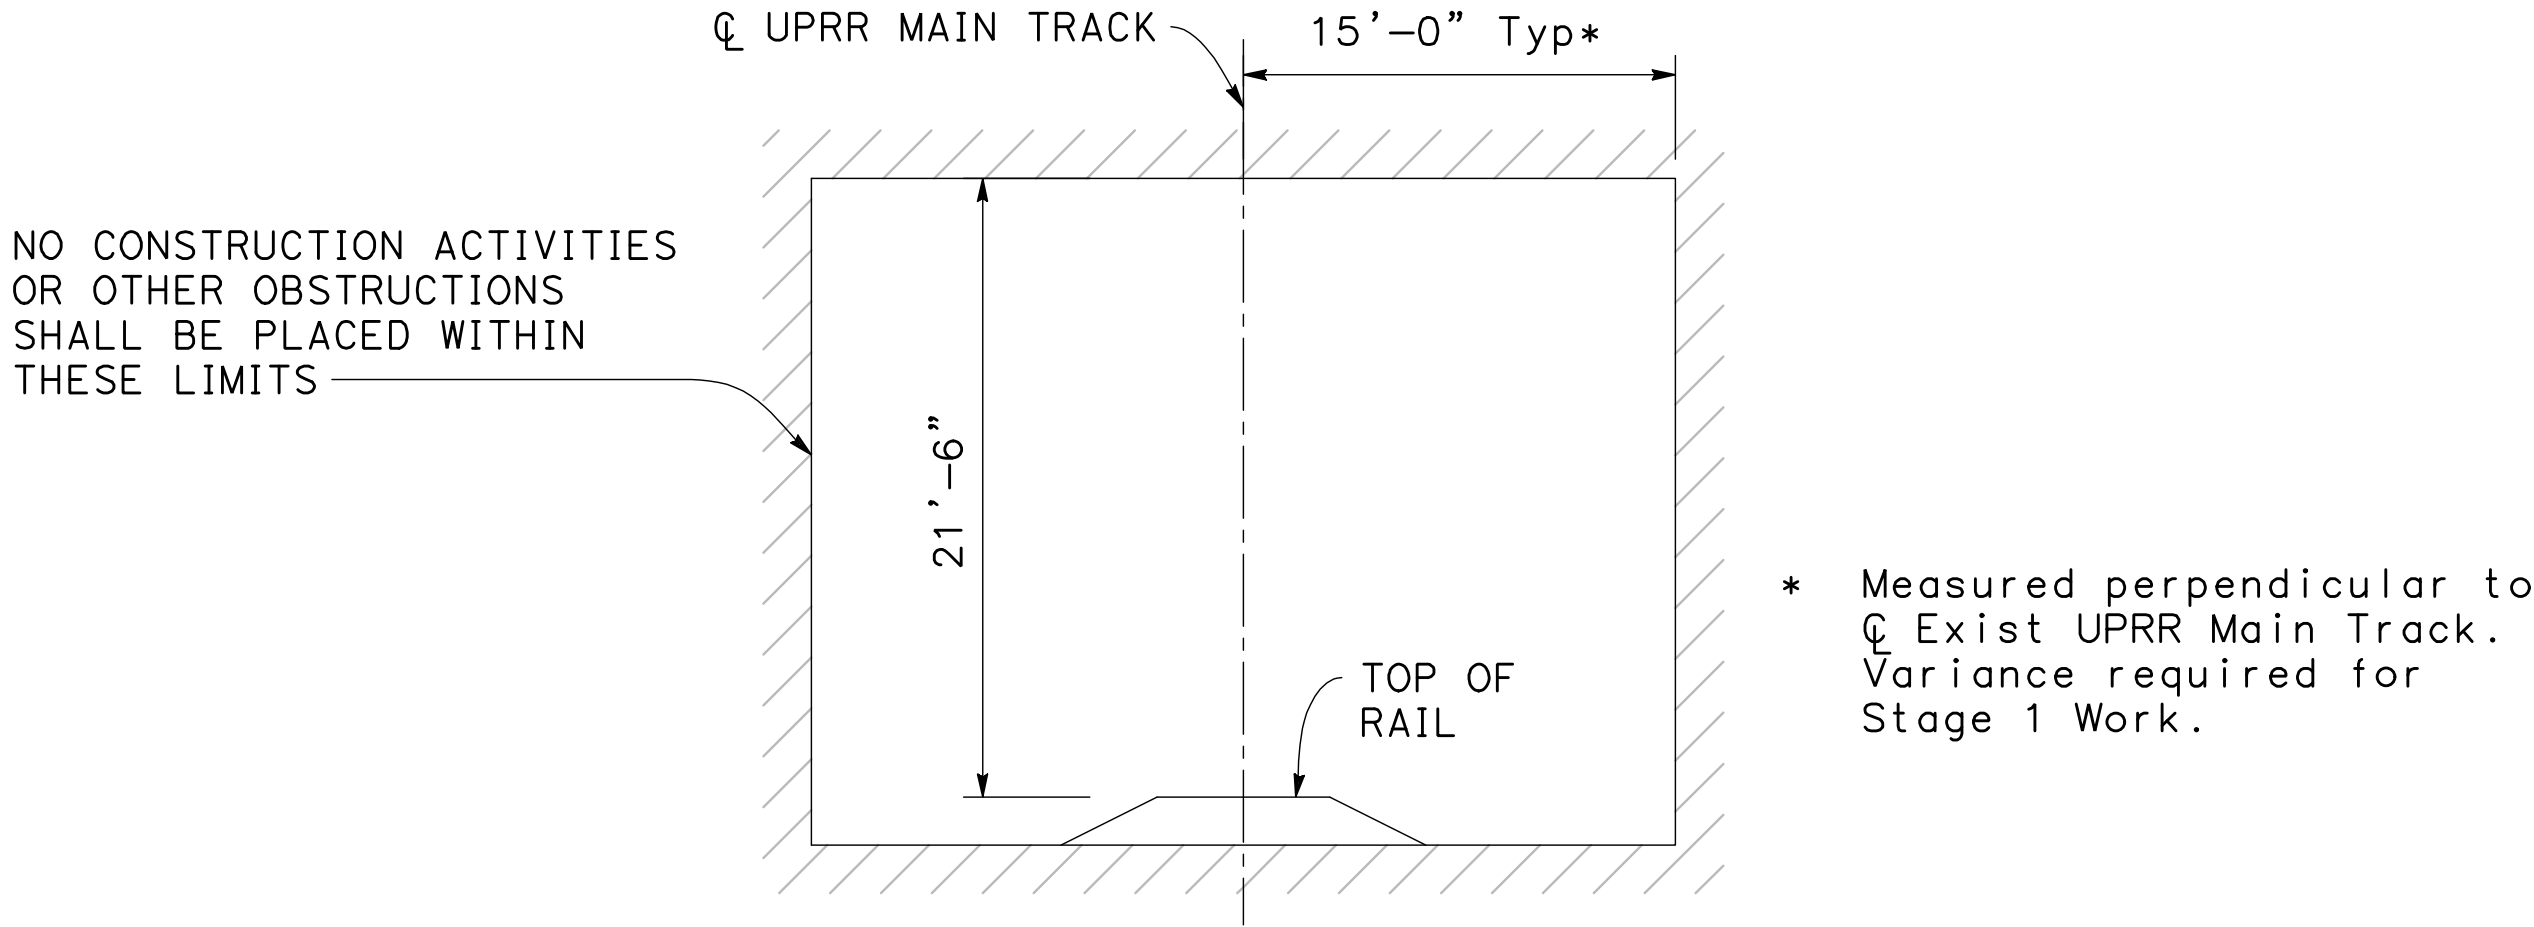

MINIMUM TEMPORARY CONSTRUCTION
CLEARANCE DIAGRAM

NO SCALE

REV. # BY DATE DESCRIPTION				811 CALL BEFORE YOU DIG		CAUTION Overhead Power Lines		ACE ALTAMONT CORRIDOR EXPRESS		MARK THOMAS		UNION PACIFIC		SHEET #: S-5 DOCUMENT TYPE: 30% DESIGN	
														DRAWN BY: JV CHECKED BY: YR	
														UNION PACIFIC RAILROAD For Use in Agreement with: ACE	
														LOCATION & DESCRIPTION: Elk Grove, CA – Elk Grove Station Project Latitude: 38°25'34"N : Longitude: 121°27'24"W	
														DATE: 01/07/22 PAGE NUMBER of XX SHEET TITLE: INDEX TO PLANS	