
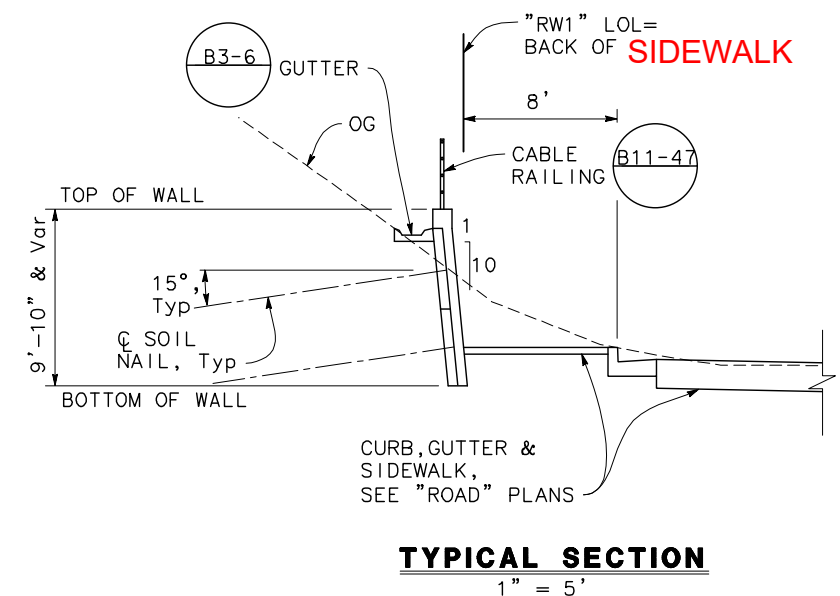
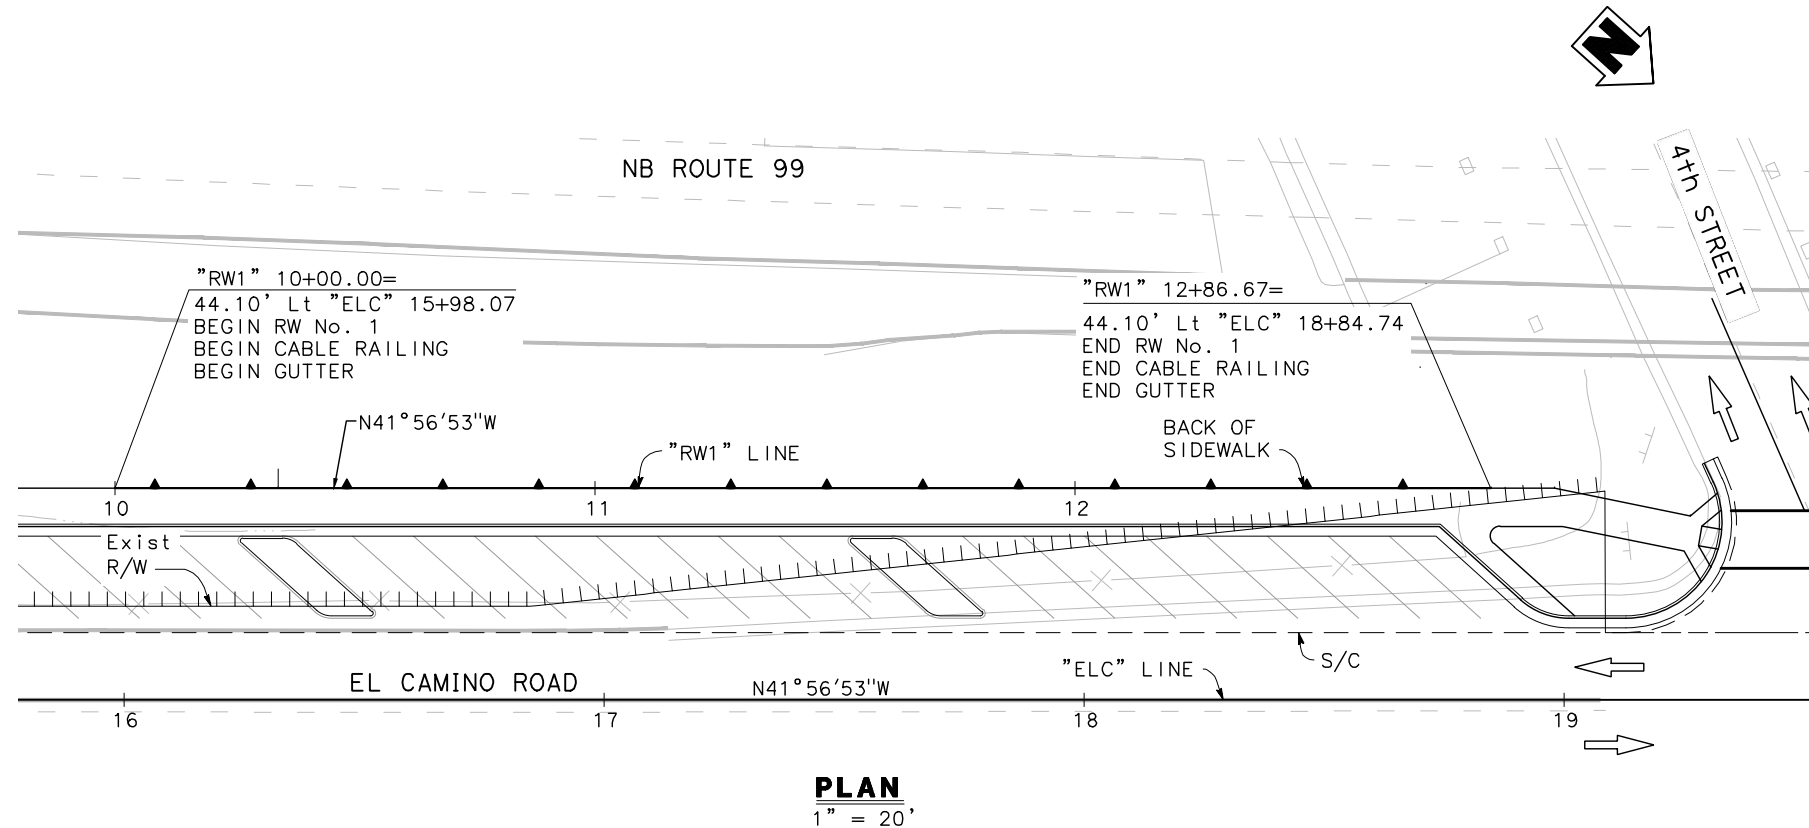



| Dist | COUNTY | ROUTE | POST MILES<br>TOTAL PROJECT | SHEET<br>No. | TOTAL<br>SHEETS |
|------|--------|-------|-----------------------------|--------------|-----------------|
| 10   | Sta    | 99    | R11.50/R11.74               |              |                 |

|   |                                                                                     |
|---|-------------------------------------------------------------------------------------|
| REGISTERED STRUCTURAL ENGINEER   | DATE                                                                                |
| PLANS APPROVAL DATE   |  |
| <p>THE STATE OF CALIFORNIA OR ITS OFFICERS OR AGENTS SHALL NOT BE RESPONSIBLE FOR THE ACCURACY OR COMPLETENESS OF SCANNED COPIES OF THIS PLAN SHEET.</p> |                                                                                     |

|                                                                            |
|----------------------------------------------------------------------------|
| ALTAMONT CORRIDOR EXPRESS<br>949 EAST CHANNEL STREET<br>STOCKTON, CA 95202 |
| MARK THOMAS<br>701 UNIVERSITY AVENUE, SUITE 200<br>SACRAMENTO, CA 95825    |

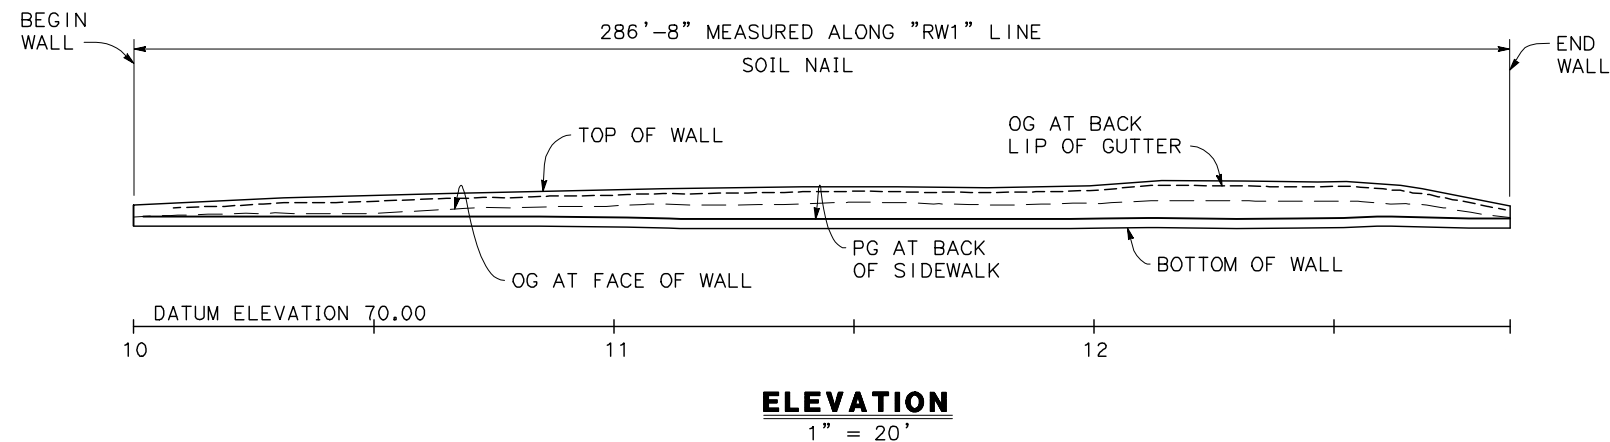

LEGEND:

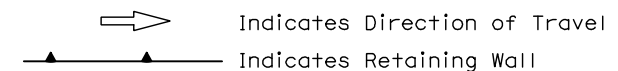

|   |               
|---|---------------|---------------|---------|------------------------------------|----------------|--------------|--------------------------|-------------------------------------------------------------------------|------------------------------------|------------|----------------------|----------------------------------|--|---------------|--|----------------------------------------------------|--|----------------|--|--|--|-------|----|
| DESIGN OVERSIGHT   | DESIGN        | BY<br>Y. REN  | CHECKED | LOAD & RESISTANCE<br>FACTOR DESIGN |                | LIVE LOADING |                          | PREPARED FOR THE<br>STATE OF CALIFORNIA<br>DEPARTMENT OF TRANSPORTATION | E. FREDRICKSON<br>PROJECT ENGINEER | BRIDGE No. | RETAINING WALL No. 1 |                                  |  |               |  |                                                    |  |                |  |  |  |       |    |
|   | DETAILS       | BY<br>J. DOTY | CHECKED | LAYOUT                             | BY             | CHECKED      | 38EXXX1                  |                                                                         |                                    |            |                      |                                  |  |               |  |                                                    |  |                |  |  |  |       |    |
|   | SIGN OFF DATE | QUANTITIES    | BY      | CHECKED                            | SPECIFICATIONS | BY           | PLANS AND SPECS COMPARED |                                                                         |                                    | R11.50     | GENERAL PLAN         |                                  |  |               |  |                                                    |  |                |  |  |  |       |    |
| <div>DATE PLOTTED =&gt; 5/12/2021<br/>FILE =&gt; 01_RW1_GP.dwg</div> <div>TIME PLOTTED =&gt; 5:02 PM<br/>USERNAME =&gt; JDOTY</div> <div>ORIGINAL SCALE<br/>IN INCHES FOR<br/>REDUCED PLANS</div> <div>0123</div> |               |               |         |                                    |                |              |                          |                                                                         |                                    |            |                      | UNIT:<br>PROJECT NUMBER & PHASE: |  | CONTRACT No.: |  | DISREGARD PRINTS BEARING<br>EARLIER REVISION DATES |  | REVISION DATES |  |  |  | SHEET | OF |
|   |               |               |         |                                    |                |              |                          |                                                                         |                                    |            |                      | 1/2/34                           |  |               |  |                                                    |  |                |  |  |  |       |    |

| Dist | COUNTY | ROUTE | POST MILES<br>TOTAL PROJECT | SHEET<br>No. | TOTAL<br>SHEETS |
|------|--------|-------|-----------------------------|--------------|-----------------|
| 10   | Sta    | 99    | R11.50/R11.74               |              |                 |

|   |      |
|---|------|
| REGISTERED STRUCTURAL ENGINEER   | DATE |
| PLANS APPROVAL DATE   |      |
| THE STATE OF CALIFORNIA OR ITS OFFICERS OR AGENTS SHALL NOT BE RESPONSIBLE FOR THE ACCURACY OR COMPLETENESS OF SCANNED COPIES OF THIS PLAN SHEET. |      |

REGISTERED PROFESSIONAL ENGINEER

YING REN

No. S5786


Exp. 12-31-21

STRUCTURAL

STATE OF CALIFORNIA

ALTAMONT CORRIDOR EXPRESS  
949 EAST CHANNEL STREET  
STOCKTON, CA 95202

MARK THOMAS  
701 UNIVERSITY AVENUE, SUITE 200  
SACRAMENTO, CA 95825

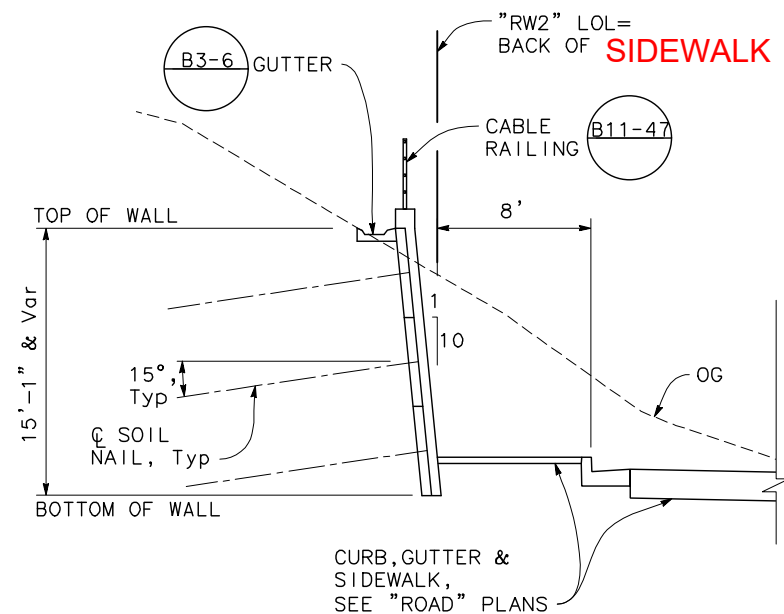


**TYPICAL SECTION**  
1" = 5'


**LEGEND:**

→ Indicates Direction of Travel

▲ Indicates Retaining Wall

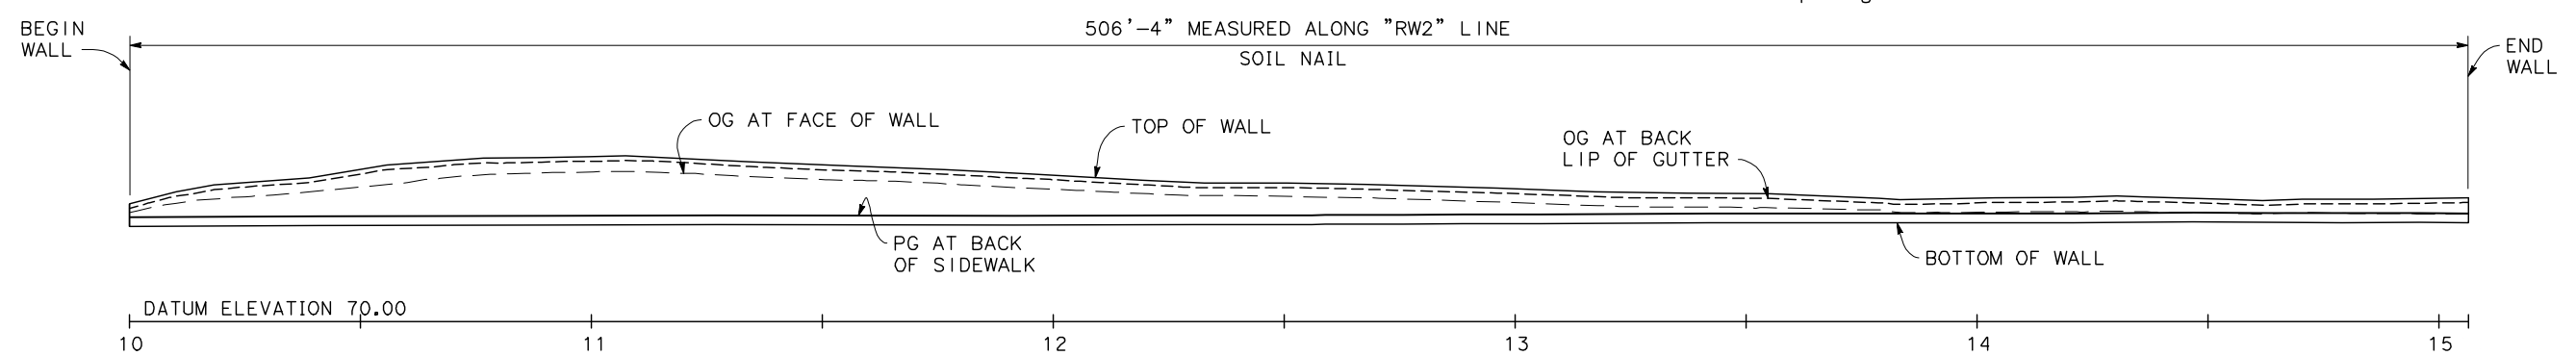

**ELEVATION**  
1" = 20'

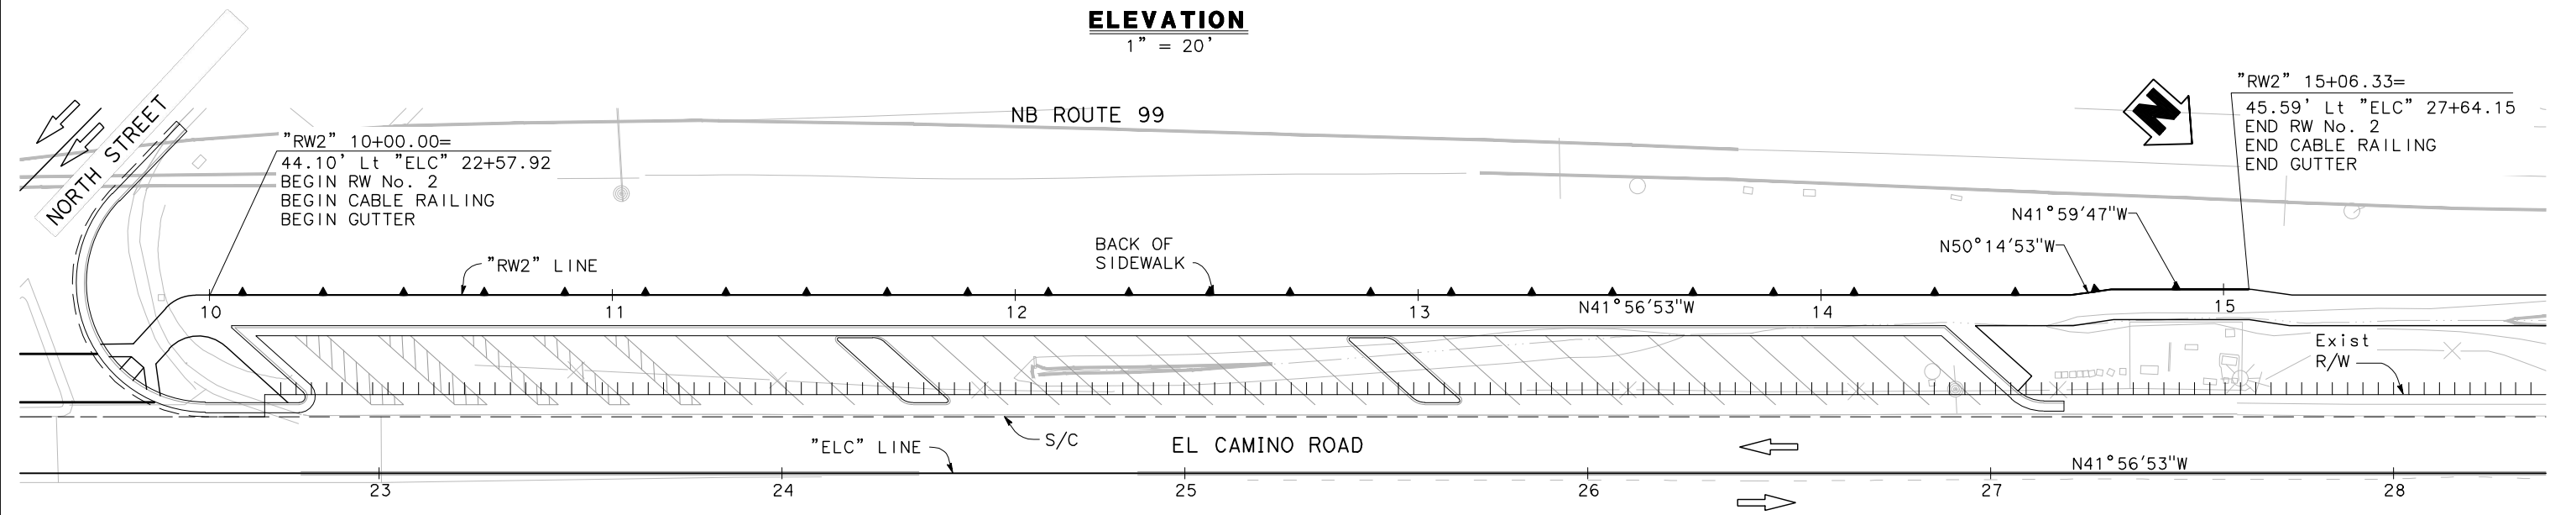

**PLAN**  
1" = 20'

|                  |                                                    |            |                                              |                                 |                                                  |                          |                                                                                |                                    |            |                             |                                  |               |                                                  |                |       |    |
|------------------|----------------------------------------------------|------------|----------------------------------------------|---------------------------------|--------------------------------------------------|--------------------------|--------------------------------------------------------------------------------|------------------------------------|------------|-----------------------------|----------------------------------|---------------|--------------------------------------------------|----------------|-------|----|
| DESIGN OVERSIGHT | DESIGN                                             | BY Y. REN  | CHECKED                                      | LOAD & RESISTANCE FACTOR DESIGN |                                                  | LIVE LOADING             | PREPARED FOR THE<br><b>STATE OF CALIFORNIA</b><br>DEPARTMENT OF TRANSPORTATION | E. FREDRICKSON<br>PROJECT ENGINEER | BRIDGE No. | <b>RETAINING WALL No. 2</b> |                                  |               |                                                  |                |       |    |
|                  | DETAILS                                            | BY J. DOTY | CHECKED                                      | LAYOUT                          | BY                                               | CHECKED                  |                                                                                |                                    | 38EXXX2    |                             |                                  |               |                                                  |                |       |    |
|                  | QUANTITIES                                         | BY         | CHECKED                                      | SPECIFICATIONS                  | BY                                               | PLANS AND SPECS COMPARED |                                                                                |                                    | R11.64     |                             |                                  |               |                                                  |                |       |    |
| SIGN OFF DATE    | DATE PLOTTED => 5/12/2021<br>FILE => 03_RW2_GP.dwg |            | TIME PLOTTED => 5:10 PM<br>USERNAME => JDOTY |                                 | ORIGINAL SCALE<br>IN INCHES FOR<br>REDUCED PLANS |                          | 0                                                                              | 1                                  | 2          | 3                           | UNIT:<br>PROJECT NUMBER & PHASE: | CONTRACT No.: | DISCARD PRINTS BEARING<br>EARLIER REVISION DATES | REVISION DATES | SHEET | OF |

| Dist | COUNTY | ROUTE | POST MILES<br>TOTAL PROJECT | SHEET<br>No. | TOTAL<br>SHEETS |
|------|--------|-------|-----------------------------|--------------|-----------------|
| 10   | Sta    | 99    | R11.50/R11.74               |              |                 |



REGISTERED STRUCTURAL ENGINEER      DATE

PLANS APPROVAL DATE

THE STATE OF CALIFORNIA OR ITS OFFICERS OR AGENTS  
SHALL NOT BE RESPONSIBLE FOR THE ACCURACY OR  
COMPLETENESS OF SCANNED COPIES OF THIS PLAN SHEET.


ALTAMONT CORRIDOR EXPRESS  
949 EAST CHANNEL STREET  
STOCKTON, CA 95202

MARK THOMAS  
701 UNIVERSITY AVENUE, SUITE 200  
SACRAMENTO, CA 95825

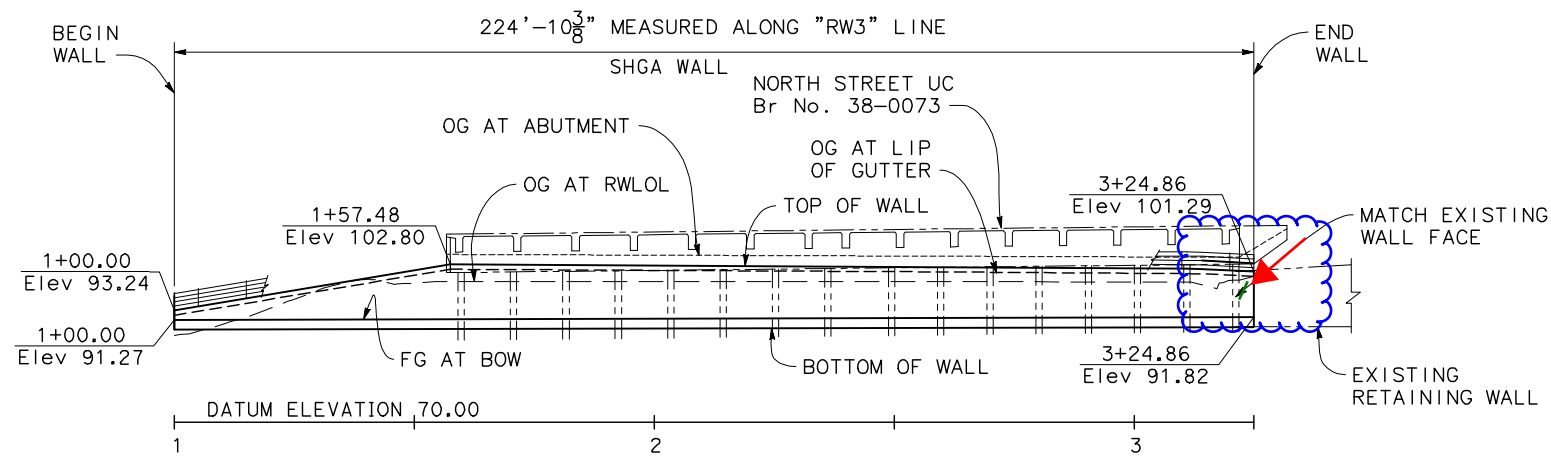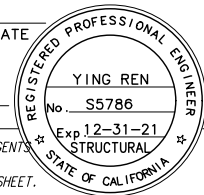


### MIRRORED DEVELOPED ELEVATION

1" = 20'

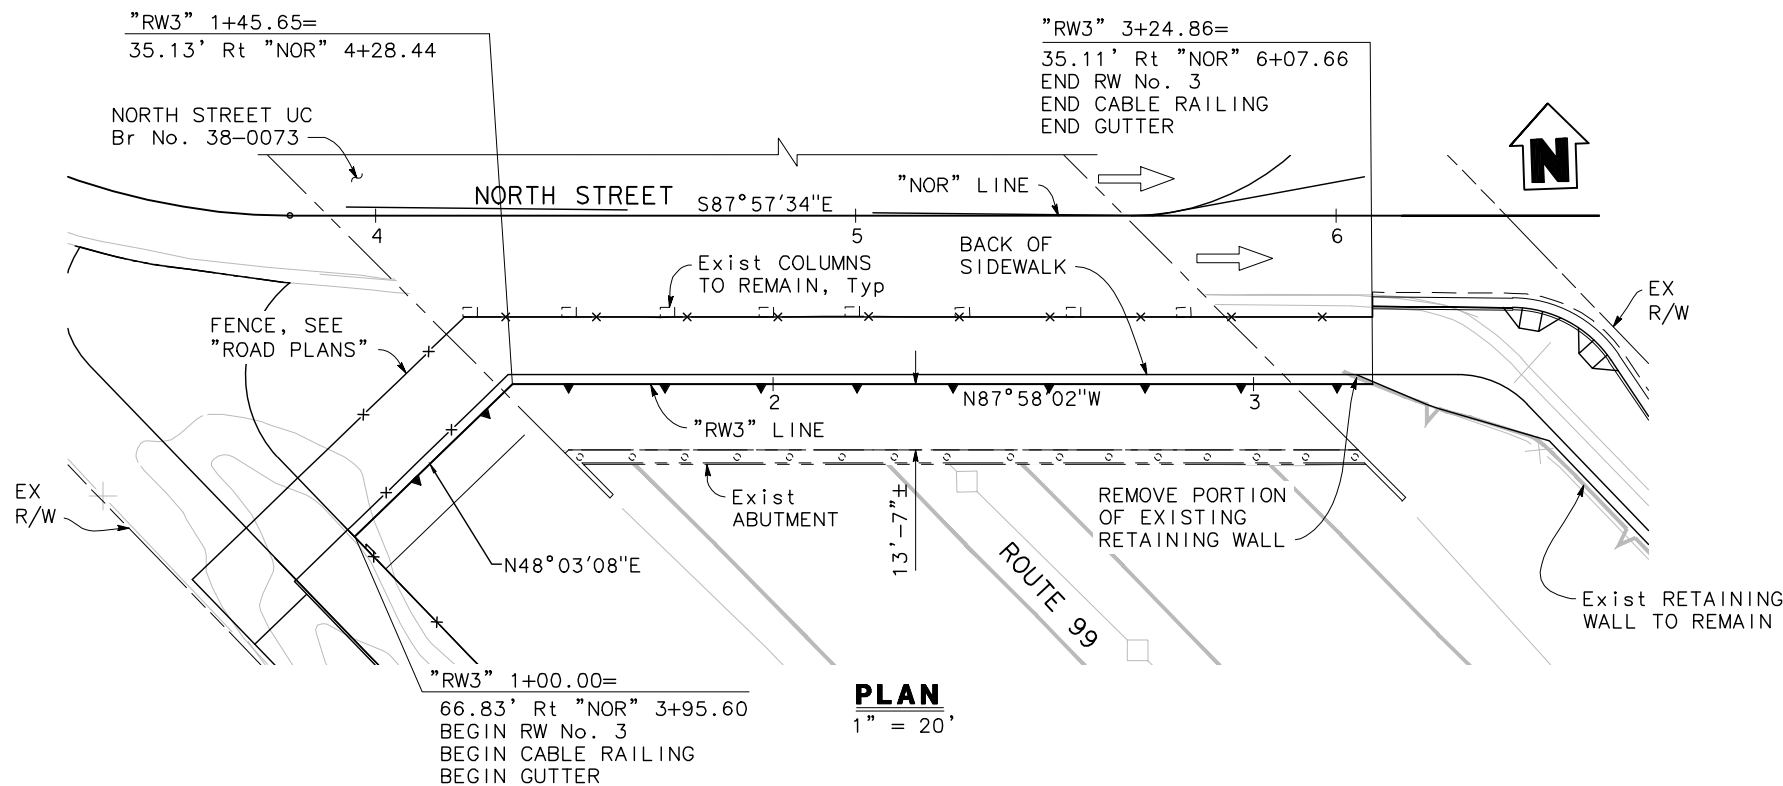

### PLAN

1" = 20'

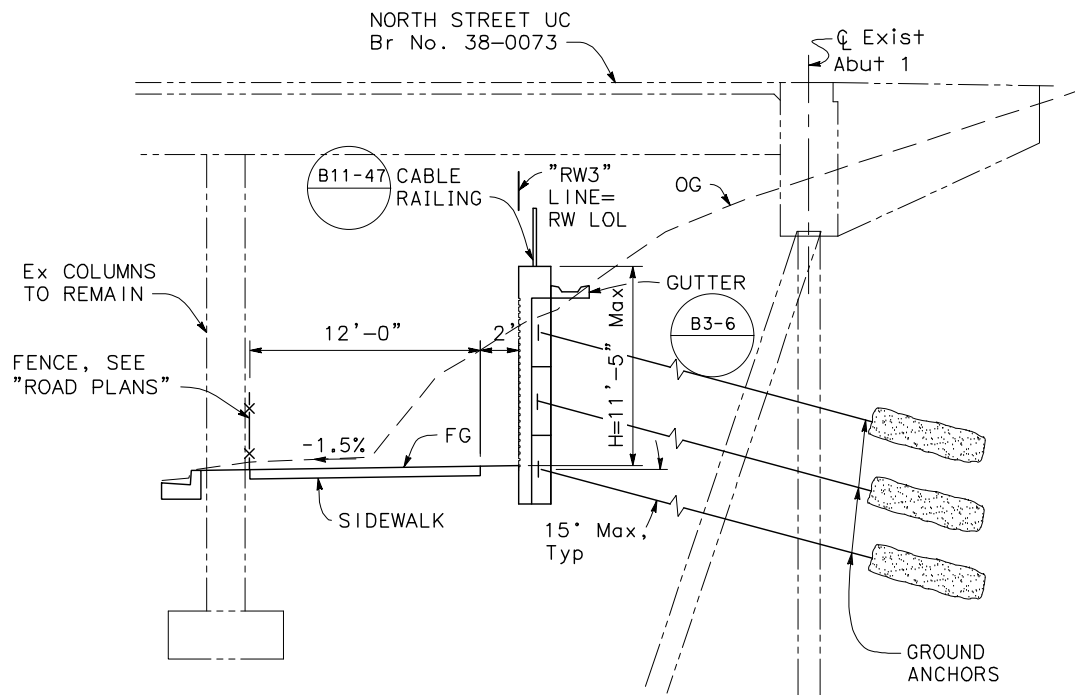

### TYPICAL SECTION

1" = 5'

#### LEGEND:

- Indicates Direction of Travel
- Indicates Retaining Wall
- Indicates Existing Structure
- SHGA Sub Horizontal Ground Anchor

|                                                    |            |               |         |                                    |              |                                                                         |                                    |                                              |                                      |  |                                                    |  |
|----------------------------------------------------|------------|---------------|---------|------------------------------------|--------------|-------------------------------------------------------------------------|------------------------------------|----------------------------------------------|--------------------------------------|--|----------------------------------------------------|--|
| DESIGN OVERSIGHT                                   | DESIGN     | BY<br>Y. REN  | CHECKED | LOAD & RESISTANCE<br>FACTOR DESIGN | LIVE LOADING | PREPARED FOR THE<br>STATE OF CALIFORNIA<br>DEPARTMENT OF TRANSPORTATION | E. FREDRICKSON<br>PROJECT ENGINEER | BRIDGE No.<br>38EXXX3<br>POST MILE<br>R11.62 | RETAINING WALL No. 3<br>GENERAL PLAN |  |                                                    |  |
| SIGN OFF DATE                                      | DETAILS    | BY<br>J. DOTY | CHECKED | LAYOUT                             | BY           | PLANS AND SPECS COMPARED                                                |                                    |                                              |                                      |  |                                                    |  |
|                                                    | QUANTITIES | BY            | CHECKED | SPECIFICATIONS                     | BY           |                                                                         |                                    |                                              |                                      |  |                                                    |  |
| DATE PLOTTED => 5/12/2021<br>FILE => 05_RW3_GP.dwg |            |               |         |                                    |              |                                                                         | UNIT:<br>PROJECT NUMBER & PHASE:   |                                              | CONTRACT No.:                        |  | DISREGARD PRINTS BEARING<br>EARLIER REVISION DATES |  |
| TIME PLOTTED => 5:13 PM<br>USERNAME => JDOTY       |            |               |         |                                    |              |                                                                         |                                    |                                              |                                      |  | REVISION DATES                                     |  |
| ORIGINAL SCALE<br>IN INCHES FOR<br>REDUCED PLANS   |            |               |         |                                    |              |                                                                         |                                    |                                              |                                      |  | SHEET                                              |  |
|                                                    |            |               |         |                                    |              |                                                                         |                                    |                                              |                                      |  | OF                                                 |  |

|      |        |       |                             |              |                 |
|------|--------|-------|-----------------------------|--------------|-----------------|
| Dist | COUNTY | ROUTE | POST MILES<br>TOTAL PROJECT | SHEET<br>No. | TOTAL<br>SHEETS |
| 10   | Sta    | 99    | R11.50/R11.74               |              |                 |

REGISTERED STRUCTURAL ENGINEER

DATE

YING REN

No. S5786

Exp. 12-31-21

STRUCTURAL


STATE OF CALIFORNIA

PLANS APPROVAL DATE

THE STATE OF CALIFORNIA OR ITS OFFICERS OR AGENTS  
SHALL NOT BE RESPONSIBLE FOR THE ACCURACY OR  
COMPLETENESS OF SCANNED COPIES OF THIS PLAN SHEET.


ALTAMONT CORRIDOR EXPRESS  
949 EAST CHANNEL STREET  
STOCKTON, CA 95202

MARK THOMAS  
701 UNIVERSITY AVENUE, SUITE 200  
SACRAMENTO, CA 95825

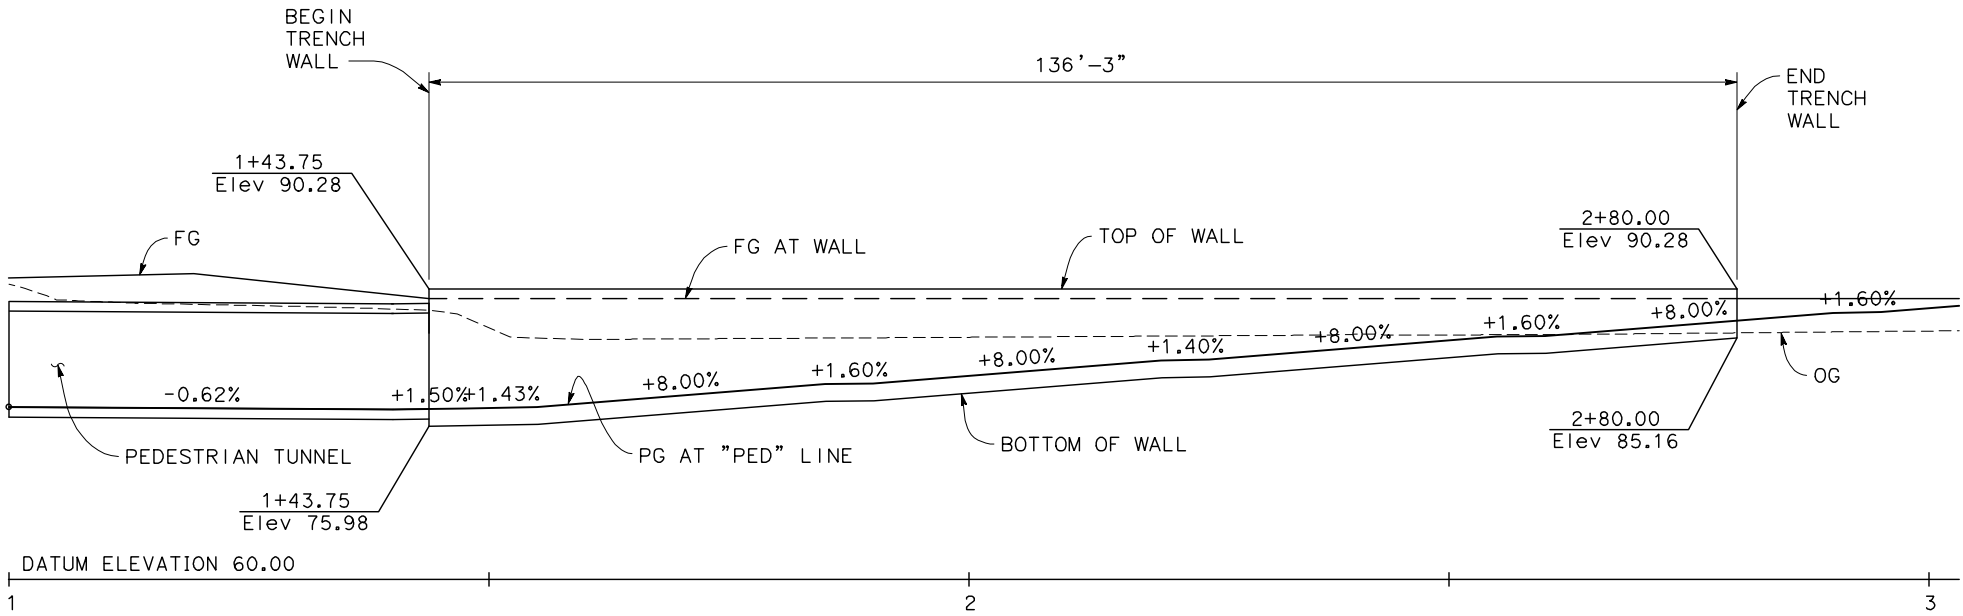


**DEVELOPED ELEVATION**

1" = 10'

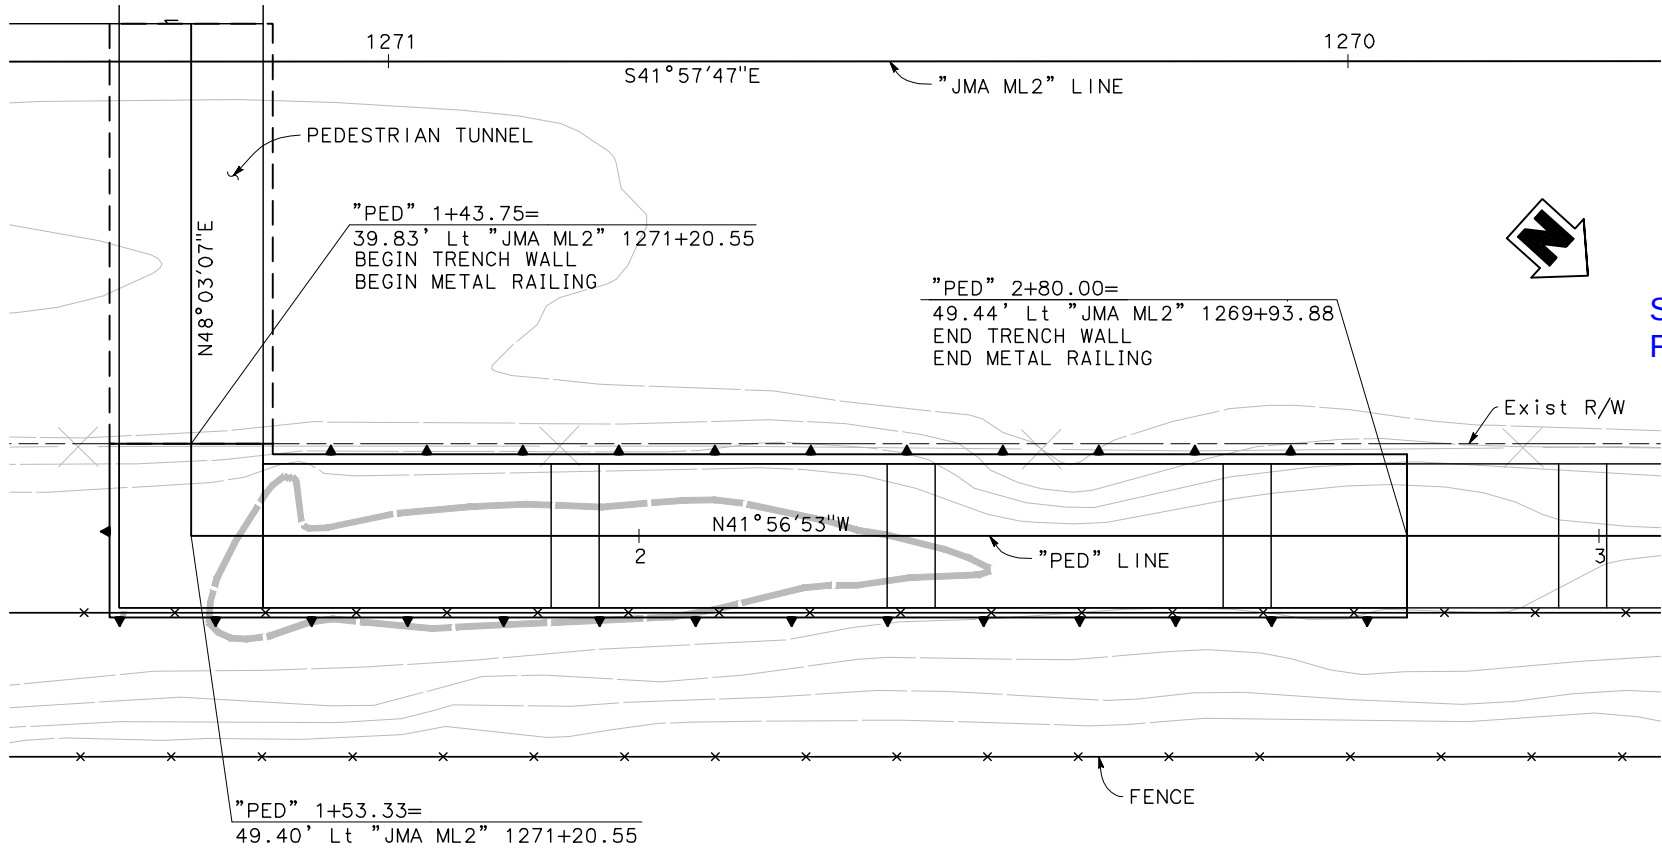

**PLAN**

1" = 10'

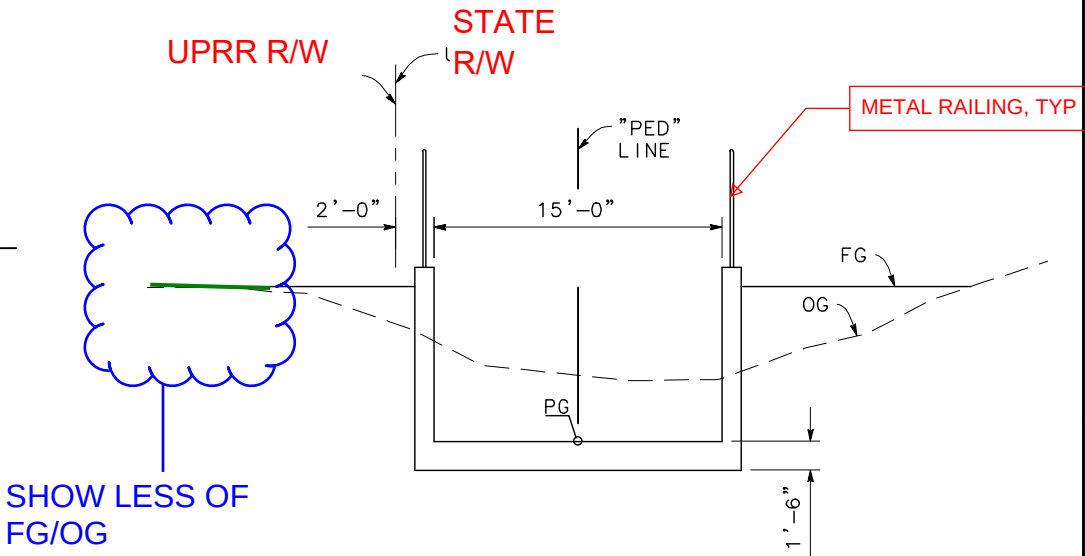

**TYPICAL SECTION**

1" = 5'

LEGEND:

Indicates Retaining Wall

|                  |            
|------------------|------------|---------------|---------|----------------------------------------------------|--------------|----------------------------------------------|-------------------------------------------------------------------------|--------------------------------------------------|-----------------------|------------------------|----------------------------------------------------|---|--|--------|--|---|--|-------|--|----|--|
|                  | DESIGN     | BY<br>Y. REN  | CHECKED | LOAD & RESISTANCE<br>FACTOR DESIGN                 | LIVE LOADING |                                              | PREPARED FOR THE<br>STATE OF CALIFORNIA<br>DEPARTMENT OF TRANSPORTATION | E. FREDRICKSON                                   | BRIDGE No.<br>38EXXX4 | PEDESTRIAN TRENCH WALL |                                                    |   |  |        |  |   |  |       |  |    |  |
| DESIGN OVERSIGHT | DETAILS    | BY<br>J. DOTY | CHECKED | LAYOUT                                             | BY           |                                              |                                                                         | PROJECT ENGINEER                                 | POST MILE             | GENERAL PLAN           |                                                    |   |  |        |  |   |  |       |  |    |  |
| SIGN OFF DATE    | QUANTITIES | BY            | CHECKED | SPECIFICATIONS                                     | BY           |                                              |                                                                         | PLANS AND SPECS COMPARED                         | R11.60                |                        |                                                    |   |  |        |  |   |  |       |  |    |  |
|                  |            |               |         | DATE PLOTTED => 5/12/2021<br>FILE => 05_RW4_GP.dwg |              | TIME PLOTTED => 5:18 PM<br>USERNAME => JDOTY |                                                                         | ORIGINAL SCALE<br>IN INCHES FOR<br>REDUCED PLANS |                       | 0                      |                                                    | 1 |  | 2      |  | 3 |  |       |  |    |  |
|                  |            |               |         |                                                    |              |                                              |                                                                         | UNIT:<br>PROJECT NUMBER & PHASE:                 | CONTRACT No. :        |                        | DISREGARD PRINTS BEARING<br>EARLIER REVISION DATES |   |  | 1/2/34 |  |   |  | SHEET |  | OF |  |