


DIST	COUNTY	ROUTE	POST MILES TOTAL PROJECT	SHEET No	TOTAL SHEETS
05	SCr	1	10.54/13.44	416	453

DRAFT 65% PLANS

REGISTERED STRUCTURAL ENGINEER DATE

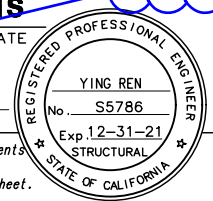


PLANS APPROVAL DATE

The State of California or its officers or agents shall not be responsible for the accuracy or completeness of scanned copies of this plan sheet.


MARK THOMAS
701 UNIVERSITY AVE., SUITE 200
SACRAMENTO, CA 95825

SCCRTC
1523 PACIFIC AVENUE
SANTA CRUZ, CA 95090

roadway will update
this later

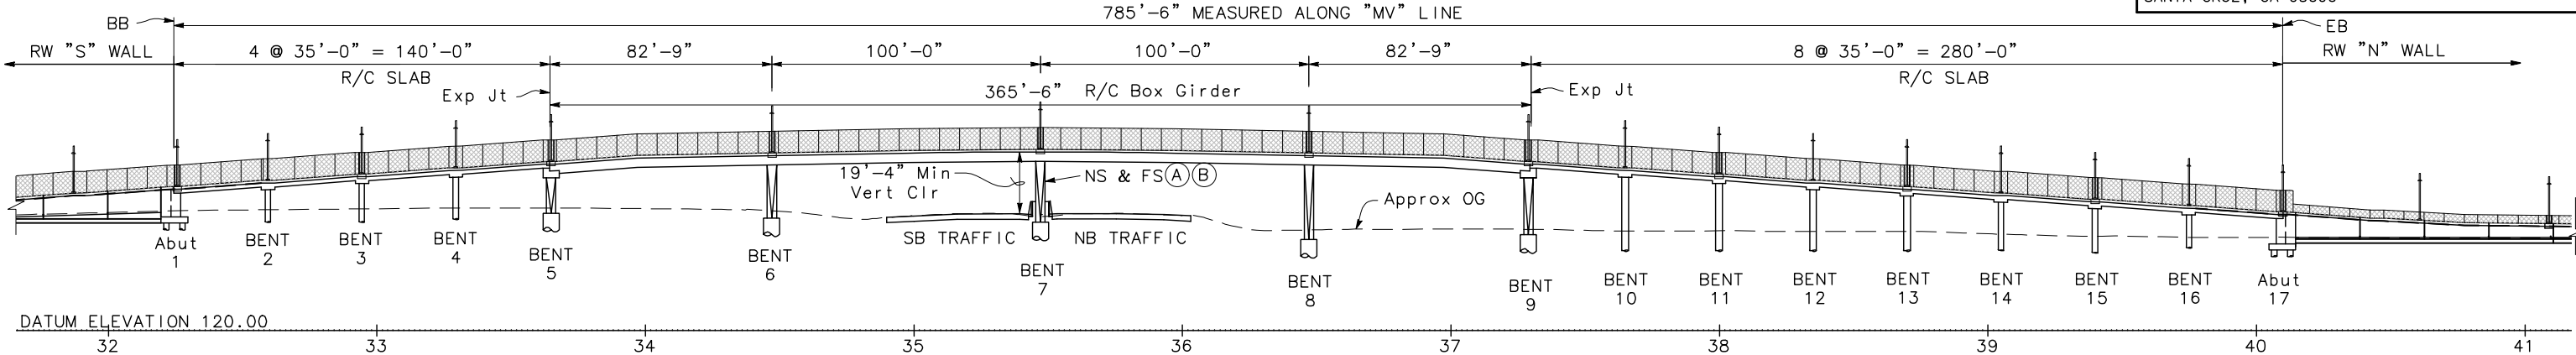

DEVELOPED ELEVATION
1" = 30'

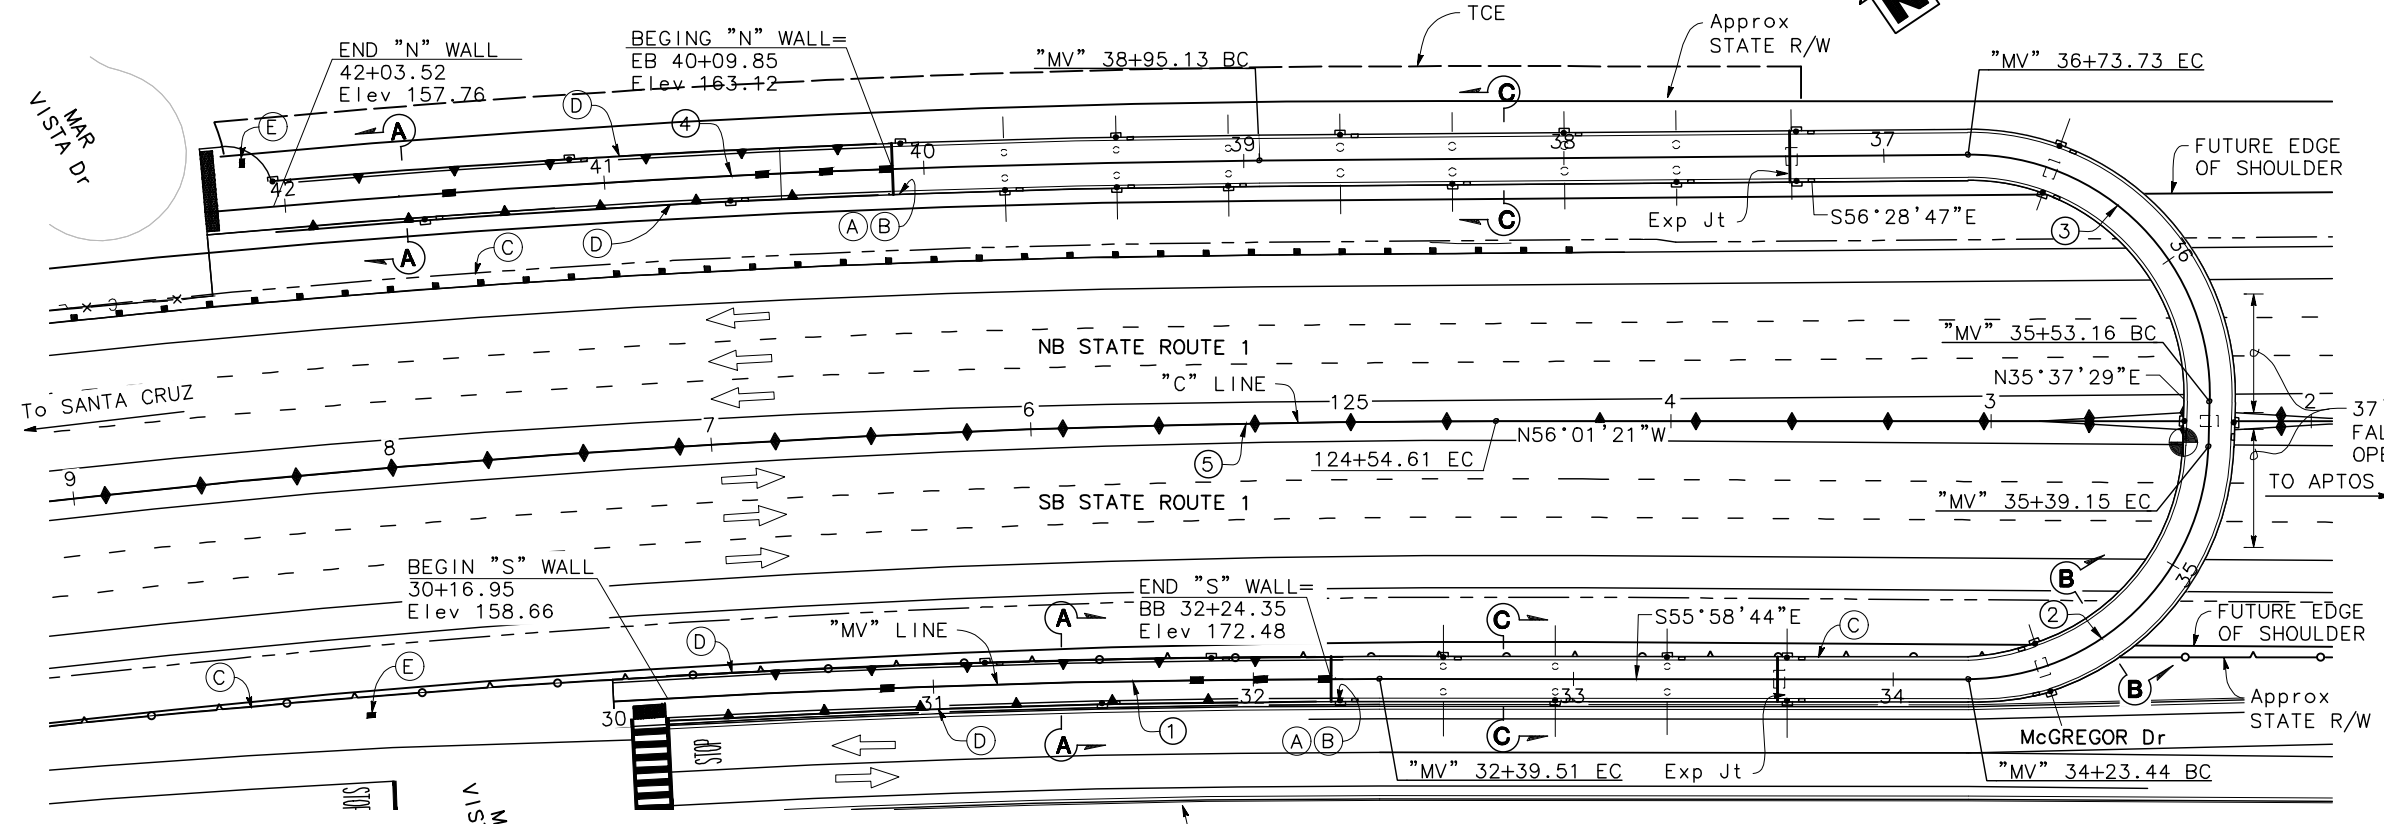

PLAN
1" = 30'

NOTES:

- (A) Point "MAR VISTA DR POC"
- (B) Point "BR No. 36-0128" & YEAR CONSTRUCTED
- (C) Sound Wall, see "ROAD PLANS"
- (D) Retaining Wall
- (E) Entry Monument

For "SECTION A-A", "SECTION B-B", "SECTION C-C" and "PROFILE GRADE", see "GENERAL PLAN No. 2" sheet.

LEGEND:

- Indicates Point of Minimum Vertical Clearance
- Indicates approximate location of Settlement Platforms, see project specifications for additional information

CURVE DATA				
No.	R	Δ	T	L
①	3926.00'	3°29'43"	119.79'	239.51'
②	75.00'	88°23'48"	72.93'	115.71'
③	75.00'	92°06'16"	77.81'	120.56'
④	4000.00'	4°43'34"	165.07'	329.95'
⑤	4100.00'	23°16'26"	844.37'	1665.45'

DESIGN OVERSIGHT	DESIGN BY Y. REN	CHECKED T. PHAM	LOAD & RESISTANCE FACTOR DESIGN	LIVE LOADING: 90 PSF AND H-10 TRUCK
SIGN OFF DATE	DETAILS BY J. DOTY	CHECKED	LAYOUT BY K. DAVIS	CHECKED Y. REN
	QUANTITIES BY	CHECKED	SPECIFICATIONS BY	PLANS AND SPECS COMPARED

PREPARED FOR THE
STATE OF CALIFORNIA
DEPARTMENT OF TRANSPORTATION

ERIC FREDRICKSON
PROJECT ENGINEER

BRIDGE NO.	36-0128
POST MILES	10.87

MAR VISTA DRIVE POC
GENERAL PLAN No. 1

DIST	COUNTY	ROUTE	POST MILES TOTAL PROJECT	SHEET No	TOTAL SHEETS
05	SCr	1	10.54/13.44	417	453

DRAFT 65% PLANS



REGISTERED STRUCTURAL ENGINEER DATE

PLANS APPROVAL DATE


The State of California or its officers or agents shall not be responsible for the accuracy or completeness of scanned copies of this plan sheet.

MARK THOMAS
701 UNIVERSITY AVE., SUITE 200
SACRAMENTO, CA 95825


SCCRTC
1523 PACIFIC AVENUE
SANTA CRUZ, CA 95090

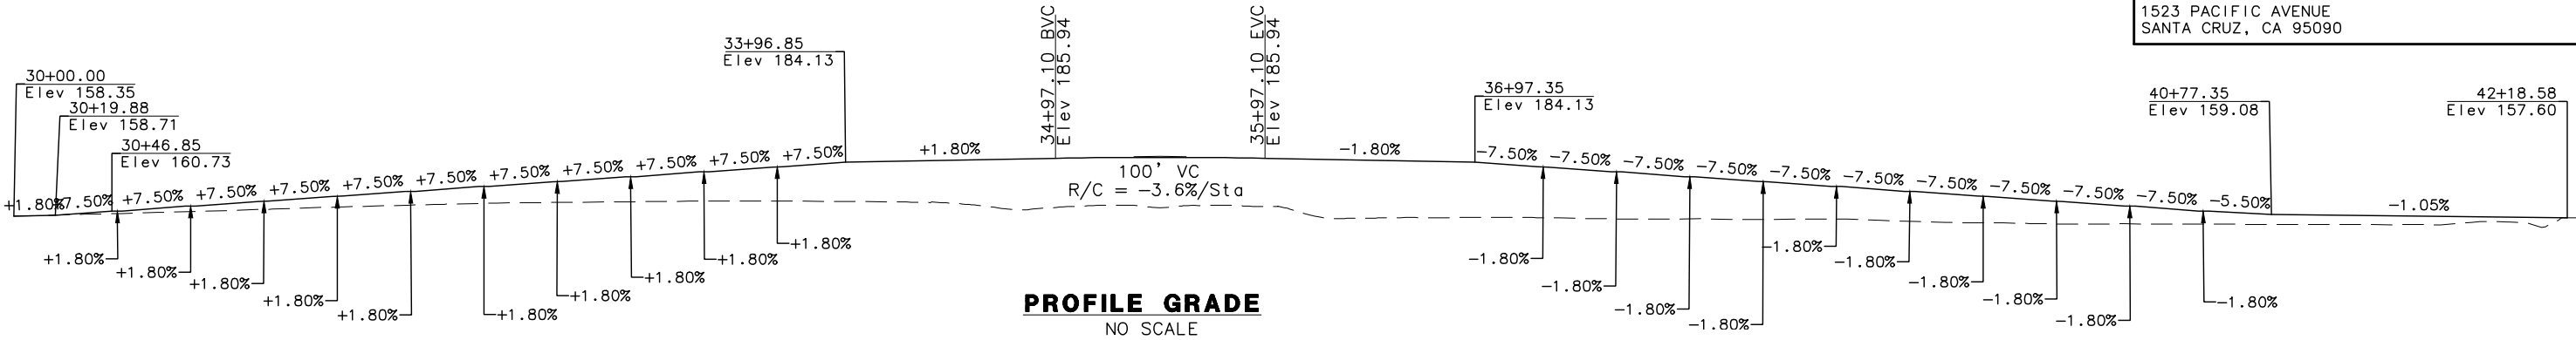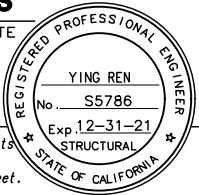


- NOTES:
- Grades at 1.80% have a length of 5 feet unless otherwise noted.
 - Grades at 7.50% have a length of 30 feet unless otherwise noted.

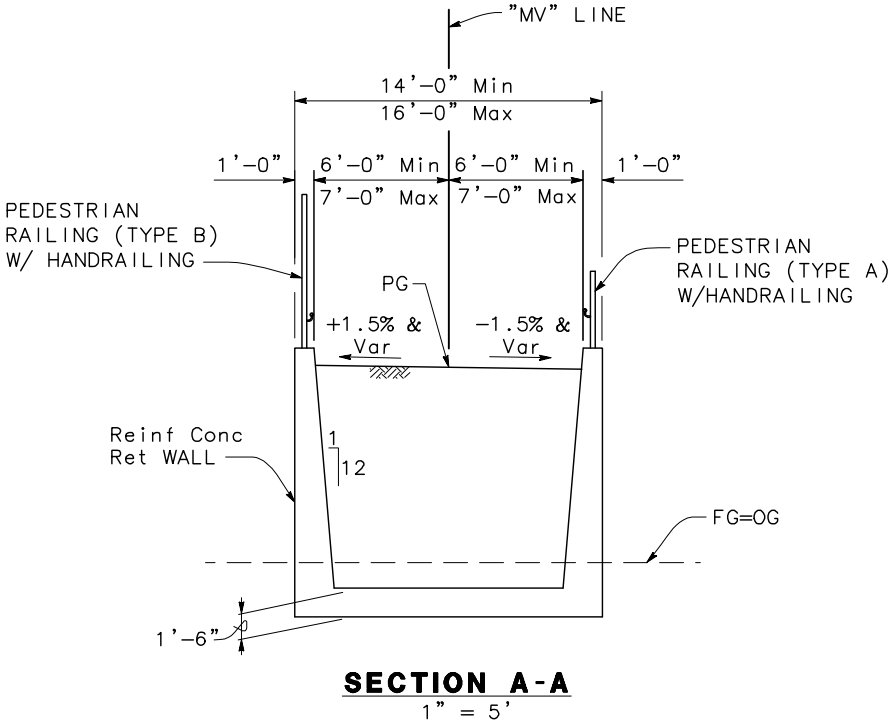

SECTION A-A
1" = 5'

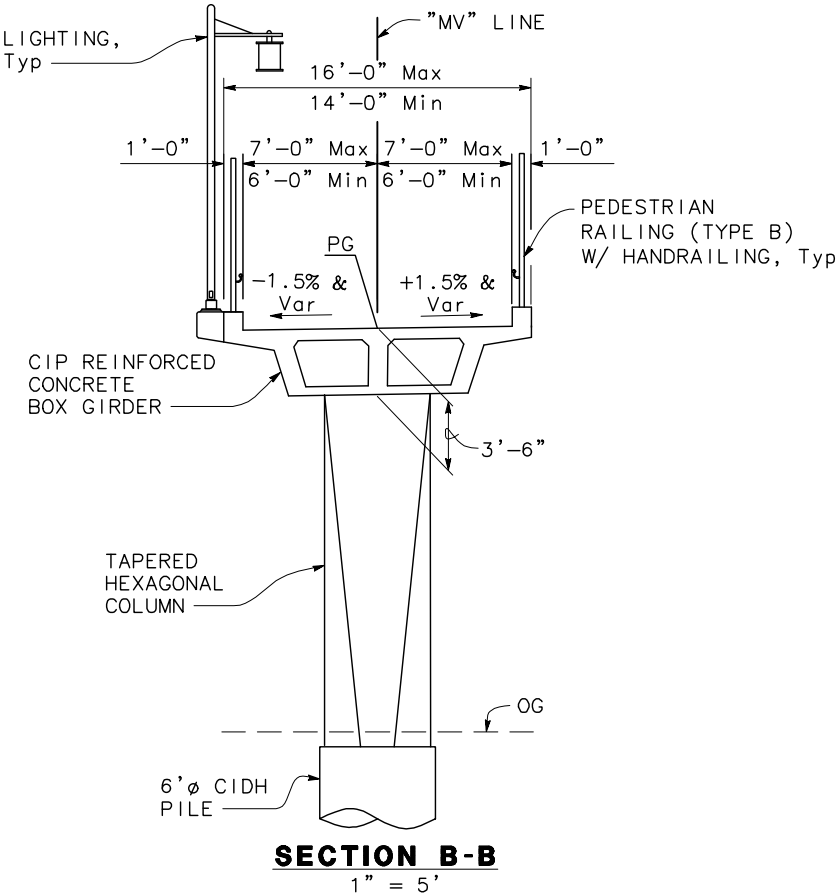

SECTION B-B
1" = 5'

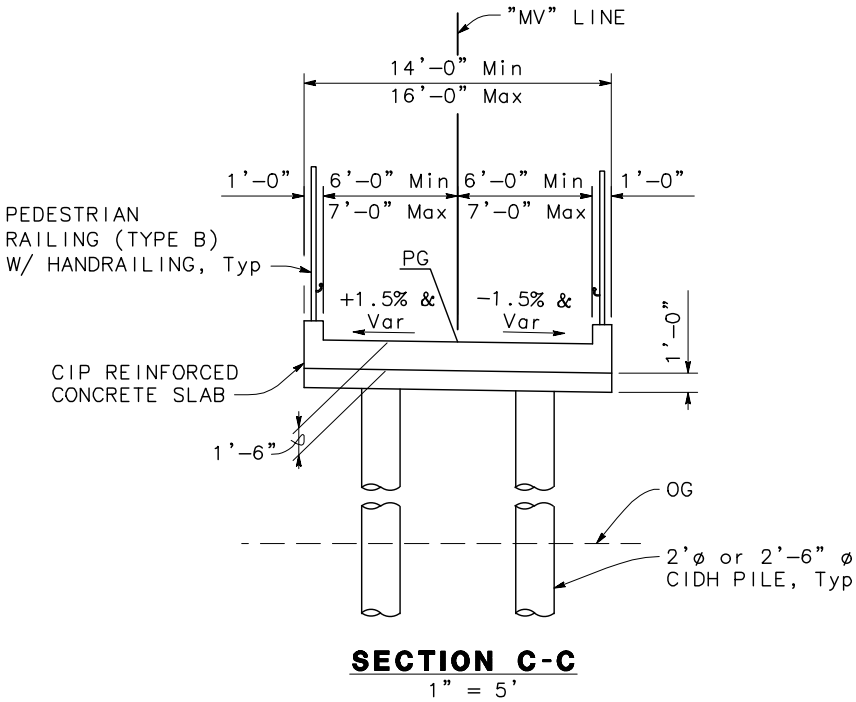


SECTION C-C
1" = 5'

DESIGN OVERSIGHT	DESIGN	BY Y. REN	CHECKED T. PHAM	LOAD & RESISTANCE FACTOR DESIGN	LIVE LOADING: 90 PSF AND H-10 TRUCK	PREPARED FOR THE STATE OF CALIFORNIA DEPARTMENT OF TRANSPORTATION	ERIC FREDRICKSON PROJECT ENGINEER	BRIDGE NO. 36-0128	MAR VISTA DRIVE POC GENERAL PLAN No. 2	
SIGN OFF DATE	DETAILS	BY J. DOTY	CHECKED	LAYOUT	BY K. DAVIS			POST MILES 10.87		
DESIGN GENERAL PLAN SHEET (ENGLISH) (REV. 03/14/12)	QUANTITIES	BY	CHECKED	SPECIFICATIONS	BY	PLANS AND SPECS COMPARED			REVISION DATES	SHEET 2
ORIGINAL SCALE IN INCHES FOR REDUCED PLANS							UNIT: PROJECT NUMBER & PHASE: 0518000116	CONTRACT NO.: 05-0C7331	DISREGARD PRINTS BEARING EARLIER REVISION DATES	
FILE => 01-02_MV_POC_GP									OF 38	

STANDARD PLANS DATED 2018

A3A - A3C	ABBREVIATIONS
A10A - A10E	LEGEND - LINES AND SYMBOLS
A10F - A10G	LEGEND - SOIL
A10H	LEGEND - ROCK
A62C	LIMITS OF PAYMENT FOR EXCAVATION AND BACKFILL - BRIDGE
RSP B0-1	BRIDGE DETAILS
B0-3	BRIDGE DETAILS
B0-5	BRIDGE DETAILS
B0-13	BRIDGE DETAILS
B2-3	16" AND 24" CAST-IN-DRILLED-HOLE CONCRETE PILE
B3-5	RETAINING WALL DETAILS No.1
B6-21	JOINT SEALS (MAXIMUM MOVEMENT RATING = 2")
B7-1	BOX GIRDER DETAILS
RSP B7-10	UTILITY OPENING BOX GIRDER
RSP B11-7	CHAIN LINK RAILING
B14-5	WATER SUPPLY LINE (DETAILS) (PIPE SIZES LESS THAN 4")
RSP ES-9C	ELECTRICAL SYSTEMS (STRUCTURE PULL BOX)

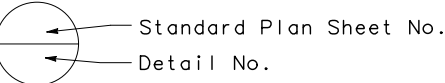

GENERAL NOTES

LOAD AND RESISTANCE FACTOR DESIGN

DESIGN:
AASHTO LRFD Bridge Design Specifications, 8th edition and the California Amendments, preface dated January 2014.
AASHTO LRFD Guide Specification for Design of Pedestrian Bridges, 2nd edition, December 2009.

SEISMIC DESIGN:
Caltrans Seismic Design Criteria (SDC), Version 2.0 dated April 2019

DEAD LOAD:
Includes 35 psf for future wearing surface

LIVE LOADING:
H10 & 90 psf pedestrian load

SEISMIC LOADING:
Soil Profile: Vs30 = 295 m/s (951 ft/s) for top 100 ft
Moment Magnitude: 7.1
Peak Ground Acceleration: 0.71g
kh = 0.36g
See Modified ARS Curve

CONCRETE:
fy = 60 ksi
f'c = 3.6 ksi unless otherwise noted


PILE:
See "PILE DATA TABLE" on "FOUNDATION PLAN" sheet

QUANTITIES

STRUCTURE EXCAVATION (BRIDGE)	CY
STRUCTURE EXCAVATION (RETAINING WALL)	CY
STRUCTURE BACKFILL (BRIDGE)	CY
STRUCTURE BACKFILL (RETAINING WALL)	CY
72" PERMANENT STEEL CASING	LF
24" CAST-IN-DRILLED-HOLE CONCRETE PILING	LF
72" CAST-IN-DRILLED-HOLE CONCRETE PILING	LF
STRUCTURAL CONCRETE, BRIDGE FOOTING	CY
STRUCTURAL CONCRETE, BRIDGE	CY
STRUCTURAL CONCRETE, BRIDGE (POLYMER FIBER)	CY
STRUCTURAL CONCRETE (RETAINING WALL)	CY
JOINT SEAL ASSEMBLY (MR 2")	LF
BAR REINFORCING STEEL (BRIDGE)	LB
BAR REINFORCING STEEL (RETAINING WALL)	LB
ISOLATION CASING	LB
MISCELLANEOUS METAL (BRIDGE)	LB
PEDESTRIAN RAILING (TYPE "A")	LF
PEDESTRIAN RAILING (TYPE "B")	LF
REDWOOD FOREST CUTOUTS	LS


INDEX TO PLANS

No.	TITLE
1	GENERAL PLAN No. 1
2	GENERAL PLAN No. 2
3	INDEX TO PLAN
4	DECK CONTOURS No. 1
5	DECK CONTOURS No. 2
6	ABUTMENT CONSTRUCTION SEQUENCE
7	FOUNDATION PLAN No. 1
8	FOUNDATION PLAN No. 2
9	ABUTMENT LAYOUT
10	ABUTMENT DETAILS No. 1
11	ABUTMENT DETAILS No. 2
12	RETAINING WALL "S" LAYOUT
13	RETAINING WALL "N" LAYOUT
14	RETAINING WALL DETAILS
15	BENT 2 THRU 4, 10 THRU 16 LAYOUT AND DETAILS
16	BENT 5 AND 9 LAYOUT
17	BENT 5 AND 9 DETAILS
18	BENT 6 THRU 8 LAYOUT
19	BENT 6 THRU 8 DETAILS
20	CIDH PILE DETAILS
21	ISOLATION CASING DETAILS
22	TYPICAL SECTION No. 1
23	TYPICAL SECTION No. 2
24	GIRDER LAYOUT No. 1
25	GIRDER LAYOUT No. 2
26	GIRDER REINFORCEMENT No. 1
27	GIRDER REINFORCEMENT No. 2
28	ABUTMENT DRAINAGE DETAILS
29	JOINT ARMOR FOR PEDESTRIAN WALKWAYS
30	PEDESTRIAN RAILINGS No. 1
31	PEDESTRIAN RAILINGS No. 2
32	PEDESTRIAN RAILINGS No. 3
33	PEDESTRIAN RAILINGS No. 4
34	ENTRY MONUMENT DETAILS
35	REDWOOD FOREST CUTOUT LAYOUT
36	REDWOOD FOREST CUTOUT DETAILS
37	RETAINING WALL "N" AESTHETIC TREATMENT
38	RETAINING WALL "S" AESTHETIC TREATMENT
39	LOG OF TEST BORINGS 1 OF 2
40	LOG OF TEST BORINGS 2 OF 2

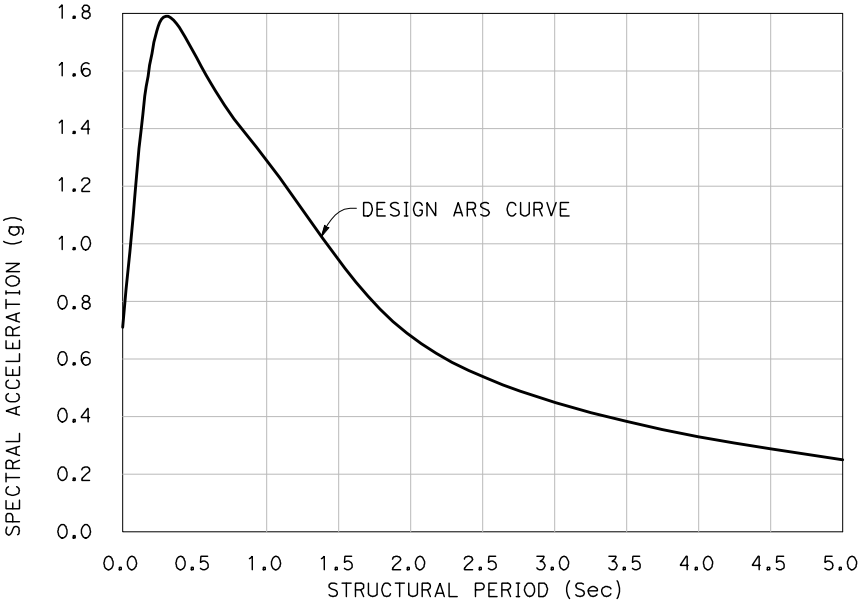

MODIFIED ARS CURVE

5% DAMPING

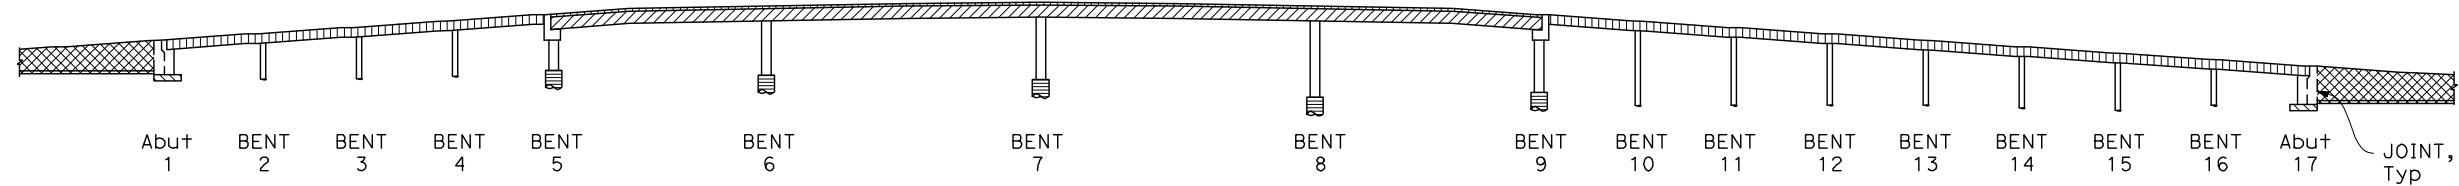

	Structural Concrete, Bridge
	Structural Concrete, Bridge (f'c = 6 ksi @ 28 days)
	Structural Concrete, Bridge (Polymer Fiber) (f'c = 6 ksi @ 28 days)

	CIDH Concrete Pile
	Structural Concrete, Bridge Footing
	Structural Concrete, Retaining Wall

CONCRETE STRENGTH AND TYPE LIMITS

NO SCALE

Dist	COUNTY	ROUTE	POST MILES TOTAL PROJECT	SHEET No.	TOTAL SHEETS
05	Scr	1	10.54/13.44	418	453

DRAFT 65% PLANS



REGISTERED STRUCTURAL ENGINEER DATE

PLANS APPROVAL DATE


THE STATE OF CALIFORNIA OR ITS OFFICERS OR AGENTS SHALL NOT BE RESPONSIBLE FOR THE ACCURACY OR COMPLETENESS OF SCANNED COPIES OF THIS PLAN SHEET.

MARK THOMAS
701 UNIVERSITY AVE., SUITE 200
SACRAMENTO, CA 95825


SCCRTC
1523 PACIFIC AVENUE
SANTA CRUZ, CA 95090

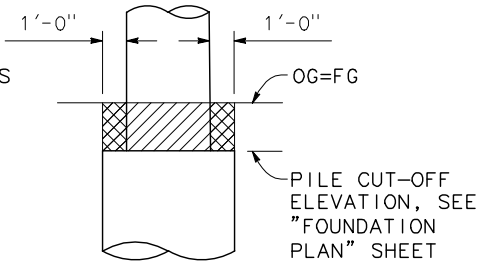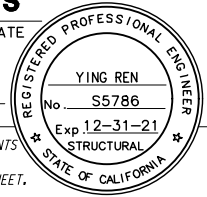

BENT 5, 7 THRU 9

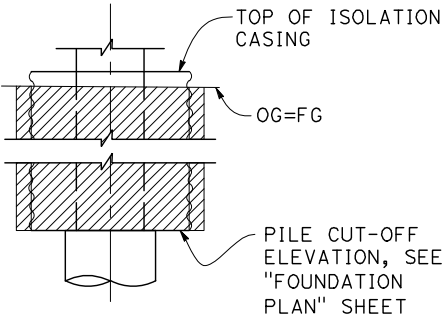

BENTS 2, 6 AND 13

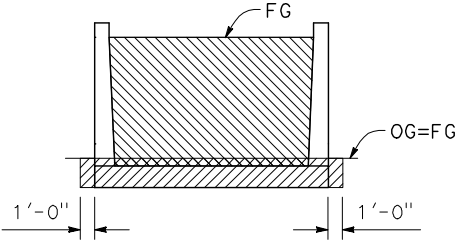

RW "S" & RW "N"

LIMITS OF EXCAVATION AND BACKFILL

NO SCALE

	Structure Excavation
	Structure Backfill

X	DESIGN OVERSIGHT
X	SIGN OFF DATE

DESIGN	BY Y. REN	CHECKED X
DETAILS	BY J. DOTY	CHECKED X
QUANTITIES	BY X	CHECKED X

PREPARED FOR THE
STATE OF CALIFORNIA
DEPARTMENT OF TRANSPORTATION

ERIC FREDRICKSON
PROJECT ENGINEER


BRIDGE No.
36-0128
POST MILE
10.87

MAR VISTA DRIVE POC
INDEX TO PLANS

DATE PLOTTED => 11/18/2021
FILE => 03_MV_POC_ITP.dwg
TIME PLOTTED => 11:26 AM
USERNAME => JVALENZUELA
ORIGINAL SCALE IN INCHES FOR REDUCED PLANS

UNIT: X
PROJECT NUMBER & PHASE: 0518000116
CONTRACT No.: 05-0C7331

REVISION DATES	SHEET	OF
6-18-21	418	453

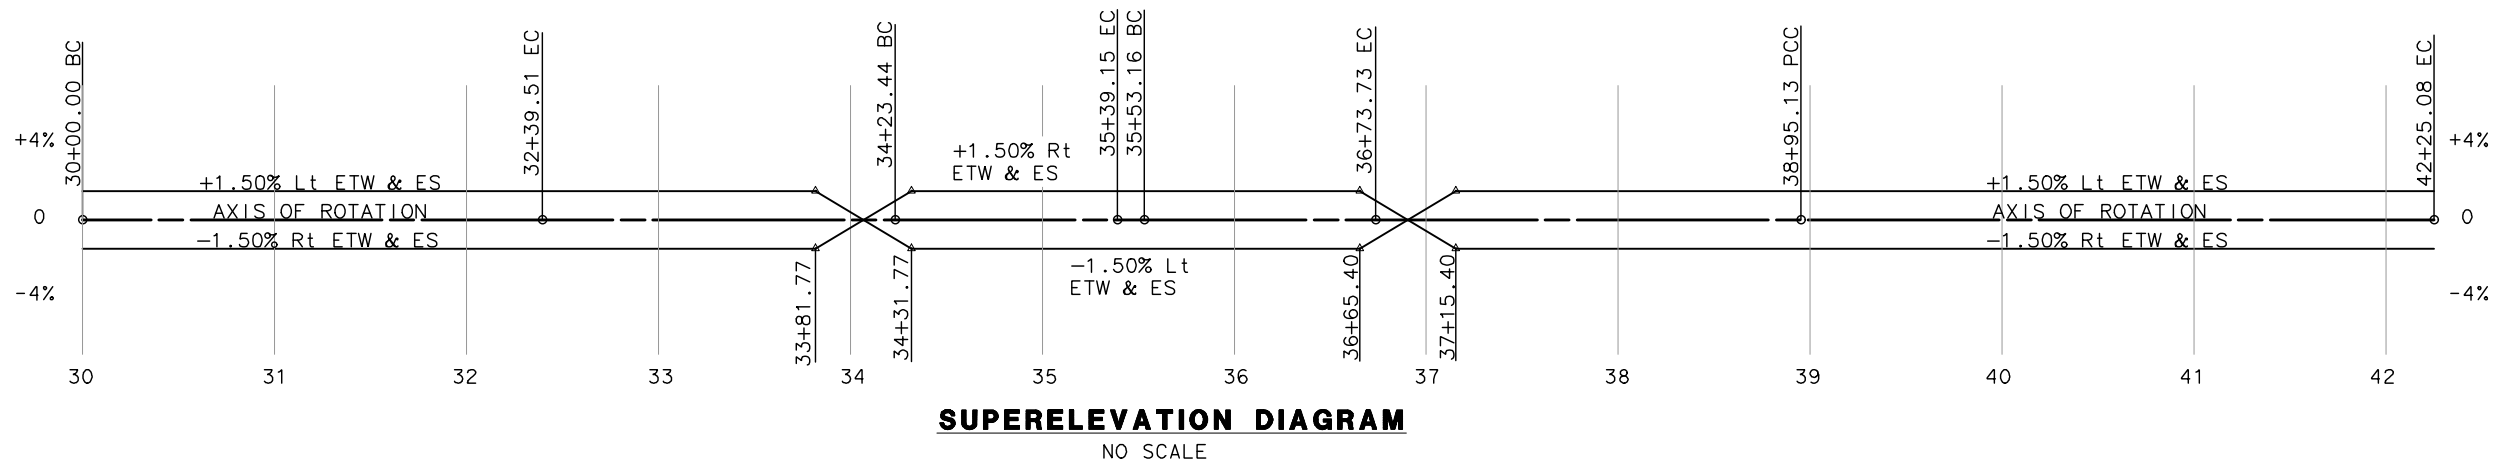


Dist	COUNTY	ROUTE	POST MILES TOTAL PROJECT	SHEET NO.	TOTAL SHEETS
05	Scr	1	10.54/13.44	419	453

DRAFT 65% PLANS
REGISTERED STRUCTURAL ENGINEER DATE

REGISTERED PROFESSIONAL ENGINEER
YING REN
No. S5786
Exp. 12-31-21
STRUCTURAL
STATE OF CALIFORNIA

PLANS APPROVAL DATE
THE STATE OF CALIFORNIA OR ITS OFFICERS OR AGENTS
SHALL NOT BE RESPONSIBLE FOR THE ACCURACY OR
COMPLETENESS OF SCANNED COPIES OF THIS PLAN SHEET.
MARK THOMAS
701 UNIVERSITY AVE., SUITE 200
SACRAMENTO, CA 95825
SCCRTC
1523 PACIFIC AVENUE
SANTA CRUZ, CA 95090

- NOTES:
1. Contour interval is 0.01 feet.
 2. Contours do not include camber or falsework settlement.
 3. X - Indicates 10 foot intervals, measured along "MV" Line.
 4. □ - Indicates half foot contour.

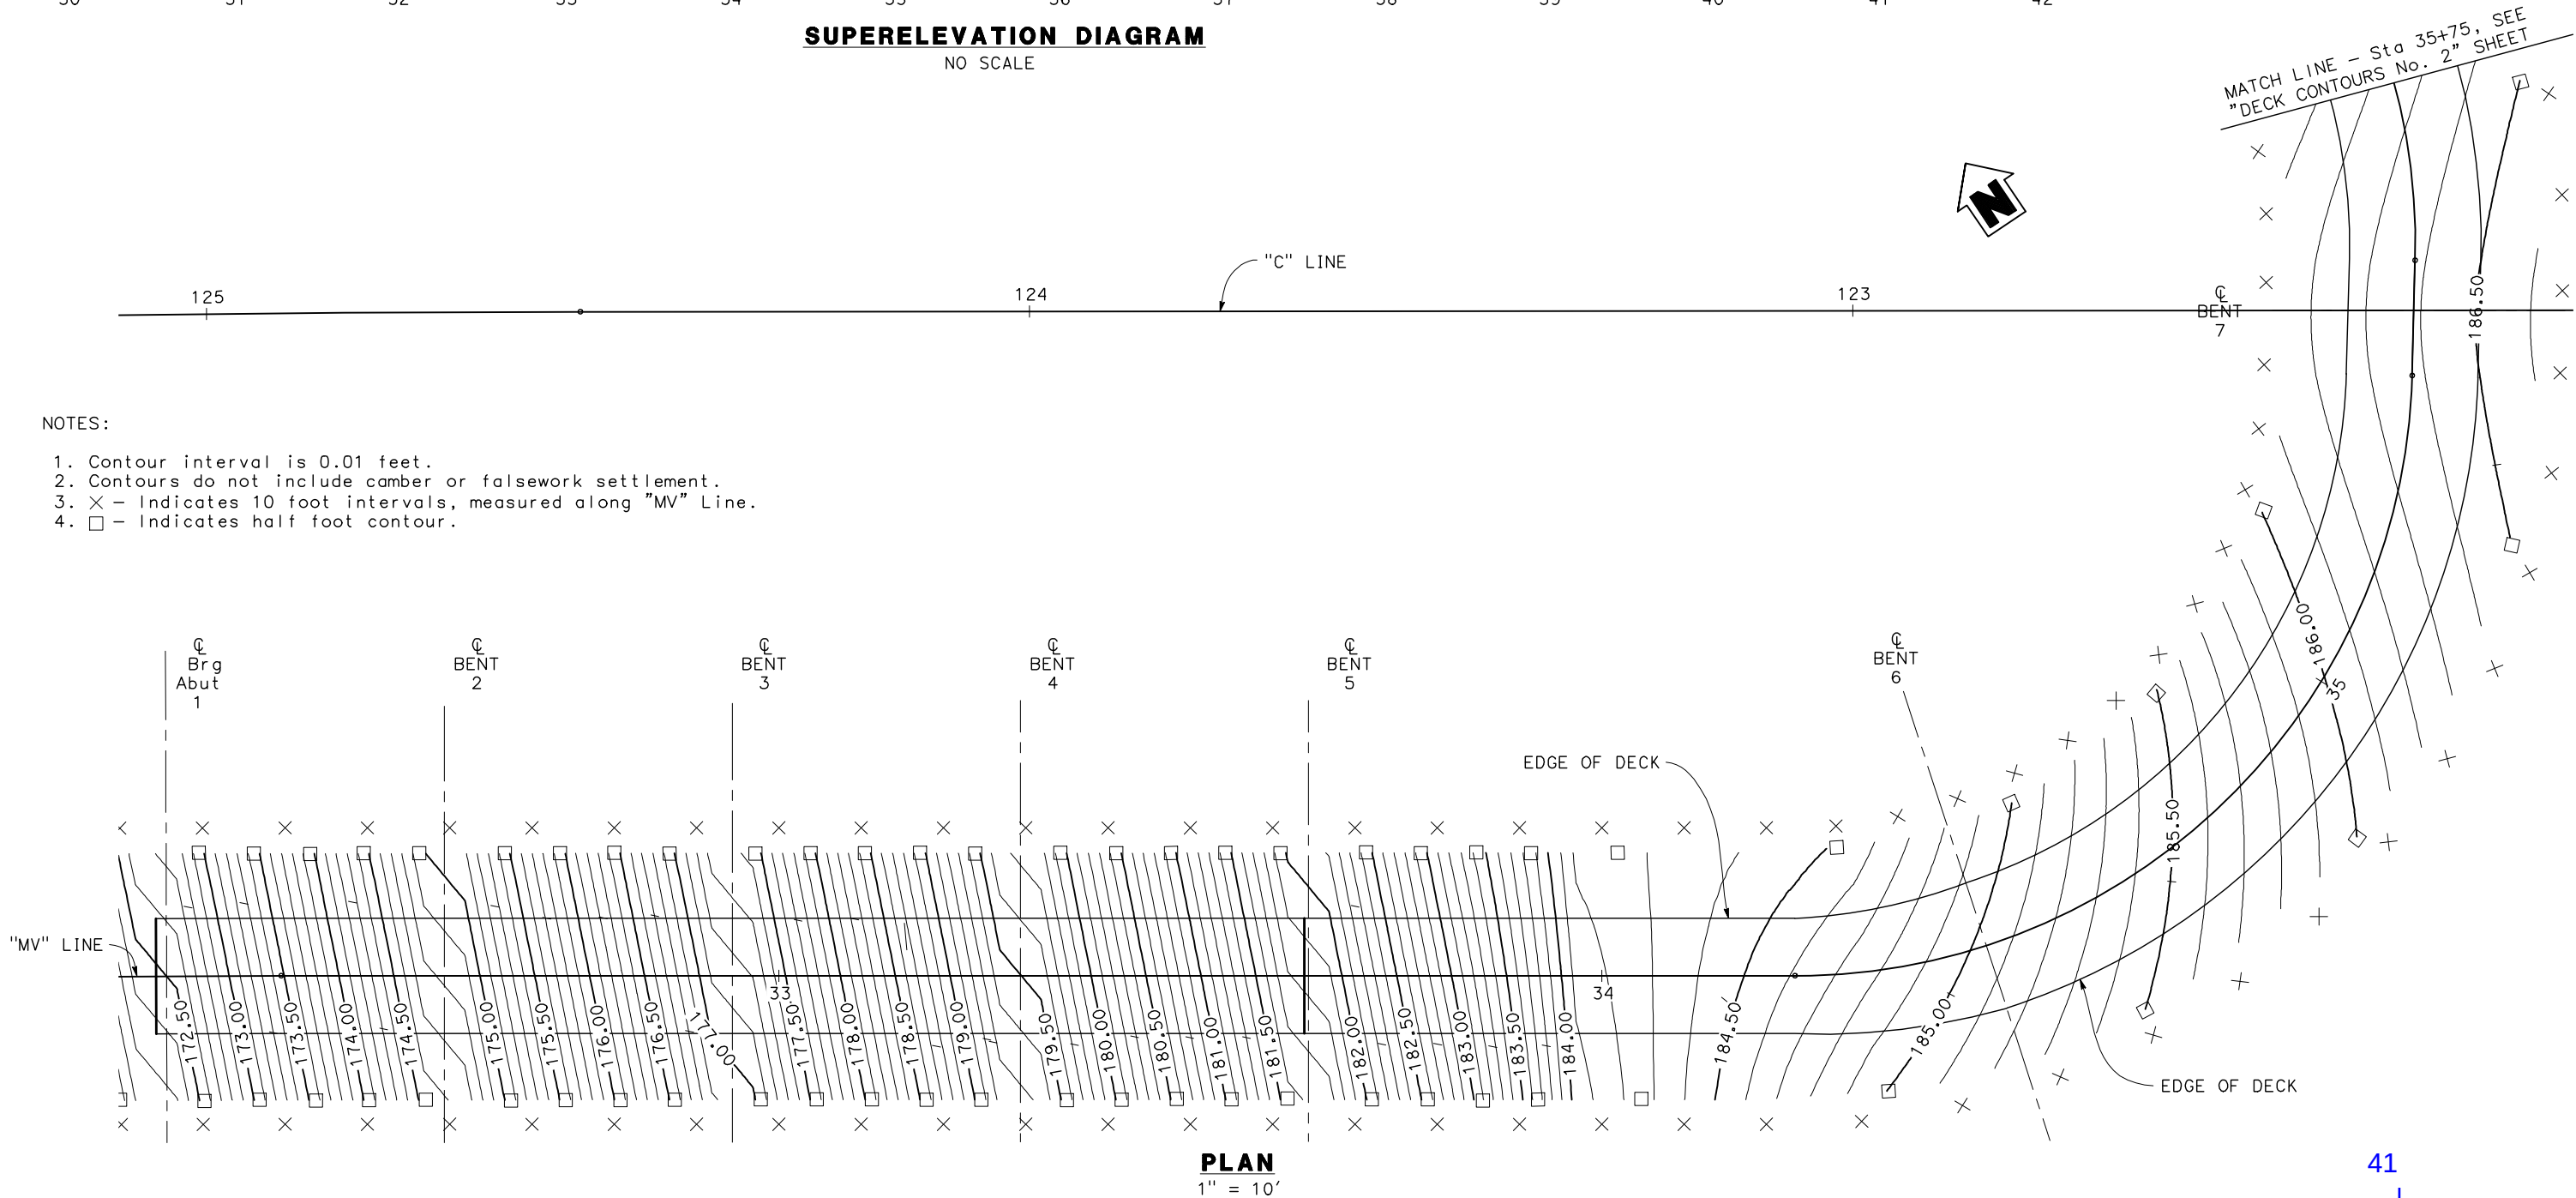

X DESIGN OVERSIGHT X SIGN OFF DATE	DESIGN BY Y. REN DETAILS BY J. DOTY QUANTITIES BY X	CHECKED X X X	PREPARED FOR THE STATE OF CALIFORNIA DEPARTMENT OF TRANSPORTATION	ERIC FREDRICKSON PROJECT ENGINEER	BRIDGE No. 36-0128	MAR VISTA DRIVE POC DECK CONTOURS No. 1						
					POST MILE 10.87							
DATE PLOTTED => 11/16/2021 FILE => 04-05_MV_POC_DC.dwg				TIME PLOTTED => 9:23 PM USERNAME => JVALENZUELA		ORIGINAL SCALE IN INCHES FOR REDUCED PLANS	UNIT: X PROJECT NUMBER & PHASE: 0518000116	CONTRACT No.: 05-OC7331	DISREGARD PRINTS BEARING EARLIER REVISION DATES	REVISION DATES 6-18-21	SHEET 41	OF 38

Dist	COUNTY	ROUTE	POST MILES TOTAL PROJECT	SHEET No.	TOTAL SHEETS
05	Scr	1	10.54/13.44	420	453

DRAFT 65% PLANS


REGISTERED STRUCTURAL ENGINEER DATE

PLANS APPROVAL DATE

THE STATE OF CALIFORNIA OR ITS OFFICERS OR AGENTS
SHALL NOT BE RESPONSIBLE FOR THE ACCURACY OR
COMPLETENESS OF SCANNED COPIES OF THIS PLAN SHEET.


MARK THOMAS
701 UNIVERSITY AVE., SUITE 200
SACRAMENTO, CA 95825

SCCRTC
1523 PACIFIC AVENUE
SANTA CRUZ, CA 95090

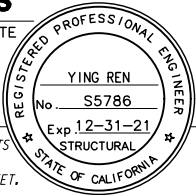


NOTES:

1. Contour interval is 0.01 feet.
2. Contours do not include camber or falsework settlement.
3. X - Indicates 10 foot intervals, measured along "MV" Line.
4. □ - Indicates half foot contour.

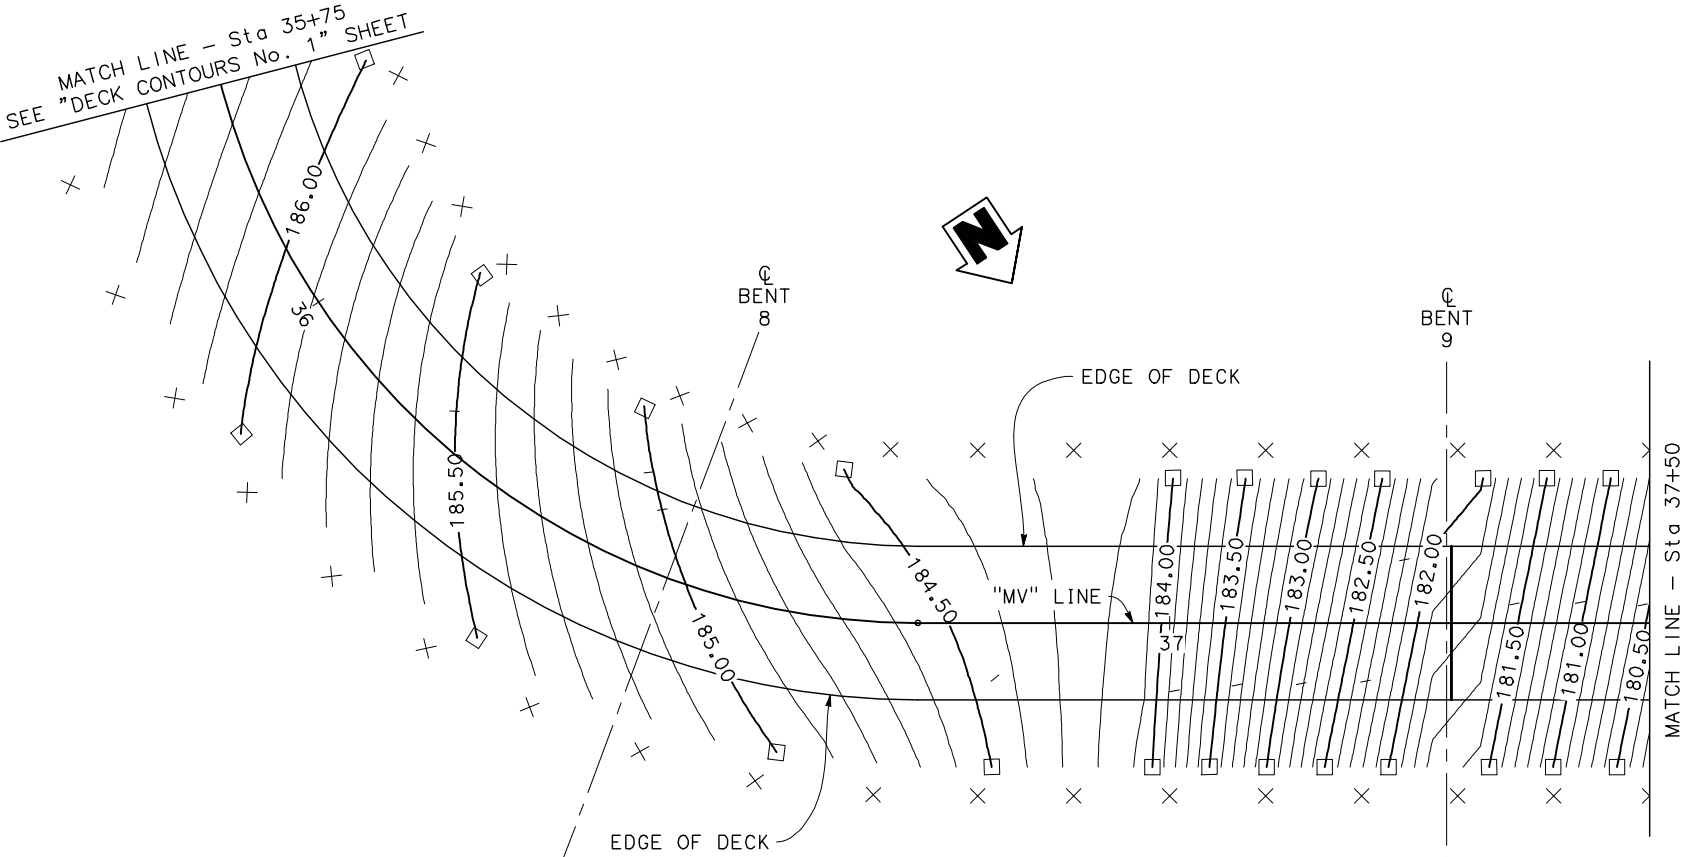


PLAN
1" = 10'

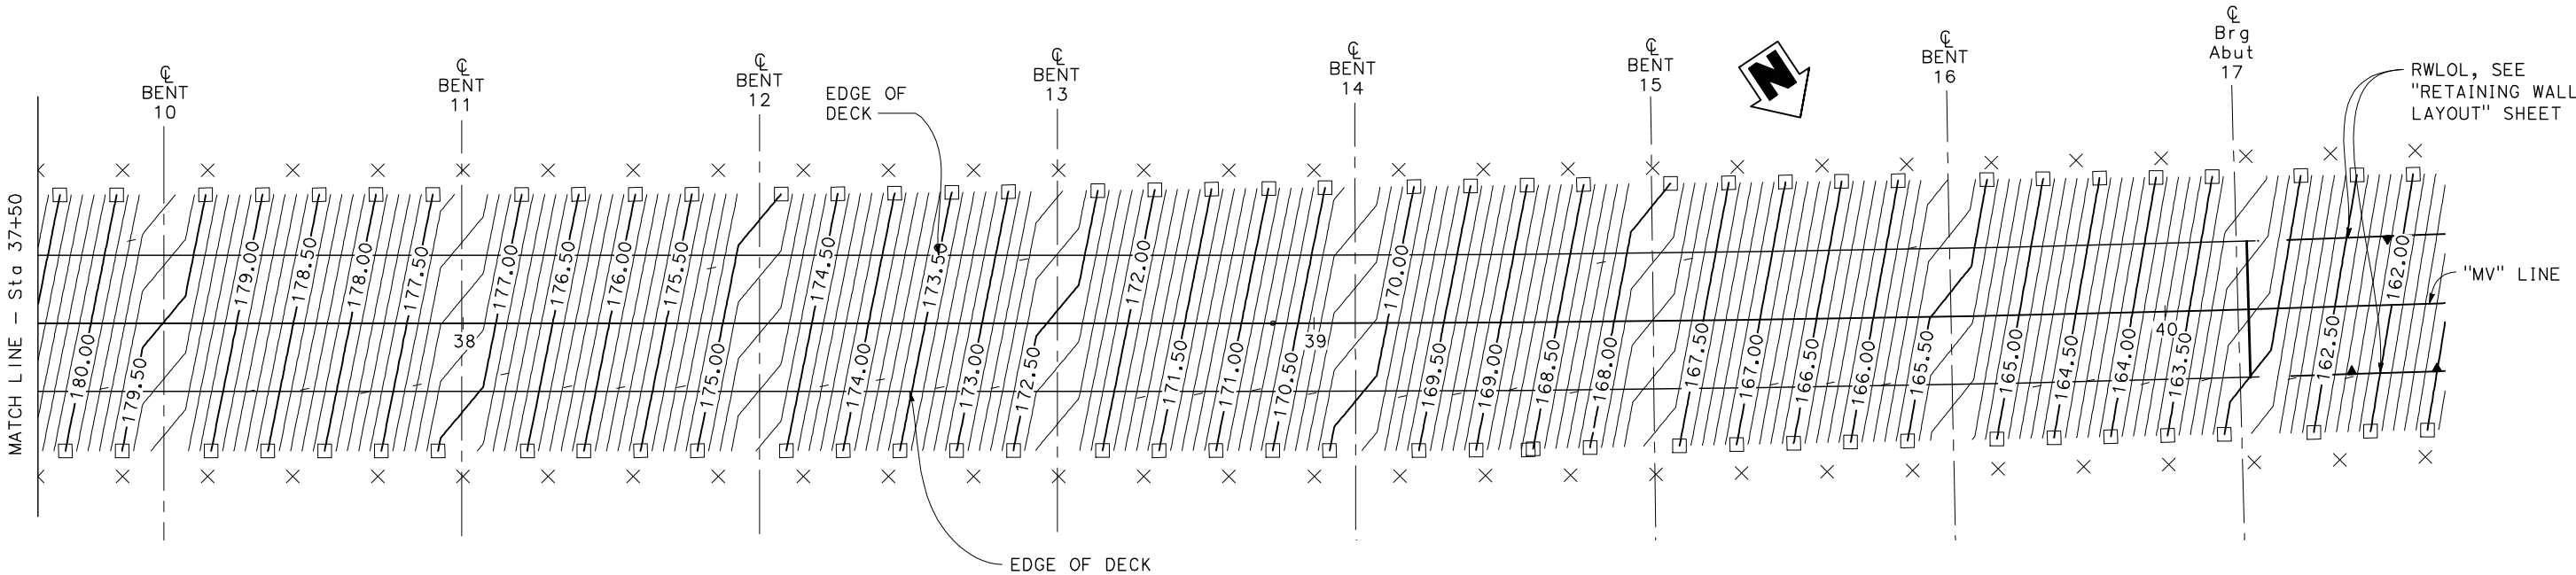


PLAN
1" = 10'


X DESIGN OVERSIGHT X SIGN OFF DATE		DESIGN BY Y. REN DETAILS BY J. DOTY QUANTITIES BY X		CHECKED X X X		PREPARED FOR THE STATE OF CALIFORNIA DEPARTMENT OF TRANSPORTATION		ERIC FREDRICKSON PROJECT ENGINEER		BRIDGE No. 36-0128 POST MILE 10.87		MAR VISTA DRIVE POC DECK CONTOURS No. 2																					
DATE PLOTTED ==> 11/16/2021 FILE ==> 04-05_MV_POC_DC.dwg										TIME PLOTTED ==> 10:22 PM USERNAME ==> JVALENZUELA										ORIGINAL SCALE IN INCHES FOR REDUCED PLANS		UNIT: X PROJECT NUMBER & PHASE: 0518000116		CONTRACT No.: 05-OC7331		DISREGARD PRINTS BEARING EARLIER REVISION DATES		REVISION DATES		SHEET 5		OF 38	
																								6-18-21									

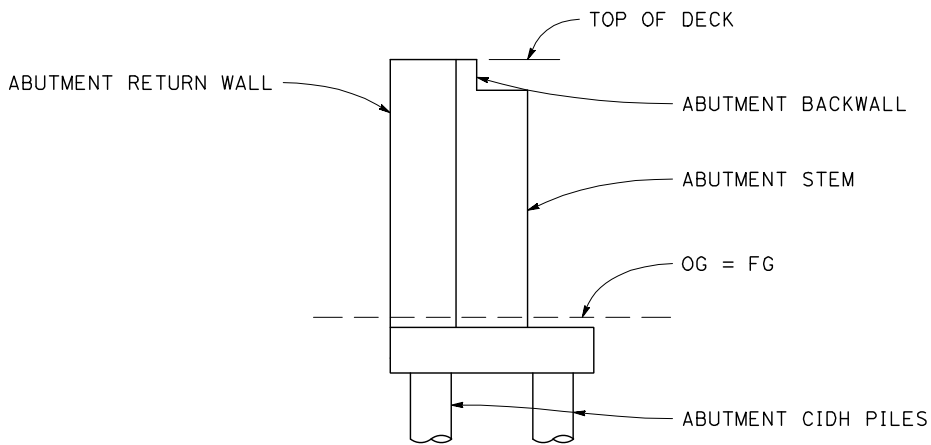

STEP 1

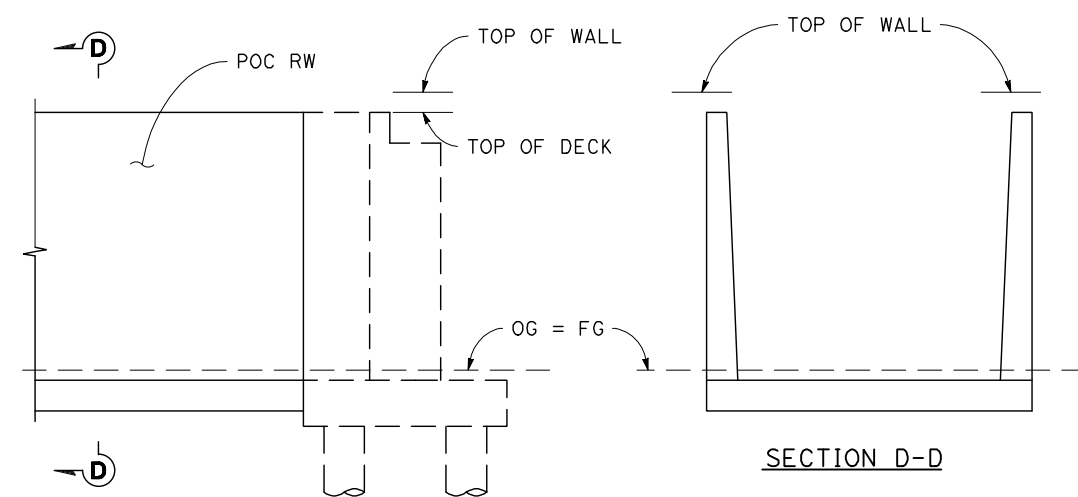


STEP 2

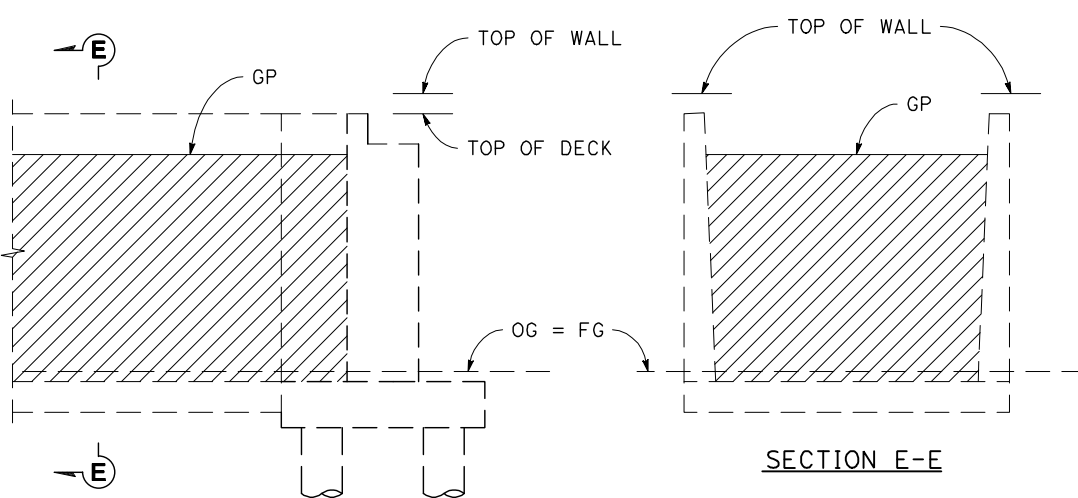


STEP 3 AND 4

ABUTMENT CONSTRUCTION SEQUENCE

- Step 1: Construct Abutment 1 and Abutment 17.
- Step 2: Construct RW "N" and RW "S" to 1' below top of wall elevations.
- Step 3: Place RW "N" and RW "S" backfill.
- Step 4: Allow the approaches to settle for the duration of time specified in the project specifications.
- Step 5: Construct RW "N" and RW "S" to top of wall elevations.
- Step 6: Place any additional backfill required due to settlement, and construct trail structural section to finished grade elevations.

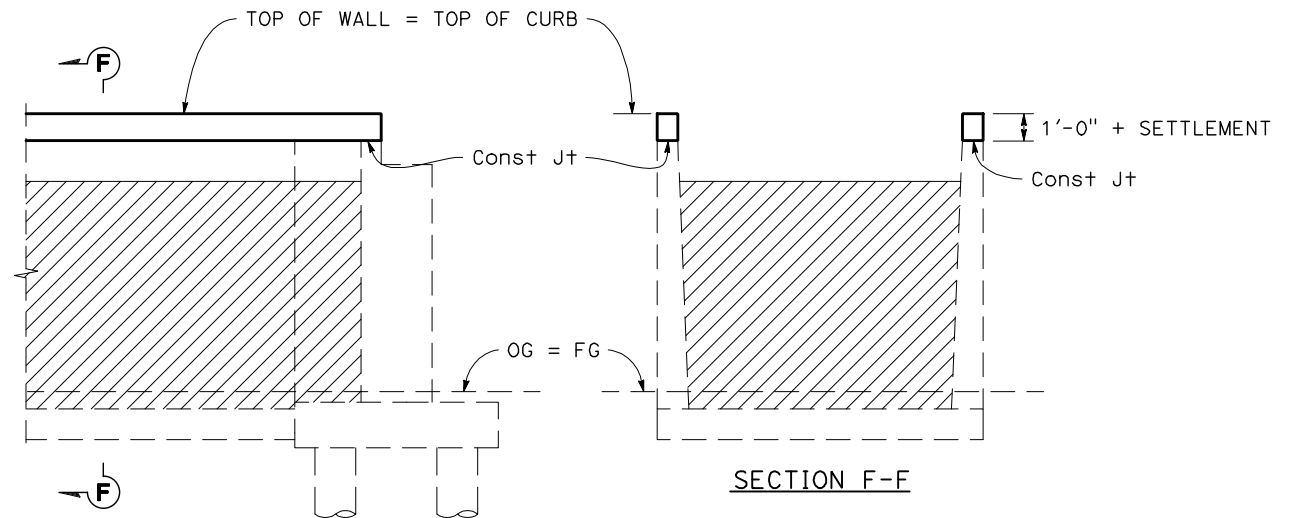

STEP 5

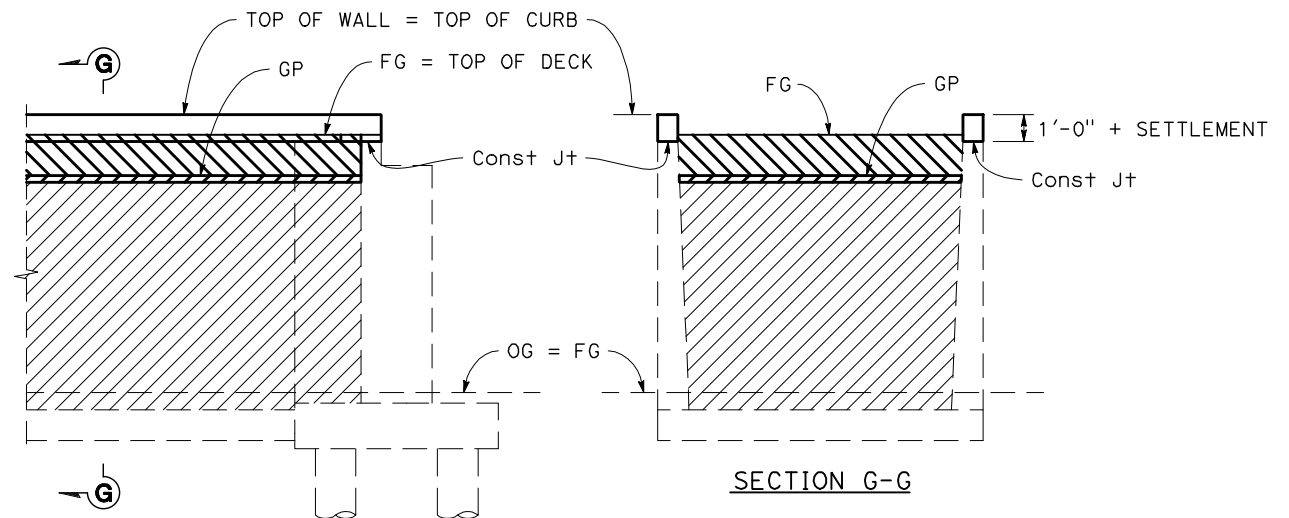

STEP 6

Note: Abutment 1 shown, Abutment 17 similar.

STRUCTURAL BACKFILL ROADWAY STRUCTURAL SECTION

X DESIGN OVERSIGHT X SIGN OFF DATE		DESIGN BY Y. REN DETAILS BY J. DOTY QUANTITIES BY X	CHECKED X X X	PREPARED FOR THE STATE OF CALIFORNIA DEPARTMENT OF TRANSPORTATION	ERIC FREDRICKSON PROJECT ENGINEER	BRIDGE No. 36-0128 POST MILE 10.87	MAR VISTA DRIVE POC ABUTMENT CONSTRUCTION SEQUENCE							
DESIGN DETAIL SHEET (ENGLISH) (REVISION 4/19/2018)		DATE PLOTTED => 11/17/2021 FILE => 06_MV_POC_ACS.dwg		TIME PLOTTED => 6:55 AM USERNAME => JVALENZUELA		ORIGINAL SCALE IN INCHES FOR REDUCED PLANS		0 1 2 3	UNIT: X PROJECT NUMBER & PHASE: 0518000116	CONTRACT No.: 05-0C7331	DISREGARD PRINTS BEARING EARLIER REVISION DATES	REVISION DATES 6-18-21	SHEET 8	OF 38


UTILITIES

- (A) Indicates Existing 4" Gas, PG&E to remain
- (B) Indicates Existing Comcast (OH) to remain
- (C) Indicates Existing 21kV, PG&E (OH) to remain
- (D) Indicates Existing 8"AC Water, SCWD to remain

DIST	COUNTY	ROUTE	POST MILES TOTAL PROJECT	SHEET No	TOTAL SHEETS
05	SCr	1	10.54/13.44	422	453

DRAFT 65% PLANS

REGISTERED STRUCTURAL ENGINEER DATE

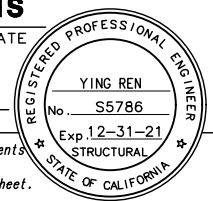


PLANS APPROVAL DATE

The State of California or its officers or agents shall not be responsible for the accuracy or completeness of scanned copies of this plan sheet.

MARK THOMAS
701 UNIVERSITY AVE., SUITE 200
SACRAMENTO, CA 95825

SCCRTC
1523 PACIFIC AVENUE
SANTA CRUZ, CA 95090

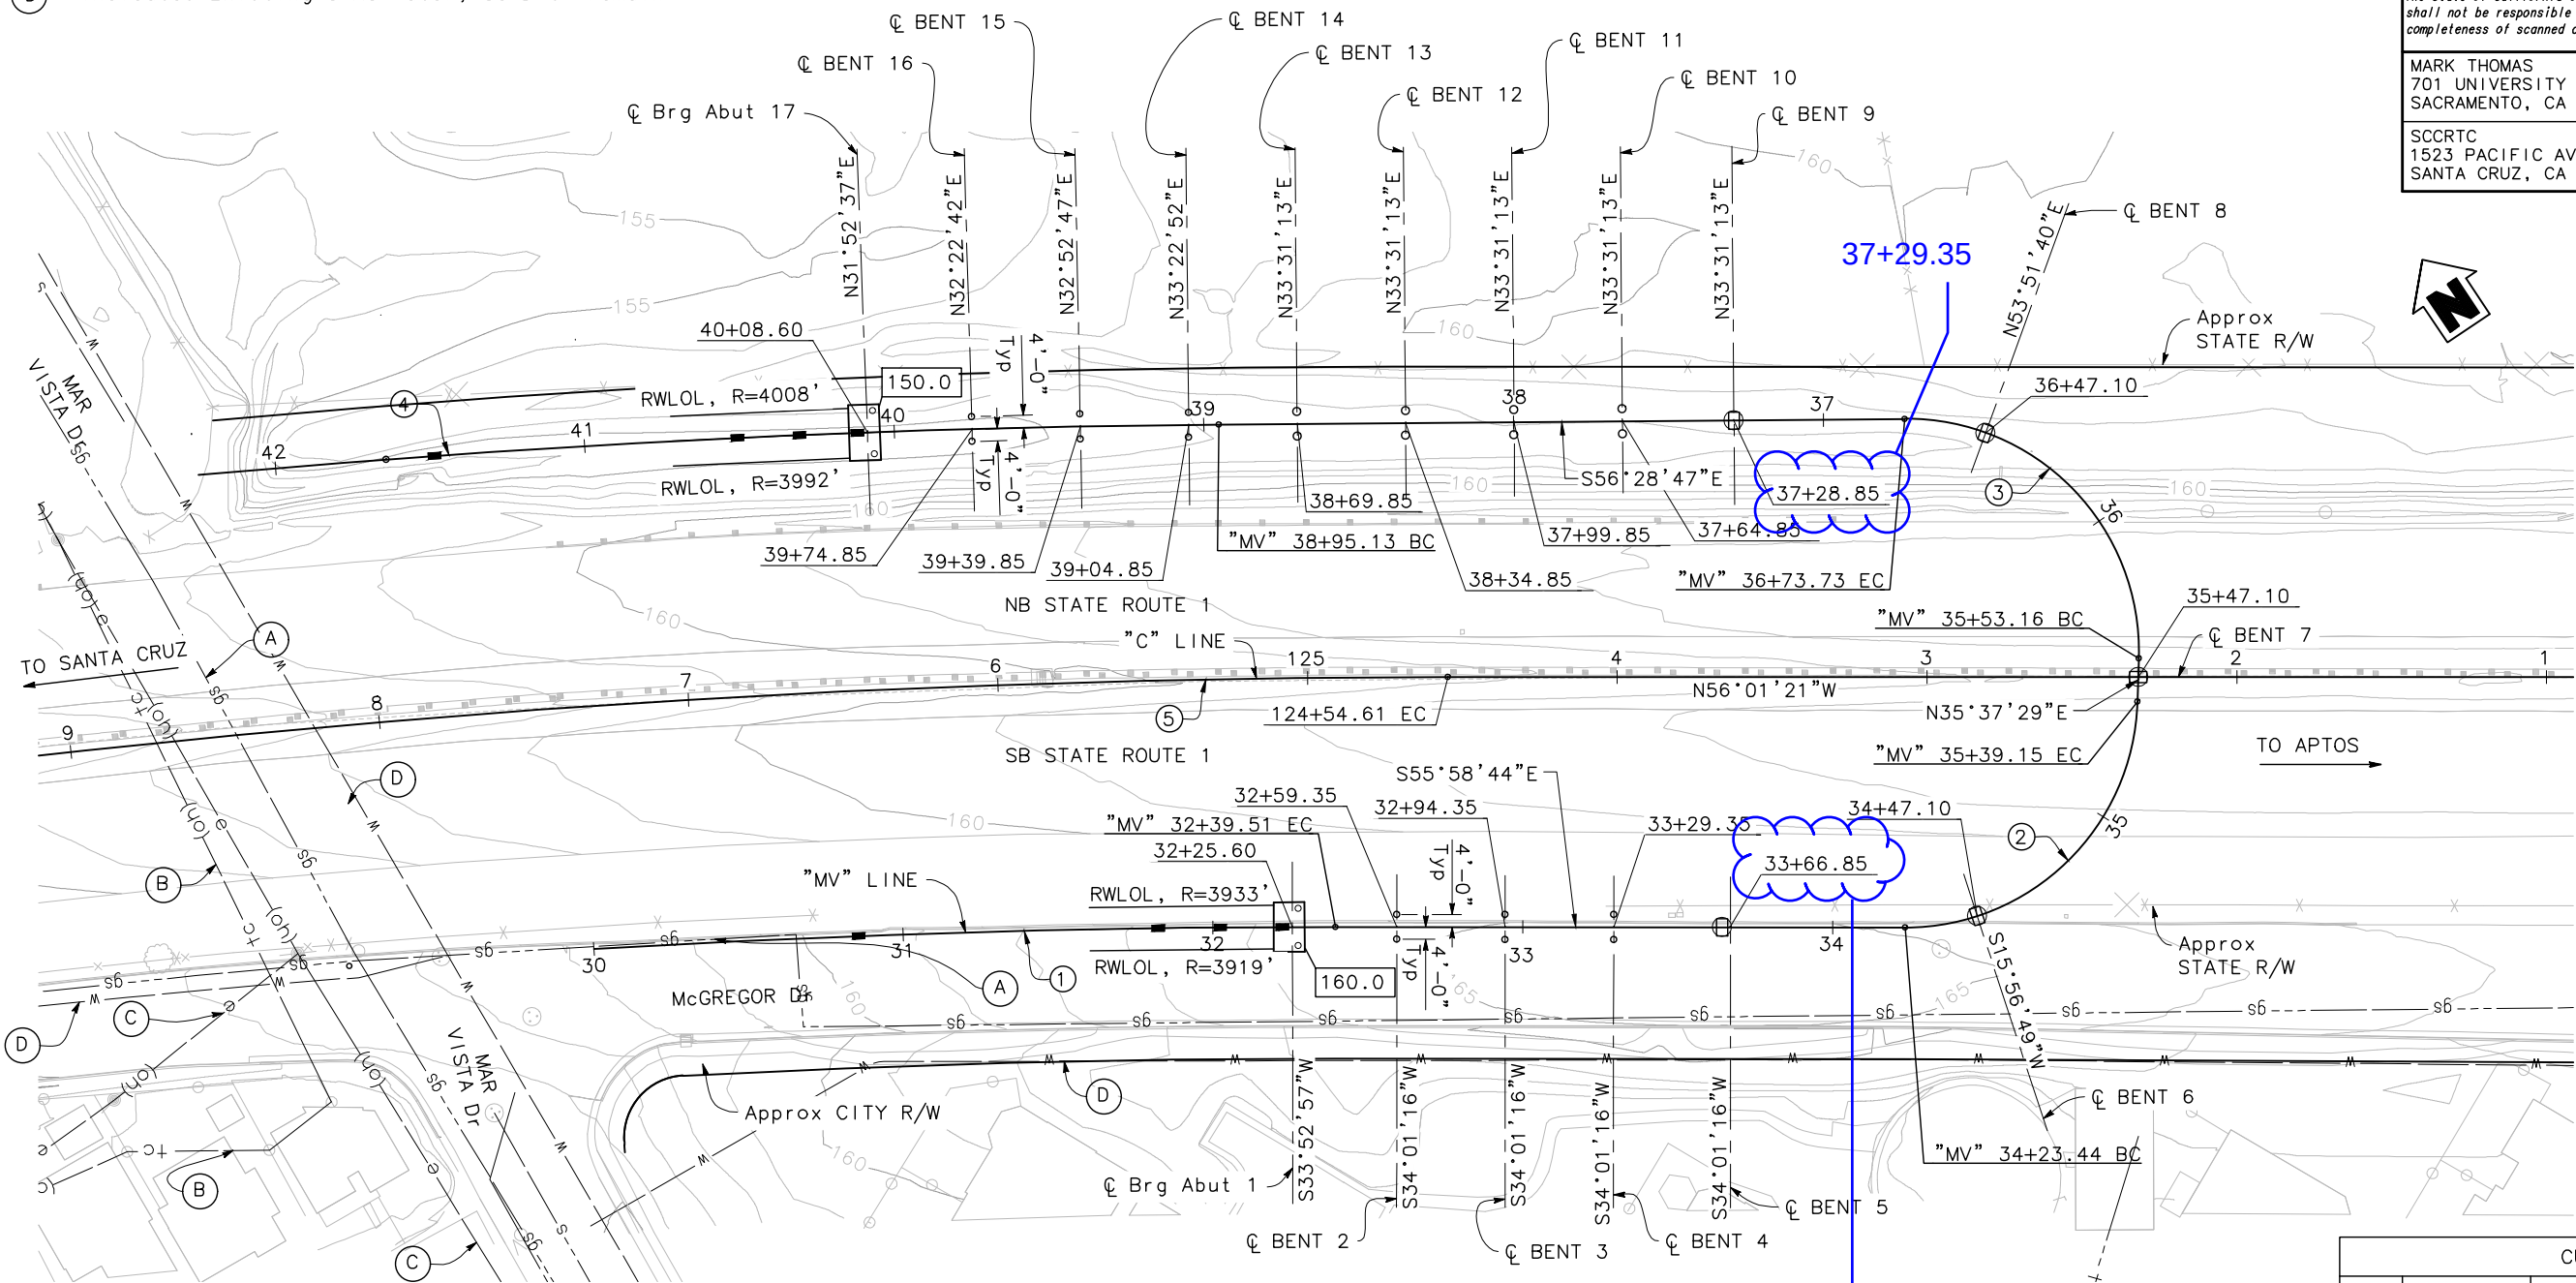

PLAN
1" = 30'

LEGEND:

- XXX.X Indicates Bottom of Footing Elevation (Feet)
- Indicates 72" Cast-In-Drilled-Hole Concrete Piling
- Indicates 24" Cast-In-Drilled-Hole Concrete Piling

NOTE:

For Pile Data Table, Retaining Wall Data Table and Benchmark Information, see "FOUNDATION PLAN No. 2" sheet.

CURVE DATA				
No.	R	Δ	T	L
①	3926.00'	3°29'43"	119.79'	239.51'
②	75.00'	88°23'48"	72.93'	115.71'
③	75.00'	92°06'16"	77.81'	120.56'
④	4000.00'	4°43'34"	165.07'	329.95'
⑤	4100.00'	23°16'26"	844.37'	1665.45'

DESIGN OVERSIGHT	SCALE: 1" = 30'	VERT. DATUM X	HORZ. DATUM X	DESIGN	BY Y. REN	CHECKED	T. PHAM	PREPARED FOR THE STATE OF CALIFORNIA DEPARTMENT OF TRANSPORTATION	E FREDRICKSON PROJECT ENGINEER	BRIDGE NO. 36-0128 POST MILES 10.87
	PHOTOGRAMMETRY AS OF: X	ALIGNMENT TIES X		DETAILS	BY J. DOTY	CHECKED				
	SURVEYED BY X	DRAFTED BY X		QUANTITIES	BY	CHECKED				
	FIELD CHECKED BY X	CHECKED BY X								

FOUNDATION PLAN SHEET (ENGLISH) (REV. 03/14/12)

ORIGINAL SCALE IN INCHES
FOR REDUCED PLANS

UNIT: PROJECT NUMBER & PHASE: 0518000116 CONTRACT NO.: 05-0C7331

FILE => 07-08_MV_POC_FP

MAR VISTA DRIVE POC
FOUNDATION PLAN No. 1

DISREGARD PRINTS BEARING
EARLIER REVISION DATES

REVISION DATES	SHEET	OF
6-18-21	422	453

TIME PLOTTED => 6:12 PM
USERNAME => SUBERNUEVA DATE PLOTTED => 11-Nov-21

PILE DATA TABLE

Location	Pile Type	Cut-off Elevations (ft)	Nominal Resistance (kips)		Design Tip Elevations (ft)	Specified Tip Elevations (ft)	Steel Casing Specified Tip Elevations (ft)	Bottom of Isolation Casing Elevations (ft)
			Compression	Tension				
Abut 1	24" CIDH	160.25	280	N/A	134.0 (a) 156.0 (c) 137.0 (d)	134.0	N/A	N/A
BENT 2	24" CIDH	165.0	320	-20	131.0 (a) 155.0 (b) 156.5 (c) 137.0 (d)	131.0	N/A	163.0
BENT 3	24" CIDH	165.0	280	-40	134.0 (a) 155.0 (b) 157.0 (c) 137.0 (d)	134.0	N/A	N/A
BENT 4	24" CIDH	165.0	320	-20	132.0 (a) 155.0 (b) 157.0 (c) 138.0 (d)	132.0	N/A	N/A
BENT 5	72" CIDH	163.0	660	N/A	133.0 (a) 149.0 (c) 119.0 (d)	119.0	150.5	N/A
BENT 6	72" CIDH	160.0	1230	N/A	112.0 (a) 139.0 (c) 106.0 (d)	106.0	147.5	160.0
BENT 7	72" CIDH	161.0	1350	N/A	103.0 (a) 143.5 (c) 106.0 (d)	103.0	148.5	N/A
BENT 8	72" CIDH	156.0	1350	N/A	101.0 (a) 132.0 (c) 103.0 (d)	101.0	143.5	N/A
BENT 9	72" CIDH	155.0	1320	N/A	115.0 (a) 139.0 (c) 105.0 (d)	105.0	142.5	N/A
BENT 10	30" CIDH	157.0	780	-10	111.0 (a) 147.0 (b) 149.5 (c) 131.0 (d)	111.0	N/A	N/A
BENT 11	30" CIDH	157.0	380	-20	120.0 (a) 147.0 (b) 149.5 (c) 129.0 (d)	120.0	N/A	N/A
BENT 12	30" CIDH	157.0	330	-20	120.0 (a) 147.0 (b) 149.5 (c) 130.0 (d)	120.0	N/A	N/A
BENT 13	30" CIDH	155.0	330	-20	120.0 (a) 147.0 (b) 149.5 (c) 130.0 (d)	120.0	N/A	155.00
BENT 14	24" CIDH	156.0	330	-20	120.0 (a) 146.0 (b) 148.5 (c) 128.0 (d)	120.0	N/A	N/A
BENT 15	24" CIDH	156.0	320	-30	117.0 (a) 146.0 (b) 149.0 (c) 130.0 (d)	117.0	N/A	N/A
BENT 16	24" CIDH	155.0	360	-10	113.0 (a) 145.0 (b) 148.0 (c) 130.0 (d)	113.0	N/A	N/A
Abut 17	24" CIDH	150.0	290	N/A	119.0 (a) 147.5 (c) 126.0 (d)	110.0	N/A	N/A

- (i) Design tip elevations for Abutments are controlled by: (a) Compression; (c) Settlement; (d) Lateral Load
(ii) Design tip elevations for Bents are controlled by: (a) Compression; (b) Tension; (c) Settlement; (d) Lateral Load

update/replace pile data table on next page

RETAINING WALL DATA TABLE

Bridge No.		Segment (ft)		Design Height (ft)	Service Limit State Permissible Net Contact Stress (ksf)	Strength Gross Nominal Bearing Resistance for Controlling Load Case $\phi_b = 0.55$ (ksf)	Extreme Event Gross Nominal Bearing Resistance $\phi_b = 0.80$ (ksf)
		Begin Station	End Station				
36-0128	"S" WALL	"MV" 30+16.94	"MV" 32+23.75	4-12	4.07	6.72	9.77
	"N" WALL	"MV" 40+14.60	"MV" 42+03.50	6-10	4.09	6.75	9.82

BENCHMARK

ORTHOMETRIC HEIGHTS SHOWN ARE NAVD88 BASED ON SANTA CRUZ COUNTY MONUMENTS AND CONTROL PROVIDED BY CALTRANS DISTRICT 5 BENCHMARKS.

Points #	BM:203	BM:233	BM:332
Elevation	NAVD88:129.78'	NAVD88:66.91'	NAVD88:117.37'
Description	40' N from C/L of Soquel Drive and 39' W from C/L of Fairway Drive in Conc Curb @ back of drop inlet @ entrance to Monterey Bay Heights, Standard Brass Cap	County brass tag in west end of a concrete ditch, near the overside drain, about 30' E of New Brighton Beach Access Road & 55' W of C/L of SPRR Tracks	Brass cap with rivet in concrete wingwall on N'LY side of Rodeo Gulch Bridge on Soquel Drive, 33' N'LY of the center of Soquel Drive
Northing	1821312.47	1819062.89	1821363.30
Easting	6139251.78	6141748.87	6132404.49

SCALE: 1" = 30'		VERT. DATUM: X		HORIZ. DATUM: X		DESIGN BY: Y. REN	CHECKED BY: T. PHAM	PREPARED FOR THE STATE OF CALIFORNIA DEPARTMENT OF TRANSPORTATION		BRIDGE NO. 36-0128	MAR VISTA DRIVE POC FOUNDATION PLAN No. 2	
DESIGN OVERSIGHT	PHOTOGRAMMETRY AS OF: X		ALIGNMENT TIES X		DETAILS BY: J. DOTY	CHECKED		E FREDRICKSON PROJECT ENGINEER	POST MILES 10.87			
SIGN OFF DATE	SURVEYED BY: X		DRAFTED BY: X		QUANTITIES BY:	CHECKED						
FOUNDATION PLAN SHEET (ENGLISH) (REV. 03/14/12)				ORIGINAL SCALE IN INCHES FOR REDUCED PLANS		0 1 2 3		UNIT: X PROJECT NUMBER & PHASE: 0518000116		CONTRACT NO.: 05-0C7331		
								DISREGARD PRINTS BEARING EARLIER REVISION DATES		REVISION DATES 6-18-21		
										SHEET 38		

TABLE 8: PILE DATA TABLE

Location	Cut-off Elevation (ft)	Pile Type	Nominal Resistance (kips)		Design Tip Elev. (ft)	Specified Tip Elev. (ft)	Steel Casing Specified Tip Elevation
			Compression	Tension			
Abut 1	160.0	24" CIDH (Type I Shaft)	330	N/A	126.0 (a), 156.0 (c), 137.0 (d)	126.0	N/A
Bent 2	163.0	24" CIDH (Type I Shaft)	300	90	129.0 (a), 147.0 (b), 156.5 (c), 135.0 (d)	129.0	N/A
Bent 3	165.0	24" CIDH (Type I Shaft)	260	90	136.0 (a), 150.0 (b), 157.0 (c), 138.0 (d)	136.0	N/A
Bent 4	165.0	24" CIDH (Type I Shaft)	300	60	134.0 (a), 157.0 (b), 157.0 (c), 141.0 (d)	134.0	N/A
Bent 5	163.0	72" CIDH (Type II Shaft)	660	0	133.0 (a), 149.0 (c), 118.0 (d)	118.0	150.5
Bent 6	160.0	72" CIDH (Type II Shaft)	1230	0	110.0 (a), 139.0 (c), 108.0 (d)	108.0	147.5
Bent 7	161.0	72" CIDH (Type II Shaft)	1460	0	103.0 (a), 143.5 (c), 108.0 (d)	103.0	148.5
Bent 8	156.0	72" CIDH (Type II Shaft)	1260	0	103.0 (a), 132.0 (c), 102.0 (d)	102.0	143.5
Bent 9	155.0	72" CIDH (Type II Shaft)	700	0	112.0 (a), 139.0 (c), 100.0 (d)	100.0	142.5
Bent 10	157.0	30" CIDH (Type II Shaft)	360	200	119.0 (a), 130.0 (b), 149.5 (c), 125.0 (d)	119.0	N/A
Bent 11	157.0	30" CIDH (Type II Shaft)	330	180	123.0 (a), 136.0 (b), 149.5 (c), 124.0 (d)	123.0	N/A
Bent 12	157.0	30" CIDH (Type II Shaft)	330	180	123.0 (a), 136.0 (b), 149.5 (c), 124.0 (d)	123.0	N/A
Bent 13	155.0	30" CIDH (Type II Shaft))	320	160	122.0 (a), 134.0 (b), 149.5 (c), 121.0 (d)	121.0	N/A
Bent 14	156.0	24" CIDH (Type I Shaft)	320	95	119.0 (a), 141.0 (b), 148.5 (c), 128.0 (d)	119.0	N/A
Bent 15	156.0	24" CIDH (Type I Shaft)	300	85	120.0 (a), 141.0 (b), 149.0 (c), 133.0 (d)	120.0	N/A
Bent 16	155.0	24" CIDH (Type I Shaft)	350	95	114.0 (a), 140.0 (b), 148.0 (c), 131.0 (d)	114.0	N/A
Abut 17	150.0	24" CIDH (Type I Shaft)	390	N/A	103.0 (a), 137.0 (c), 126.0 (d)	103.0	N/A

- (1) Design tip elevations for Abutments are controlled by: (a) Compression, (c) Settlement and (d) Lateral Load
- (2) Design tip elevations for Bents are controlled by: (a) Compression, (b) Tension, (c) Settlement, (d) Lateral Load.
- (3) Isolation Casing used for structural design and casing tip elevations were provided by the designer.
- (4) Type II shaft with 12.5 feet embedment depth of permanent steel casing is recommended below construction joint for bent 5 through 9 piles.



Dist05COUNTYSCRROUTE1POST MILESTOTAL PROJECT10.54/13.44SHEET NO.424TOTAL SHEETS453

DRAFT 65% PLANS

REGISTERED STRUCTURAL ENGINEER DATE






YING REN
No. S5786
Exp. 12-31-21
STRUCTURAL
STATE OF CALIFORNIA

PLANS APPROVAL DATE

THE STATE OF CALIFORNIA OR ITS OFFICERS OR AGENTS SHALL NOT BE RESPONSIBLE FOR THE ACCURACY OR COMPLETENESS OF SCANNED COPIES OF THIS PLAN SHEET.

MARK THOMAS
701 UNIVERSITY AVE., SUITE 200
SACRAMENTO, CA 95825

SCCRTC
1523 PACIFIC AVENUE
SANTA CRUZ, CA 95090

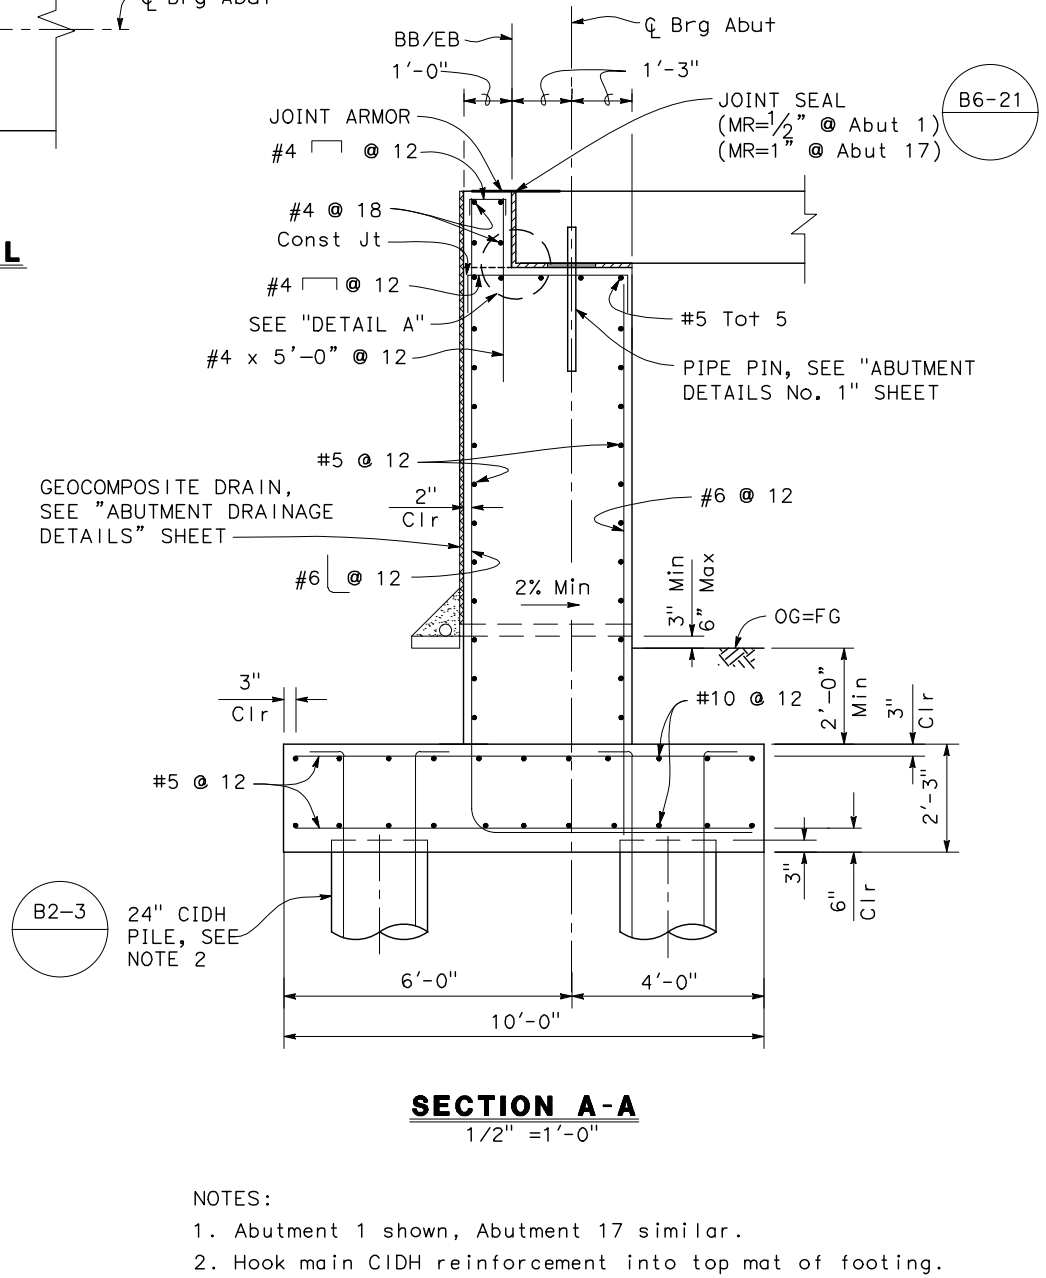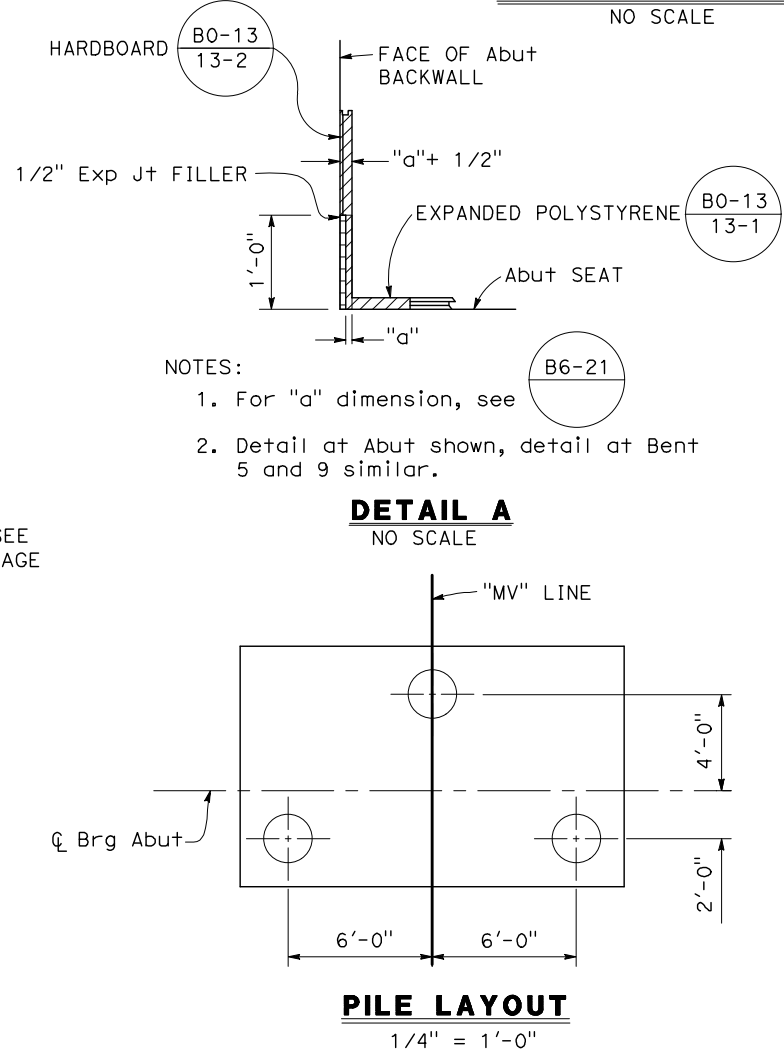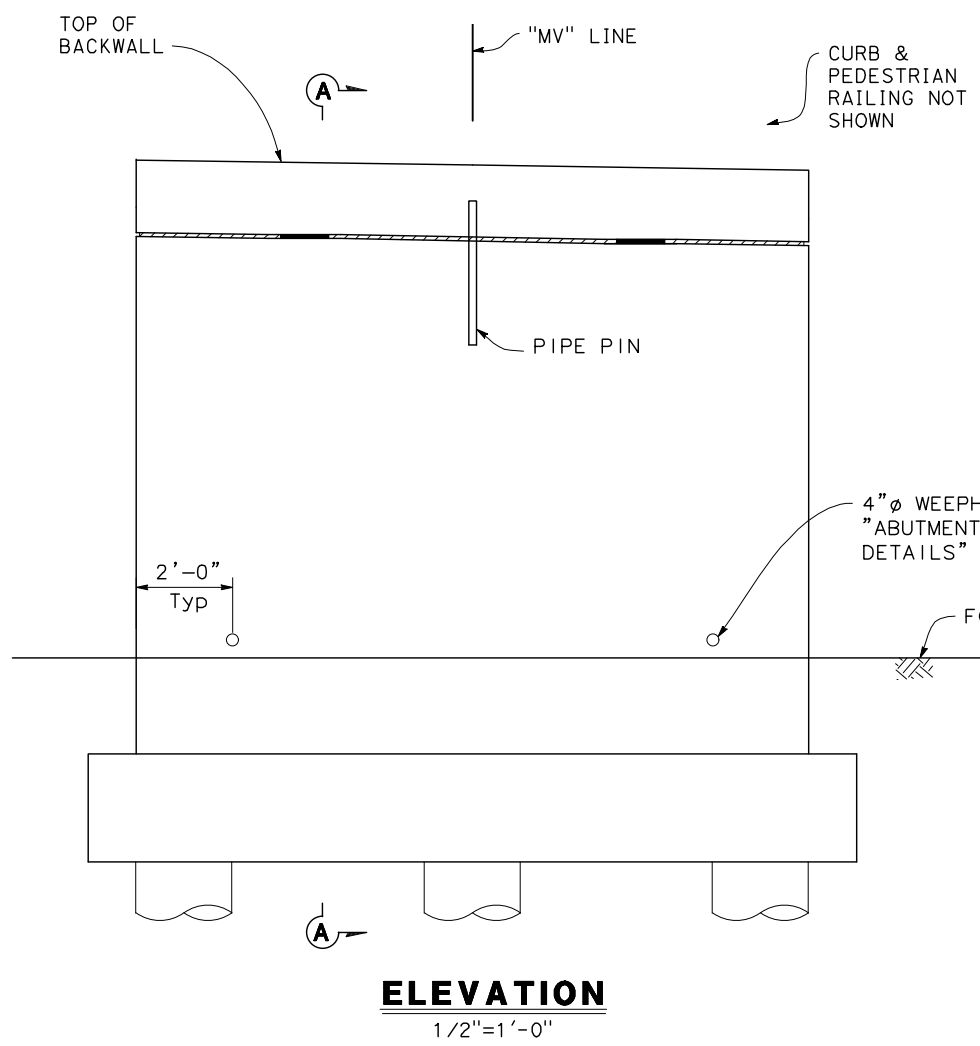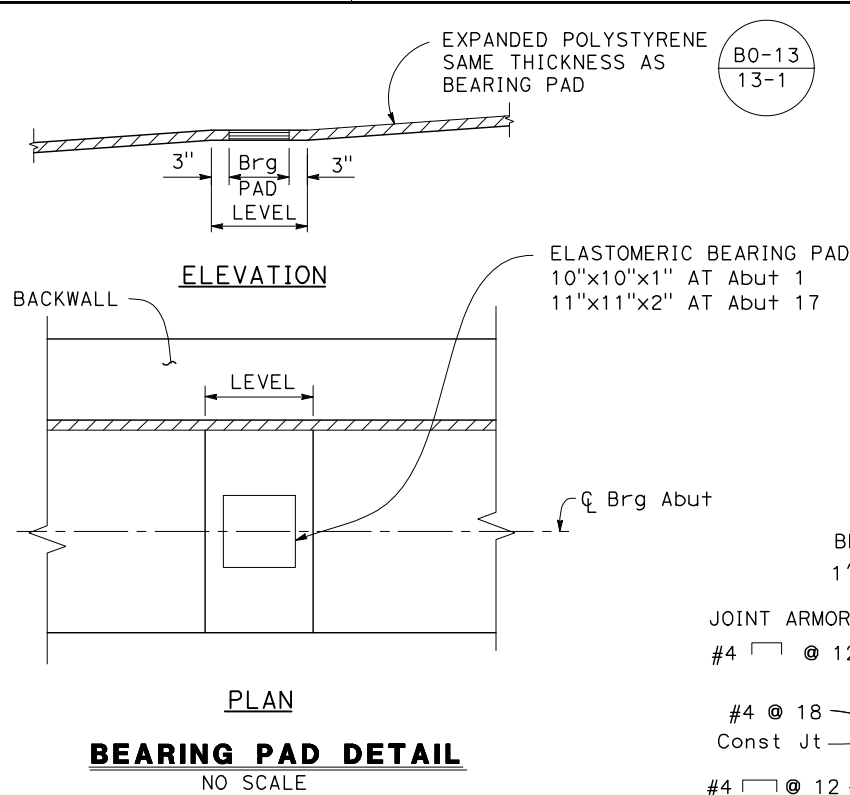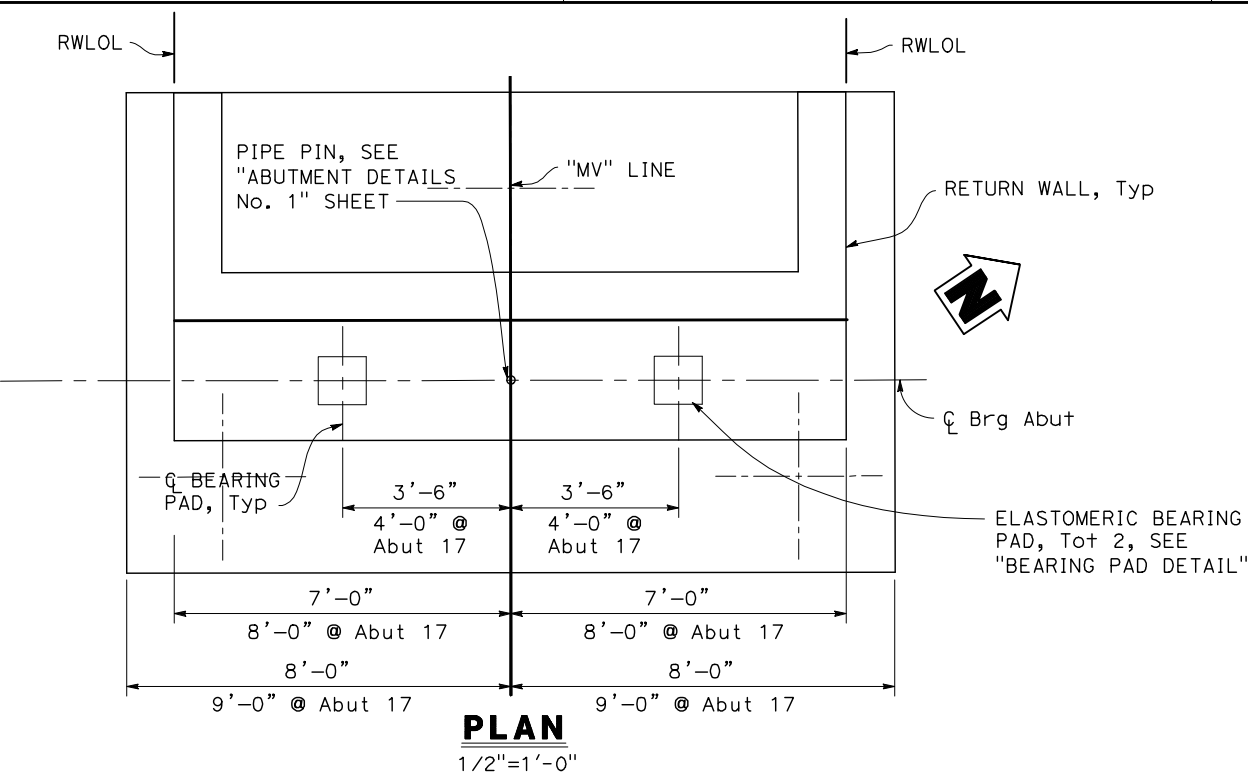

Dist	COUNTY	ROUTE	POST MILES TOTAL PROJECT	SHEET No.	TOTAL SHEETS
05	Scr	1	10.54/13.44	425	453

DRAFT 65% PLANS




REGISTERED STRUCTURAL ENGINEER DATE

PLANS APPROVAL DATE


THE STATE OF CALIFORNIA OR ITS OFFICERS OR AGENTS
SHALL NOT BE RESPONSIBLE FOR THE ACCURACY OR
COMPLETENESS OF SCANNED COPIES OF THIS PLAN SHEET.

MARK THOMAS
701 UNIVERSITY AVE., SUITE 200
SACRAMENTO, CA 95825


SCCRTC
1523 PACIFIC AVENUE
SANTA CRUZ, CA 95090

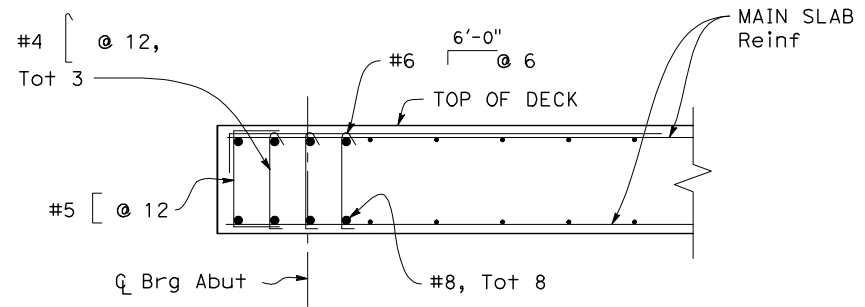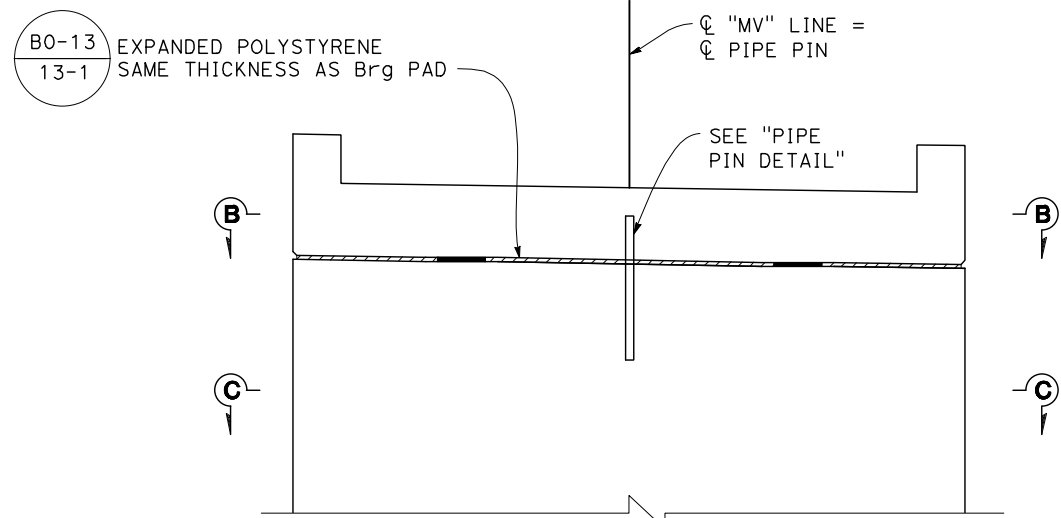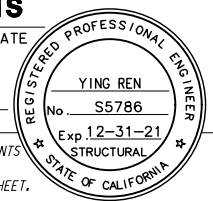


END DIAPHRAGM
3/4" = 1'-0"

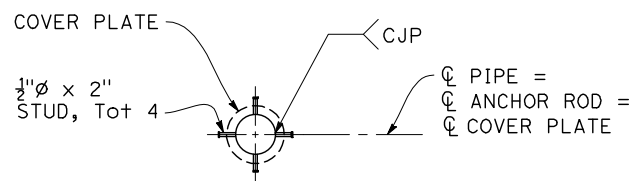


STUD DETAIL
1" = 1'-0"

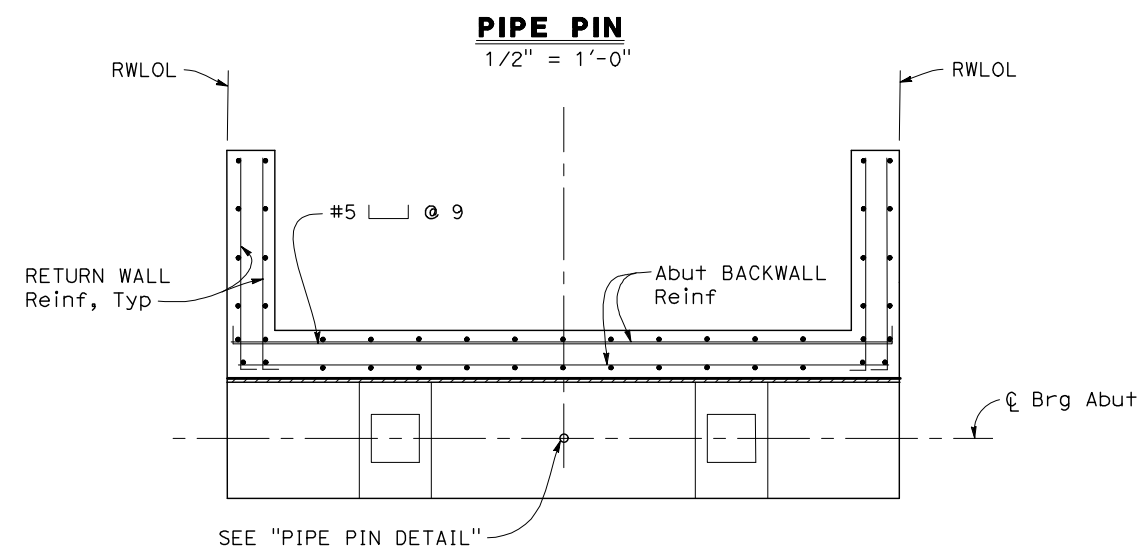

SECTION B-B
1/2" = 1'-0"

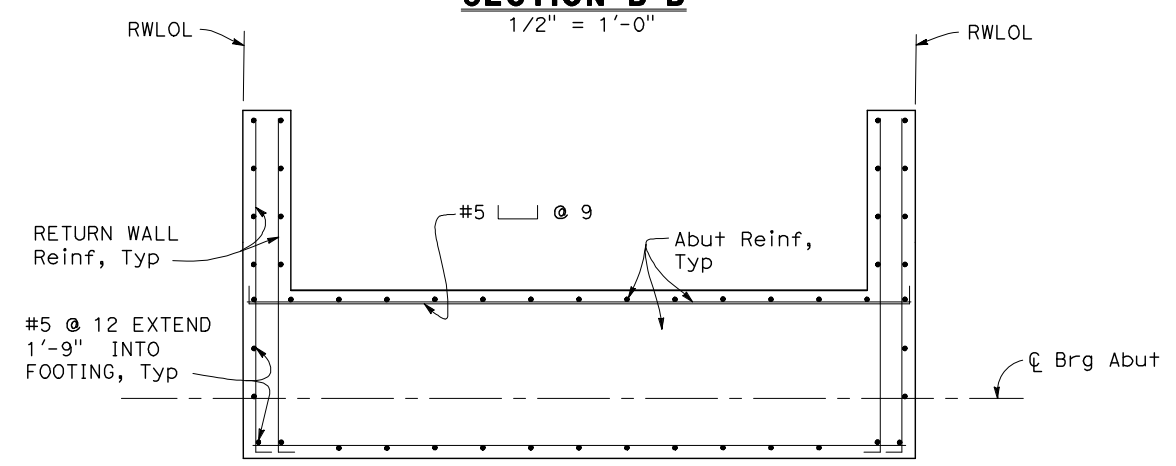

SECTION C-C
1/2" = 1'-0"

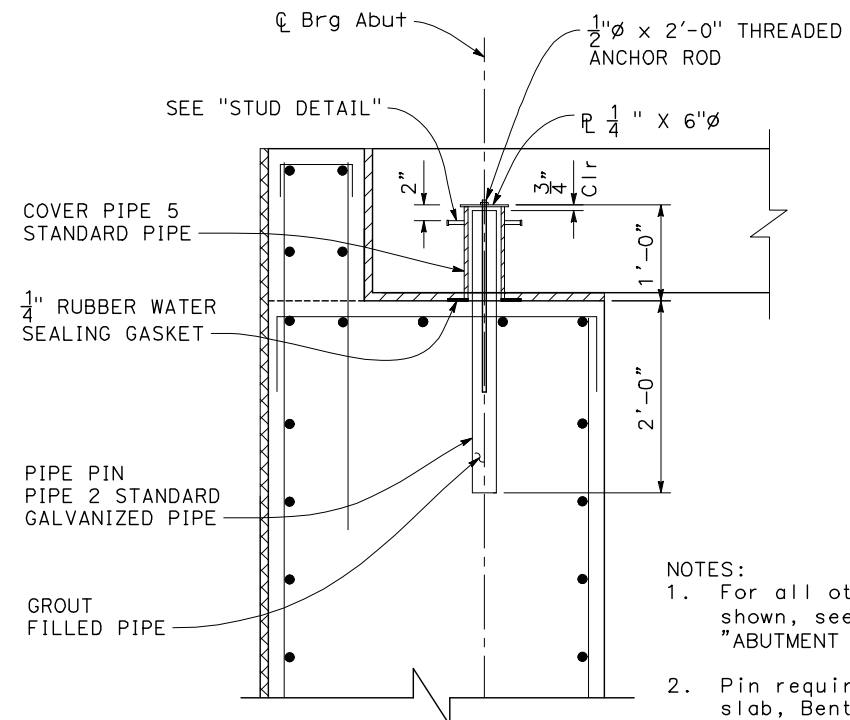

PIPE PIN DETAIL
1" = 1'-0"

- NOTES:
- For all other information not shown, see "SECTION A-A" on "ABUTMENT LAYOUT" sheet.
 - Pin required at all end of slab, Bents 5, 9, and 13.


X DESIGN OVERSIGHT X SIGN OFF DATE	DESIGN BY Y. REN DETAILS BY J. DOTY QUANTITIES BY X	CHECKED X CHECKED X CHECKED X	PREPARED FOR THE STATE OF CALIFORNIA DEPARTMENT OF TRANSPORTATION	ERIC FREDRICKSON PROJECT ENGINEER	BRIDGE No.	MAR VISTA DRIVE POC ABUTMENT DETAILS No. 1			
					36-0128				
DATE PLOTTED => 11/17/2021 FILE => 10-11_MV_POC_AD.dwg				UNIT: X PROJECT NUMBER & PHASE: 0518000116		CONTRACT No.: 05-0C7331	REVISION DATES 6-18-21	SHEET 40	OF 38

Dist	COUNTY	ROUTE	POST MILES TOTAL PROJECT	SHEET No.	TOTAL SHEETS
05	Scr	1	10.54/13.44	426	453

DRAFT 65% PLANS

REGISTERED STRUCTURAL ENGINEER DATE


PLANS APPROVAL DATE

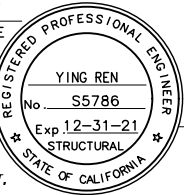

THE STATE OF CALIFORNIA OR ITS OFFICERS OR AGENTS
SHALL NOT BE RESPONSIBLE FOR THE ACCURACY OR
COMPLETENESS OF SCANNED COPIES OF THIS PLAN SHEET.


MARK THOMAS
701 UNIVERSITY AVE., SUITE 200
SACRAMENTO, CA 95825

SCCRTC
1523 PACIFIC AVENUE
SANTA CRUZ, CA 95090

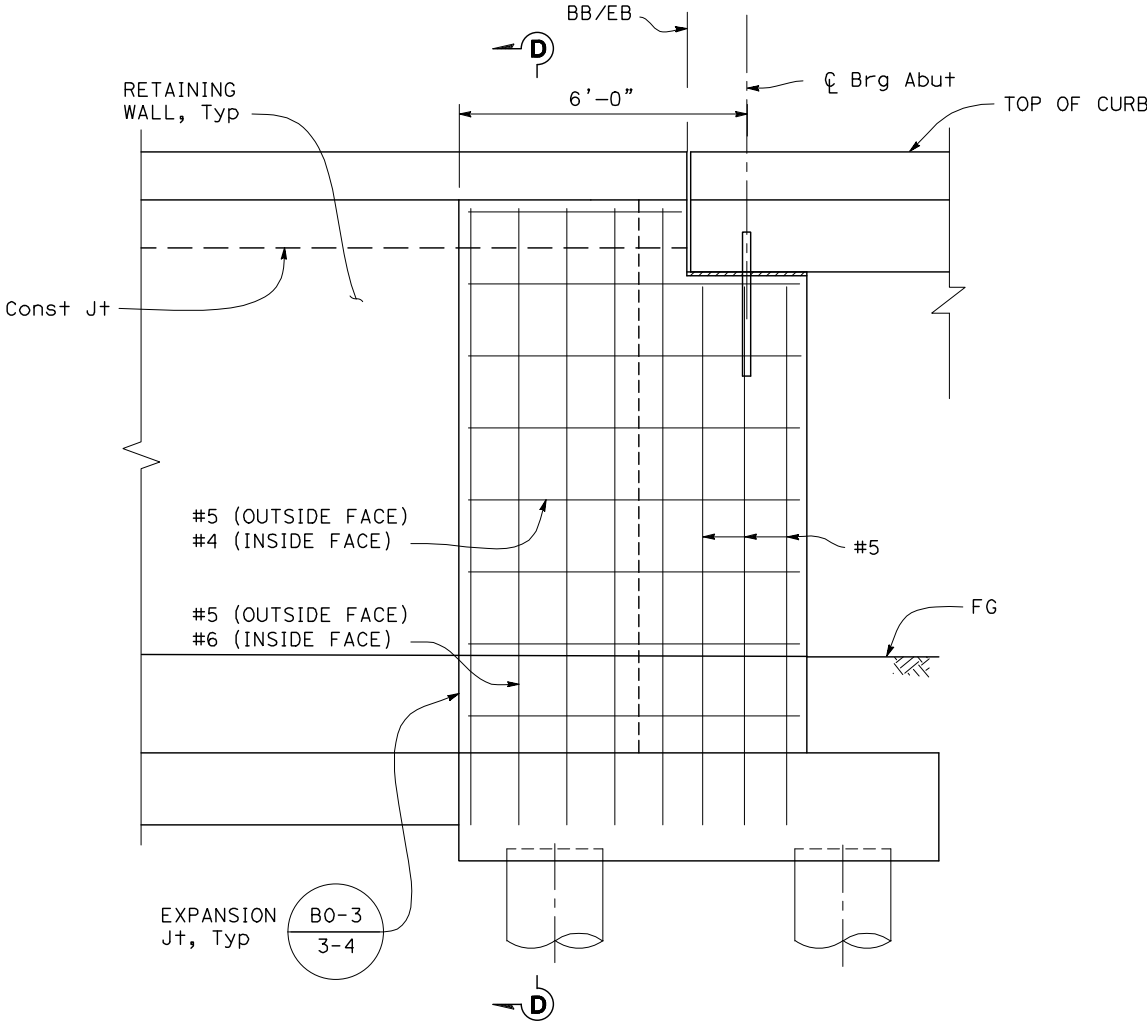

RETURN WALL ELEVATION

1/2" = 1'-0"

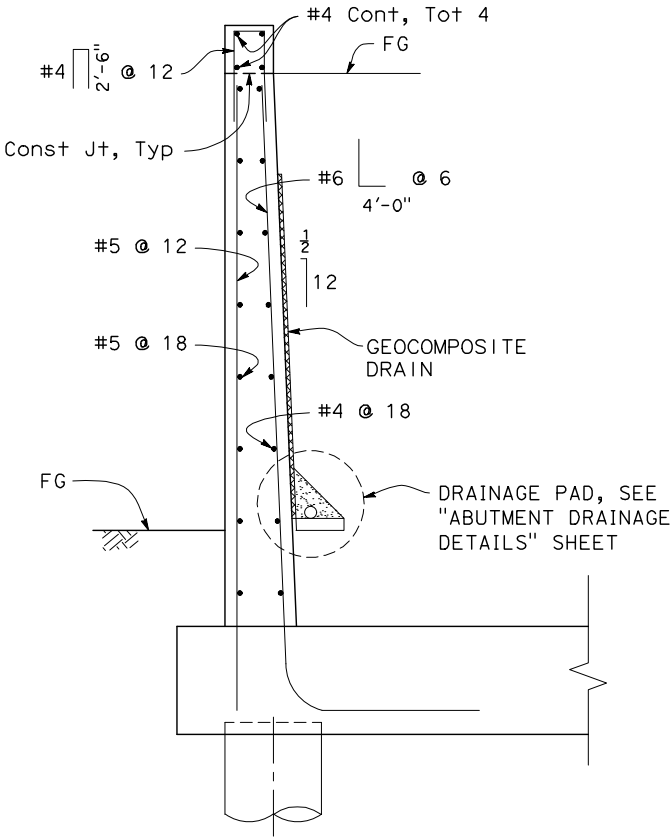

SECTION D-D

1/2" = 1'-0"

X
DESIGN OVERSIGHT
X
SIGN OFF DATE

DESIGN	BY Y. REN	CHECKED X
DETAILS	BY J. DOTY	CHECKED X
QUANTITIES	BY X	CHECKED X

**PREPARED FOR THE
STATE OF CALIFORNIA
DEPARTMENT OF TRANSPORTATION**

ERIC FREDRICKSON
PROJECT ENGINEER

BRIDGE No.
36-0128
POST MILE
10.87

**MAR VISTA DRIVE POC
ABUTMENT DETAILS No. 2**

DESIGN DETAIL SHEET
(ENGLISH) (REVISION 4/19/2018)

DATE PLOTTED => 11/17/2021
FILE => 10-11_MV_POC_AD.dwg

TIME PLOTTED => 9:37 AM
USERNAME => JVALENZUELA
ORIGINAL SCALE
IN INCHES FOR
REDUCED PLANS

0 1 2 3

UNIT: X
PROJECT NUMBER & PHASE: 0518000116

CONTRACT No.: 05-OC7331

DISREGARD PRINTS BEARING
EARLIER REVISION DATES

REVISION DATES
6-18-21

SHEET
1

OF
38

DRAFT 65% PLANS	
REGISTERED STRUCTURAL ENGINEER	DATE _____
PLANS APPROVAL DATE _____	
THE STATE OF CALIFORNIA OR ITS OFFICERS OR AGENTS SHALL NOT BE RESPONSIBLE FOR THE ACCURACY OR COMPLETENESS OF SCANNED COPIES OF THIS PLAN SHEET.	
MARK THOMAS 701 UNIVERSITY AVE., SUITE 200 SACRAMENTO, CA 95825	
SCCRTC 1523 PACIFIC AVENUE SANTA CRUZ, CA 95090	





X DESIGN OVERSIGHT X SIGN OFF DATE		DESIGNBY Y. REN DETAILSBY J. DOTY QUANTITIESBY X		CHECKED X CHECKED X CHECKED X		PREPARED FOR THE STATE OF CALIFORNIA DEPARTMENT OF TRANSPORTATION		ERIC FREDRICKSON PROJECT ENGINEER		BRIDGE No. 36-0128 POST MILE 10.87		MAR VISTA DRIVE POC RETAINING WALL "S" LAYOUT					
DESIGN DETAIL SHEET (ENGLISH) (REVISION 4/19/2018)		DATE PLOTTED => 11/11/2021 FILE => 12_MV_POC_RWLS.dwg USERNAME => JVALENZUELA		TIME PLOTTED => 6:49 PM ORIGINAL SCALE IN INCHES FOR REDUCED PLANS		0123		UNIT: X PROJECT NUMBER & PHASE: 0518000116 CONTRACT No.: 05-OC7331		DISREGARD PRINTS BEARING EARLIER REVISION DATES		REVISION DATES 6-18-21		SHEET 2		OF 38	

DRAFT 65% PLANS	
REGISTERED STRUCTURAL ENGINEER	DATE _____
PLANS APPROVAL DATE _____	
<i>THE STATE OF CALIFORNIA OR ITS OFFICERS OR AGENTS SHALL NOT BE RESPONSIBLE FOR THE ACCURACY OR COMPLETENESS OF SCANNED COPIES OF THIS PLAN SHEET.</i>	
MARK THOMAS 701 UNIVERSITY AVE., SUITE 200 SACRAMENTO, CA 95825	
SCCRTC 1523 PACIFIC AVENUE SANTA CRUZ, CA 95090	






Dist	COUNTY	ROUTE	POST MILES TOTAL PROJECT	SHEET NO.	TOTAL SHEETS
05	Scr	1	10.54/13.44	429	453

DRAFT 65% PLANS

REGISTERED STRUCTURAL ENGINEER DATE

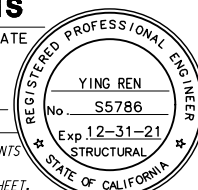


PLANS APPROVAL DATE

THE STATE OF CALIFORNIA OR ITS OFFICERS OR AGENTS
SHALL NOT BE RESPONSIBLE FOR THE ACCURACY OR
COMPLETENESS OF SCANNED COPIES OF THIS PLAN SHEET.

MARK THOMAS
701 UNIVERSITY AVE., SUITE 200
SACRAMENTO, CA 95825

SCCRTC
1523 PACIFIC AVENUE
SANTA CRUZ, CA 95090

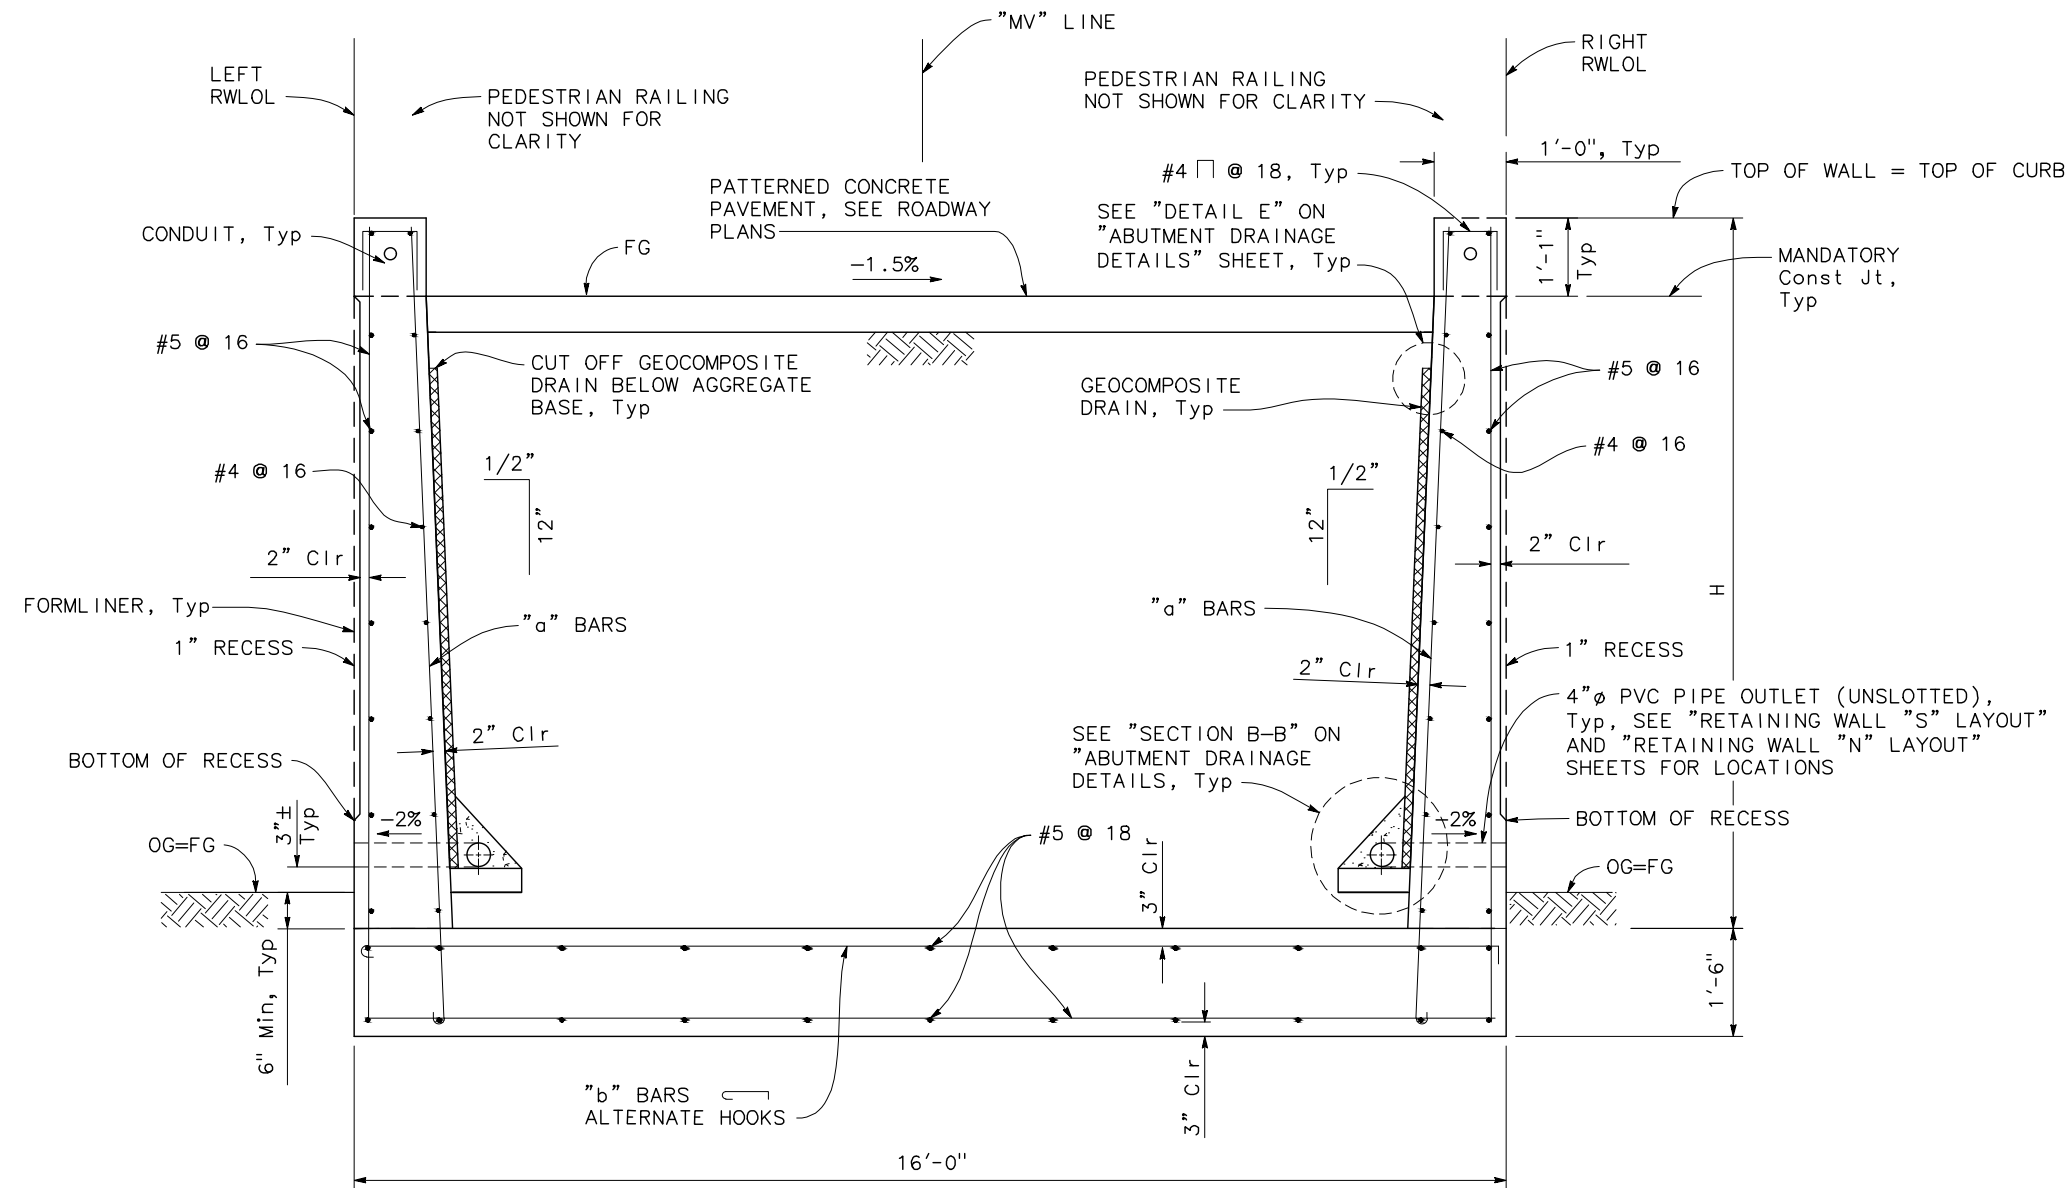

TYPICAL SECTION

3/4" = 1'-0"


DESIGN H	"a" Bars"	"b" Bars"
4'	#7 @ 12	#7 @ 12
6'	#7 @ 10	#7 @ 10
8'	#7 @ 12	#8 @ 12
10'	#7 @ 12	#9 @ 12
12'	#7 @ 10	#10 @ 10





Notes:

- At "a" bars:
H ≤ 6', no splices are allowed within 1'-8" above the top of footing.
H > 6', no splices are allowed within H/4 above the top of footing.
- Provide #6 @ 8 "a" bars in addition to tabulated "a" bars over a distance of 8'-0" measured from all expansion joints, begin wall and end wall locations.

X DESIGN OVERSIGHT X SIGN OFF DATE	DESIGN BY Y. REN DETAILS BY J. DOTY QUANTITIES BY X	CHECKED X CHECKED X CHECKED X	PREPARED FOR THE STATE OF CALIFORNIA DEPARTMENT OF TRANSPORTATION	ERIC FREDRICKSON PROJECT ENGINEER	BRIDGE No.	MAR VISTA DRIVE POC RETAINING WALL DETAILS			
					36-0128				
					POST MILE 10.87				
DESIGN DETAIL SHEET (ENGLISH) (REVISION 4/19/2018)	DATE PLOTTED => 11/17/2021 FILE => 14_MV_POC_RWD.dwg	TIME PLOTTED => 10:28 AM USERNAME => JVALENZUELA	ORIGINAL SCALE IN INCHES FOR REDUCED PLANS	UNIT: X PROJECT NUMBER & PHASE: 0518000116	CONTRACT No.: 05-OC7331	DISREGARD PRINTS BEARING EARLIER REVISION DATES	REVISION DATES	SHEET 74	OF 38

DRAFT 65% PLANS	
REGISTERED STRUCTURAL ENGINEER	DATE _____
PLANS APPROVAL DATE _____	
THE STATE OF CALIFORNIA OR ITS OFFICERS OR AGENTS SHALL NOT BE RESPONSIBLE FOR THE ACCURACY OR COMPLETENESS OF SCANNED COPIES OF THIS PLAN SHEET.	
MARK THOMAS 701 UNIVERSITY AVE., SUITE 200 SACRAMENTO, CA 95825	
SCCRTC 1523 PACIFIC AVENUE SANTA CRUZ, CA 95090	

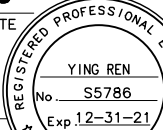

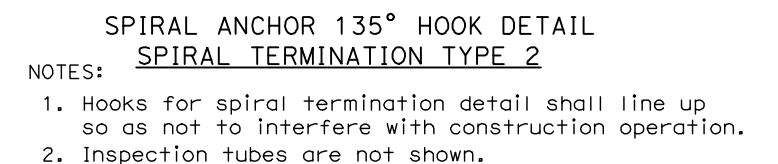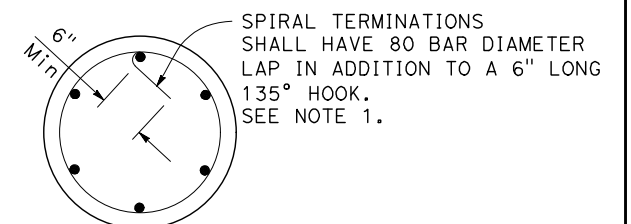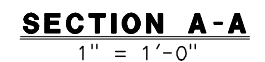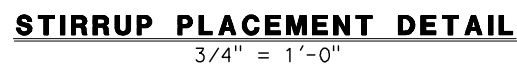

41

X DESIGN OVERSIGHT X SIGN OFF DATE	DESIGN	BY Y. REN	CHECKED X	PREPARED FOR THE STATE OF CALIFORNIA DEPARTMENT OF TRANSPORTATION	ERIC FREDRICKSON PROJECT ENGINEER	BRIDGE No.	MAR VISTA DRIVE POC BENT 2 THRU 4, 10 THRU 16 LAYOUT AND DETAILS						
	DETAILS	BY J. DOTY	CHECKED X			36-0128							
	QUANTITIES	BY X	CHECKED X			POST MILE							
						10.87							
DESIGN DETAIL SHEET (ENGLISH) (REVISION 4/19/2018)				DATE PLOTTED => 11/17/2021 FILE => 15_MV_POC_B2L.dwg USERNAME => JVALENZUELA		TIME PLOTTED => 2:41 PM ORIGINAL SCALE 1 IN INCHES FOR 10 FEET REDUCED PLANS		UNIT: X PROJECT NUMBER & PHASE: 0518000116	CONTRACT No.: 05-OC7331	DISREGARD PRINTS BEARING EARLIER REVISION DATES	REVISION DATES	SHEET 5	OF 38

Dist	COUNTY	ROUTE	POST MILES TOTAL PROJECT	SHEET NO.	TOTAL SHEETS
05	Scr	1	10.54/13.44	431	453

DRAFT 65% PLANS







REGISTERED STRUCTURAL ENGINEER DATE

PLANS APPROVAL DATE

THE STATE OF CALIFORNIA OR ITS OFFICERS OR AGENTS
SHALL NOT BE RESPONSIBLE FOR THE ACCURACY OR
COMPLETENESS OF SCANNED COPIES OF THIS PLAN SHEET.

MARK THOMAS
701 UNIVERSITY AVE., SUITE 200
SACRAMENTO, CA 95825

SCCRTC
1523 PACIFIC AVENUE
SANTA CRUZ, CA 95090

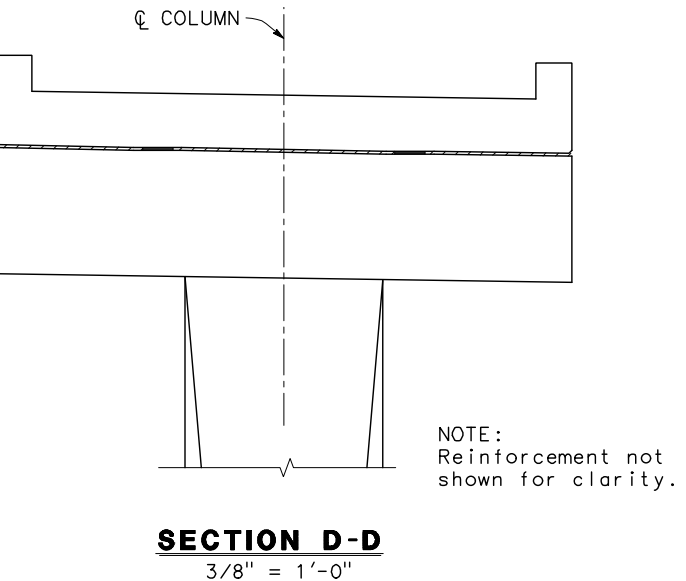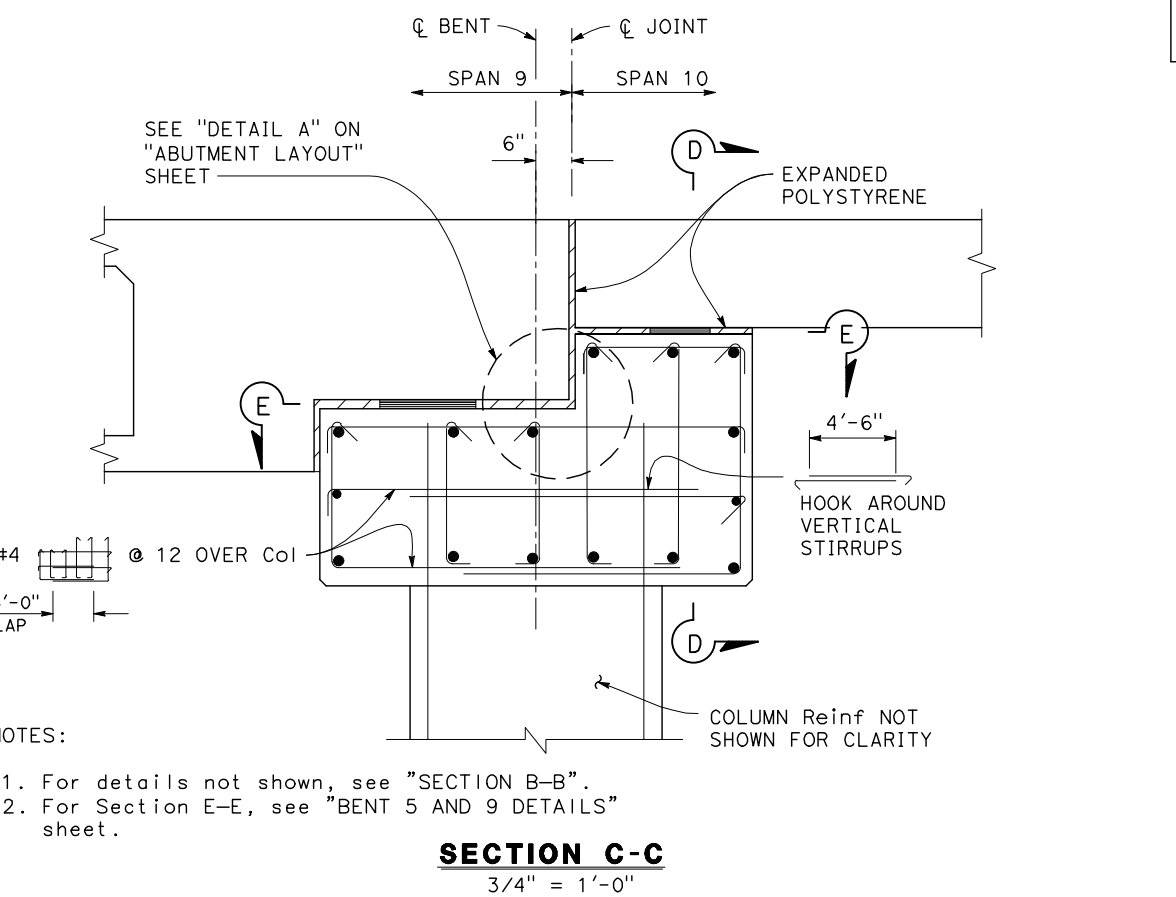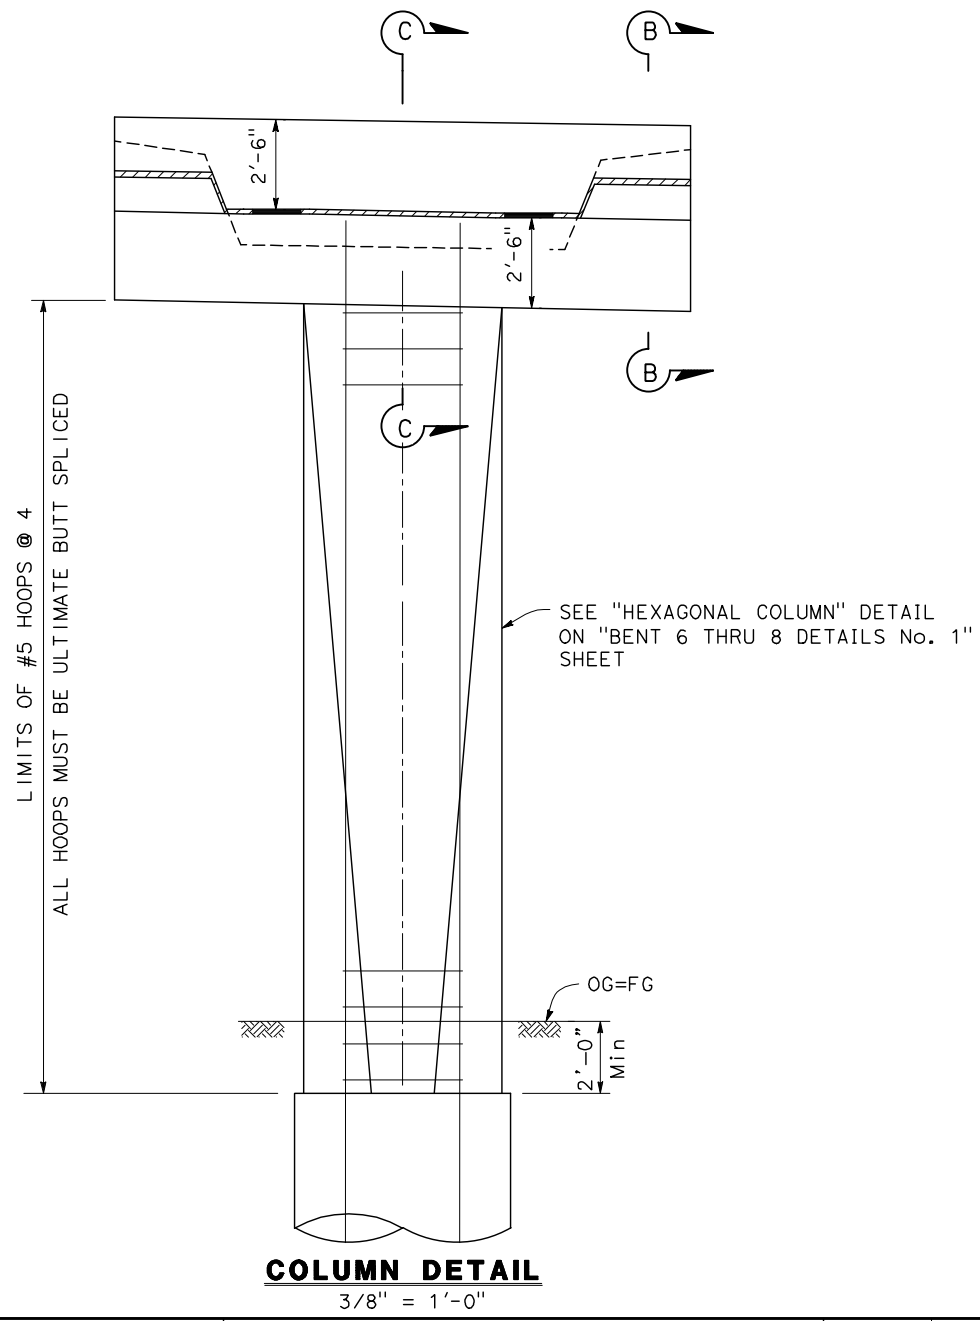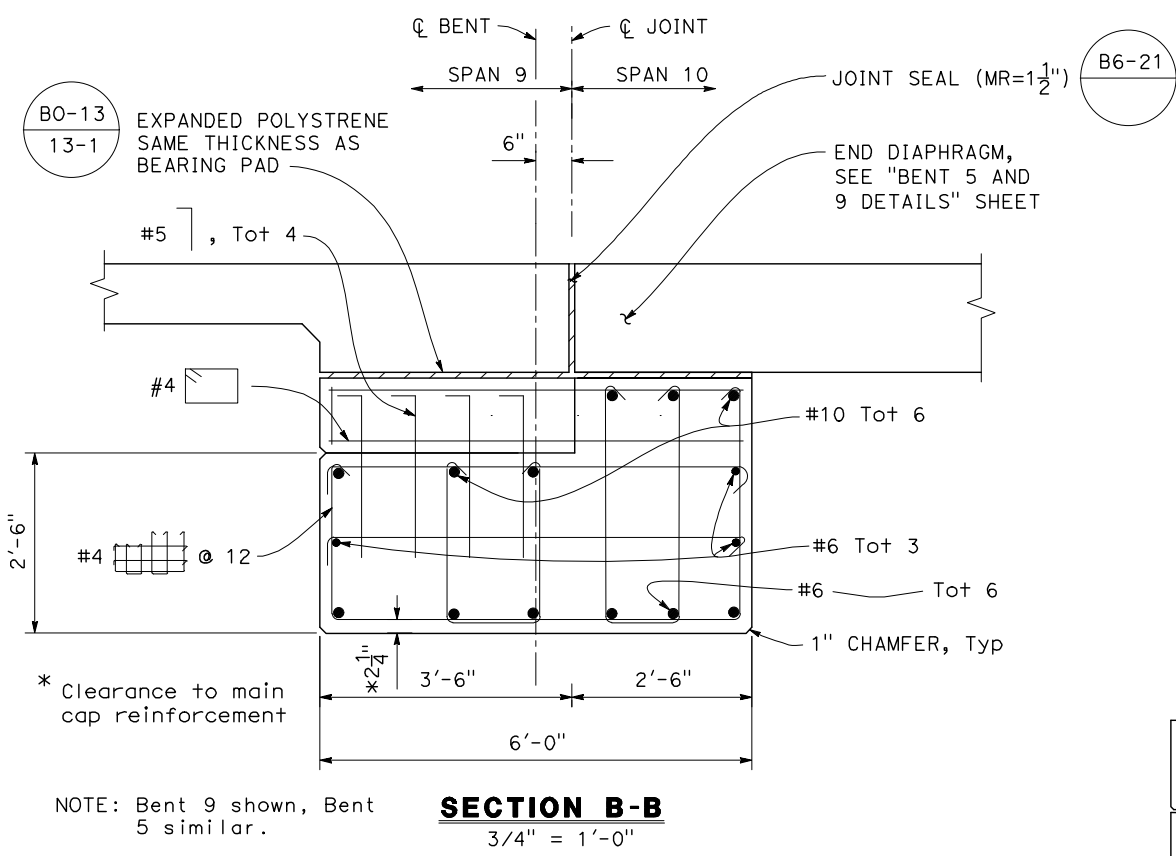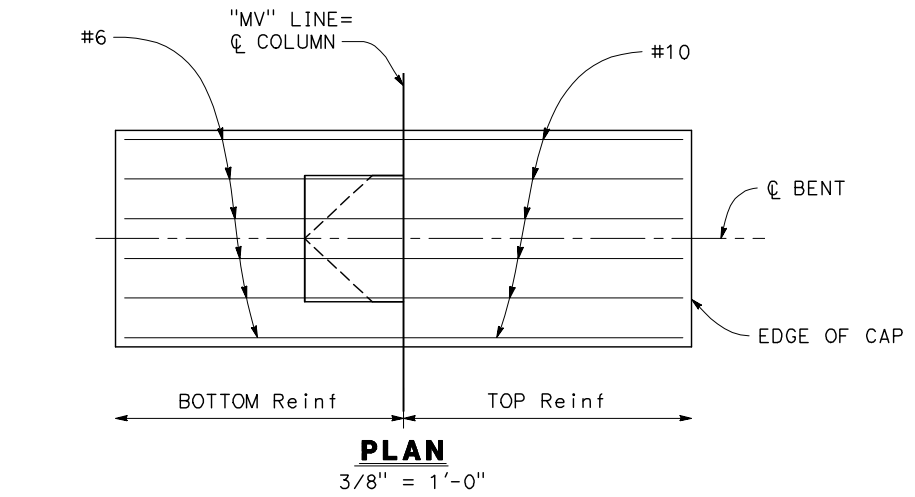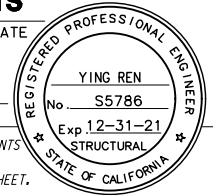

- NOTES:
1. For details not shown, see "SECTION B-B".
 2. For Section E-E, see "BENT 5 AND 9 DETAILS" sheet.

DESIGN BY Y. REN CHECKED X		DETAILS BY J. DOTY CHECKED X		QUANTITIES BY X CHECKED X		PREPARED FOR THE STATE OF CALIFORNIA DEPARTMENT OF TRANSPORTATION		BRIDGE No. 36-0128 POST MILE 10.87		MAR VISTA DRIVE POC BENT 5 AND 9 LAYOUT	
DESIGN OVERSIGHT X		SIGN OFF DATE		DATE PLOTTED => 11/17/2021 FILE => 16_MV_POC_B5L.dwg		TIME PLOTTED => 2:34 PM USERNAME => JVALENZUELA		ORIGINAL SCALE IN INCHES FOR REDUCED PLANS		UNIT: X PROJECT NUMBER & PHASE: 0518000116	
CONTRACT No.: 05-OC7331		REVISION DATES		SHEET		OF		DISREGARD PRINTS BEARING EARLIER REVISION DATES		6-18-21	
				76		38					

Dist	COUNTY	ROUTE	POST MILES TOTAL PROJECT	SHEET NO.	TOTAL SHEETS
05	Scr	1	10.54/13.44	432	453

DRAFT 65% PLANS




REGISTERED STRUCTURAL ENGINEER DATE

PLANS APPROVAL DATE

THE STATE OF CALIFORNIA OR ITS OFFICERS OR AGENTS
SHALL NOT BE RESPONSIBLE FOR THE ACCURACY OR
COMPLETENESS OF SCANNED COPIES OF THIS PLAN SHEET.


MARK THOMAS
701 UNIVERSITY AVE., SUITE 200
SACRAMENTO, CA 95825

SCCRTC
1523 PACIFIC AVENUE
SANTA CRUZ, CA 95090

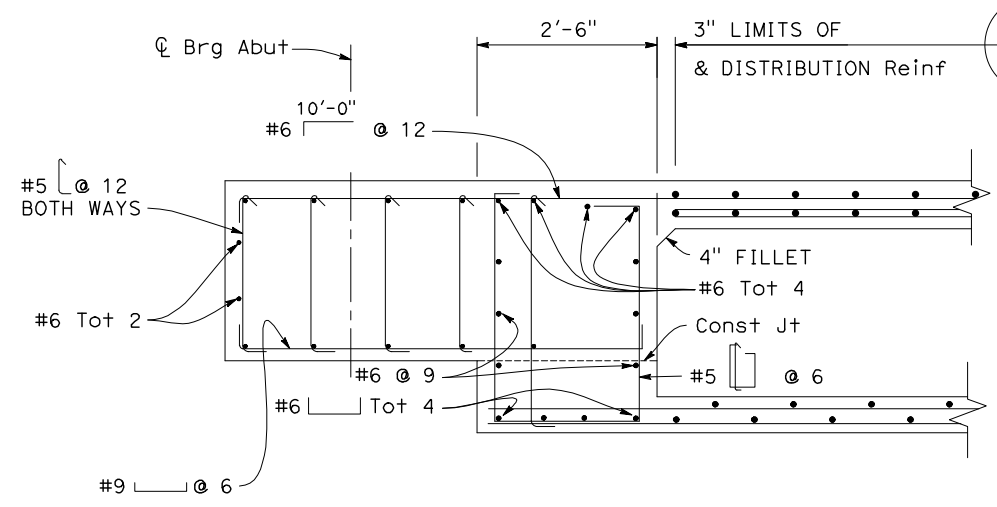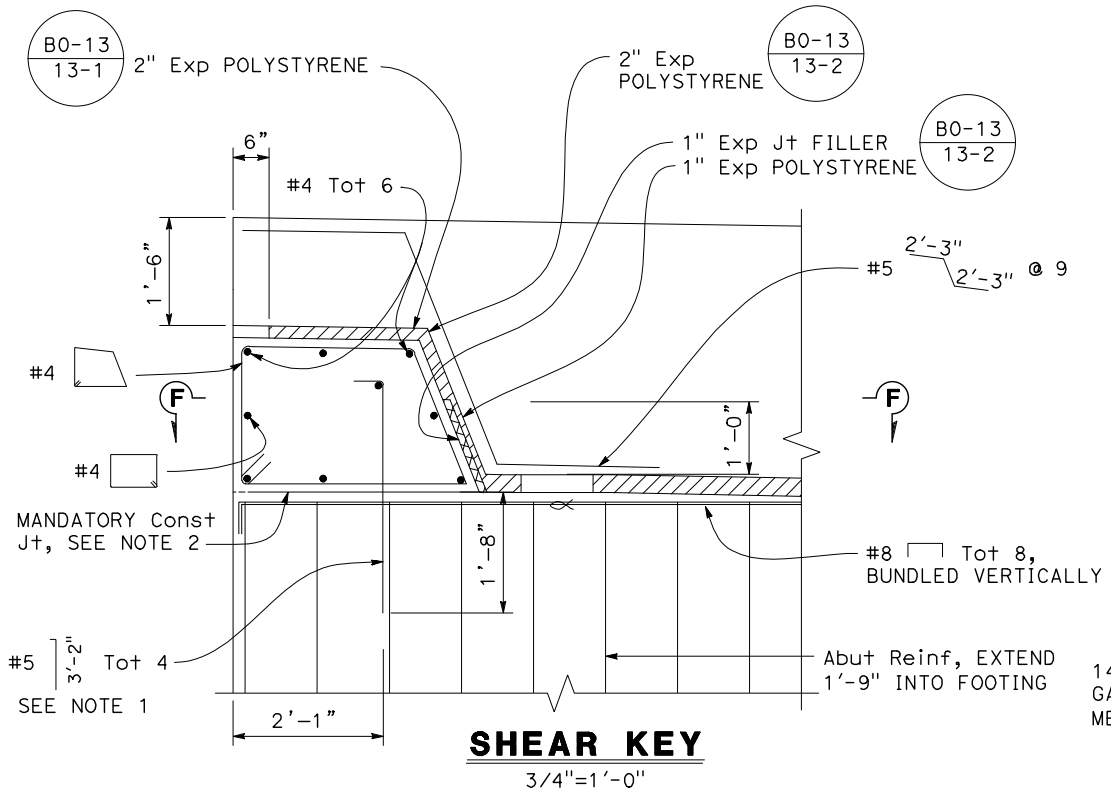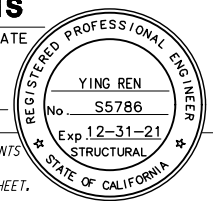


END DIAPHRAGM

3/4" = 1'-0"

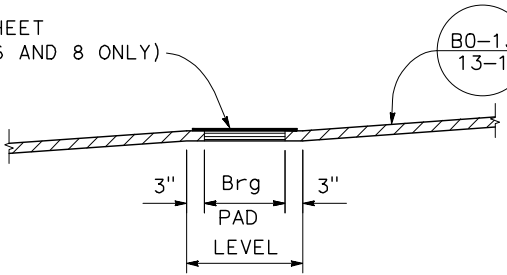


ELEVATION

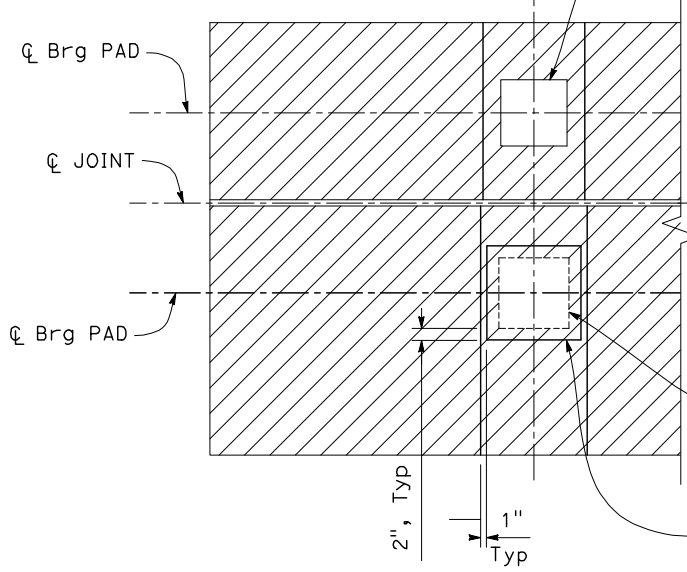

PLAN

BEARING PAD DETAIL

3/4"=1'-0"

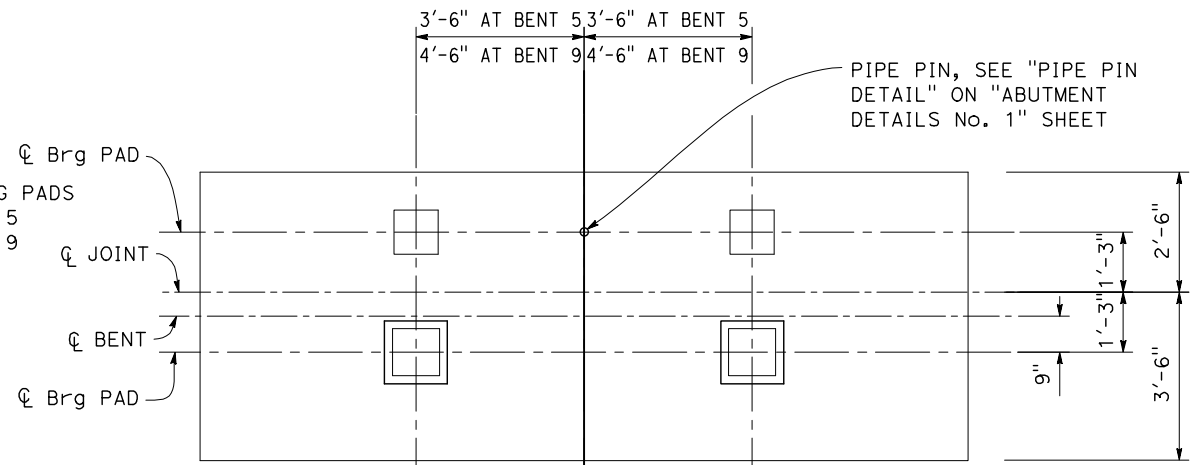

SECTION E-E

1/2"=1'-0"

NOTE: Bent 9 shown, Bent 5 similar.

NOTES:

1. Main vertical shear key reinforcement must be galvanized.
2. Mandatory construction joint shall be smooth finished and lined with 15 pound building paper. Leave 3" at outer edge without smoothing and building paper.

X
DESIGN OVERSIGHT
X
SIGN OFF DATE

DESIGN BY Y. REN
DETAILS BY J. DOTY
QUANTITIES BY X

CHECKED X
CHECKED X
CHECKED X

PREPARED FOR THE
STATE OF CALIFORNIA
DEPARTMENT OF TRANSPORTATION

ERIC FREDRICKSON
PROJECT ENGINEER

BRIDGE No.
36-0128
POST MILE
10.87

MAR VISTA DRIVE POC
BENT 5 AND 9 DETAILS

DESIGN DETAIL SHEET
(ENGLISH) (REVISION 4/19/2018)

DATE PLOTTED => 11/17/2021
TIME PLOTTED => 3:45 PM
ORIGINAL SCALE IN INCHES FOR
FILE => 17_MV_POC_B50.dwg
USERNAME => JVALENZUELA
REDUCED PLANS

UNIT: X
PROJECT NUMBER & PHASE: 0518000116


CONTRACT No.: 05-0C7331

DISREGARD PRINTS BEARING
EARLIER REVISION DATES
REVISION DATES
SHEET 47 OF 38

Dist	COUNTY	ROUTE	POST MILES TOTAL PROJECT	SHEET NO.	TOTAL SHEETS
05	Scr	1	10.54/13.44	433	453

DRAFT 65% PLANS

REGISTERED STRUCTURAL ENGINEER DATE

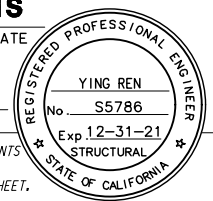


PLANS APPROVAL DATE

THE STATE OF CALIFORNIA OR ITS OFFICERS OR AGENTS
SHALL NOT BE RESPONSIBLE FOR THE ACCURACY OR
COMPLETENESS OF SCANNED COPIES OF THIS PLAN SHEET.


MARK THOMAS
701 UNIVERSITY AVE., SUITE 200
SACRAMENTO, CA 95825

SCCRTC
1523 PACIFIC AVENUE
SANTA CRUZ, CA 95090

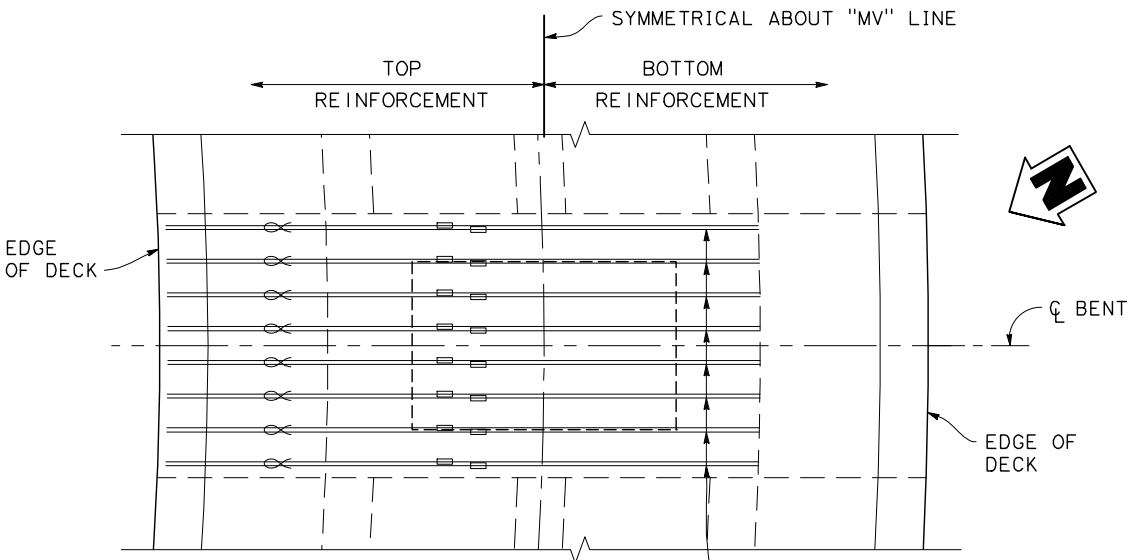

PLAN


1/2" = 1'-0"

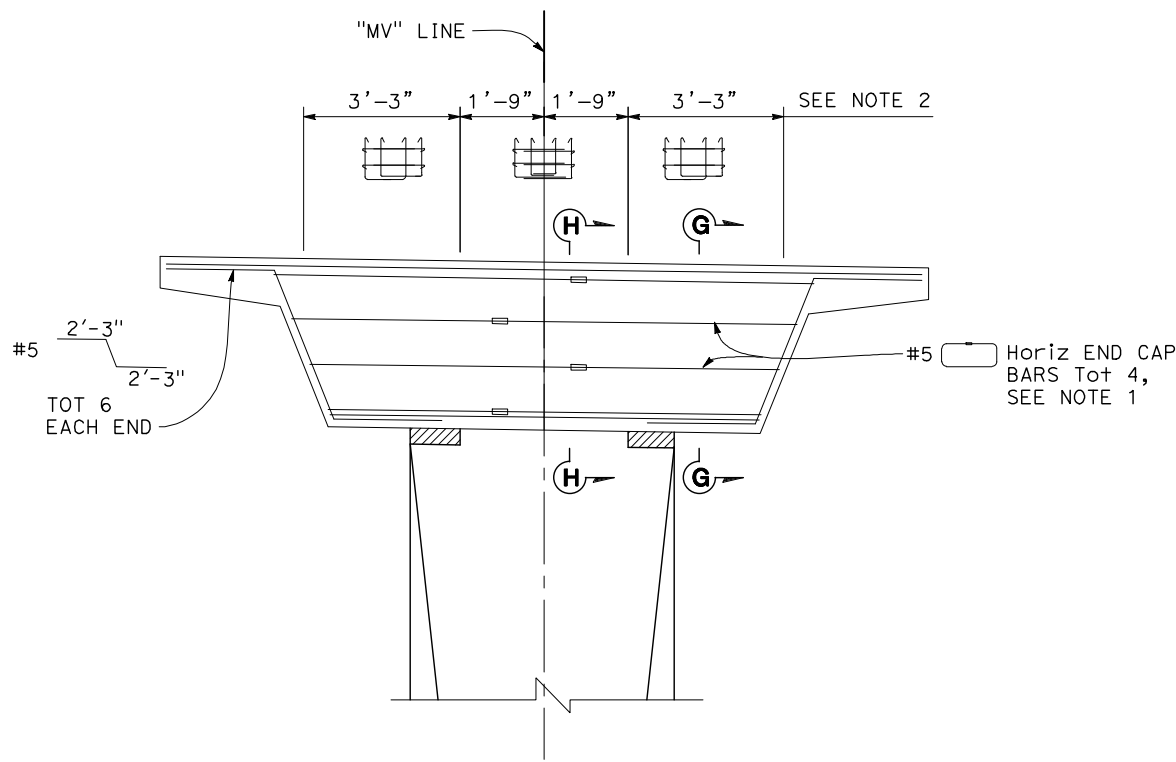

ELEVATION


1/2" = 1'-0"

NOTE: Column reinforcement not shown for clarity.

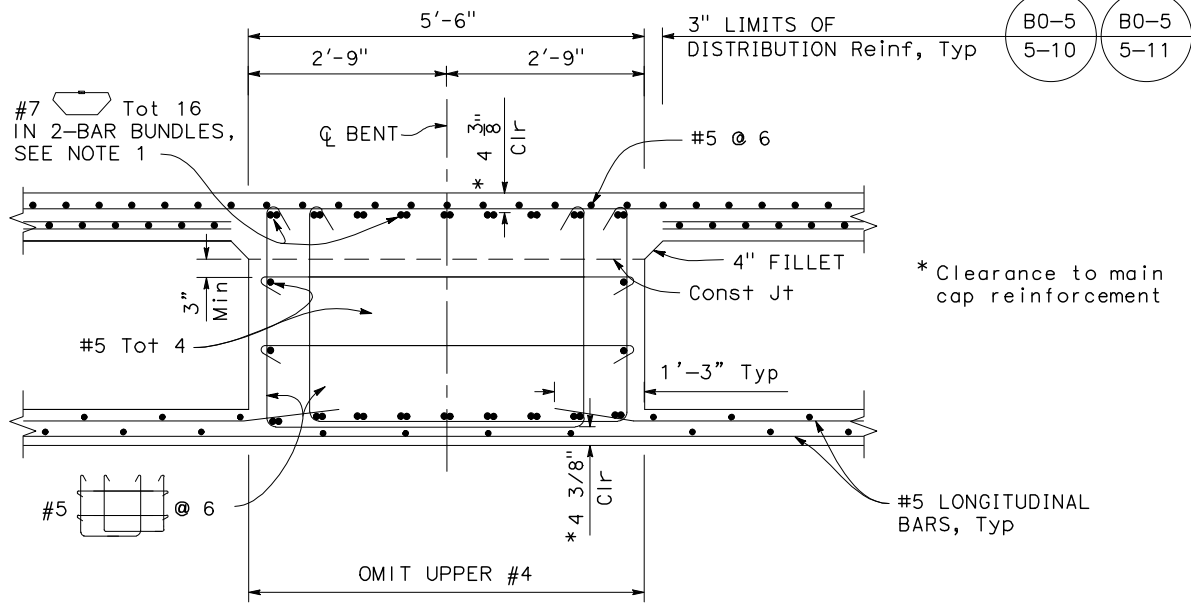

SECTION G-G

3/4" = 1'-0"

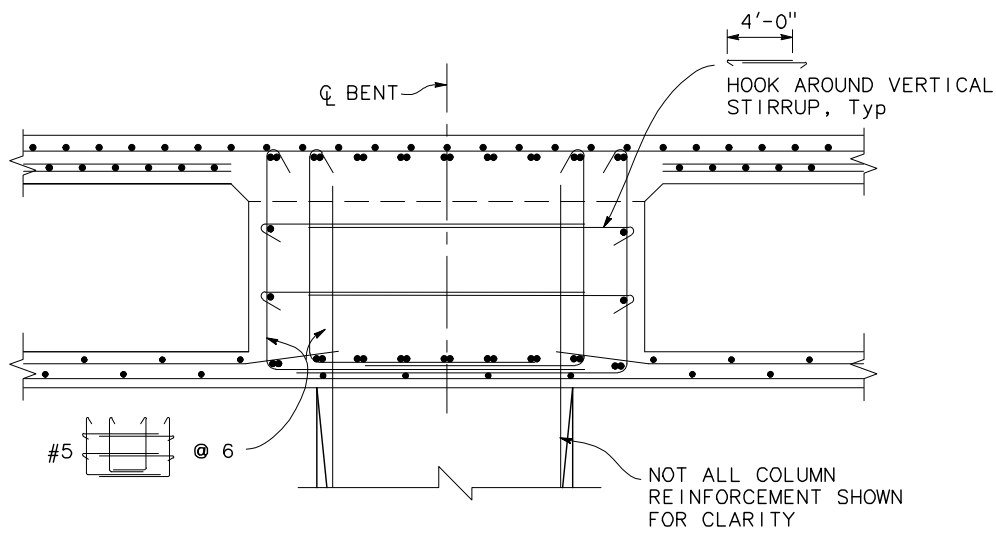

SECTION H-H

3/4" = 1'-0"

NOTE: For details not shown, see "SECTION G-G"

NOTES:

1. Ultimate butt splice only.
2. Place stirrups normal to ϕ Bent and place along ϕ Bent.

X DESIGN OVERSIGHT X SIGN OFF DATE	DESIGN BY Y. REN DETAILS BY J. DOTY QUANTITIES BY X	CHECKED X X X	PREPARED FOR THE STATE OF CALIFORNIA DEPARTMENT OF TRANSPORTATION	ERIC FREDRICKSON PROJECT ENGINEER	BRIDGE No.	MAR VISTA DRIVE POC BENT 6 THRU 8 LAYOUT											
					36-0128 POST MILE 10.87												
					UNIT: X PROJECT NUMBER & PHASE: 0518000116 CONTRACT No.: 05-0C7331					DISREGARD PRINTS BEARING EARLIER REVISION DATES	REVISION DATES		SHEET	OF			
					DESIGN DETAIL SHEET (ENGLISH) (REVISION 4/19/2018)					DATE PLOTTED => 11/17/2021 FILE => 18_MV_POC_B6L.dwg	TIME PLOTTED => 4:20 PM USERNAME => JVALENZUELA	ORIGINAL SCALE IN INCHES FOR REDUCED PLANS	0	1	2	3	6-18-21

Dist	COUNTY	ROUTE	POST MILES TOTAL PROJECT	SHEET NO.	TOTAL SHEETS
05	Scr	1	10.54/13.44	434	453

DRAFT 65% PLANS



REGISTERED STRUCTURAL ENGINEER DATE

PLANS APPROVAL DATE

THE STATE OF CALIFORNIA OR ITS OFFICERS OR AGENTS
SHALL NOT BE RESPONSIBLE FOR THE ACCURACY OR
COMPLETENESS OF SCANNED COPIES OF THIS PLAN SHEET.


MARK THOMAS
701 UNIVERSITY AVE., SUITE 200
SACRAMENTO, CA 95825

SCCRTC
1523 PACIFIC AVENUE
SANTA CRUZ, CA 95090

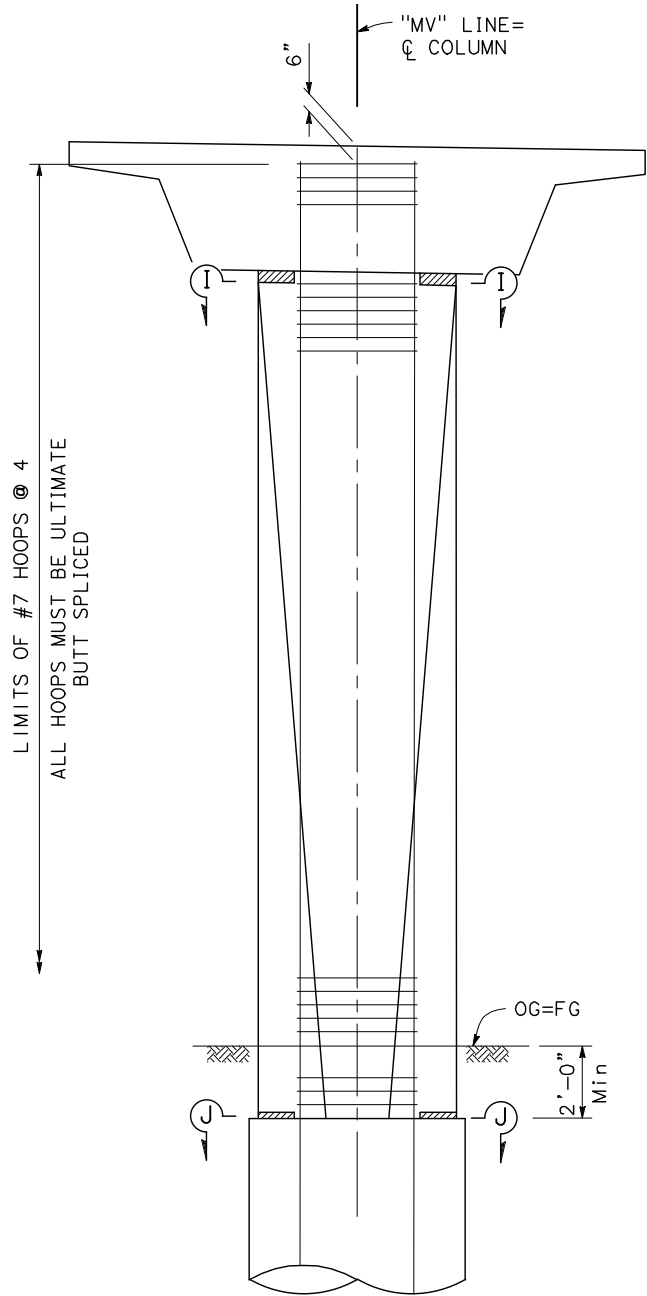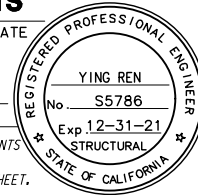

COLUMN DETAIL-BENT 7 AND 8


3/8" = 1'-0"

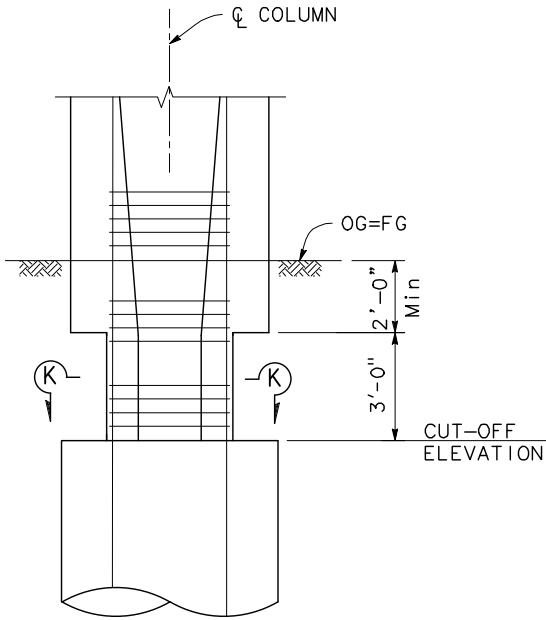

COLUMN DETAIL-BENT 6


3/8" = 1'-0"

- NOTES:
- For information not shown, see "COLUMN DETAILS-BENT 7 AND 8".
 - For Isolation Casing, see "ISOLATION CASING DETAILS" sheet.

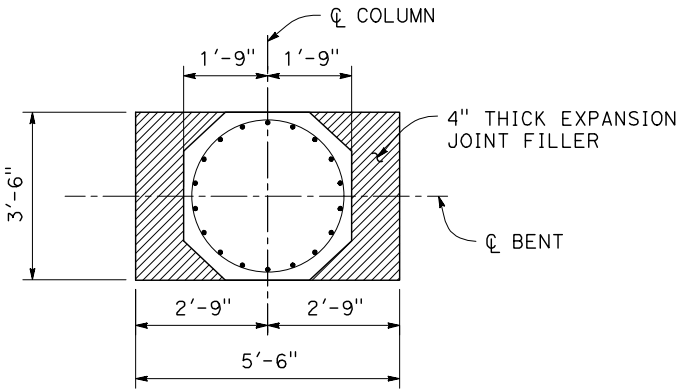


SECTION I-I

1/2" = 1'-0"

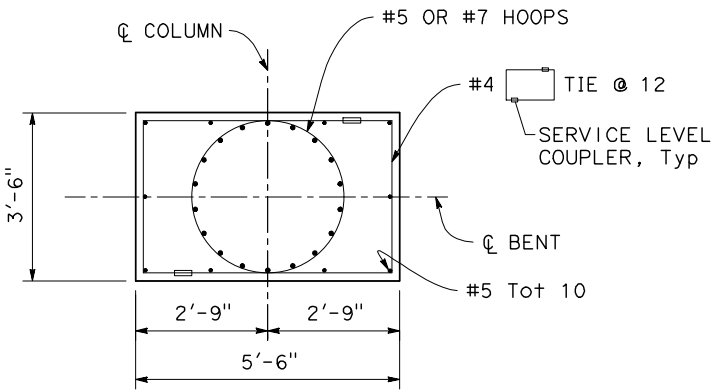


COLUMN TOP

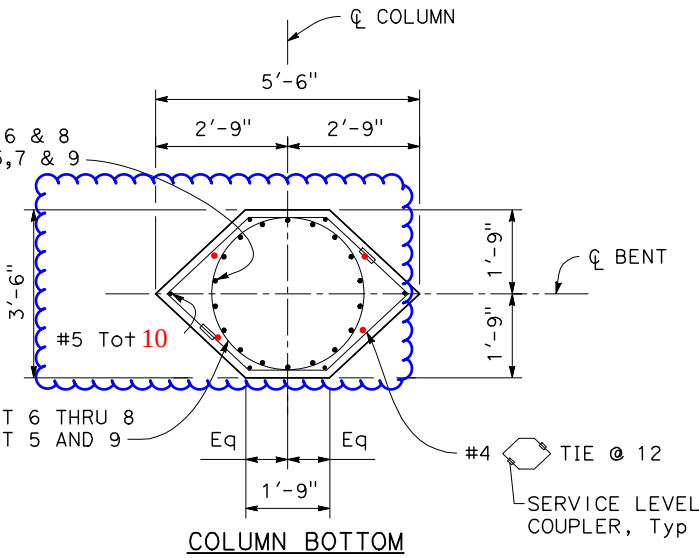


HEXAGONAL COLUMN

1/2" = 1'-0"

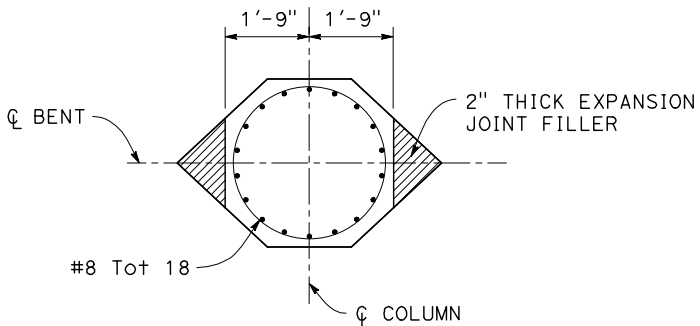

SECTION J-J

1/2" = 1'-0"

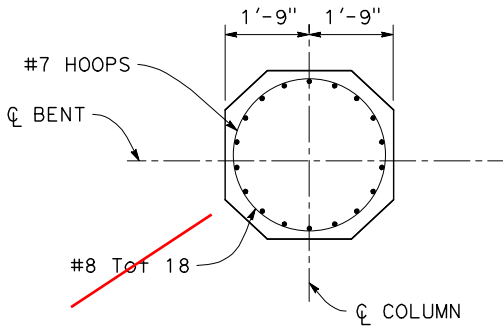

SECTION K-K

1/2" = 1'-0"

X
DESIGN OVERSIGHT
X
SIGN OFF DATE

DESIGN	BY Y. REN	CHECKED X
DETAILS	BY J. DOTY	CHECKED X
QUANTITIES	BY X	CHECKED X

**PREPARED FOR THE
STATE OF CALIFORNIA
DEPARTMENT OF TRANSPORTATION**

ERIC FREDRICKSON
PROJECT ENGINEER

BRIDGE No.
36-0128
POST MILE
10.87

**MAR VISTA DRIVE POC
BENT 6 THRU 8 DETAILS**

DESIGN DETAIL SHEET
(ENGLISH) (REVISION 4/19/2018)

DATE PLOTTED => 11/17/2021
FILE => 19_MV_POC_B6D.dwg

TIME PLOTTED => 4:36 PM
USERNAME => JVALENZUELA
ORIGINAL SCALE
IN INCHES FOR
REDUCED PLANS

0 1 2 3

UNIT: X
PROJECT NUMBER & PHASE: 0518000116


CONTRACT No.: 05-OC7331

DISREGARD PRINTS BEARING
EARLIER REVISION DATES

REVISION DATES

SHEET	OF
39	38

DRAFT 65% PLANS	
REGISTERED STRUCTURAL ENGINEER	DATE _____
_____ PLANS APPROVAL DATE	
<i>THE STATE OF CALIFORNIA OR ITS OFFICERS OR AGENTS SHALL NOT BE RESPONSIBLE FOR THE ACCURACY OR COMPLETENESS OF SCANNED COPIES OF THIS PLAN SHEET.</i>	
MARK THOMAS 701 UNIVERSITY AVE., SUITE 200 SACRAMENTO, CA 95825	
SCCRTC 1523 PACIFIC AVENUE SANTA CRUZ, CA 95090	

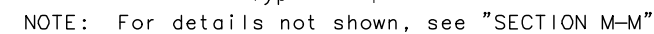


1. All column and CIDH pile hoops must utilize ultimate butt splices.
2. For specified tip elevation and cut-off elevation, see "FOUNDATION PLAN No. 2" sheet.
3. See "BENT 6 THRU 8 DETAILS" sheet for column reinforcement details.
4. Permanent steel casing used at Bents 5 thru 9.

Dist	COUNTY	ROUTE	POST MILES TOTAL PROJECT	SHEET NO.	TOTAL SHEETS
05	Scr	1	10.54/13.44	435	453

DRAFT 65% PLANS

REGISTERED STRUCTURAL ENGINEER DATE



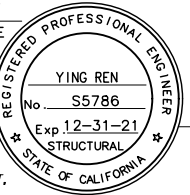


PLANS APPROVAL DATE

THE STATE OF CALIFORNIA OR ITS OFFICERS OR AGENTS
SHALL NOT BE RESPONSIBLE FOR THE ACCURACY OR
COMPLETENESS OF SCANNED COPIES OF THIS PLAN SHEET.

MARK THOMAS
701 UNIVERSITY AVE., SUITE 200
SACRAMENTO, CA 95825

SCCRTC
1523 PACIFIC AVENUE
SANTA CRUZ, CA 95090

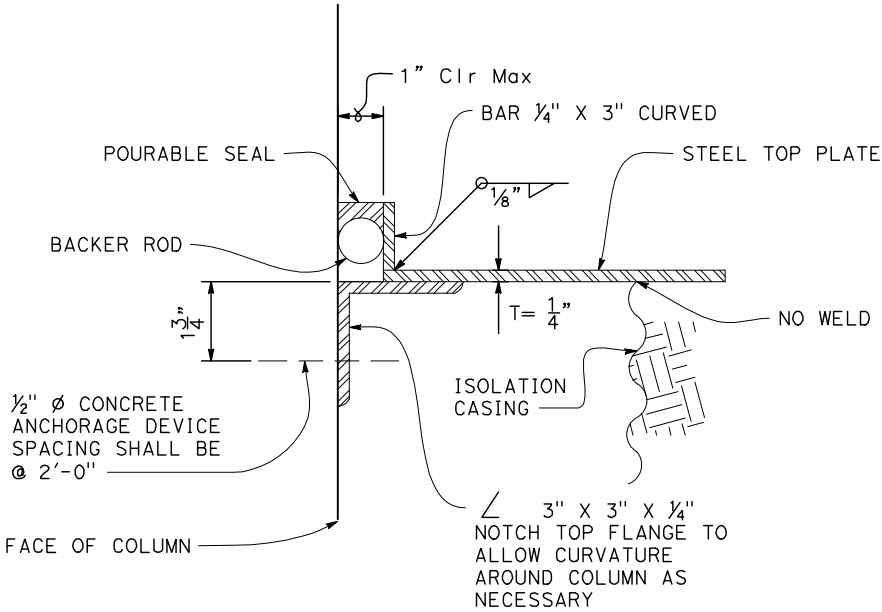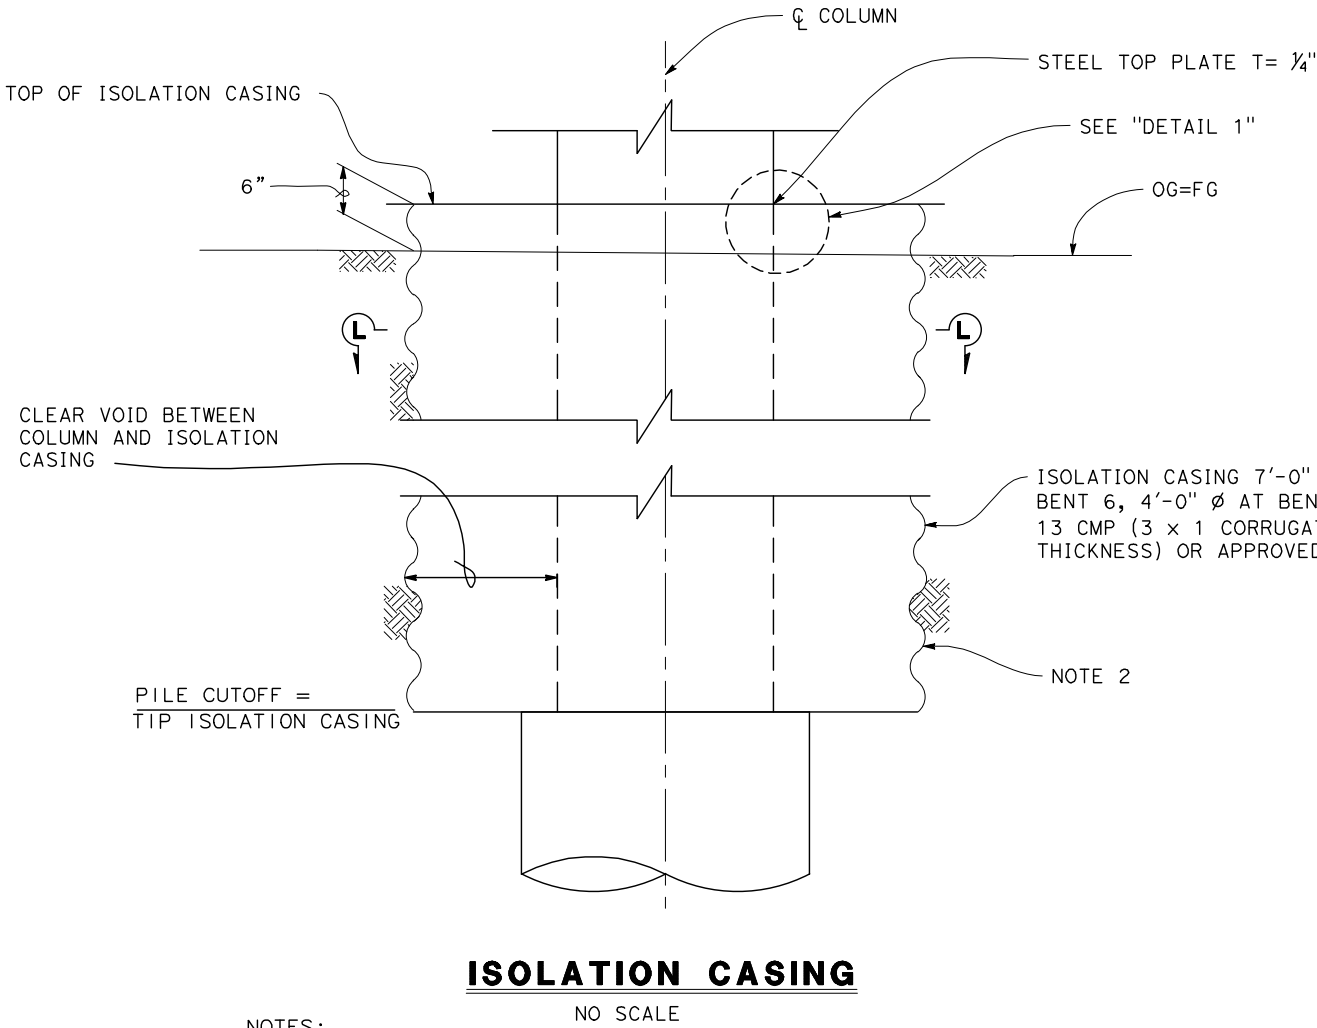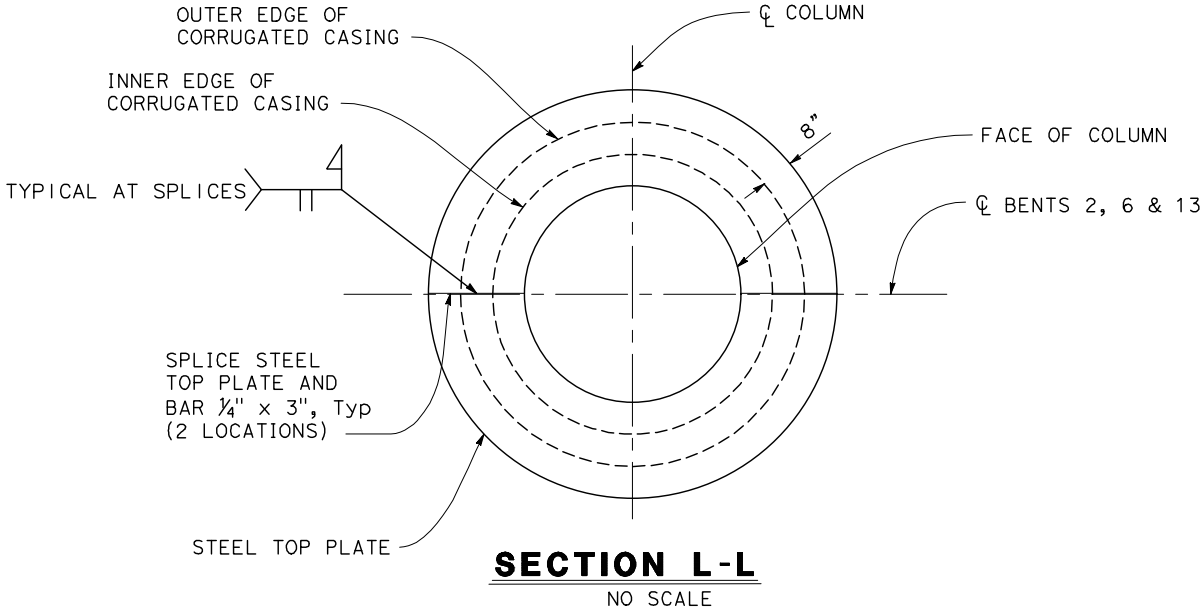


- NOTES:
1. Isolation casing to be installed at Bents 2, 6, and 13.
 2. After placement of isolation casing, place cement slurry to fill any void region outside the casing.

X DESIGN OVERSIGHT X SIGN OFF DATE		DESIGN	BY Y. REN	CHECKED X	PREPARED FOR THE STATE OF CALIFORNIA DEPARTMENT OF TRANSPORTATION	BRIDGE No.	MAR VISTA DRIVE POC ISOLATION CASING DETAILS					
		DETAILS	BY J. DOTY	CHECKED X		36-0128						
				CHECKED X								
		QUANTITIES	BY X	CHECKED X		POST MILE 10.87						
DESIGN DETAIL SHEET (ENGLISH) (REVISION 4/19/2018)		DATE PLOTTED ==> 11/17/2021 FILE ==> 21_MV_POC_ICD.dwg		TIME PLOTTED ==> 5:26 PM USERNAME ==> JVALENZUELA	ORIGINAL SCALE IN INCHES FOR REDUCED PLANS	UNIT: X PROJECT NUMBER & PHASE: 0518000116	CONTRACT No.: 05-OC7331	DISREGARD PRINTS BEARING EARLIER REVISION DATES ==>	REVISION DATES		SHEET	OF
						6-18-21					21	38

Dist	COUNTY	ROUTE	POST MILES TOTAL PROJECT	SHEET NO.	TOTAL SHEETS
05	Scr	1	10.54/13.44	437	453

DRAFT 65% PLANS

REGISTERED STRUCTURAL ENGINEER DATE

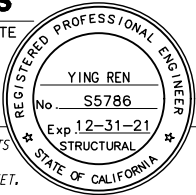


PLANS APPROVAL DATE

THE STATE OF CALIFORNIA OR ITS OFFICERS OR AGENTS
SHALL NOT BE RESPONSIBLE FOR THE ACCURACY OR
COMPLETENESS OF SCANNED COPIES OF THIS PLAN SHEET.


MARK THOMAS
701 UNIVERSITY AVE., SUITE 200
SACRAMENTO, CA 95825

SCCRTC
1523 PACIFIC AVENUE
SANTA CRUZ, CA 95090

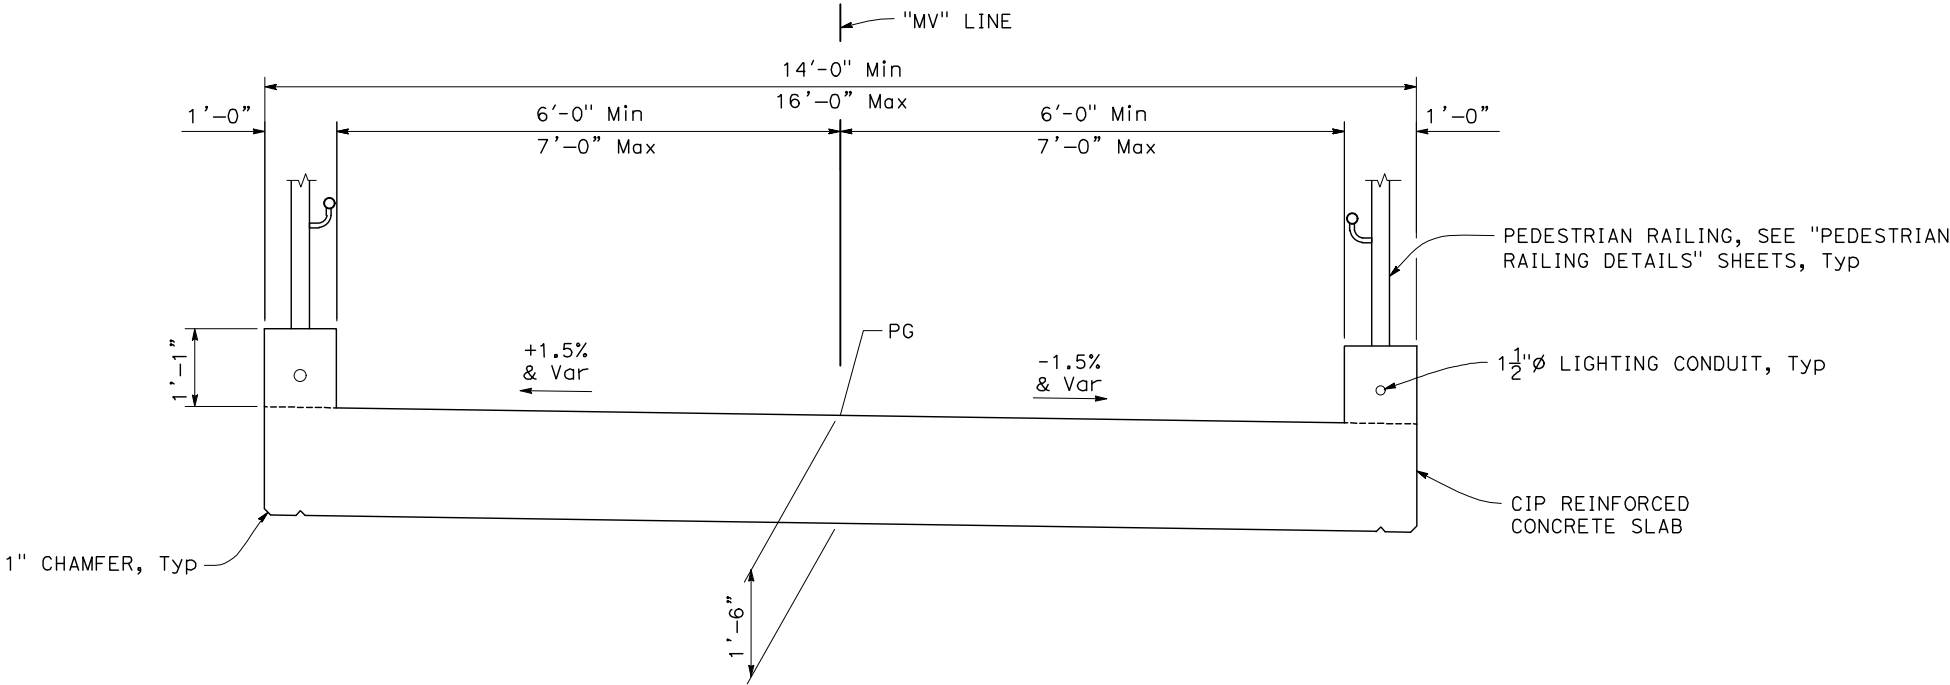

SLAB TYPICAL SECTION-SPAN 1 THRU 4, 9 THRU 16

3/4"=1'-0"

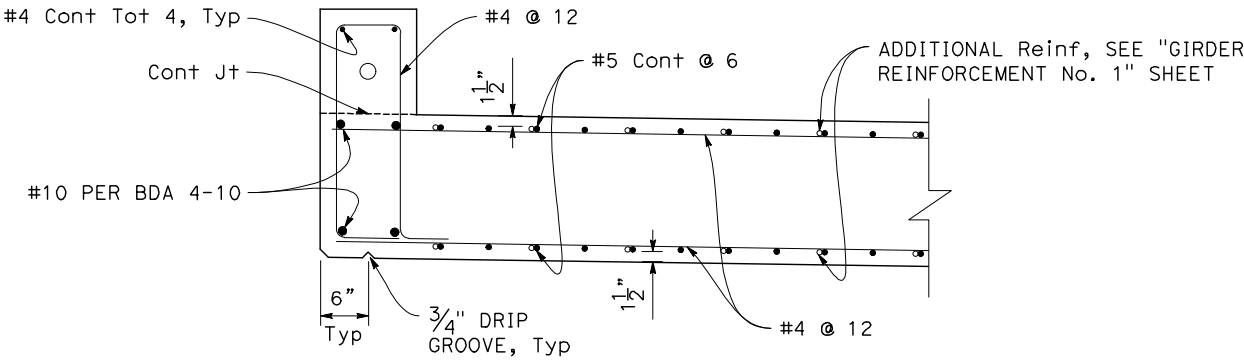

PART SLAB TYPICAL SECTION

1"=1'-0"

X
DESIGN OVERSIGHT
X
SIGN OFF DATE

DESIGN BY Y. REN
DETAILS BY J. DOTY
QUANTITIES BY X

CHECKED X
CHECKED X
CHECKED X

PREPARED FOR THE
STATE OF CALIFORNIA
DEPARTMENT OF TRANSPORTATION

ERIC FREDRICKSON
PROJECT ENGINEER

BRIDGE No.
36-0128
POST MILE
10.87

MAR VISTA DRIVE POC
TYPICAL SECTION No. 1

DESIGN DETAIL SHEET
(ENGLISH) (REVISION 4/19/2018)

DATE PLOTTED => 11/17/2021
FILE => 22_MV_POC_TS1.dwg
TIME PLOTTED => 8:00 PM
USERNAME => JVALENZUELA
ORIGINAL SCALE
IN INCHES FOR
REDUCED PLANS

0 1 2 3

UNIT: X
PROJECT NUMBER & PHASE: 0518000116

CONTRACT No.: 05-OC7331


DISREGARD PRINTS BEARING
EARLIER REVISION DATES

REVISION DATES
6-18-21
SHEET
22
OF
38

DRAFT 65% PLANS	
REGISTERED STRUCTURAL ENGINEER	DATE _____
PLANS APPROVAL DATE _____	
<i>THE STATE OF CALIFORNIA OR ITS OFFICERS OR AGENTS SHALL NOT BE RESPONSIBLE FOR THE ACCURACY OR COMPLETENESS OF SCANNED COPIES OF THIS PLAN SHEET.</i>	
MARK THOMAS 701 UNIVERSITY AVE., SUITE 200 SACRAMENTO, CA 95825	
SCCRTG 1523 PACIFIC AVENUE SANTA CRUZ, CA 95090	



X DESIGN OVERSIGHT X SIGN OFF DATE		DESIGNBY Y. RENCHECKED X DETAILSBY J. DOTYCHECKED X QUANTITIESBY XCHECKED X		PREPARED FOR THE STATE OF CALIFORNIA DEPARTMENT OF TRANSPORTATION		ERIC FREDRICKSON PROJECT ENGINEER		BRIDGE No. 36-0128 POST MILE 10.87		MAR VISTA DRIVE POC TYPICAL SECTION No. 2							
DESIGN DETAIL SHEET (ENGLISH) (REVISION 4/19/2018)		DATE PLOTTED => 11/17/2021 FILE => 23_MV_POC_TS2.dwg USERNAME => JVALENZUELA		TIME PLOTTED => 8:07 PM ORIGINAL SCALE 1 IN INCHES FOR REDUCED PLANS		0123		UNIT: X PROJECT NUMBER & PHASE: 0518000116 CONTRACT No.: 05-OC7331		DISREGARD PRINTS BEARING EARLIER REVISION DATES		REVISION DATES 6-18-21		SHEET 23		OF 38	

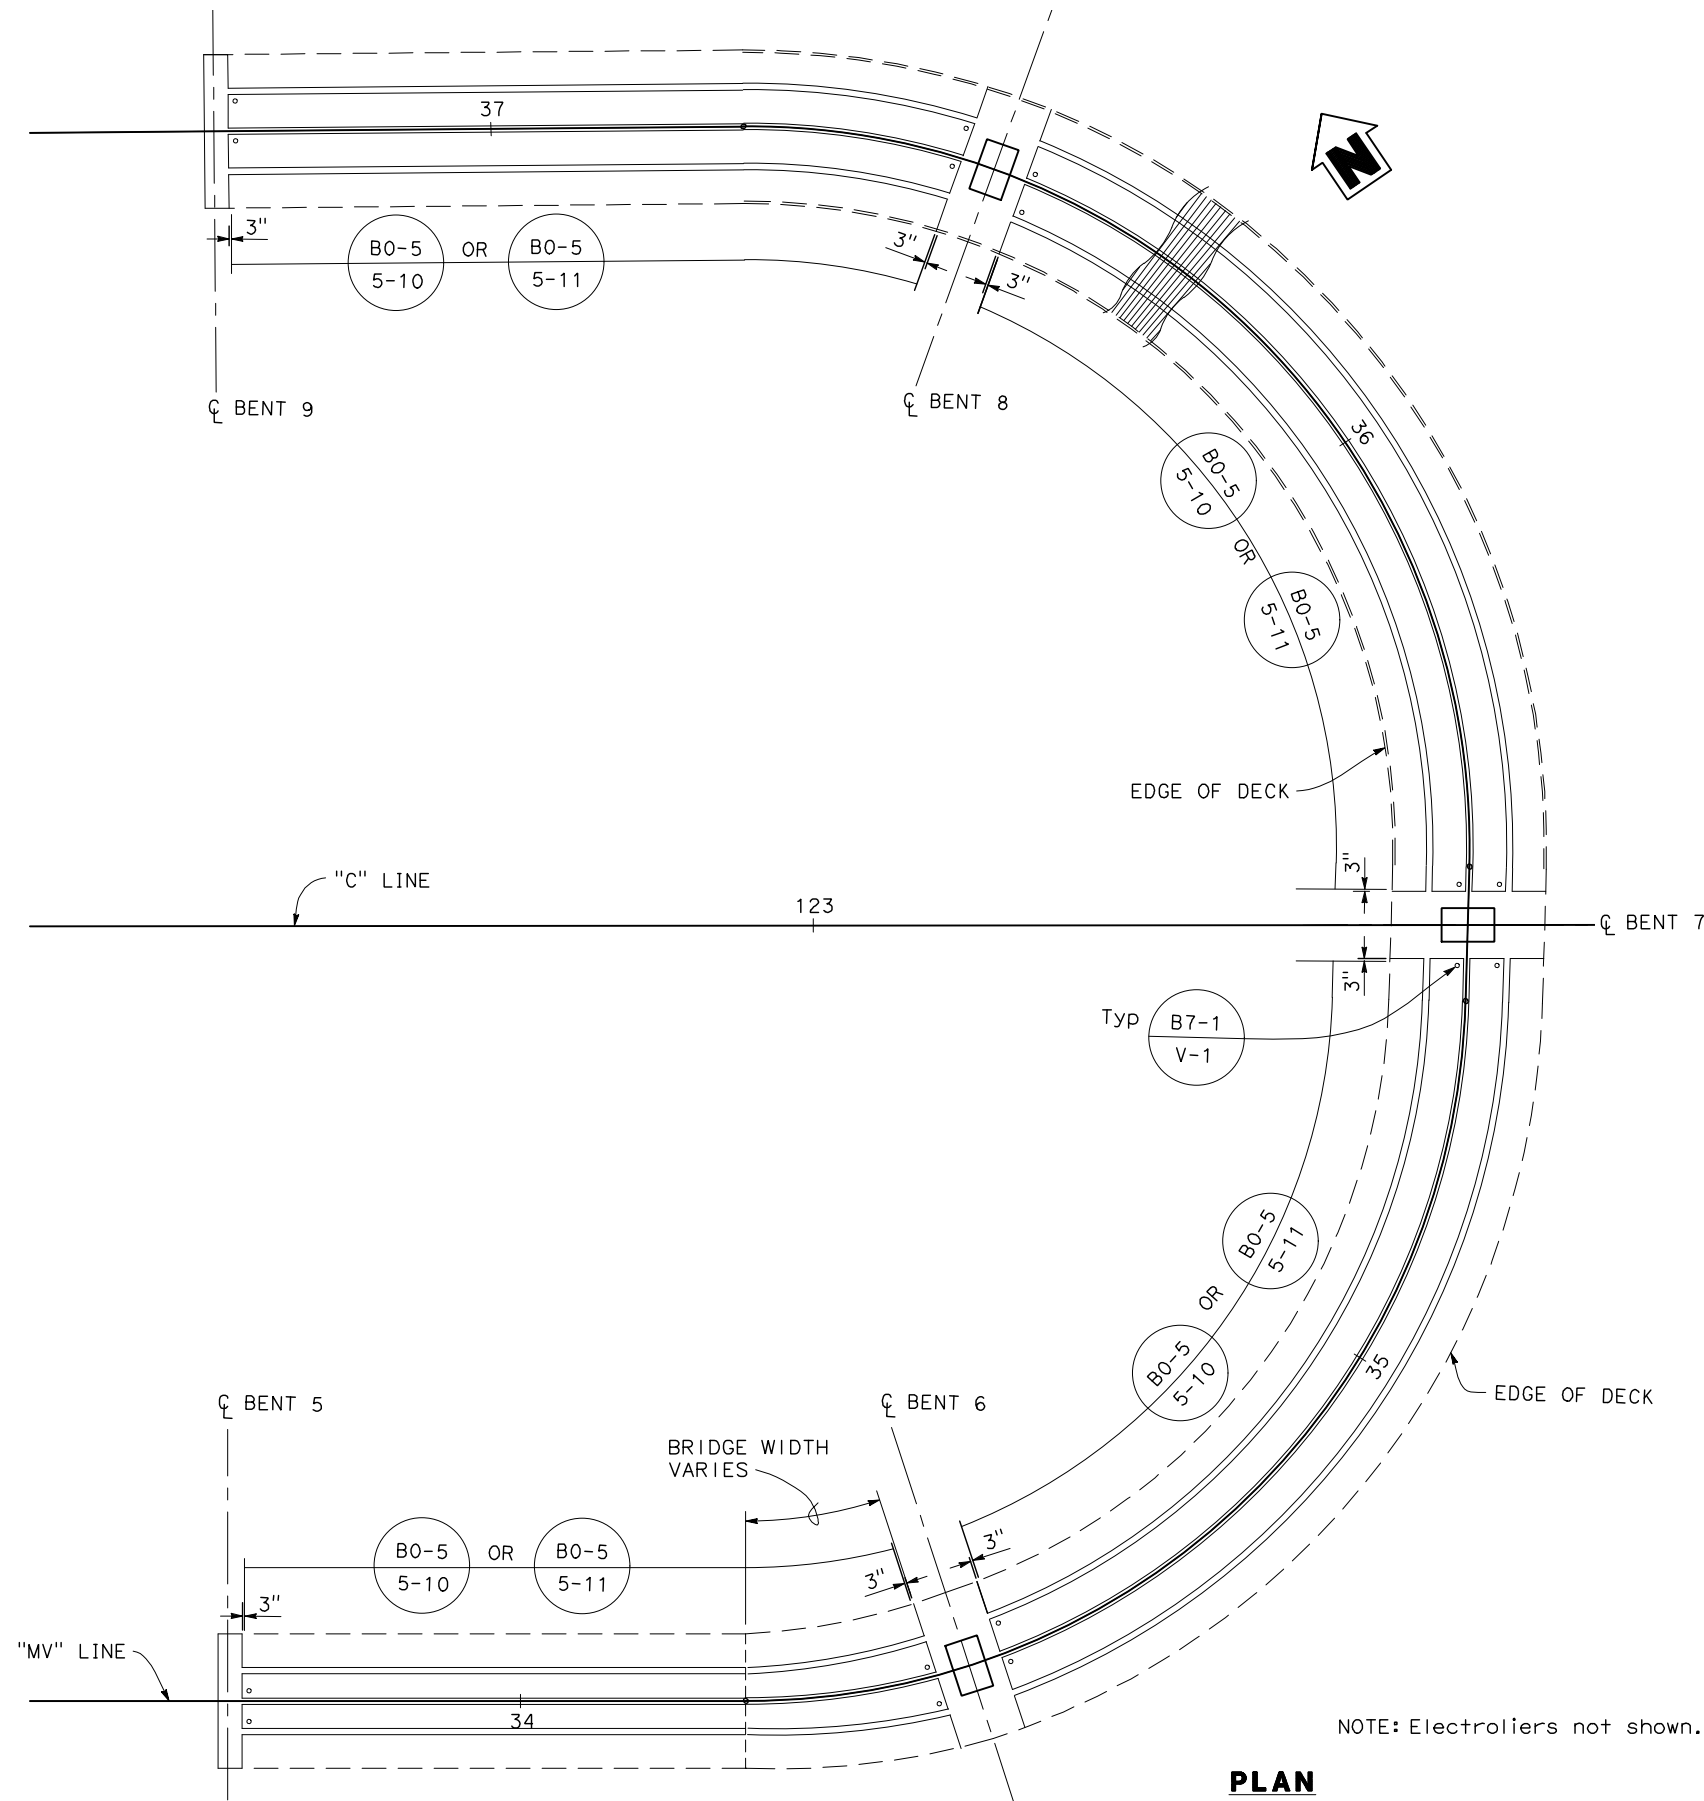

PLAN
1" = 10'

NOTE: Electroliers not shown.

Dist	COUNTY	ROUTE	POST MILES TOTAL PROJECT	SHEET NO.	TOTAL SHEETS
05	Scr	1	10.54/13.44	439	453

DRAFT 65% PLANS

REGISTERED STRUCTURAL ENGINEER DATE

PLANS APPROVAL DATE

REGISTERED PROFESSIONAL ENGINEER

YING REN

No. S5786

Exp. 12-31-21

STRUCTURAL

STATE OF CALIFORNIA

THE STATE OF CALIFORNIA OR ITS OFFICERS OR AGENTS
SHALL NOT BE RESPONSIBLE FOR THE ACCURACY OR
COMPLETENESS OF SCANNED COPIES OF THIS PLAN SHEET.

MARK THOMAS
701 UNIVERSITY AVE., SUITE 200
SACRAMENTO, CA 95825

SCCRTC
1523 PACIFIC AVENUE
SANTA CRUZ, CA 95090

X DESIGN OVERSIGHT X SIGN OFF DATE	DESIGN BY Y. REN DETAILS BY J. DOTY QUANTITIES BY X	CHECKED X CHECKED X CHECKED X	PREPARED FOR THE STATE OF CALIFORNIA DEPARTMENT OF TRANSPORTATION	ERIC FREDRICKSON PROJECT ENGINEER	BRIDGE No.	MAR VISTA DRIVE POC GIRDER LAYOUT No. 1				
					36-0128					
					POST MILE					
					10.87					
DESIGN DETAIL SHEET (ENGLISH) (REVISION 4/19/2018)	DATE PLOTTED => 11/17/2021 FILE => 24-25_MV_POC_GL.dwg	TIME PLOTTED => 8:29 PM USERNAME => JVALENZUELA	ORIGINAL SCALE IN INCHES FOR REDUCED PLANS	0 1 2 3	UNIT: X PROJECT NUMBER & PHASE: 0518000116	CONTRACT No.: 05-OC7331	DISREGARD PRINTS BEARING EARLIER REVISION DATES	REVISION DATES	SHEET	OF
							6-18-21	24	38	

41

Dist	COUNTY	ROUTE	POST MILES TOTAL PROJECT	SHEET No.	TOTAL SHEETS
05	SCr	1	10.54/13.44	440	453

DRAFT 65% PLANS



REGISTERED STRUCTURAL ENGINEER DATE 11/1/2018

PLANS APPROVAL DATE


THE STATE OF CALIFORNIA OR ITS OFFICERS OR AGENTS
SHALL NOT BE RESPONSIBLE FOR THE ACCURACY OR
COMPLETENESS OF SCANNED COPIES OF THIS PLAN SHEET.

MARK THOMAS
701 UNIVERSITY AVE., SUITE 200
SACRAMENTO, CA 95825

SCCRTC
1523 PACIFIC AVENUE
SANTA CRUZ, CA 95090

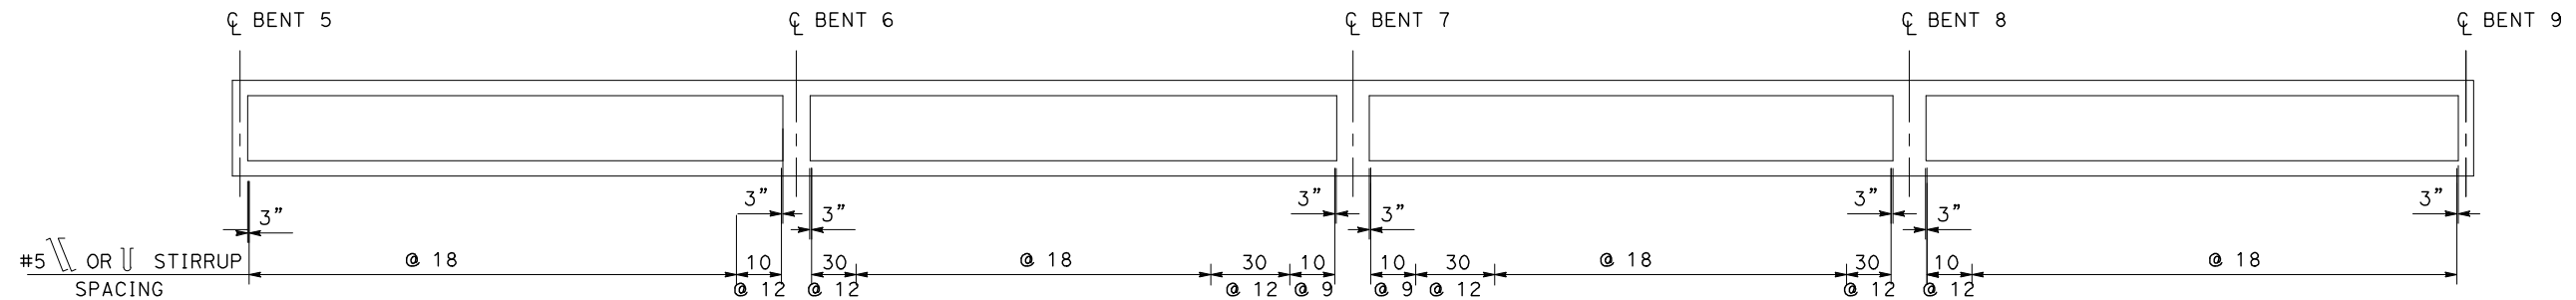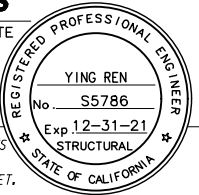

LONGITUDINAL SECTION
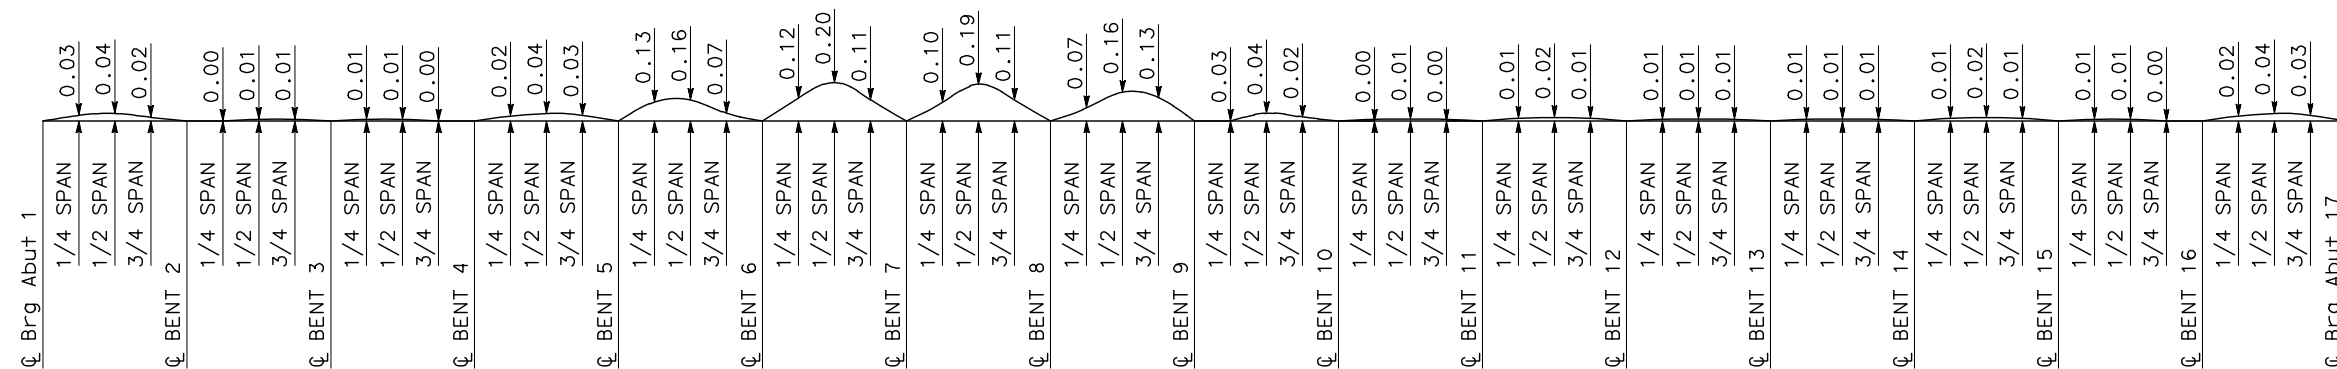
$$1'' = 10'$$


NOTE: Does not include allowance for falsework settlement.

CAMBER DIAGRAM

NO SCALE

X DESIGN OVERSIGHT X SIGN OFF DATE	DESIGN	BY Y. REN	CHECKED X	PREPARED FOR THE STATE OF CALIFORNIA DEPARTMENT OF TRANSPORTATION	ERIC FREDRICKSON PROJECT ENGINEER	BRIDGE No.	MAR VISTA DRIVE POC GIRDER LAYOUT No. 2												
	DETAILS	BY J. DOTY	CHECKED X			36-0128													
	QUANTITIES	BY X	CHECKED X			POST MILE													
						10.87													
DATE PLOTTED => 11/17/2021 FILE => 24-25_MV_POC_GLD.dwg				TIME PLOTTED => 8:36 PM USERNAME => JVALENZUELA		ORIGINAL SCALE IN INCHES FOR REDUCED PLANS		0	1	2	3	UNIT: X	PROJECT NUMBER & PHASE: 0518000116	CONTRACT No.: 05-OC7331	DISREGARD PRINTS BEARING EARLIER REVISION DATES	6-18-21	REVISION DATES	SHEET	OF
DESIGN DETAIL SHEET (ENGLISH) (REVISION 4/19/2018)																25	38		

Dist	COUNTY	ROUTE	POST MILES TOTAL PROJECT	SHEET NO.	TOTAL SHEETS
05	Scr	1	10.54/13.44	441	453

DRAFT 65% PLANS


REGISTERED STRUCTURAL ENGINEER DATE

PLANS APPROVAL DATE

THE STATE OF CALIFORNIA OR ITS OFFICERS OR AGENTS
SHALL NOT BE RESPONSIBLE FOR THE ACCURACY OR
COMPLETENESS OF SCANNED COPIES OF THIS PLAN SHEET.

MARK THOMAS
701 UNIVERSITY AVE., SUITE 200
SACRAMENTO, CA 95825


SCCRTC
1523 PACIFIC AVENUE
SANTA CRUZ, CA 95090

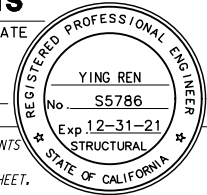

- NOTES:
- Lap splices allowed within 7'-0" either side of $\varnothing$ Bent 2 thru 4, Bent 10 thru 16.
 - No splices allowed within 15'-0" either side of $\varnothing$ Bent 6 thru 8.


LEGEND

∞ Indicates bundled bar

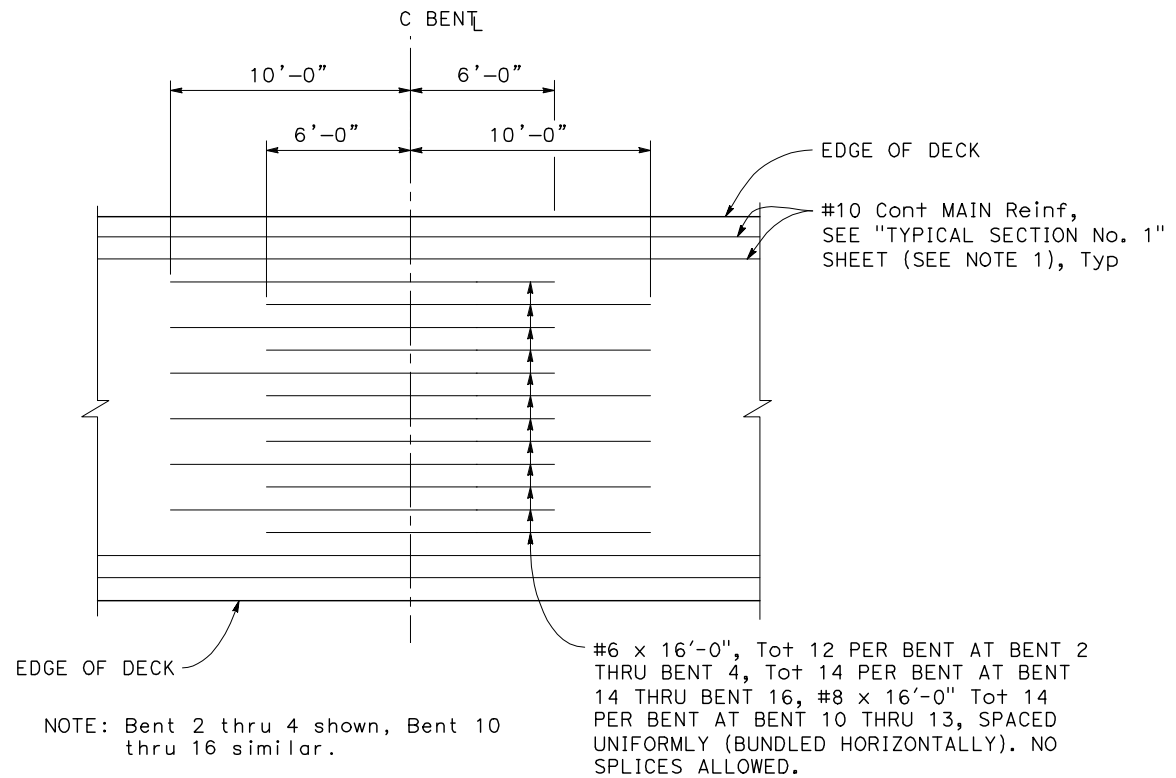


ADDITIONAL TOP GIRDER REINFORCEMENT
BENT 2 THRU 4, BENT 10 THRU 16

1/4" = 1'-0"

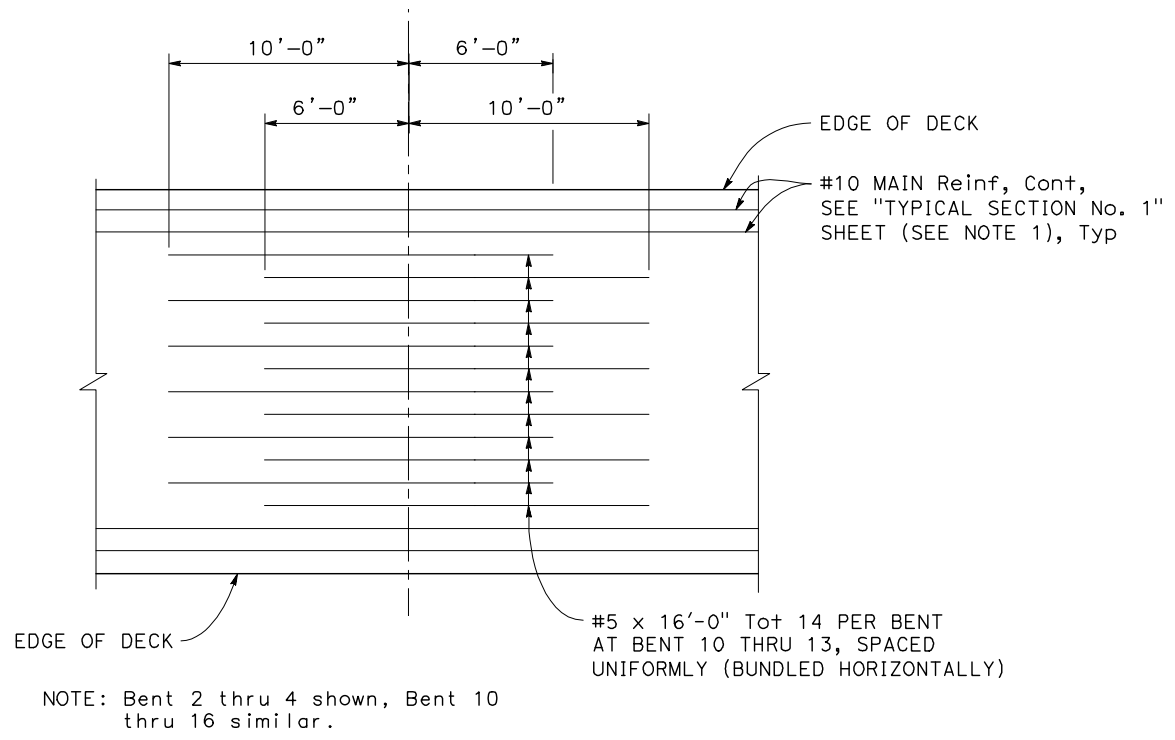


ADDITIONAL BOTTOM GIRDER REINFORCEMENT
BENT 10 THRU 13

1/4" = 1'-0"

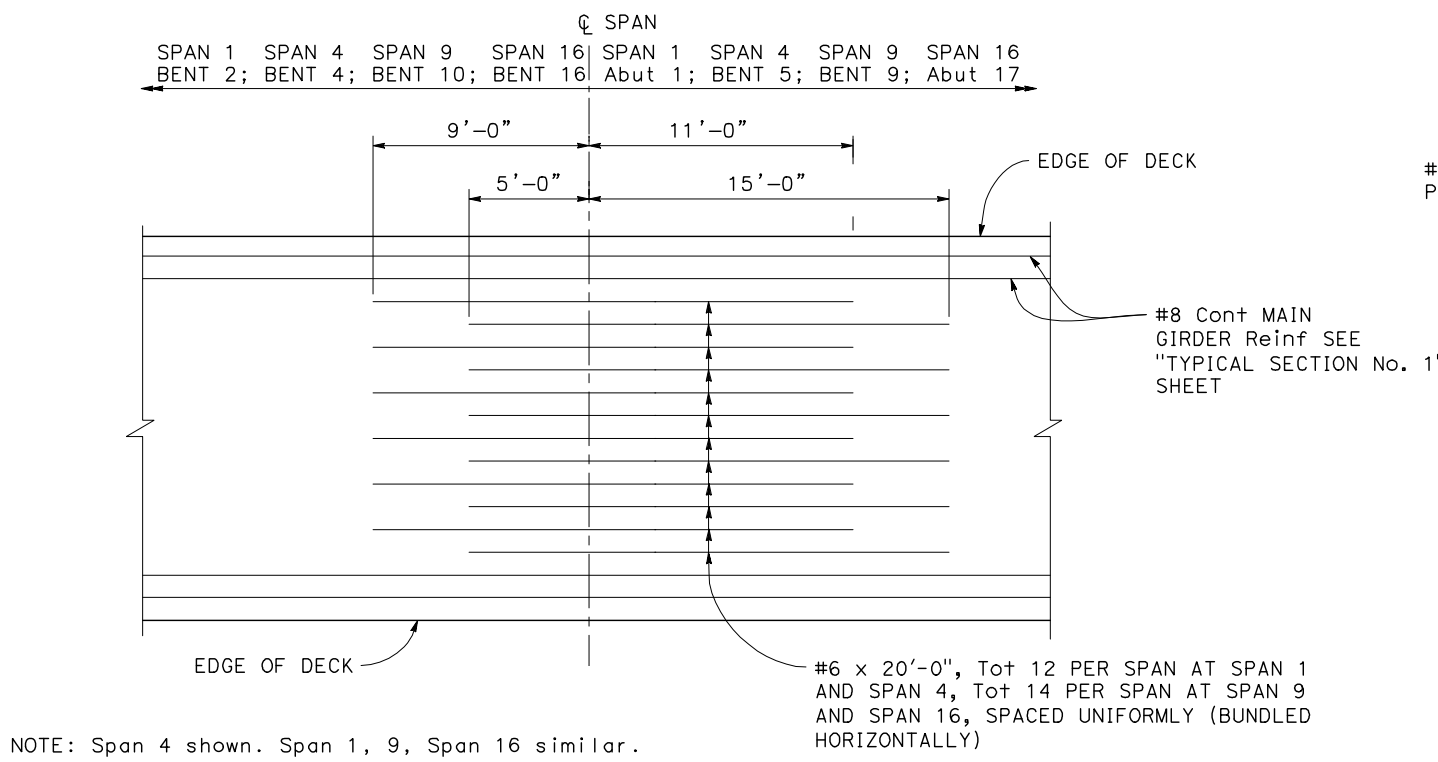

ADDITIONAL BOTTOM GIRDER REINFORCEMENT
SPAN 1 THRU 4, SPAN 9 THRU 16

1/4" = 1'-0"

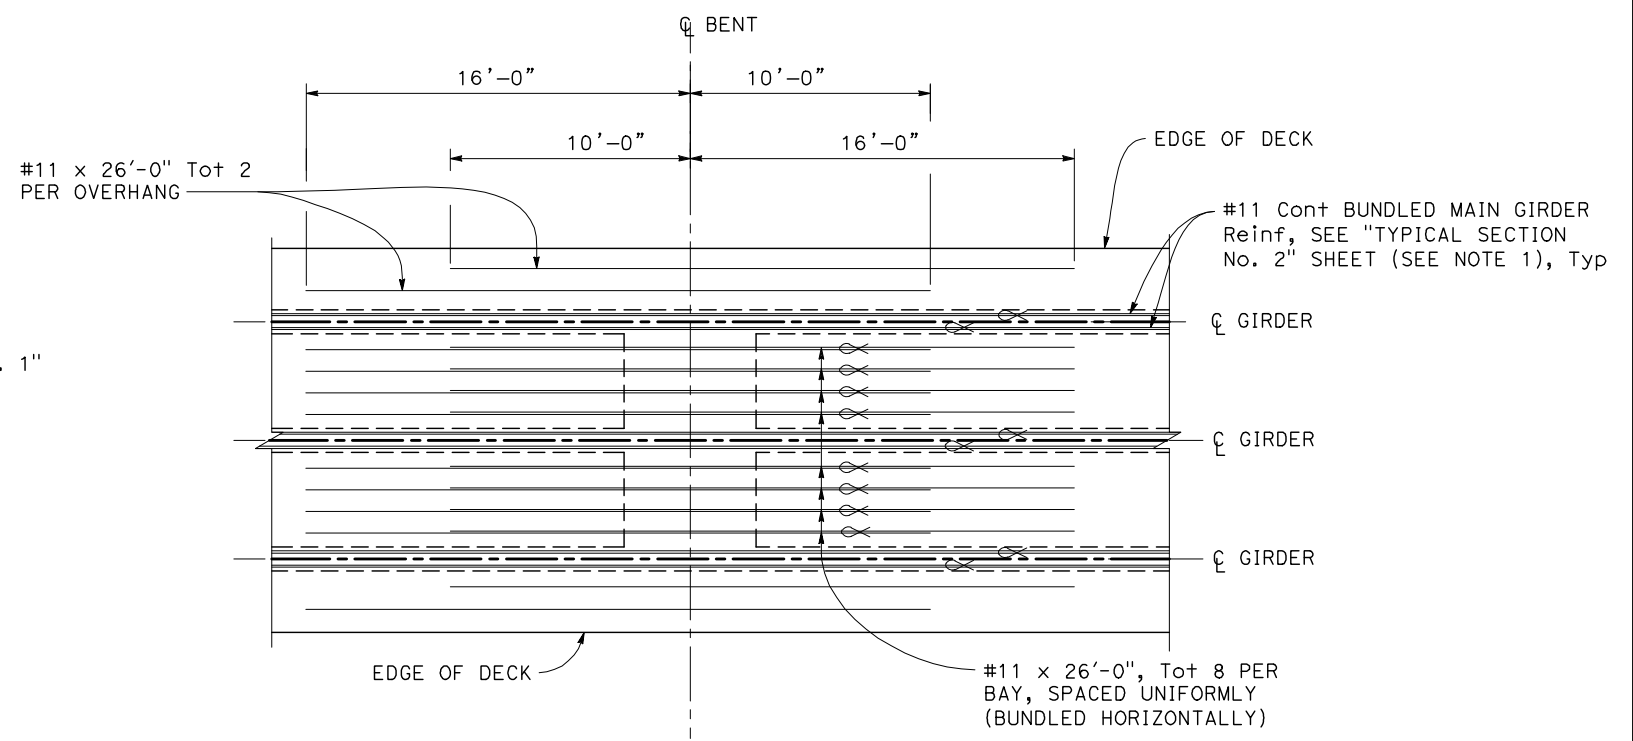

ADDITIONAL TOP GIRDER REINFORCEMENT
BENT 6 THRU 8


1/4" = 1'-0"

X DESIGN OVERSIGHT X SIGN OFF DATE		DESIGN	BY Y. REN	CHECKED X	PREPARED FOR THE STATE OF CALIFORNIA DEPARTMENT OF TRANSPORTATION	BRIDGE No.	MAR VISTA DRIVE POC GIRDER REINFORCEMENT No. 1				
		DETAILS	BY J. DOTY	CHECKED X		36-0128					
		QUANTITIES	BY X	CHECKED X		POST MILE					
						10.87					
DESIGN DETAIL SHEET (ENGLISH) (REVISION 4/19/2018)		DATE PLOTTED => 11/18/2021 FILE => 26-27_MV_POC_GR.dwg		TIME PLOTTED => 7:18 AM USERNAME => JVALENZUELA		ORIGINAL SCALE IN INCHES FOR REDUCED PLANS	UNIT: X PROJECT NUMBER & PHASE: 0518000116	CONTRACT No.: 05-0C7331	DISREGARD PRINTS BEARING EARLIER REVISION DATES	REVISION DATES	SHEET 26 OF 38

Dist	COUNTY	ROUTE	POST MILES TOTAL PROJECT	SHEET NO.	TOTAL SHEETS
05	Scr	1	10.54/13.44	442	453

DRAFT 65% PLANS

REGISTERED STRUCTURAL ENGINEER DATE

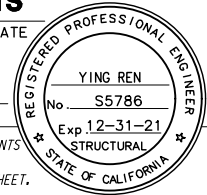

PLANS APPROVAL DATE

THE STATE OF CALIFORNIA OR ITS OFFICERS OR AGENTS
SHALL NOT BE RESPONSIBLE FOR THE ACCURACY OR
COMPLETENESS OF SCANNED COPIES OF THIS PLAN SHEET.


MARK THOMAS
701 UNIVERSITY AVE., SUITE 200
SACRAMENTO, CA 95825

SCCRTC
1523 PACIFIC AVENUE
SANTA CRUZ, CA 95090

NOTE B:
1. No splices allowed within 25'-0"
either side of ϕ Span.

LEGEND

∞ Indicates bundled bar

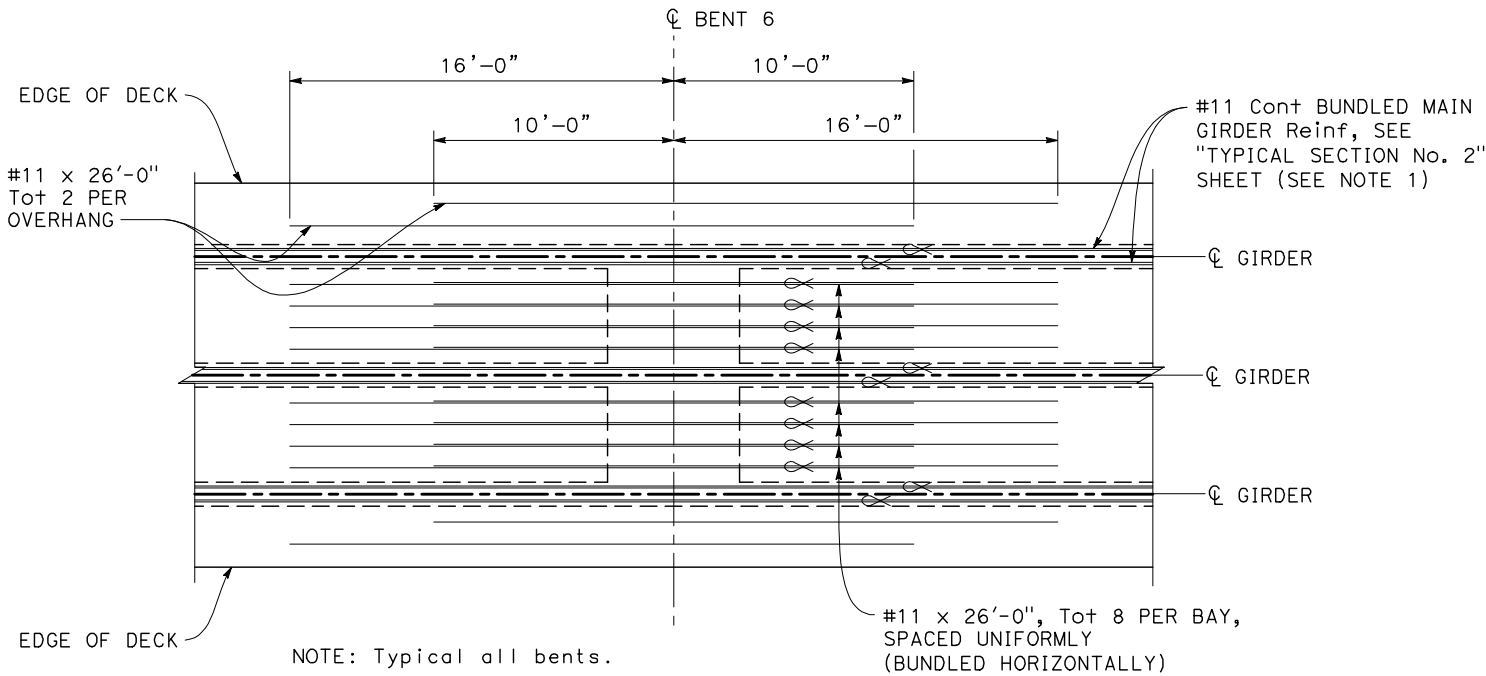


NOTE: Typical all bents.

ADDITIONAL TOP GIRDER REINFORCEMENT

BENT 6 THRU 8


1/4"= 1'-0"

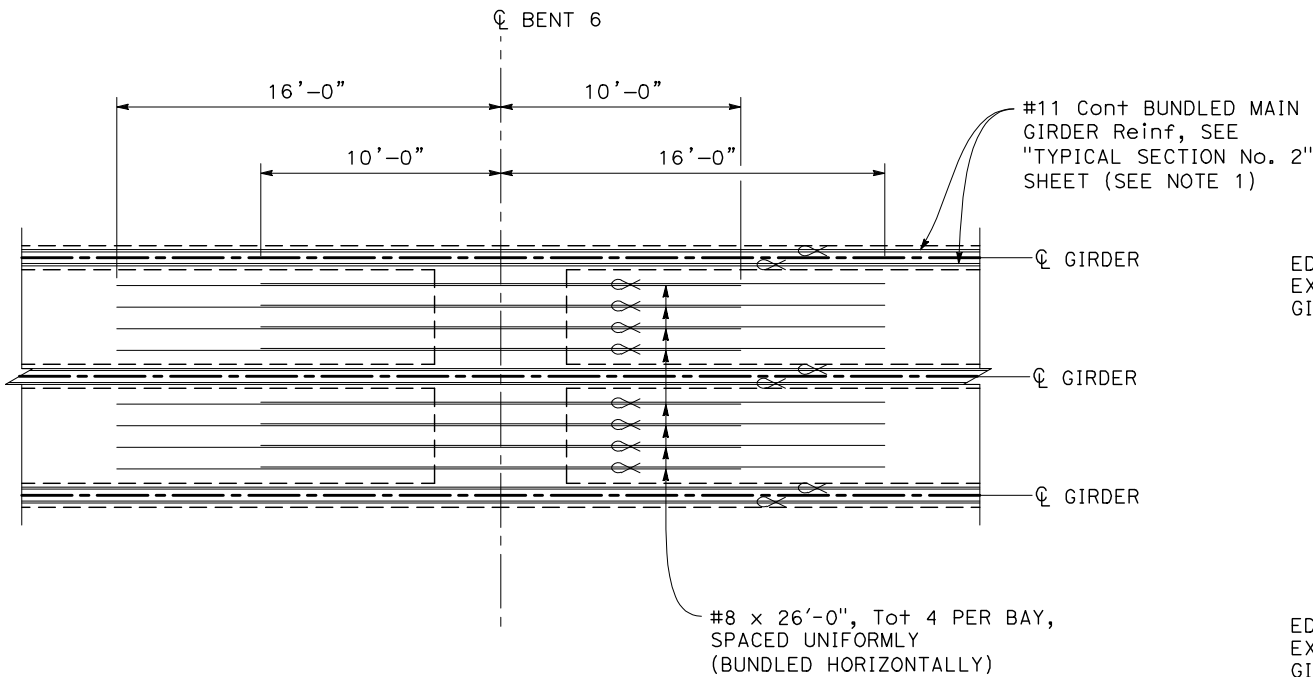

ADDITIONAL BOTTOM GIRDER REINFORCEMENT

BENT 6 THRU 8

1/4"= 1'-0"

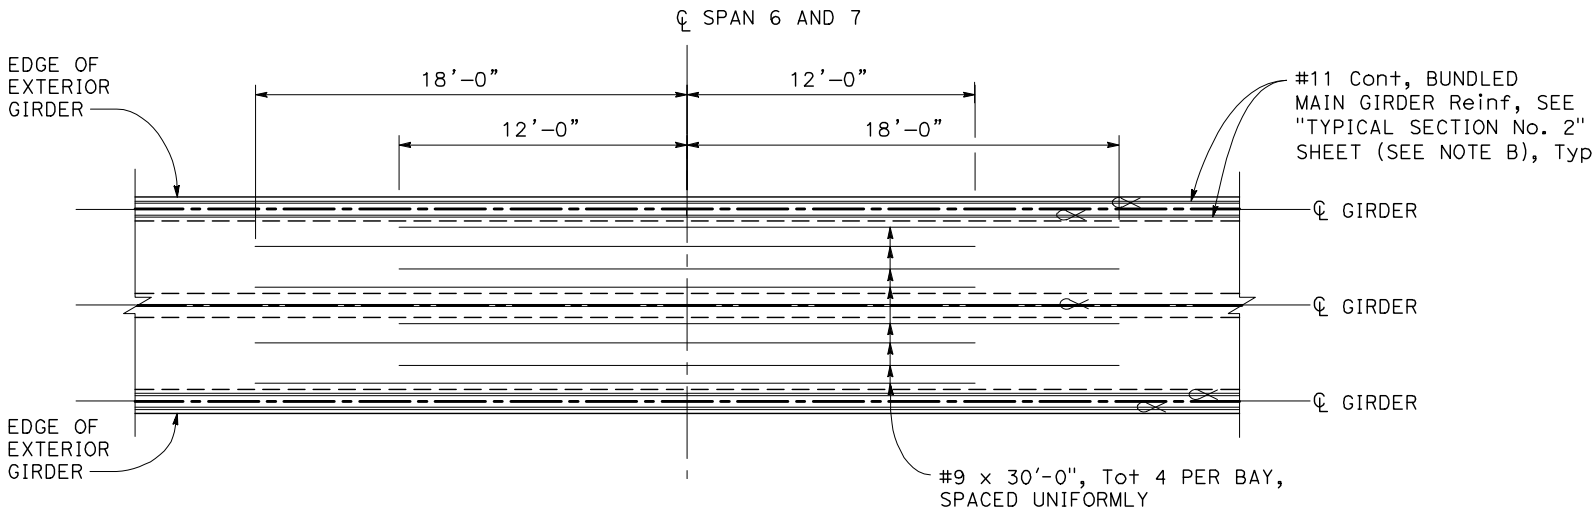

ADDITIONAL BOTTOM GIRDER REINFORCEMENT

AT MID-SPAN 6, 7


1/4"= 1'-0"

X DESIGN OVERSIGHT		DESIGN BY Y. REN		CHECKED X	PREPARED FOR THE STATE OF CALIFORNIA DEPARTMENT OF TRANSPORTATION		ERIC FREDRICKSON PROJECT ENGINEER		BRIDGE No. 36-0128		MAR VISTA DRIVE POC GIRDER REINFORCEMENT No. 2								
X SIGN OFF DATE		DETAILS BY J. DOTY		CHECKED X					POST MILE 10.87										
DESIGN DETAIL SHEET (ENGLISH) (REVISION 4/19/2018)		DATE PLOTTED => 11/18/2021 FILE => 26-27_MV_POC_GR.dwg		TIME PLOTTED => 8:40 AM USERNAME => JVALENZUELA		ORIGINAL SCALE IN INCHES FOR REDUCED PLANS		UNIT: X PROJECT NUMBER & PHASE: 0518000116		CONTRACT No.: 05-0C7331		DISREGARD PRINTS BEARING EARLIER REVISION DATES		REVISION DATES 6-18-21		SHEET 27		OF 38	

Dist	COUNTY	ROUTE	POST MILES TOTAL PROJECT	SHEET NO.	TOTAL SHEETS
05	Scr	1	10.54/13.44	443	453

DRAFT 65% PLANS

REGISTERED STRUCTURAL ENGINEER DATE

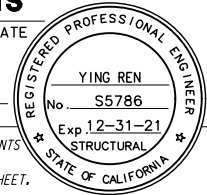


PLANS APPROVAL DATE


THE STATE OF CALIFORNIA OR ITS OFFICERS OR AGENTS
SHALL NOT BE RESPONSIBLE FOR THE ACCURACY OR
COMPLETENESS OF SCANNED COPIES OF THIS PLAN SHEET.

MARK THOMAS
701 UNIVERSITY AVE., SUITE 200
SACRAMENTO, CA 95825


SCCRTC
1523 PACIFIC AVENUE
SANTA CRUZ, CA 95090

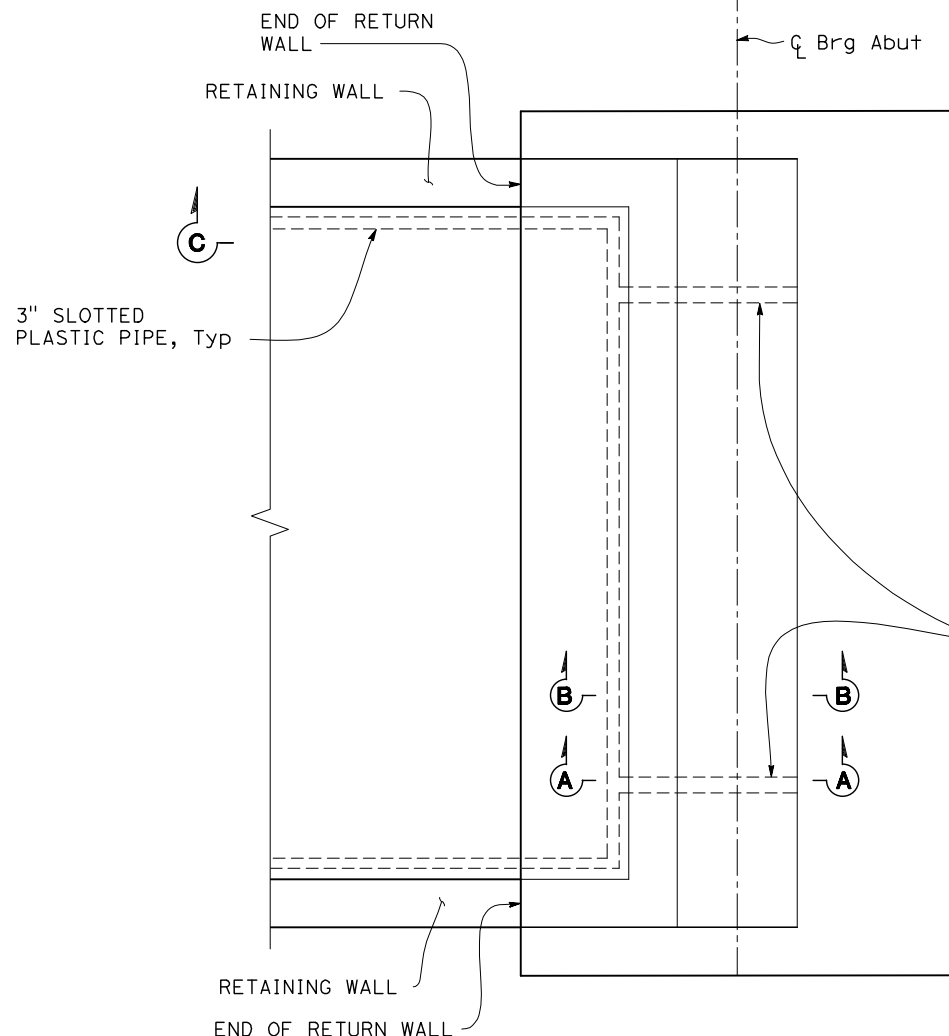


PLAN
1/2"=1'-0"

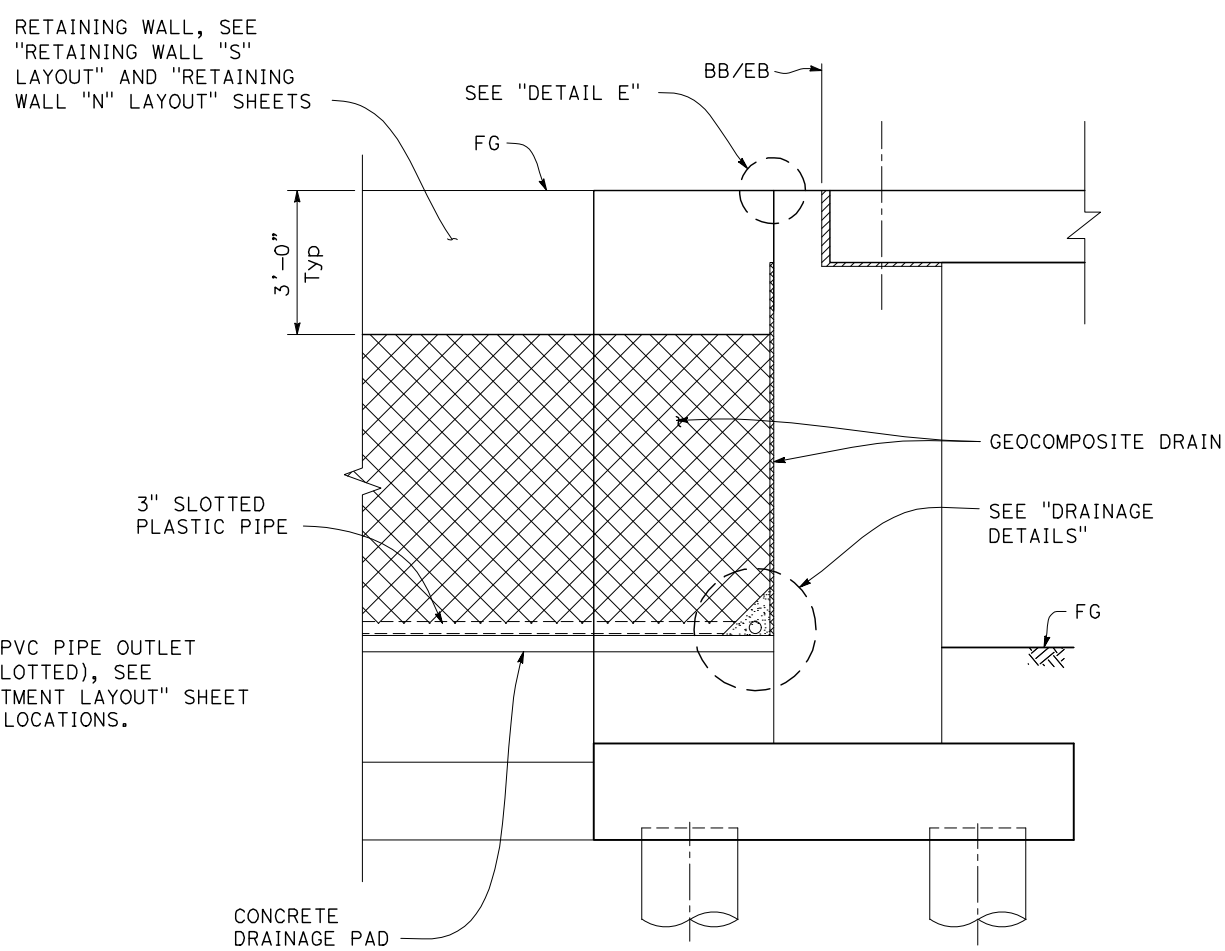


SECTION C-C
1/2" = 1'-0"

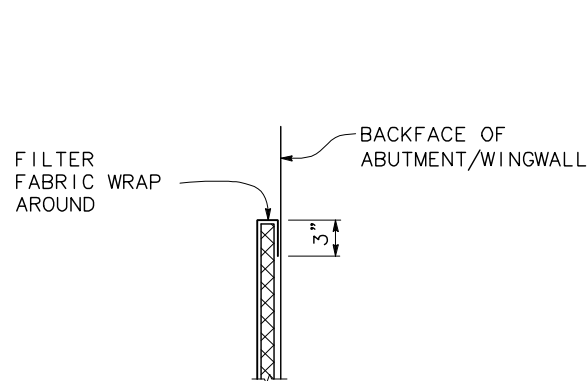


DETAIL E

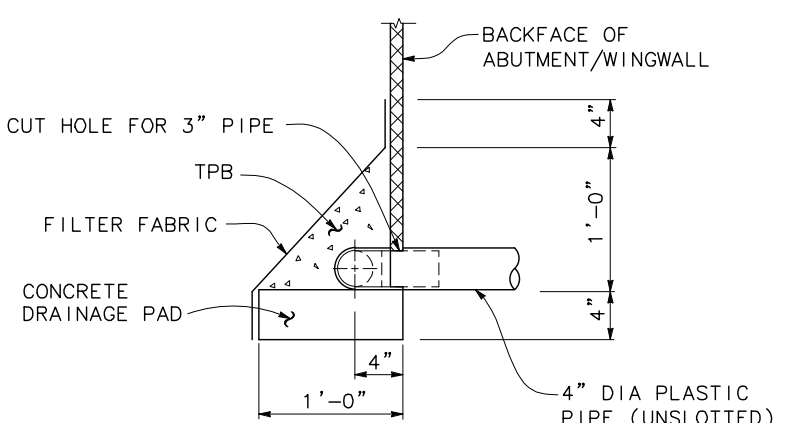

SECTION A-A

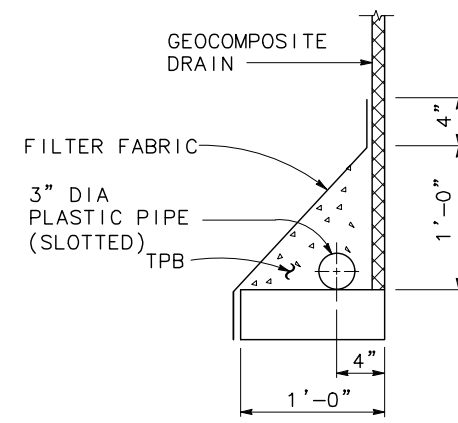

SECTION B-B

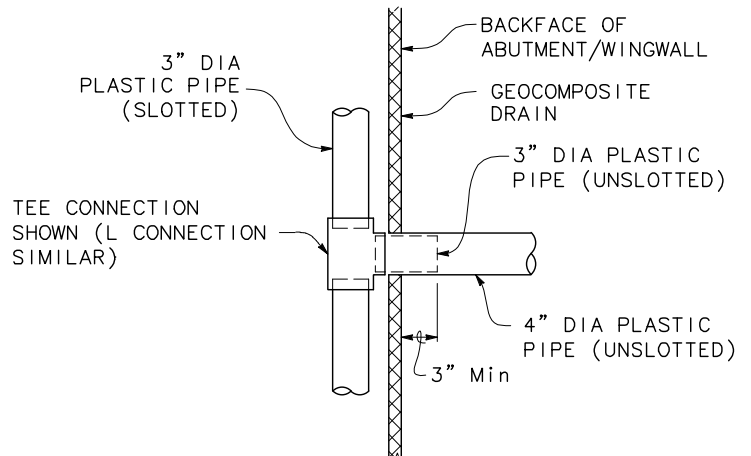

T-CONNECTION

DRAINAGE DETAILS
1 1/2" = 1'-0"

X	DESIGN OVERSIGHT
X	SIGN OFF DATE

DESIGN	BY Y. REN	CHECKED X
DETAILS	BY J. DOTY	CHECKED X
QUANTITIES	BY X	CHECKED X

**PREPARED FOR THE
STATE OF CALIFORNIA
DEPARTMENT OF TRANSPORTATION**

ERIC FREDRICKSON
PROJECT ENGINEER

BRIDGE No.	36-0128
POST MILE	10.87

**MAR VISTA DRIVE POC
ABUTMENT DRAINAGE DETAILS**

DESIGN DETAIL SHEET
(ENGLISH) (REVISION 4/19/2018)

DATE PLOTTED => 11/18/2021
FILE => 28_MV_POC_ADD.dwg
TIME PLOTTED => 8:52 AM
USERNAME => JVALENZUELA
ORIGINAL SCALE
IN INCHES FOR
REDUCED PLANS

0 1 2 3

UNIT: X
PROJECT NUMBER & PHASE: 0518000116

CONTRACT No.: 05-OC7331

DISREGARD PRINTS BEARING EARLIER REVISION DATES	REVISION DATES	SHEET	OF
	6-18-21	28	38

DIST05COUNTYSCRRUTE1POST MILESTOTAL PROJECT10.54/13.44SHEET No.444TOTAL SHEETS453

DRAFT 65% PLANS

REGISTERED STRUCTURAL ENGINEER DATE

PLANS APPROVAL DATE

YING REN

No. S5786


Exp. 12-31-21

STRUCTURAL


STATE OF CALIFORNIA

The State of California or its officers or agents shall not be responsible for the accuracy or completeness of scanned copies of this plan sheet.


The Registered Civil Engineer for the project is responsible for the selection and proper application of the component design and any modifications shown.

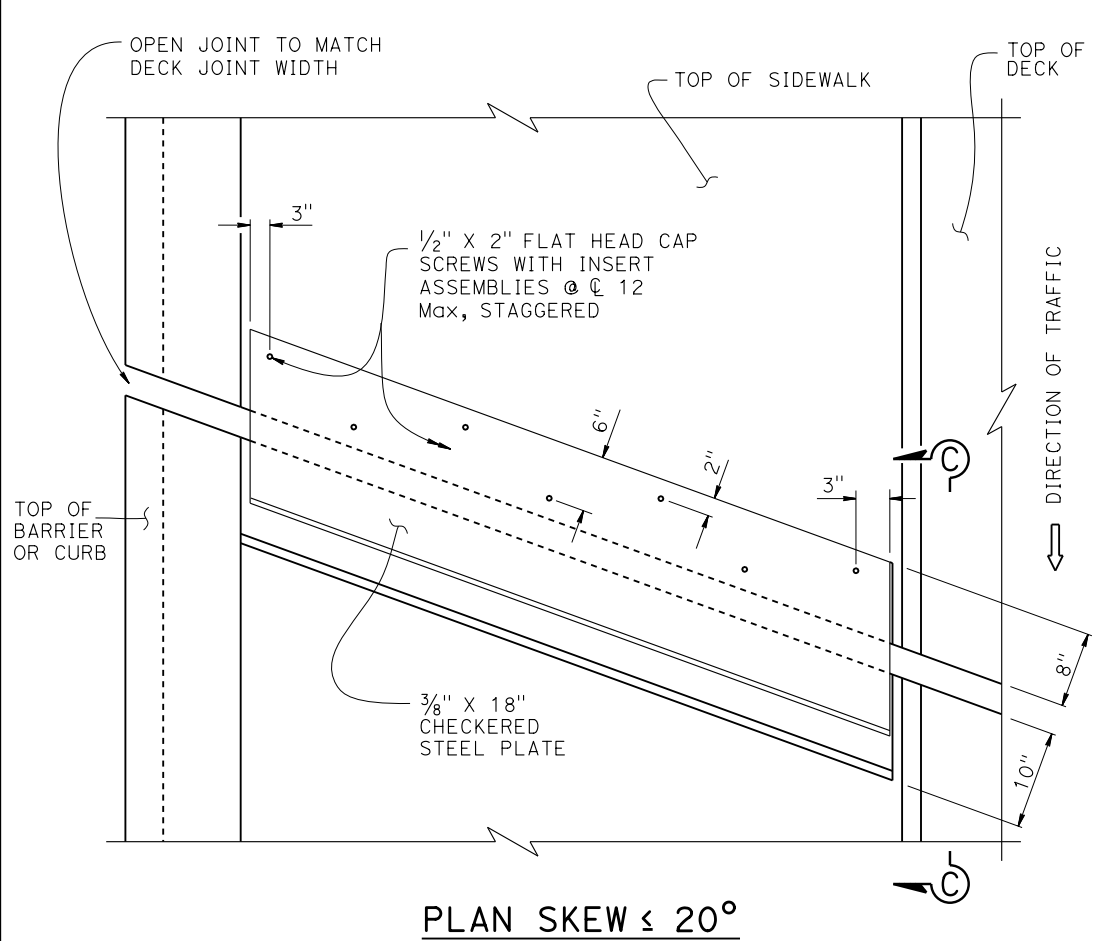


PLAN SKEW ≤ 20°

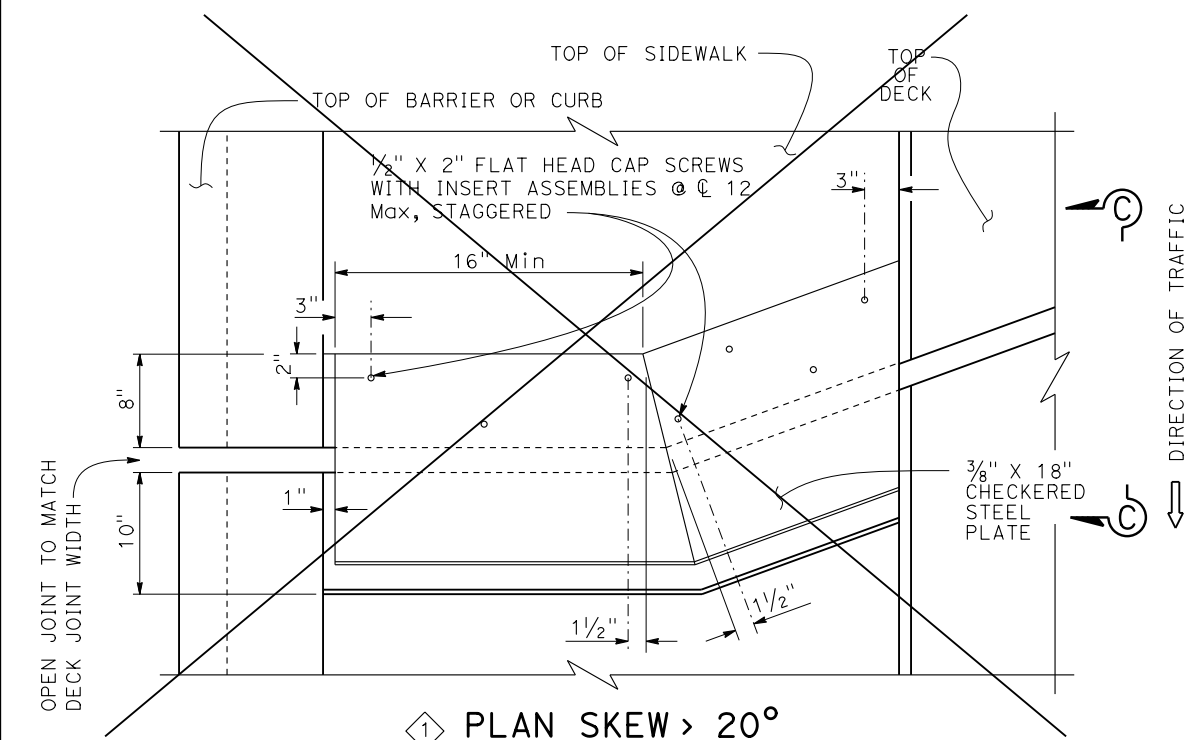


PLAN SKEW > 20°

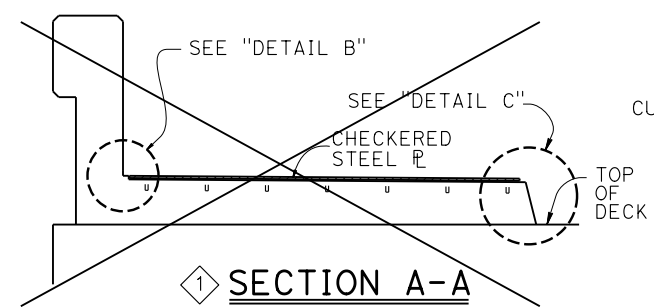


SECTION A-A

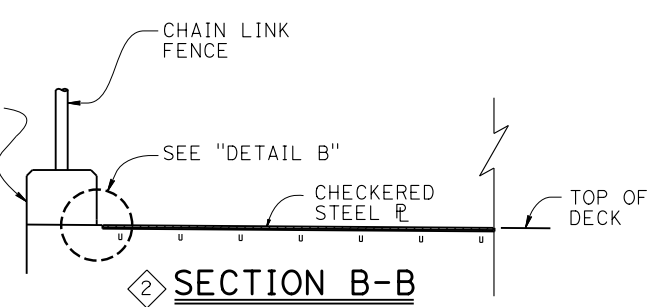

SECTION B-B

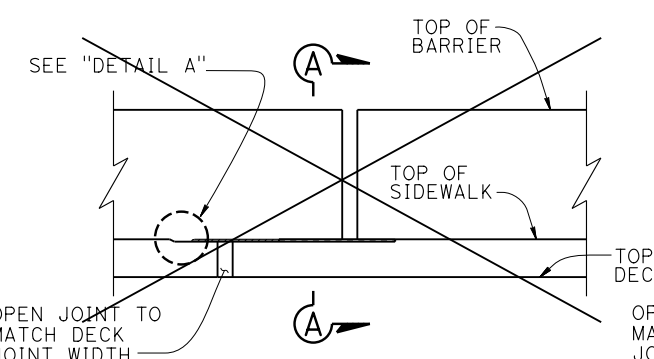


ELEVATION

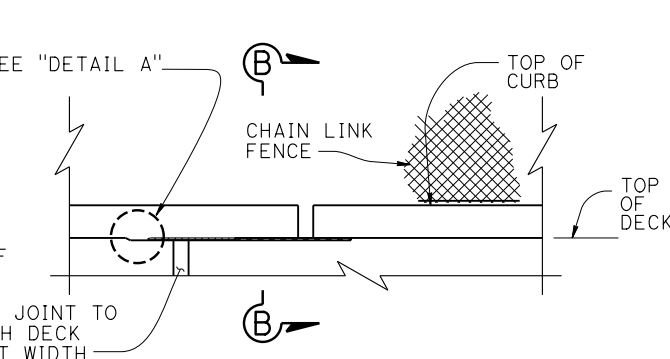


ELEVATION


NOTE: Barrier not shown for clarity

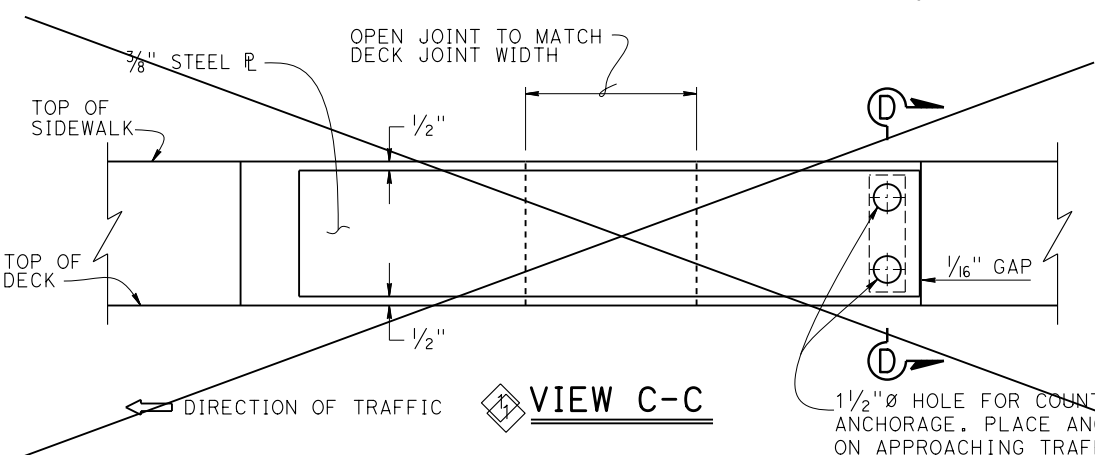


VIEW C-C

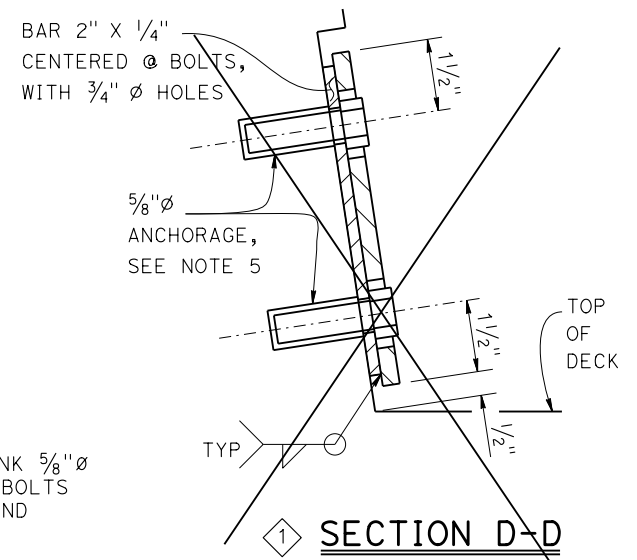


SECTION D-D

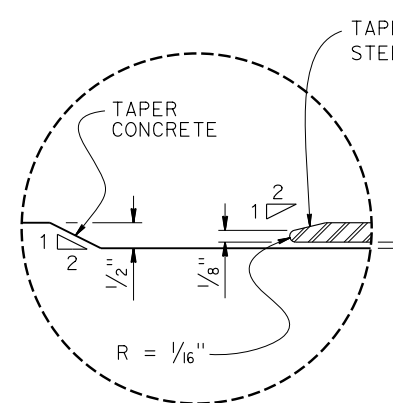

DETAIL A

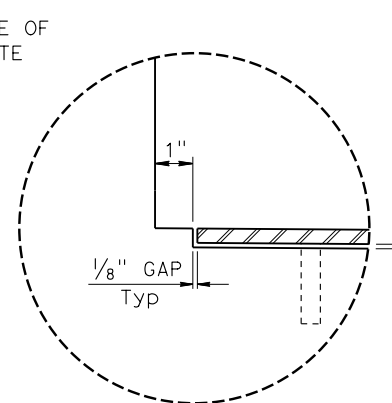

DETAIL B

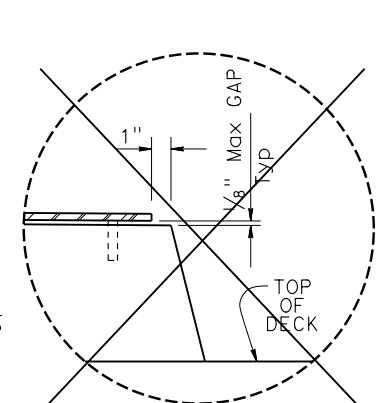

DETAIL C

NO SCALE

Dist	COUNTY	ROUTE	POST MILES TOTAL PROJECT	SHEET No.	TOTAL SHEETS
05	Scr	1	10.54/13.44	445	453

DRAFT 65% PLANS



REGISTERED STRUCTURAL ENGINEER DATE

PLANS APPROVAL DATE

THE STATE OF CALIFORNIA OR ITS OFFICERS OR AGENTS
SHALL NOT BE RESPONSIBLE FOR THE ACCURACY OR
COMPLETENESS OF SCANNED COPIES OF THIS PLAN SHEET.

MARK THOMAS
701 UNIVERSITY AVE., SUITE 200
SACRAMENTO, CA 95825

SCCRTC
1523 PACIFIC AVENUE
SANTA CRUZ, CA 95090

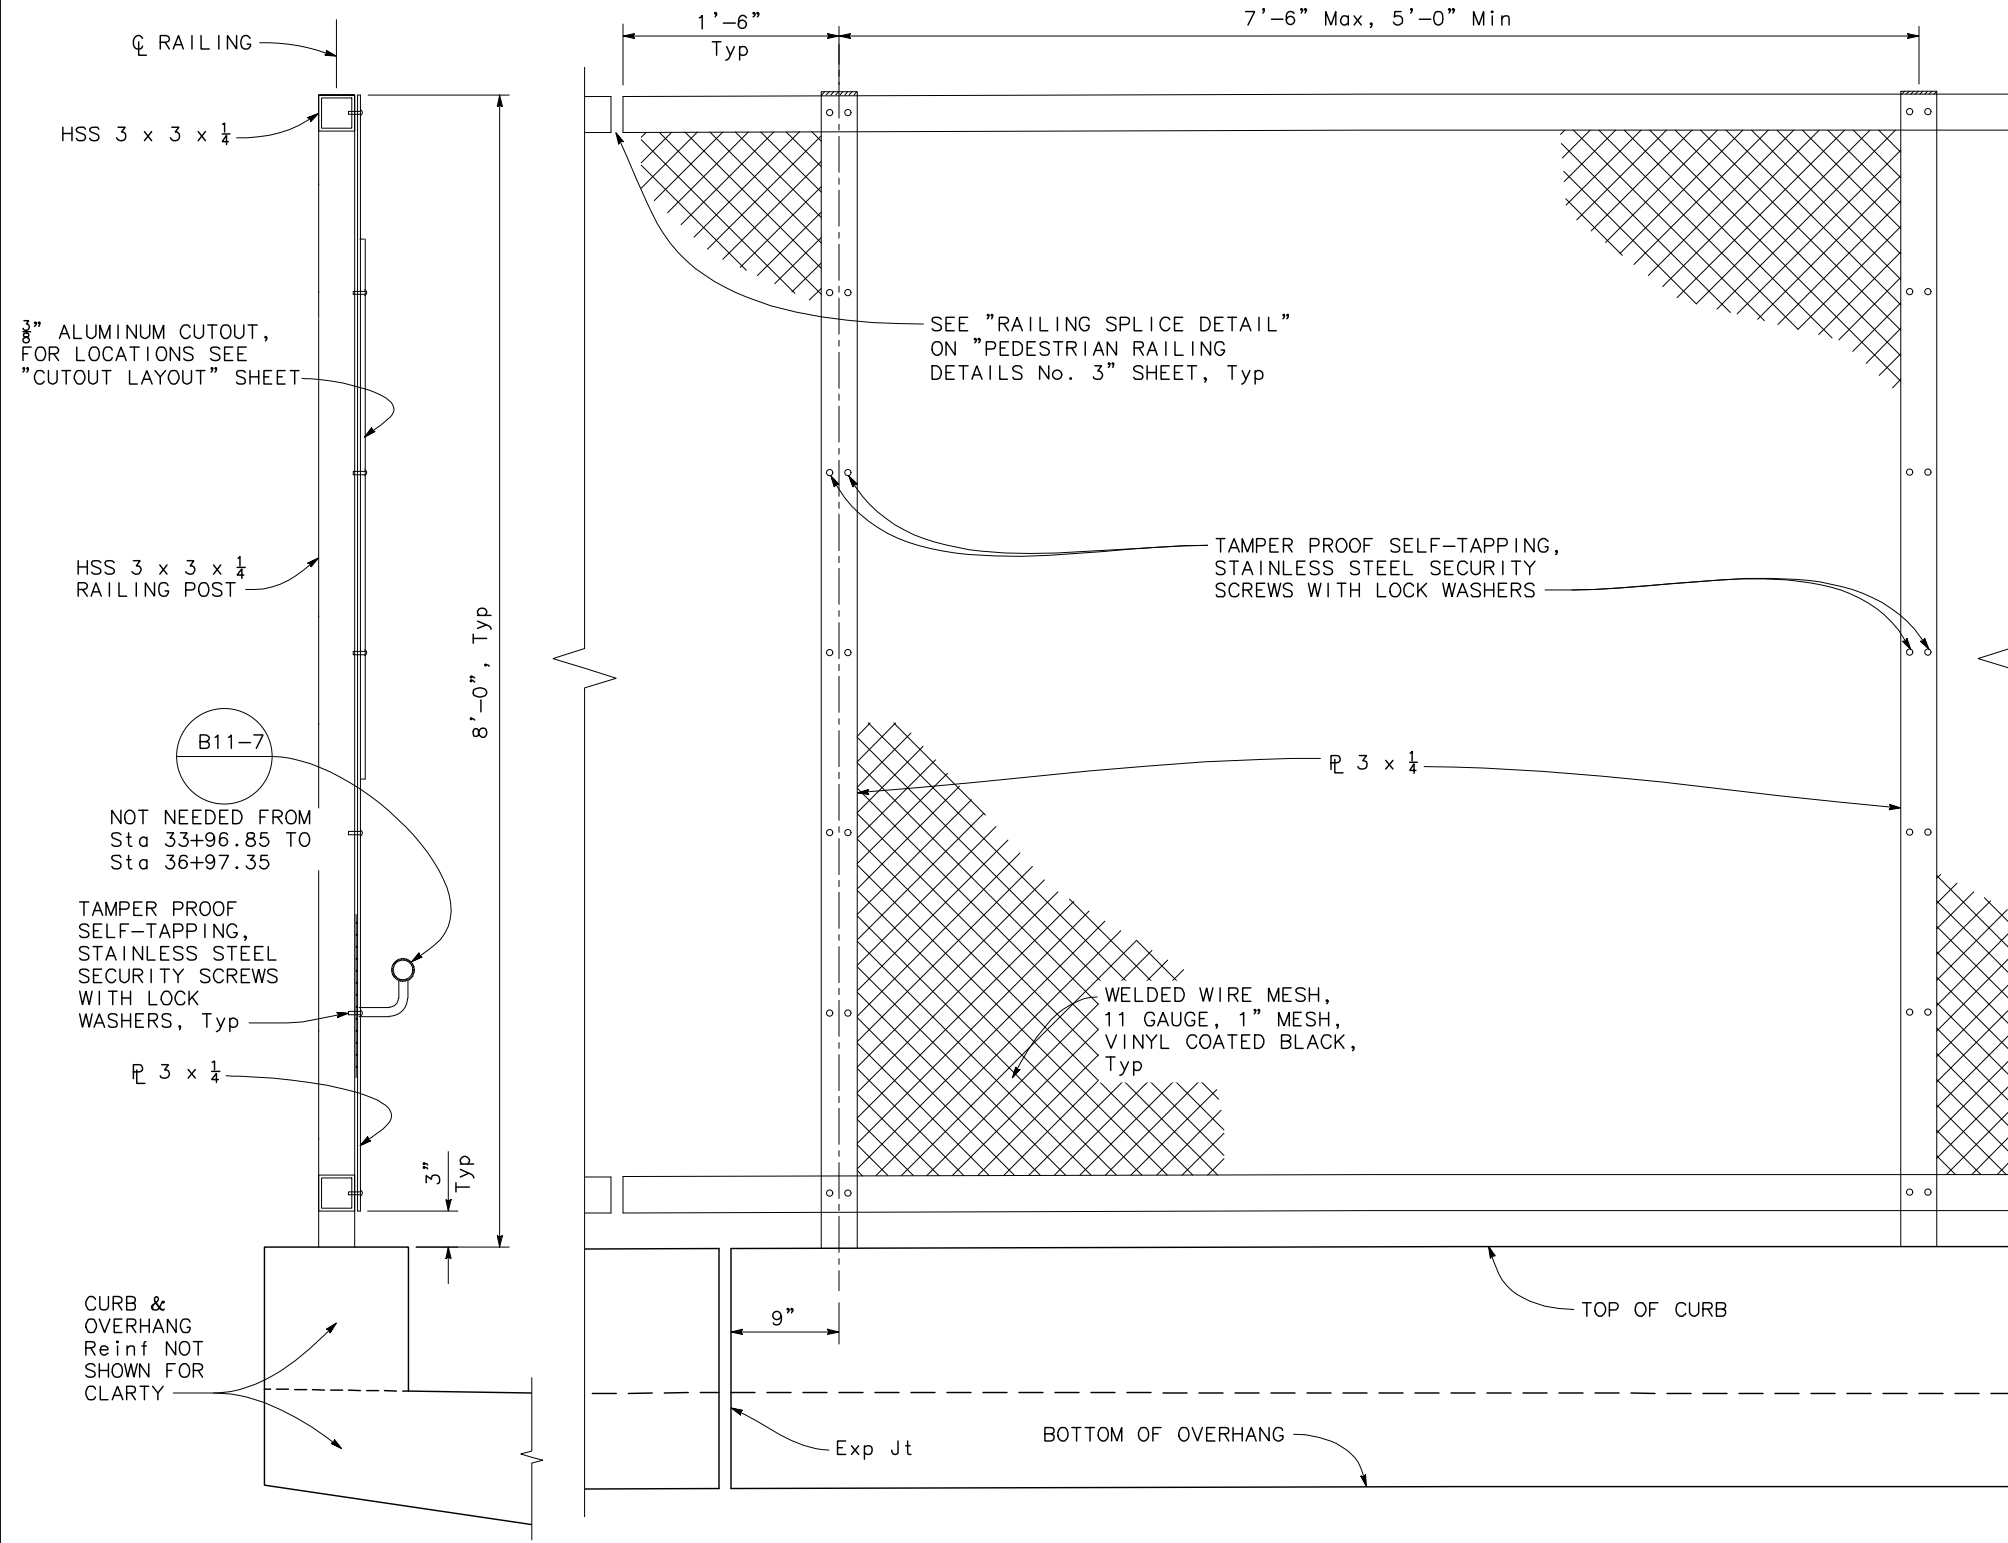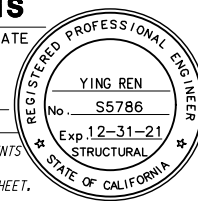


TYPICAL RAILING SECTION (TYPE B)

1 1/2"=1'-0"


RAILING ELEVATION (TYPE B)

1 1/2"=1'-0"

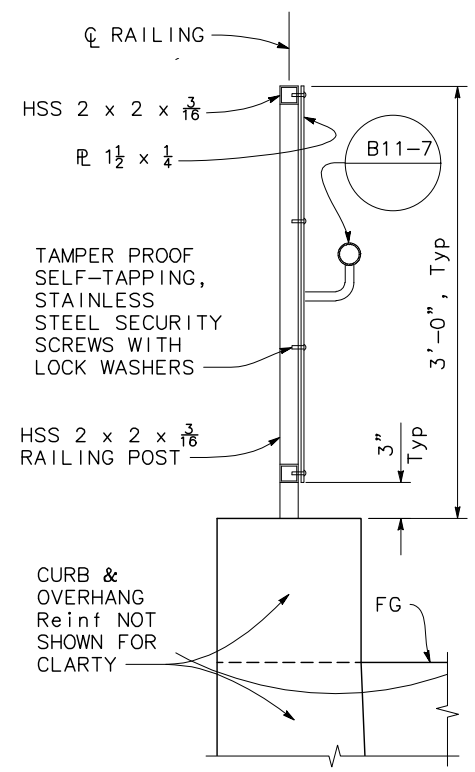

TYPICAL RAILING SECTION (TYPE A)

1 1/2"=1'-0"

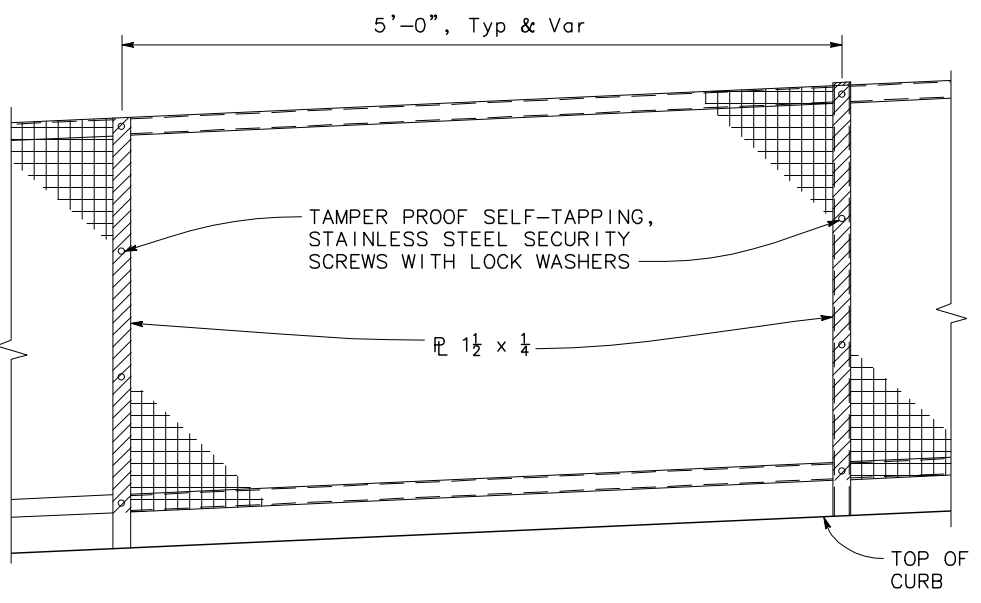

RAILING ELEVATION (TYPE A)

1 1/2"=1'-0"

- NOTES:
- All posts, horizontal members and plates for pedestrian railing (Type A) and (Type B) to be powder-coated black (FED-STD-595 No. 17038). See project specifications for more information.
 - Railing posts and horizontal HSS members to be A500 Grade B, Fy = 46 ksi.
 - Railing shall conform to horizontal and vertical alignment.
 - When railing is in slope, welded wire mesh shall be placed parallel to slope.

X	DESIGN OVERSIGHT
X	SIGN OFF DATE

DESIGN	BY Y. REN	CHECKED X
DETAILS	BY J. DOTY	CHECKED X
QUANTITIES	BY X	CHECKED X

PREPARED FOR THE
STATE OF CALIFORNIA
DEPARTMENT OF TRANSPORTATION

ERIC FREDRICKSON
PROJECT ENGINEER

BRIDGE No.
36-0128
POST MILE
10.87

MAR VISTA DRIVE POC
PEDESTRIAN RAILING DETAILS No.1

DESIGN DETAIL SHEET
(ENGLISH) (REVISION 4/19/2018)

DATE PLOTTED => 11/18/2021
FILE => 30-33_MV_POC_PRD.dwg

TIME PLOTTED => 9:31 AM
USERNAME => JVALENZUELA


ORIGINAL SCALE
IN INCHES FOR
REDUCED PLANS

0 1 2 3


UNIT: X
PROJECT NUMBER & PHASE: 0518000116

CONTRACT No.: 05-0C7331


DISREGARD PRINTS BEARING EARLIER REVISION DATES	REVISION DATES	SHEET	OF
	6-18-21	30	38

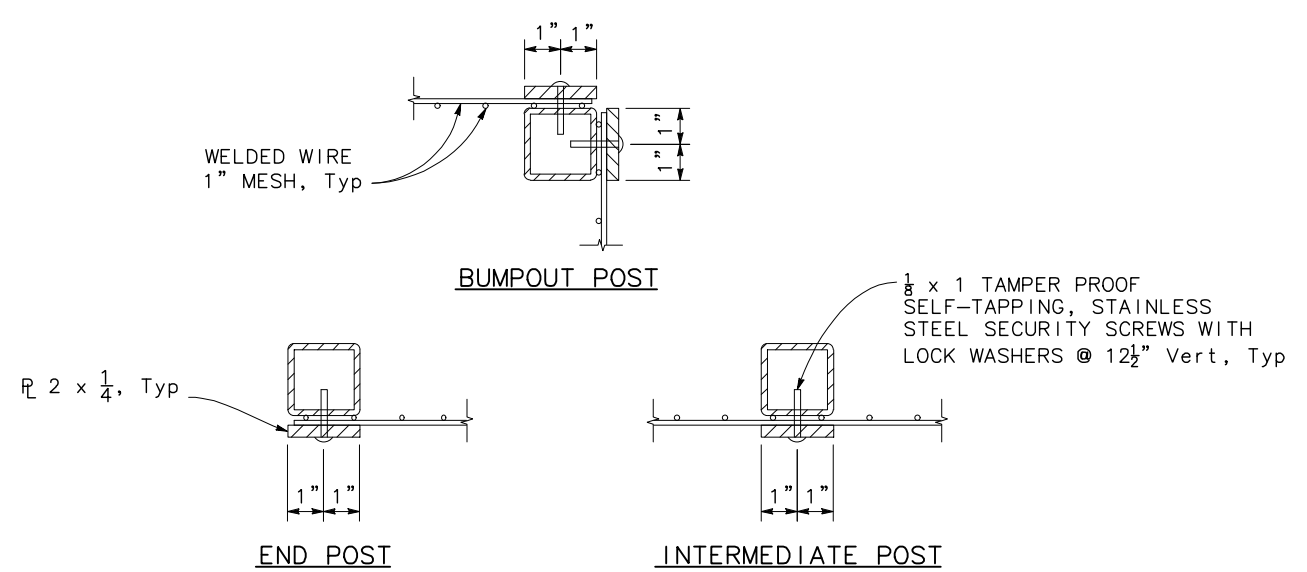


TYPICAL POST SECTIONS (TYPE A)
NO SCALE

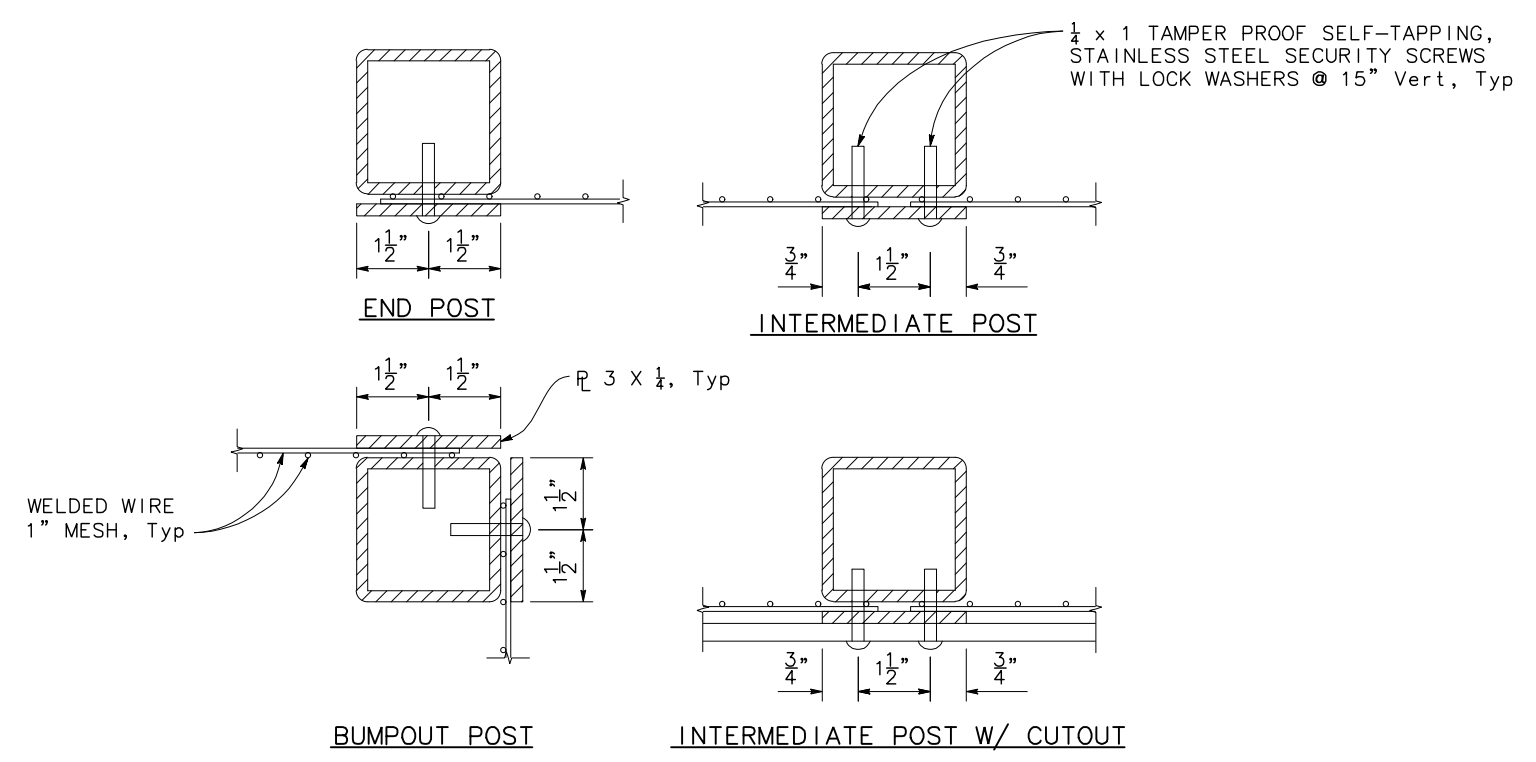

TYPICAL POST SECTIONS (TYPE B)
NO SCALE

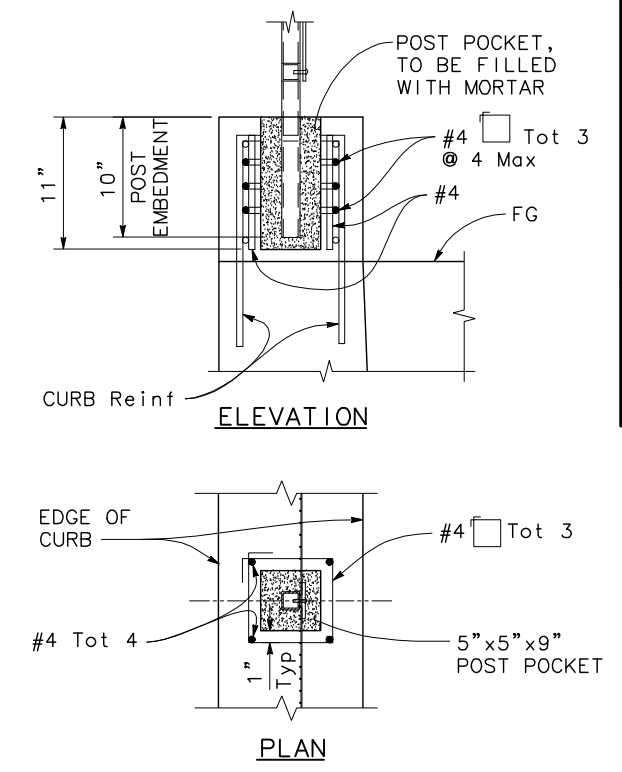

RAILING ANCHORAGE DETAILS (TYPE A)
1 1/2"=1'-0"

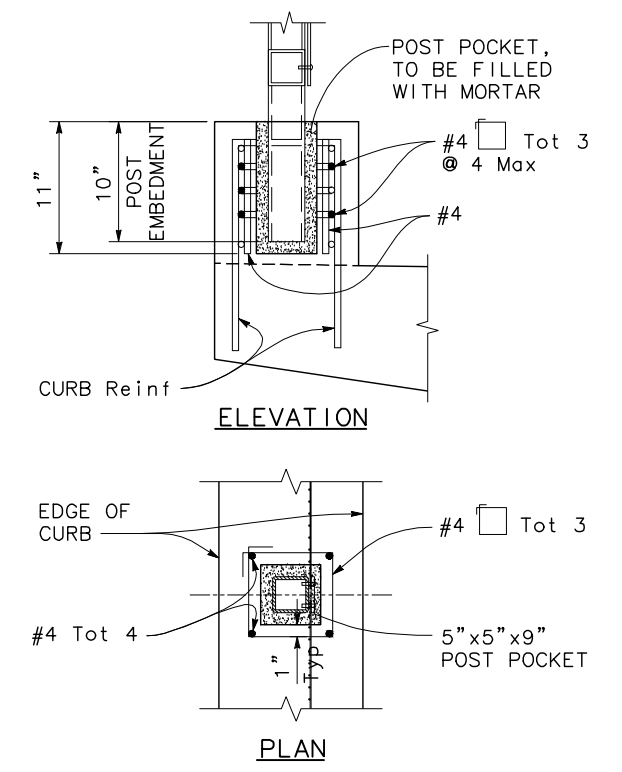

RAILING ANCHORAGE DETAILS (TYPE B)
1 1/2"=1'-0"

Dist	COUNTY	ROUTE	POST MILES TOTAL PROJECT	SHEET No.	TOTAL SHEETS
05	Scr	1	10.54/13.44	446	453

DRAFT 65% PLANS

REGISTERED STRUCTURAL ENGINEER DATE

PLANS APPROVAL DATE

THE STATE OF CALIFORNIA OR ITS OFFICERS OR AGENTS SHALL NOT BE RESPONSIBLE FOR THE ACCURACY OR COMPLETENESS OF SCANNED COPIES OF THIS PLAN SHEET.

MARK THOMAS
701 UNIVERSITY AVE., SUITE 200
SACRAMENTO, CA 95825

SCCRTC
1523 PACIFIC AVENUE
SANTA CRUZ, CA 95090

REGISTERED PROFESSIONAL ENGINEER

YING REN

No. S5786

Exp. 12-31-21

STRUCTURAL

STATE OF CALIFORNIA

Dist	COUNTY	ROUTE	POST MILES TOTAL PROJECT	SHEET NO.	TOTAL SHEETS
05	Scr	1	10.54/13.44	447	453

DRAFT 65% PLANS


REGISTERED STRUCTURAL ENGINEER DATE

PLANS APPROVAL DATE

THE STATE OF CALIFORNIA OR ITS OFFICERS OR AGENTS
SHALL NOT BE RESPONSIBLE FOR THE ACCURACY OR
COMPLETENESS OF SCANNED COPIES OF THIS PLAN SHEET.


MARK THOMAS
701 UNIVERSITY AVE., SUITE 200
SACRAMENTO, CA 95825

SCCRTC
1523 PACIFIC AVENUE
SANTA CRUZ, CA 95090

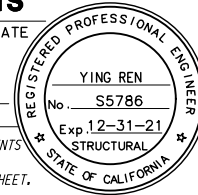

NOTES:



- See project specifications for additional information on redwood cutout fasteners.
- Number and location of mounting bolts to be determined by redwood cutout supplier.
- Mounting bolts to be provided at each pst where redwood cutouts are located. Vertical spacing of mounting bolts shall not exceed 18".

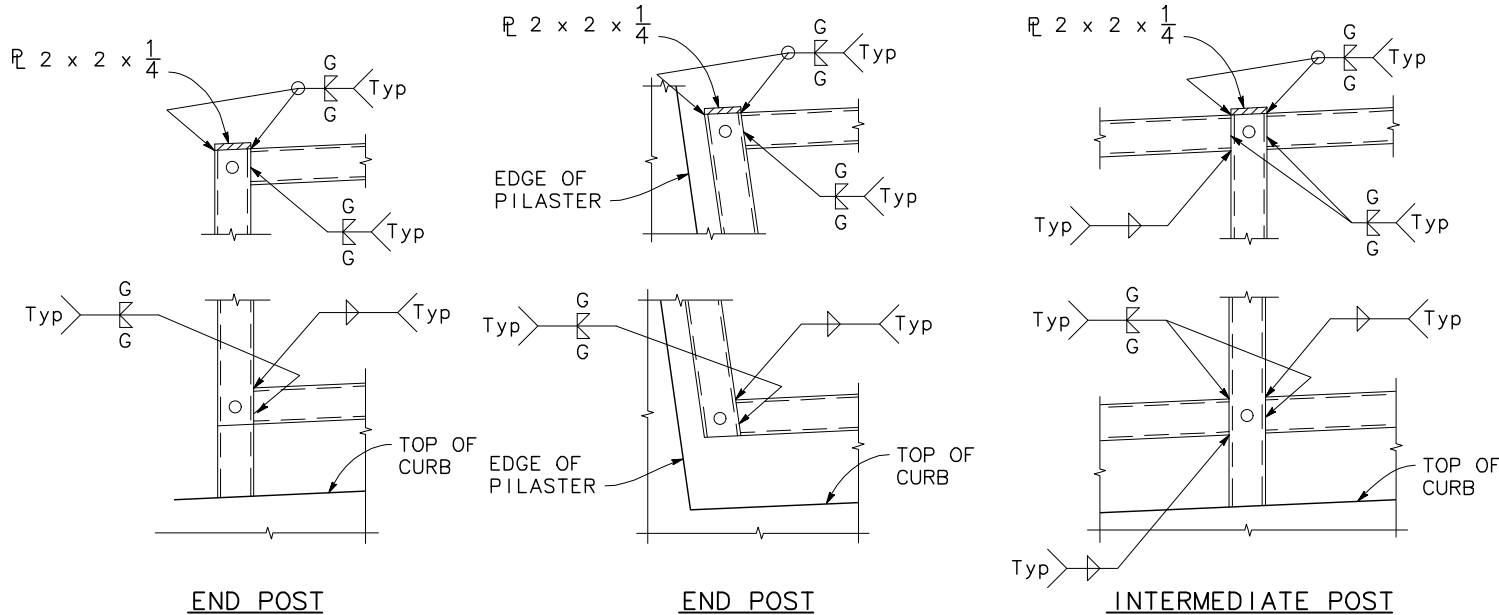

RAILING CONNECTION DETAILS (TYPE A)



3"=1'-0"

NOTE: $\angle 2 \times \frac{1}{4}$, screws and welded wire mesh not shown.

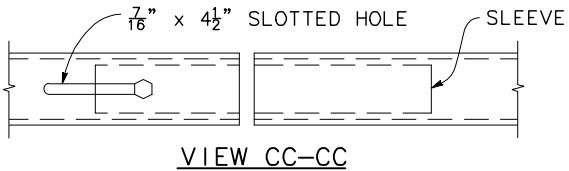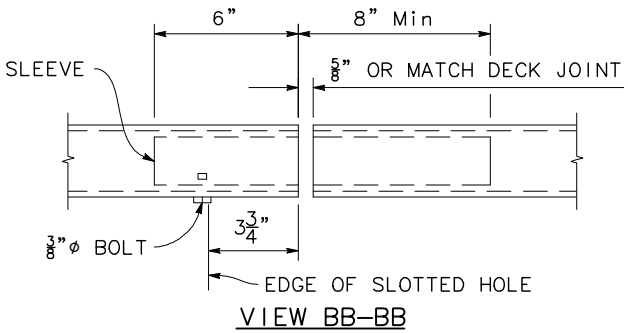

TACK WELD $\frac{3}{8}$ " NUT INSIDE OF SLEEVE FOR $\frac{3}{8}$ " Hex BOLT WITH LOCK WASHER


SLEEVE FORMED OF $\frac{3}{8}$ " $\angle$ BENT THUS $\frac{1}{2}$ ", FOR SLIDING FIT INSIDE OF RAIL TUBE

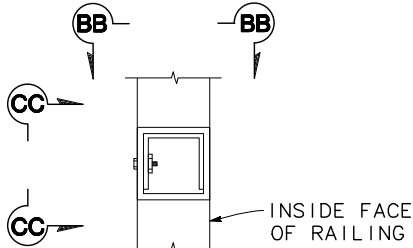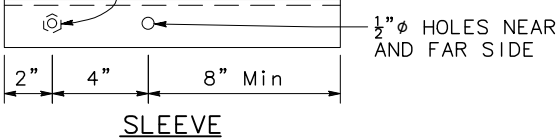

SECTION

RAILING SPLICE DETAIL


NO SCALE

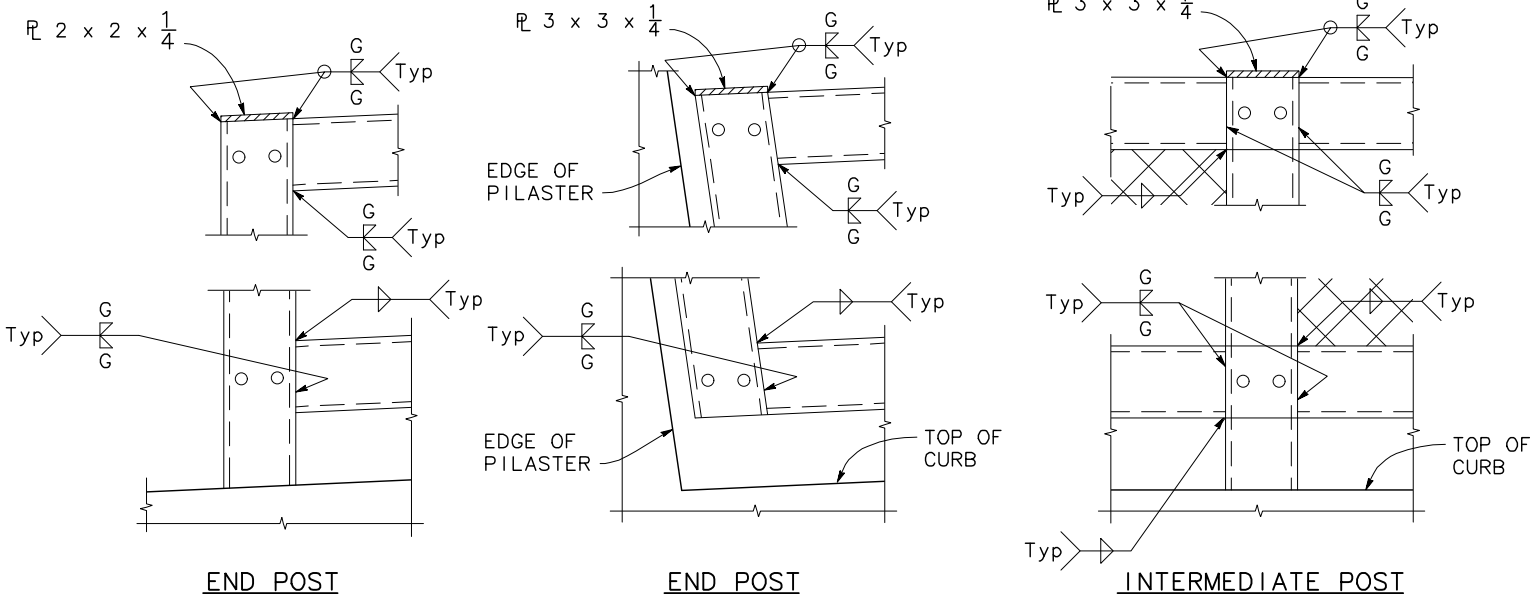

RAILING CONNECTION DETAILS (TYPE B)

3"=1'-0"

NOTE: $\angle 3 \times \frac{1}{4}$, screws and welded wire mesh not shown.

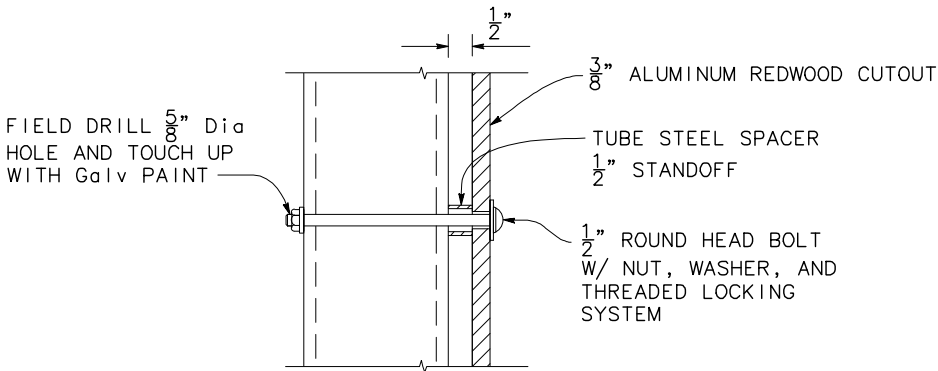

REDWOOD CUTOUT MOUNTING DETAIL


6"=1'-0"

X DESIGN OVERSIGHT X SIGN OFF DATE		DESIGN	BY Y. REN	CHECKED X	PREPARED FOR THE STATE OF CALIFORNIA DEPARTMENT OF TRANSPORTATION	BRIDGE No.	MAR VISTA DRIVE POC PEDESTRIAN RAILING DETAILS No.3								
		DETAILS	BY J. DOTY	CHECKED X		36-0128									
		QUANTITIES	BY X	CHECKED X		POST MILE									
						10.87									
DESIGN DETAIL SHEET (ENGLISH) (REVISION 4/19/2018)		DATE PLOTTED => 11/18/2021 FILE => 30-33_MV_POC_PRD.dwg		TIME PLOTTED => 11:15 AM USERNAME => JVALENZUELA		UNIT: X PROJECT NUMBER & PHASE: 0518000116		CONTRACT No.: 05-0C7331		DISREGARD PRINTS BEARING EARLIER REVISION DATES		REVISION DATES		SHEET OF	
										6-18-21		32		38	

Dist	COUNTY	ROUTE	POST MILES TOTAL PROJECT	SHEET NO.	TOTAL SHEETS
05	Scr	1	10.54/13.44	448	453

DRAFT 65% PLANS

REGISTERED STRUCTURAL ENGINEER DATE

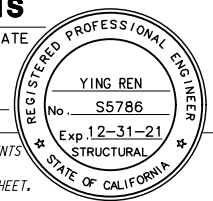


PLANS APPROVAL DATE

THE STATE OF CALIFORNIA OR ITS OFFICERS OR AGENTS
SHALL NOT BE RESPONSIBLE FOR THE ACCURACY OR
COMPLETENESS OF SCANNED COPIES OF THIS PLAN SHEET.


MARK THOMAS
701 UNIVERSITY AVE., SUITE 200
SACRAMENTO, CA 95825

SCCRTC
1523 PACIFIC AVENUE
SANTA CRUZ, CA 95090

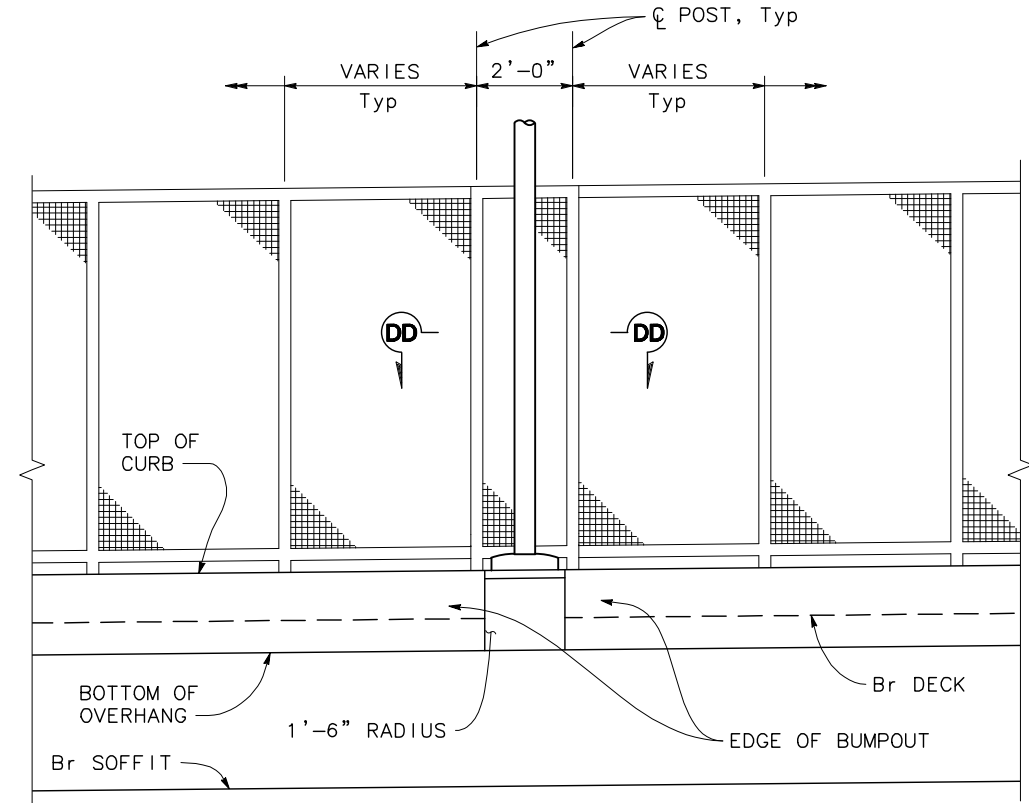


ELEVATION AT ELECTROLIER

1/2"=1'-0"

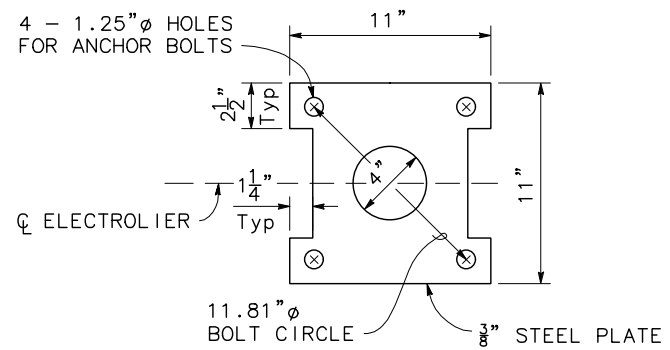

ANCHOR PLATE DETAIL

NO SCALE

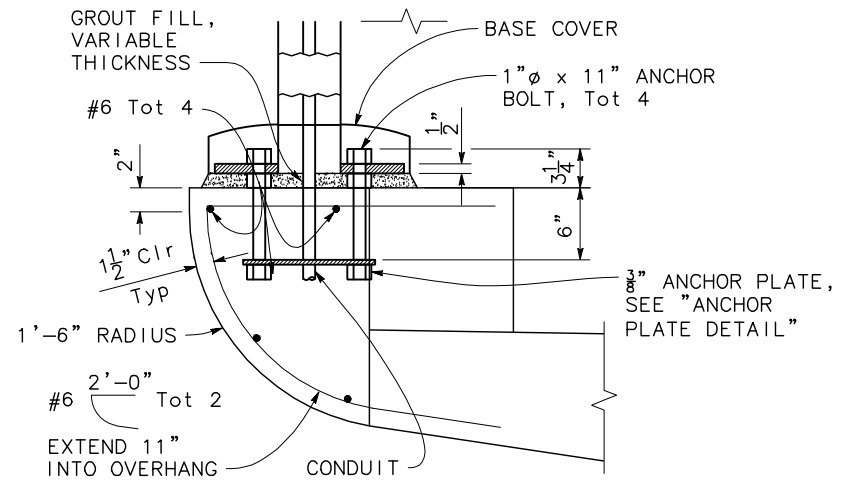


NOTE: Railing not shown for clarity.

SECTION AT CL ELECTROLIER

SECTION EE-EE

1 1/2"=1'-0"

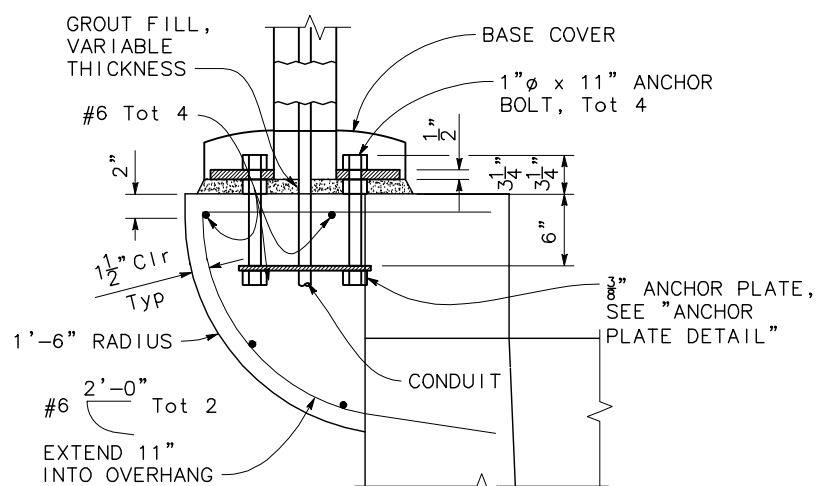


NOTE: Railing not shown for clarity.

SECTION AT CL ELECTROLIER

BUMPOUT DETAILS AT RETAINING WALLS AND BENTS

1 1/2"=1'-0"

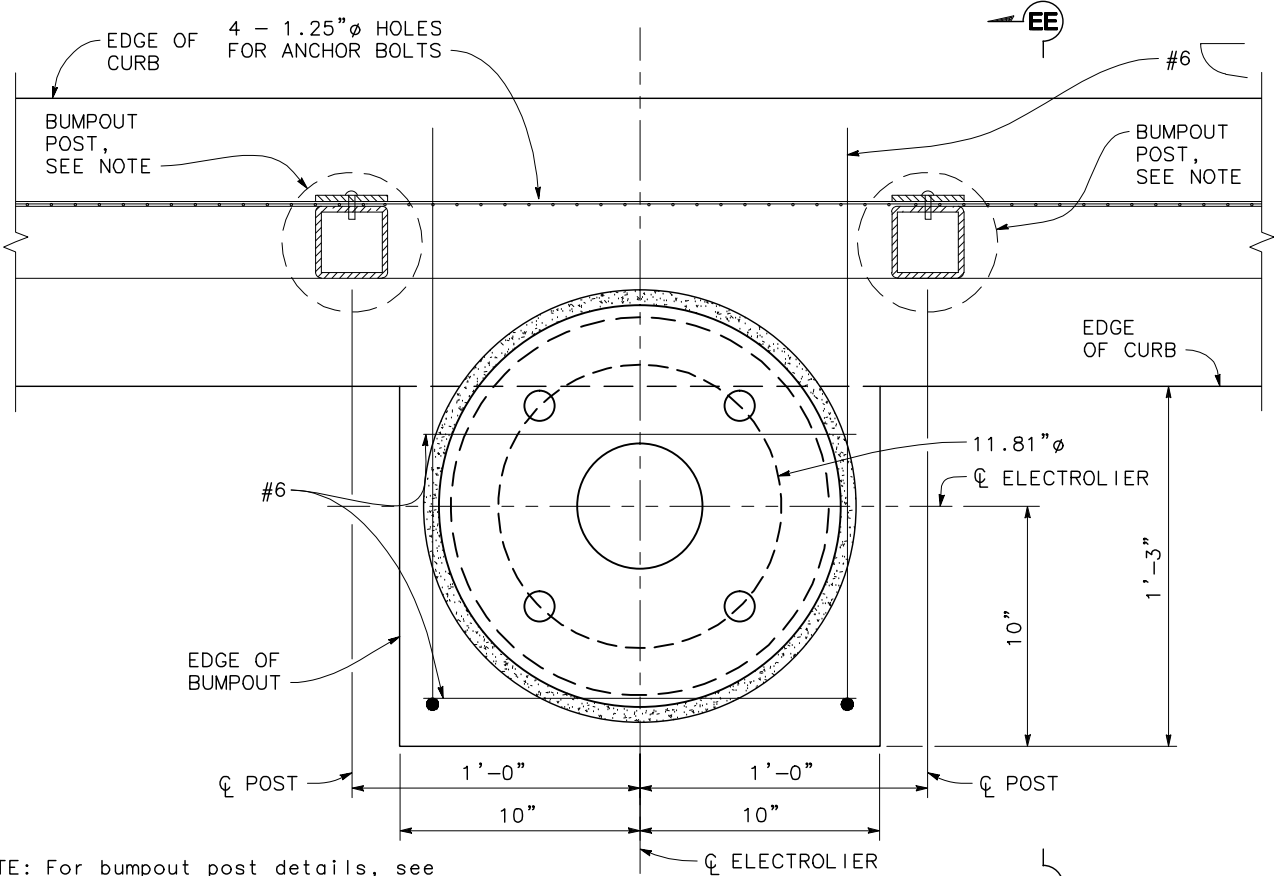

SECTION DD-DD

3"=1'-0"


NOTE: For bumpout post details, see
"TYPICAL POST SECTIONS" on
"PEDESTRIAN RAILING DETAILS
No. 2" sheet.

X DESIGN OVERSIGHT		DESIGN BY Y. REN CHECKED X		DETAILS BY J. DOTY CHECKED X		QUANTITIES BY X CHECKED X		PREPARED FOR THE STATE OF CALIFORNIA DEPARTMENT OF TRANSPORTATION		ERIC FREDRICKSON PROJECT ENGINEER		BRIDGE No. 36-0128		MAR VISTA DRIVE POC	
X SIGN OFF DATE												POST MILE 10.87		PEDESTRIAN RAILING DETAILS No.4	
DESIGN DETAIL SHEET (ENGLISH) (REVISION 4/19/2018)		DATE PLOTTED => 11/18/2021 FILE => 30-33_MV_POC_PRD.dwg		TIME PLOTTED => 11:17 AM USERNAME => JVALENZUELA		ORIGINAL SCALE IN INCHES FOR REDUCED PLANS		0		1		2		3	
								UNIT: X PROJECT NUMBER & PHASE: 0518000116		CONTRACT No.: 05-0C7331		DISREGARD PRINTS BEARING EARLIER REVISION DATES		REVISION DATES 6-18-21	
														SHEET 33	
														OF 38	

Dist	COUNTY	ROUTE	POST MILES TOTAL PROJECT	SHEET NO.	TOTAL SHEETS
05	Scr	1	10.54/13.44	449	453

DRAFT 65% PLANS

REGISTERED STRUCTURAL ENGINEER DATE

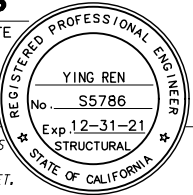


PLANS APPROVAL DATE

THE STATE OF CALIFORNIA OR ITS OFFICERS OR AGENTS
SHALL NOT BE RESPONSIBLE FOR THE ACCURACY OR
COMPLETENESS OF SCANNED COPIES OF THIS PLAN SHEET.


MARK THOMAS
701 UNIVERSITY AVE., SUITE 200
SACRAMENTO, CA 95825

SCCRTC
1523 PACIFIC AVENUE
SANTA CRUZ, CA 95090

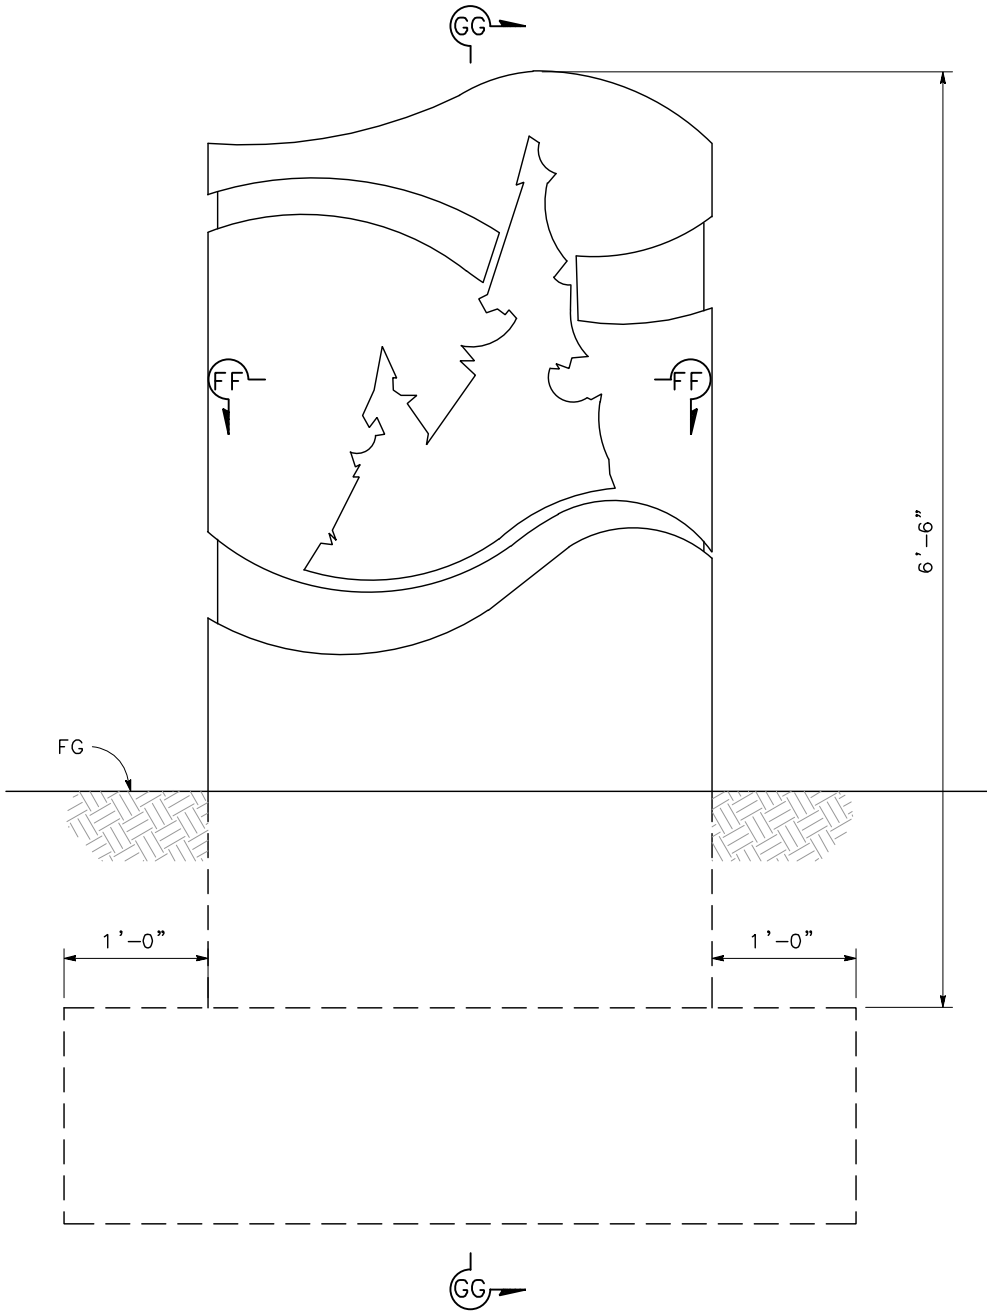


ENTRY MONUMENT

1 1/2" = 1'-0"

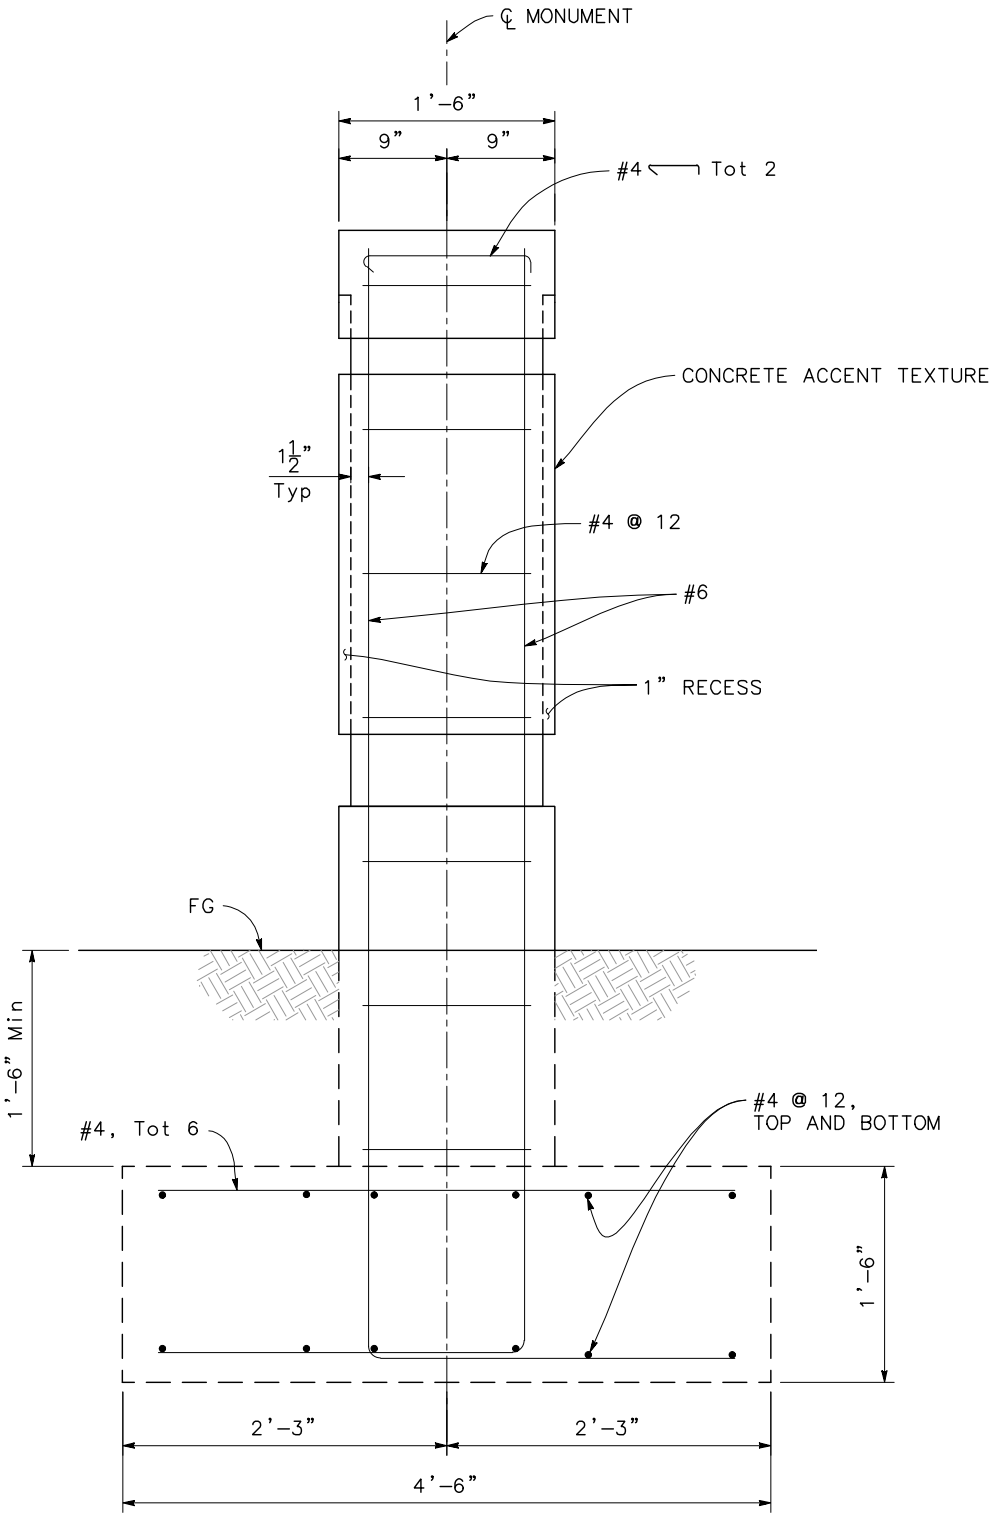

SECTION GG-GG

1 1/2" = 1'-0"

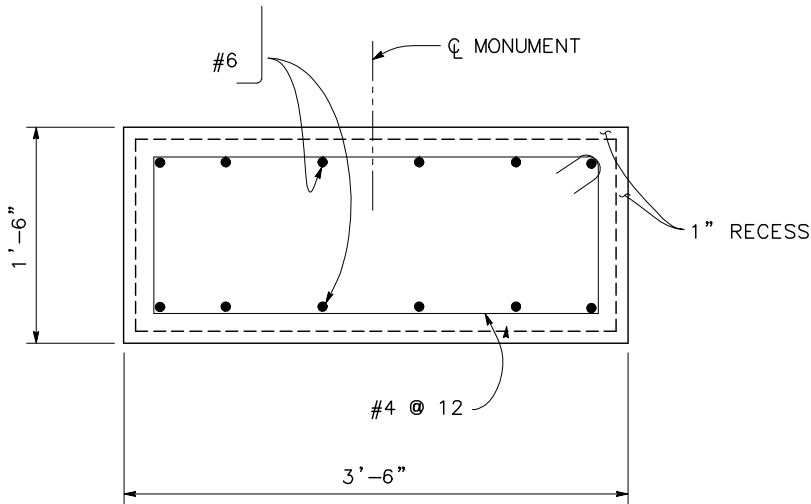

SECTION FF-FF

1 1/2" = 1'-0"

X	DESIGN OVERSIGHT
X	SIGN OFF DATE

DESIGN	BY Y. REN	CHECKED X
DETAILS	BY J. DOTY	CHECKED X
QUANTITIES	BY X	CHECKED X

**PREPARED FOR THE
STATE OF CALIFORNIA
DEPARTMENT OF TRANSPORTATION**

ERIC FREDRICKSON
PROJECT ENGINEER

BRIDGE No.
36-0128
POST MILE
10.87

**MAR VISTA DRIVE POC
ENTRY MONUMENT DETAILS**

DESIGN DETAIL SHEET
(ENGLISH) (REVISION 4/19/2018)

DATE PLOTTED => 11/18/2021
FILE => 34_MV_POC_EMD.dwg

TIME PLOTTED => 11:19 AM
USERNAME => JVALENZUELA
ORIGINAL SCALE
IN INCHES FOR
REDUCED PLANS

0 1 2 3

UNIT: X
PROJECT NUMBER & PHASE: 0518000116

CONTRACT No.: 05-OC7331

DISREGARD PRINTS BEARING
EARLIER REVISION DATES

REVISION DATES	SHEET	OF
6-18-21	34	38

DIST	COUNTY	ROUTE	POST MILES TOTAL PROJECT	SHEET NO.	TOTAL SHEETS
05	SCR	1	10.54/13.44	450	453

DRAFT 65% PLANS


REGISTERED STRUCTURAL ENGINEER DATE

PLANS APPROVAL DATE


THE STATE OF CALIFORNIA OR ITS OFFICERS OR AGENTS
SHALL NOT BE RESPONSIBLE FOR THE ACCURACY OR
COMPLETENESS OF SCANNED COPIES OF THIS PLAN SHEET.

MARK THOMAS
701 UNIVERSITY AVE., SUITE 200
SACRAMENTO, CA 95825


SCCRTC
1523 PACIFIC AVENUE
SANTA CRUZ, CA 95090

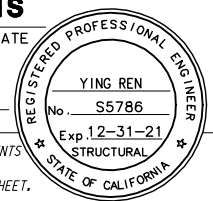

- NOTES:
1. Whale cutouts to be placed outside the electrolier bumpout regions.
 2. For cutout mounting details, see "PEDESTRIAN RAILING DETAILS No. 3" sheet.
 3. All dimensions shown are measured to the center of the whale cutouts.

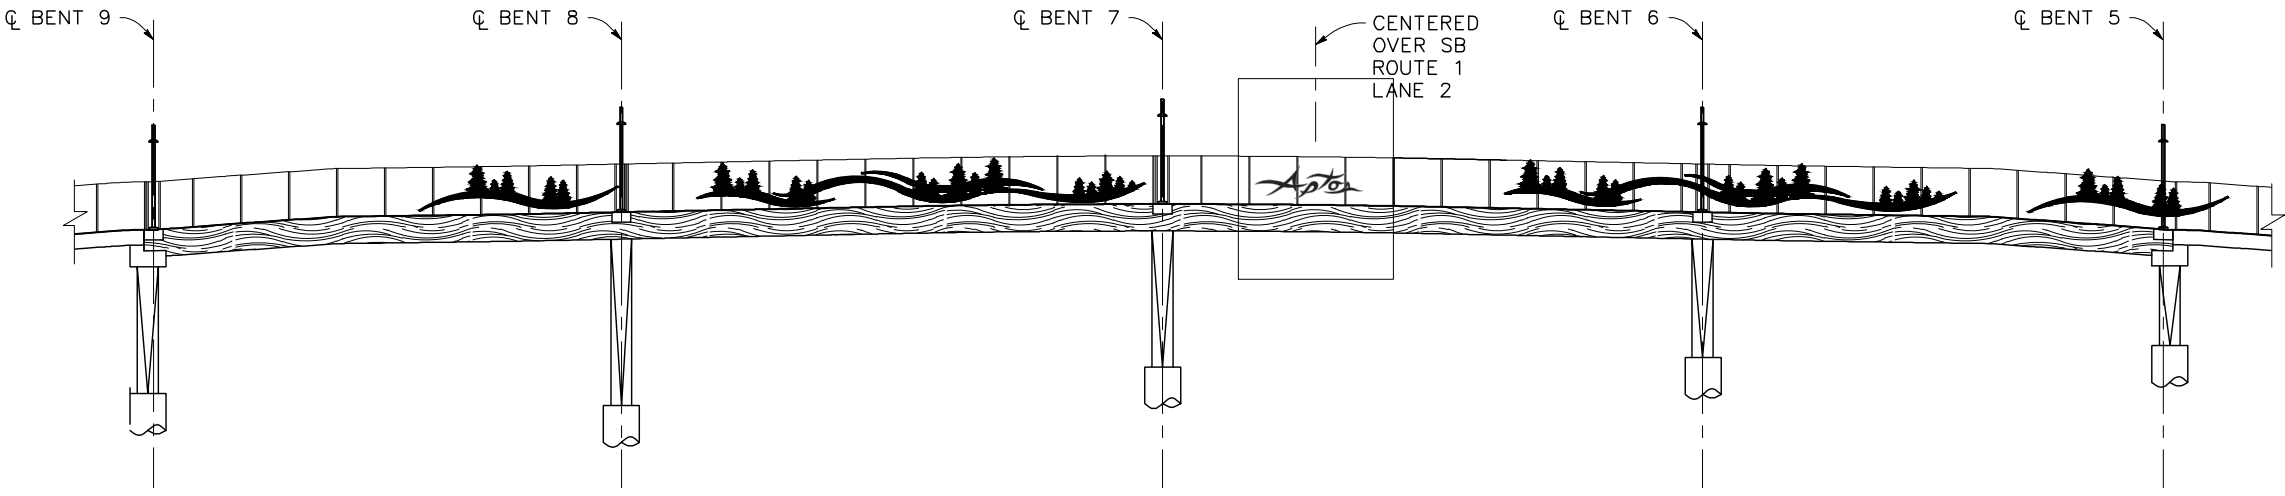

ELEVATION - SB FACING RAILING
NO SCALE

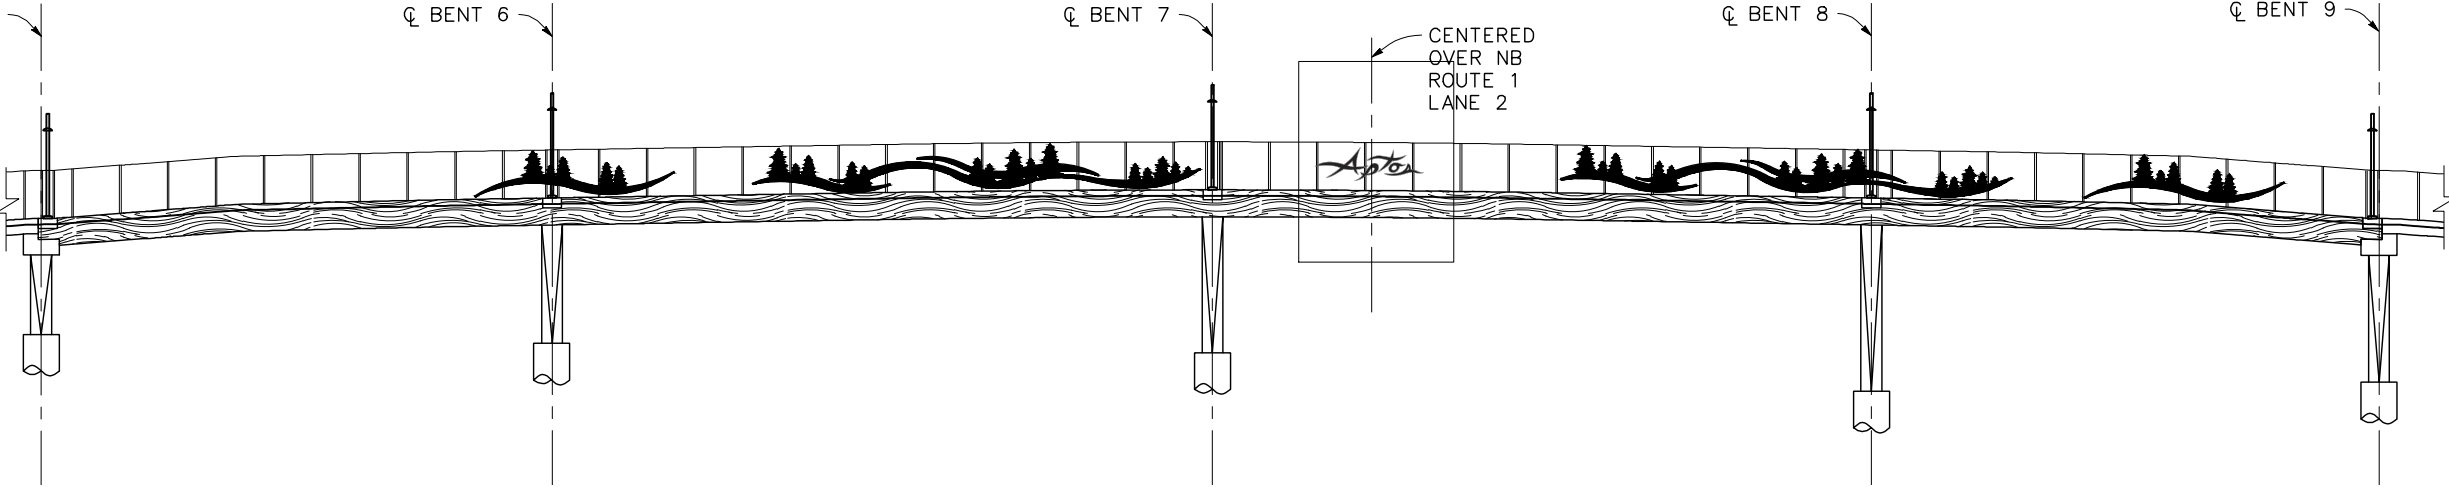


ELEVATION - NB FACING RAILING
NO SCALE

X DESIGN OVERSIGHT X SIGN OFF DATE	DESIGN BY Y. REN CHECKED X DETAILS BY J. DOTY CHECKED X QUANTITIES BY X CHECKED X	PREPARED FOR THE STATE OF CALIFORNIA DEPARTMENT OF TRANSPORTATION	ERIC FREDRICKSON PROJECT ENGINEER	BRIDGE No. 36-0128	MAR VISTA DRIVE POC REDWOOD CUTOUT LAYOUT					
				POST MILE 10.87						
DESIGN DETAIL SHEET (ENGLISH) (REVISION 4/19/2018)	DATE PLOTTED => 11/15/2021 FILE => 35-36_MV_POC_RFC.dwg	TIME PLOTTED => 2:02 PM USERNAME => JDOTY	ORIGINAL SCALE IN INCHES FOR REDUCED PLANS	0 1 2 3	UNIT: X PROJECT NUMBER & PHASE: 0518000116	CONTRACT No.: 05-0C7331	DISREGARD PRINTS BEARING EARLIER REVISION DATES	REVISION DATES 6-18-21	SHEET 35	OF 38

Dist	COUNTY	ROUTE	POST MILES TOTAL PROJECT	SHEET No.	TOTAL SHEETS
05	Scr	1	10.54/13.44	451	453

DRAFT 65% PLANS

REGISTERED STRUCTURAL ENGINEER DATE

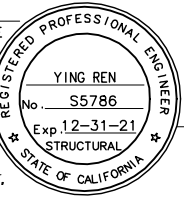


PLANS APPROVAL DATE

THE STATE OF CALIFORNIA OR ITS OFFICERS OR AGENTS
SHALL NOT BE RESPONSIBLE FOR THE ACCURACY OR
COMPLETENESS OF SCANNED COPIES OF THIS PLAN SHEET.


MARK THOMAS
701 UNIVERSITY AVE., SUITE 200
SACRAMENTO, CA 95825

SCCRTC
1523 PACIFIC AVENUE
SANTA CRUZ, CA 95090


- NOTES: 1. All cutouts to be powder-coated black (FED-STD-595 No. 17038).
2. All cutouts to be 3/8" aluminum.
3. See project specifications for more information on powder coating and whale cutout material requirements.
4. For cutout mounting details, see "PEDESTRIAN RAILING DETAILS No. 3" sheet.

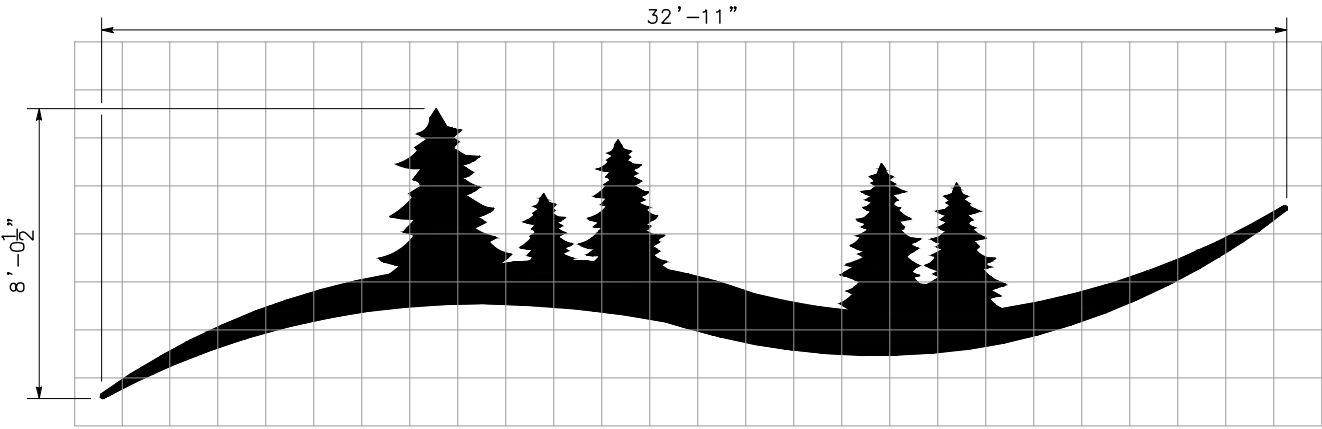


CUTOUT "A"
3/8" = 1'-0"

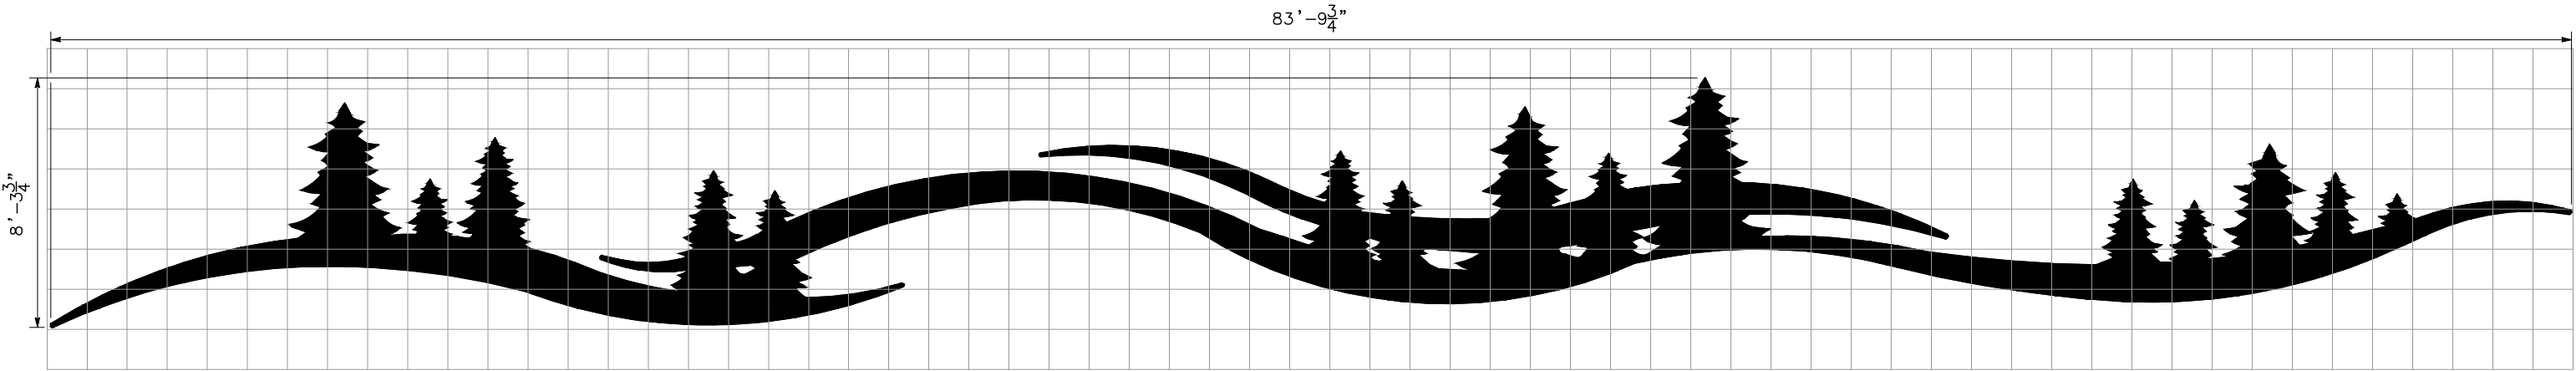


CUTOUT "B"
3/8" = 1'-0"

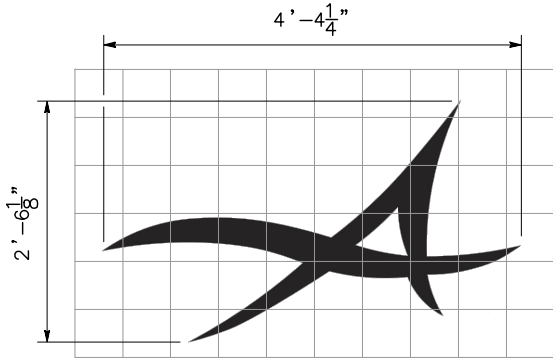


CUTOUT "C"
1/2" = 1'-0"

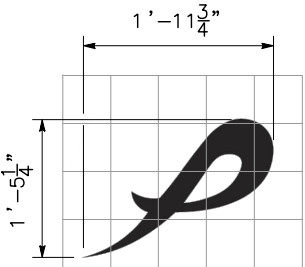


CUTOUT "D"
1/2" = 1'-0"

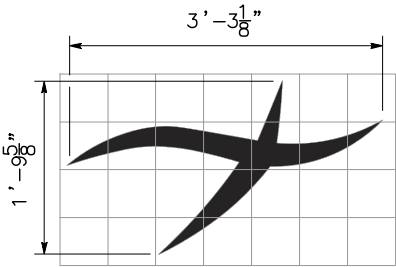

CUTOUT "E"
1/2" = 1'-0"

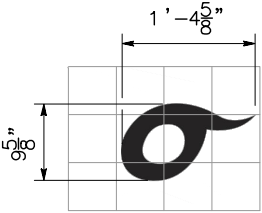

CUTOUT "F"
1/2" = 1'-0"

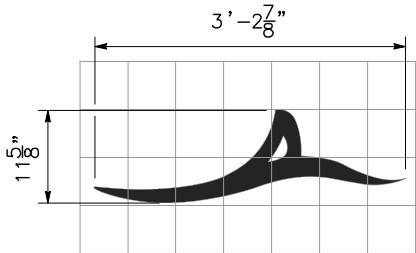

CUTOUT "G"
1/2" = 1'-0"

X
DESIGN OVERSIGHT

X
SIGN OFF DATE

DESIGN BY Y. REN
DETAILS BY J. DOTY
QUANTITIES BY X

CHECKED X
CHECKED X
CHECKED X

PREPARED FOR THE
STATE OF CALIFORNIA
DEPARTMENT OF TRANSPORTATION

ERIC FREDRICKSON
PROJECT ENGINEER

BRIDGE No.
36-0128
POST MILE
10.87

MAR VISTA DRIVE POC
REDWOOD CUTOUT DETAILS

DESIGN DETAIL SHEET
(ENGLISH) (REVISION 4/19/2018)

DATE PLOTTED => 11/15/2021
FILE => 35-36_MV_POC_RFC.dwg

TIME PLOTTED => 2:41 PM
USERNAME => JDOTY

ORIGINAL SCALE
IN INCHES FOR
REDUCED PLANS

0 1 2 3

UNIT: X
PROJECT NUMBER & PHASE: 0518000116

CONTRACT No.: 05-0C7331

DISREGARD PRINTS BEARING
EARLIER REVISION DATES

REVISION DATES
6-18-21

SHEET
38
OF
38

Dist	COUNTY	ROUTE	POST MILES TOTAL PROJECT	SHEET No.	TOTAL SHEETS
05	Scr	1	10.54/13.44		453

DRAFT 65% PLANS



REGISTERED STRUCTURAL ENGINEER DATE

PLANS APPROVAL DATE

THE STATE OF CALIFORNIA OR ITS OFFICERS OR AGENTS
SHALL NOT BE RESPONSIBLE FOR THE ACCURACY OR
COMPLETENESS OF SCANNED COPIES OF THIS PLAN SHEET.


MARK THOMAS
701 UNIVERSITY AVE., SUITE 200
SACRAMENTO, CA 95825

SCCRTC
1523 PACIFIC AVENUE
SANTA CRUZ, CA 95090

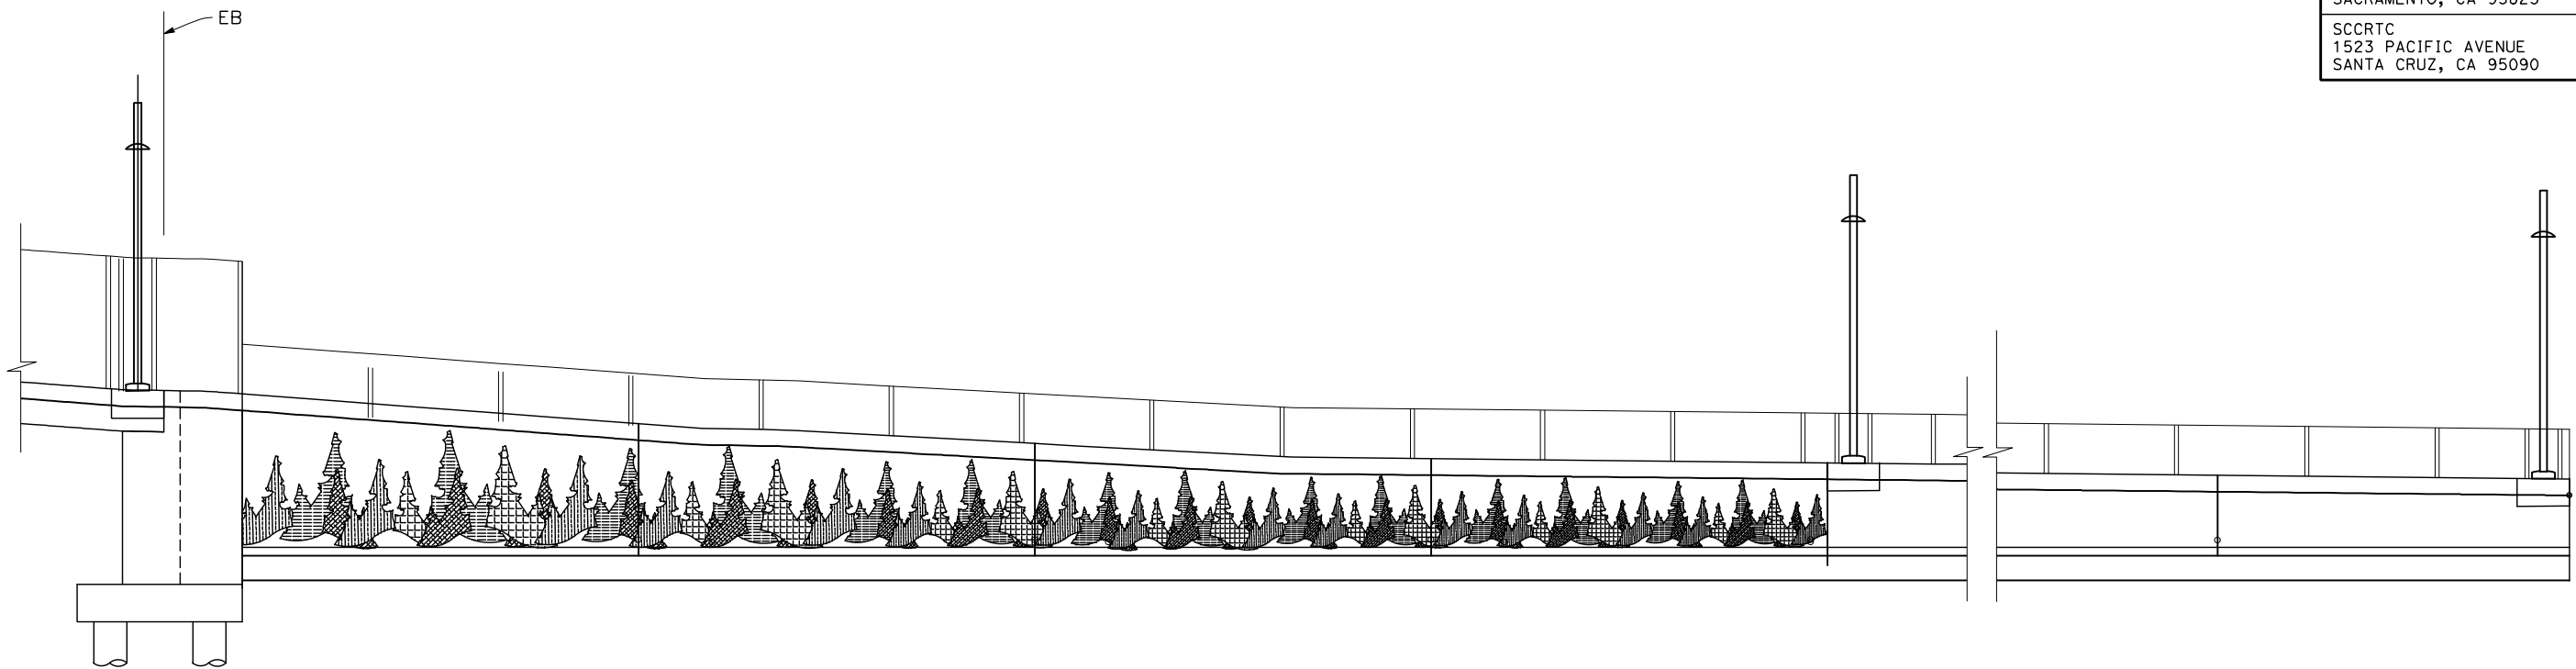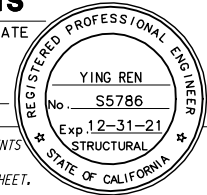

RW "N" AT RIGHT EDGE OF DECK - EB

3/16"=1'-0"

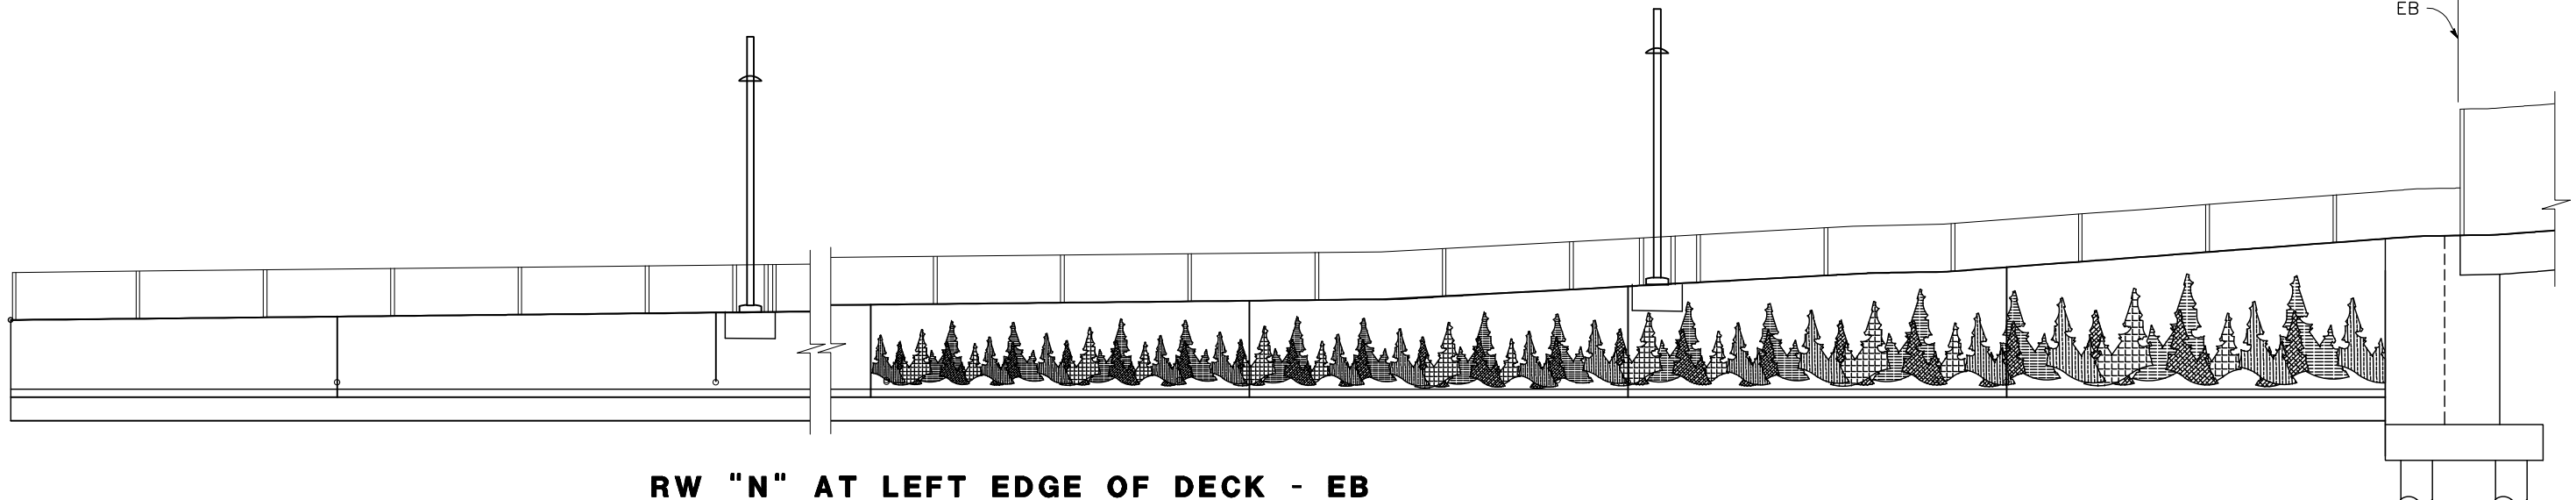

RW "N" AT LEFT EDGE OF DECK - EB

3/16"=1'-0"

X
DESIGN OVERSIGHT
X
SIGN OFF DATE

DESIGN	BY Y. REN	CHECKED X
DETAILS	BY J. DOTY	CHECKED X
QUANTITIES	BY X	CHECKED X

PREPARED FOR THE
STATE OF CALIFORNIA
DEPARTMENT OF TRANSPORTATION

ERIC FREDRICKSON
PROJECT ENGINEER

BRIDGE No.	36-0128
POST MILE	10.87

MAR VISTA DRIVE POC
RETAINING WALL "N" AESTHETIC TREATMENT

DESIGN DETAIL SHEET
(ENGLISH) (REVISION 4/19/2018)

DATE PLOTTED => 11/15/2021
FILE => 35-36_MV_POC_PL.dwg

TIME PLOTTED => 11:03 AM
USERNAME => JDOTY

ORIGINAL SCALE
IN INCHES FOR
REDUCED PLANS

0 1 2 3

UNIT: X
PROJECT NUMBER & PHASE: 0518000116

CONTRACT No.: 05-0C7331

DISREGARD PRINTS BEARING
EARLIER REVISION DATES

REVISION DATES	SHEET	OF
6-18-21	35	38

Dist	COUNTY	ROUTE	POST MILES TOTAL PROJECT	SHEET NO.	TOTAL SHEETS
05	Scr	1	10.54/13.44		453

DRAFT 65% PLANS



REGISTERED STRUCTURAL ENGINEER DATE

PLANS APPROVAL DATE

THE STATE OF CALIFORNIA OR ITS OFFICERS OR AGENTS
SHALL NOT BE RESPONSIBLE FOR THE ACCURACY OR
COMPLETENESS OF SCANNED COPIES OF THIS PLAN SHEET.


MARK THOMAS
701 UNIVERSITY AVE., SUITE 200
SACRAMENTO, CA 95825

SCCRTC
1523 PACIFIC AVENUE
SANTA CRUZ, CA 95090

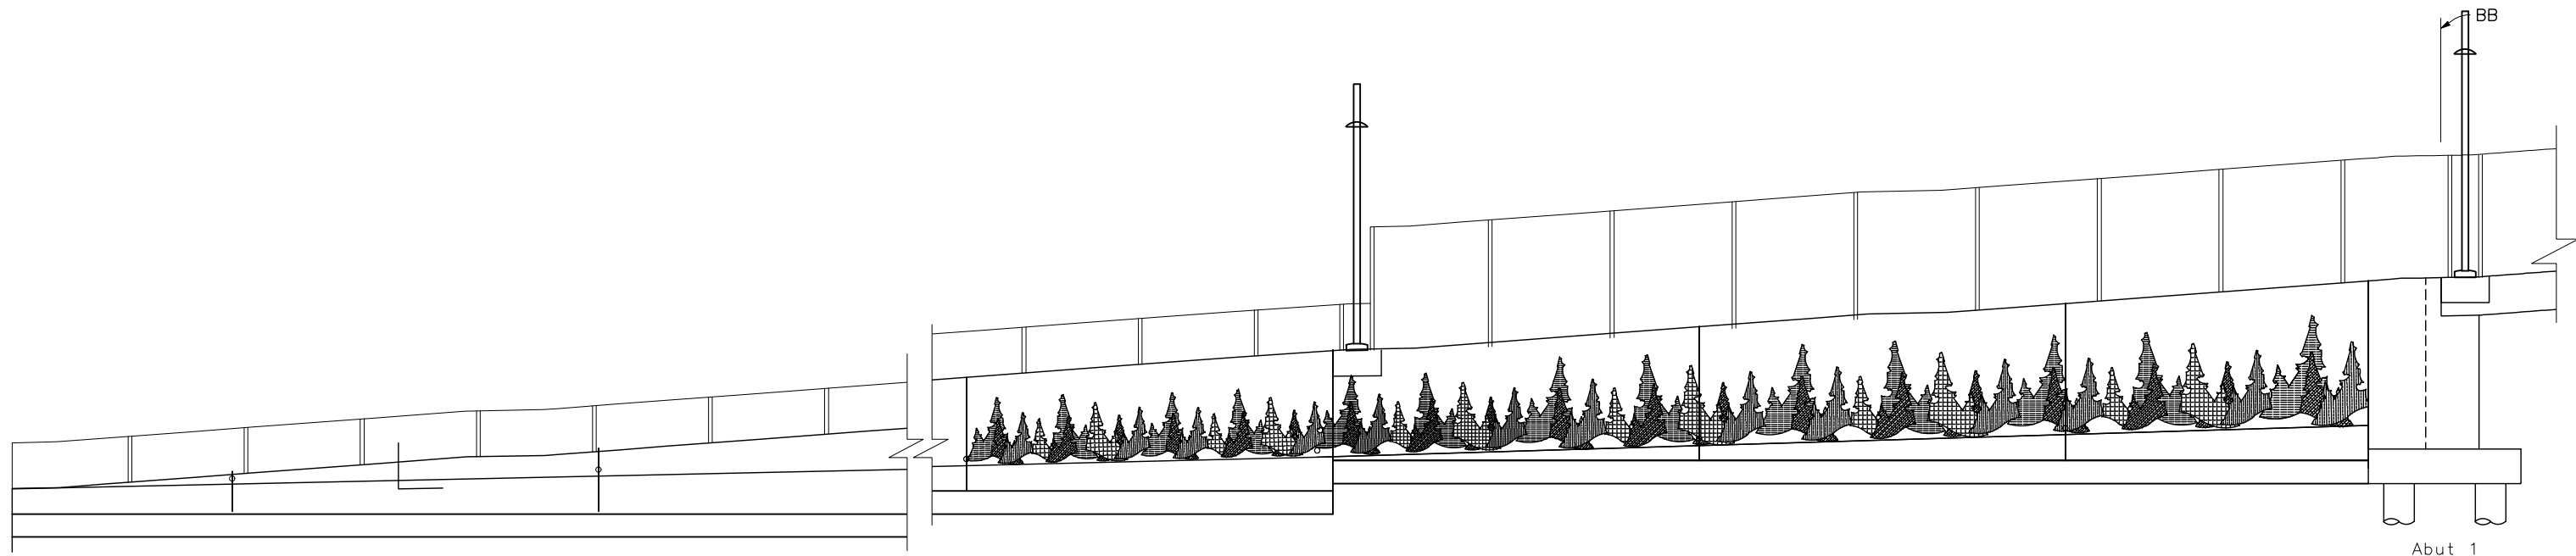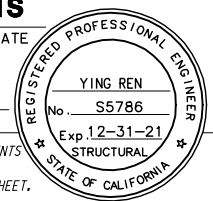

RW "S" AT RIGHT EDGE OF DECK - BB

3/16"=1'-0"

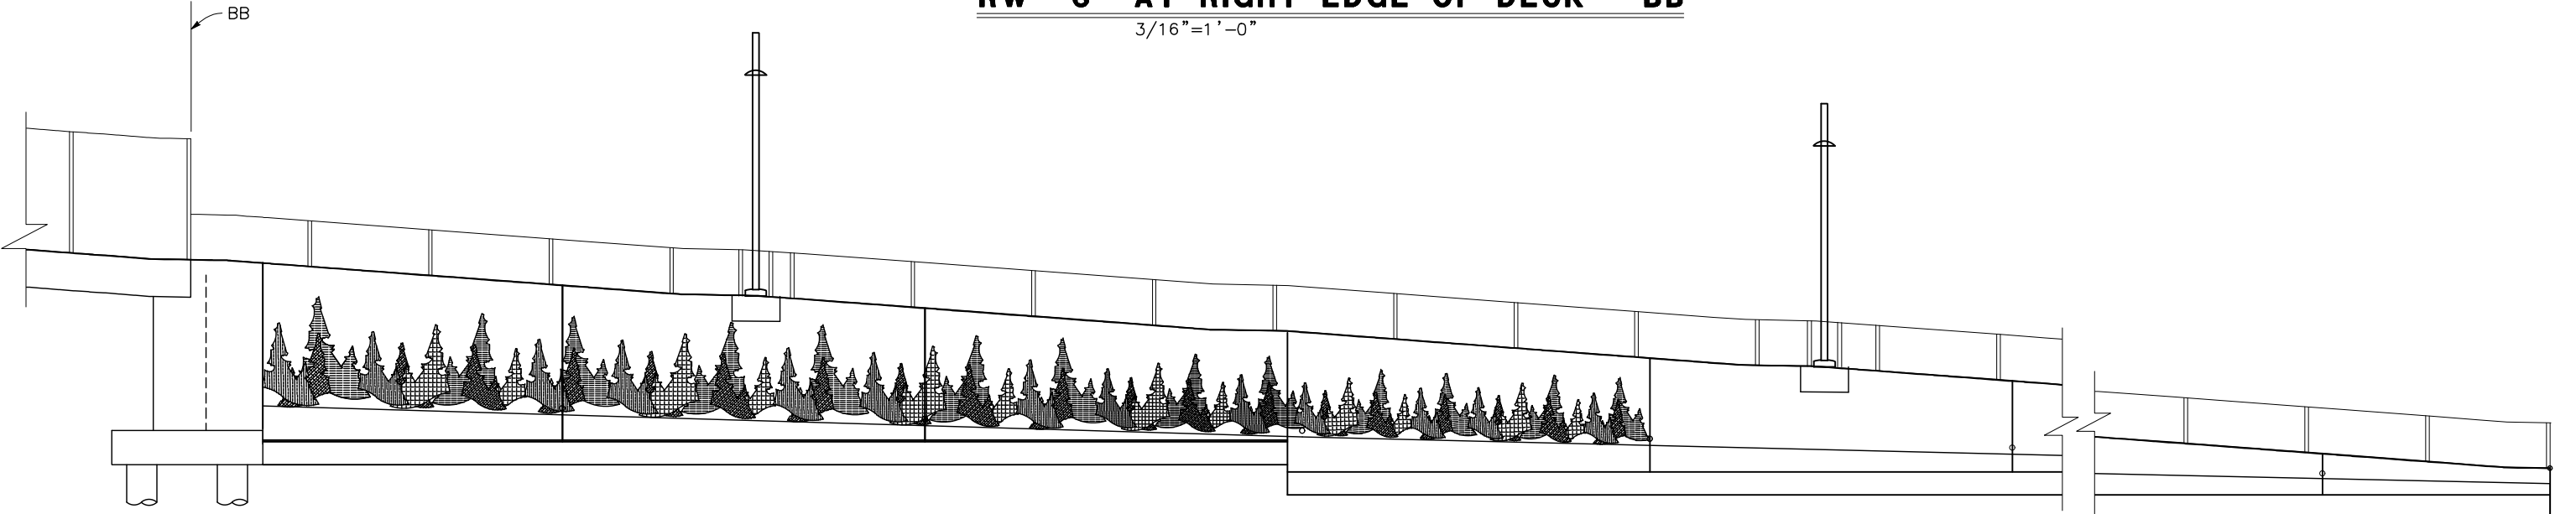

RW "S" AT LEFT EDGE OF DECK - BB

3/16"=1'-0"

X DESIGN OVERSIGHT X SIGN OFF DATE	DESIGN BY Y. REN DETAILS BY J. DOTY QUANTITIES BY X	CHECKED X X X	PREPARED FOR THE STATE OF CALIFORNIA DEPARTMENT OF TRANSPORTATION	ERIC FREDRICKSON PROJECT ENGINEER	BRIDGE No. 36-0128	MAR VISTA DRIVE POC RETAINING WALL "S" AESTHETIC TREATMENT				
					POST MILE 10.87					
DESIGN DETAIL SHEET (ENGLISH) (REVISION 4/19/2018)	DATE PLOTTED => 11/15/2021 FILE => 35-36_MV_POC_PL.dwg	TIME PLOTTED => 10:59 AM USERNAME => JDOTY	ORIGINAL SCALE IN INCHES FOR REDUCED PLANS	0 1 2 3	UNIT: X PROJECT NUMBER & PHASE: 0518000116	CONTRACT No.: 05-OC7331	DISREGARD PRINTS BEARING EARLIER REVISION DATES	REVISION DATES 6-18-21	SHEET 38	OF 38

Dist	COUNTY	ROUTE	POST MILES TOTAL PROJECT	SHEET No.	TOTAL SHEETS
05	Scr	1	10.54/13.44		453

DRAFT 65% PLANS



REGISTERED STRUCTURAL ENGINEER DATE

PLANS APPROVAL DATE

THE STATE OF CALIFORNIA OR ITS OFFICERS OR AGENTS
SHALL NOT BE RESPONSIBLE FOR THE ACCURACY OR
COMPLETENESS OF SCANNED COPIES OF THIS PLAN SHEET.

MARK THOMAS
701 UNIVERSITY AVE., SUITE 200
SACRAMENTO, CA 95825

SCCRTC
1523 PACIFIC AVENUE
SANTA CRUZ, CA 95090

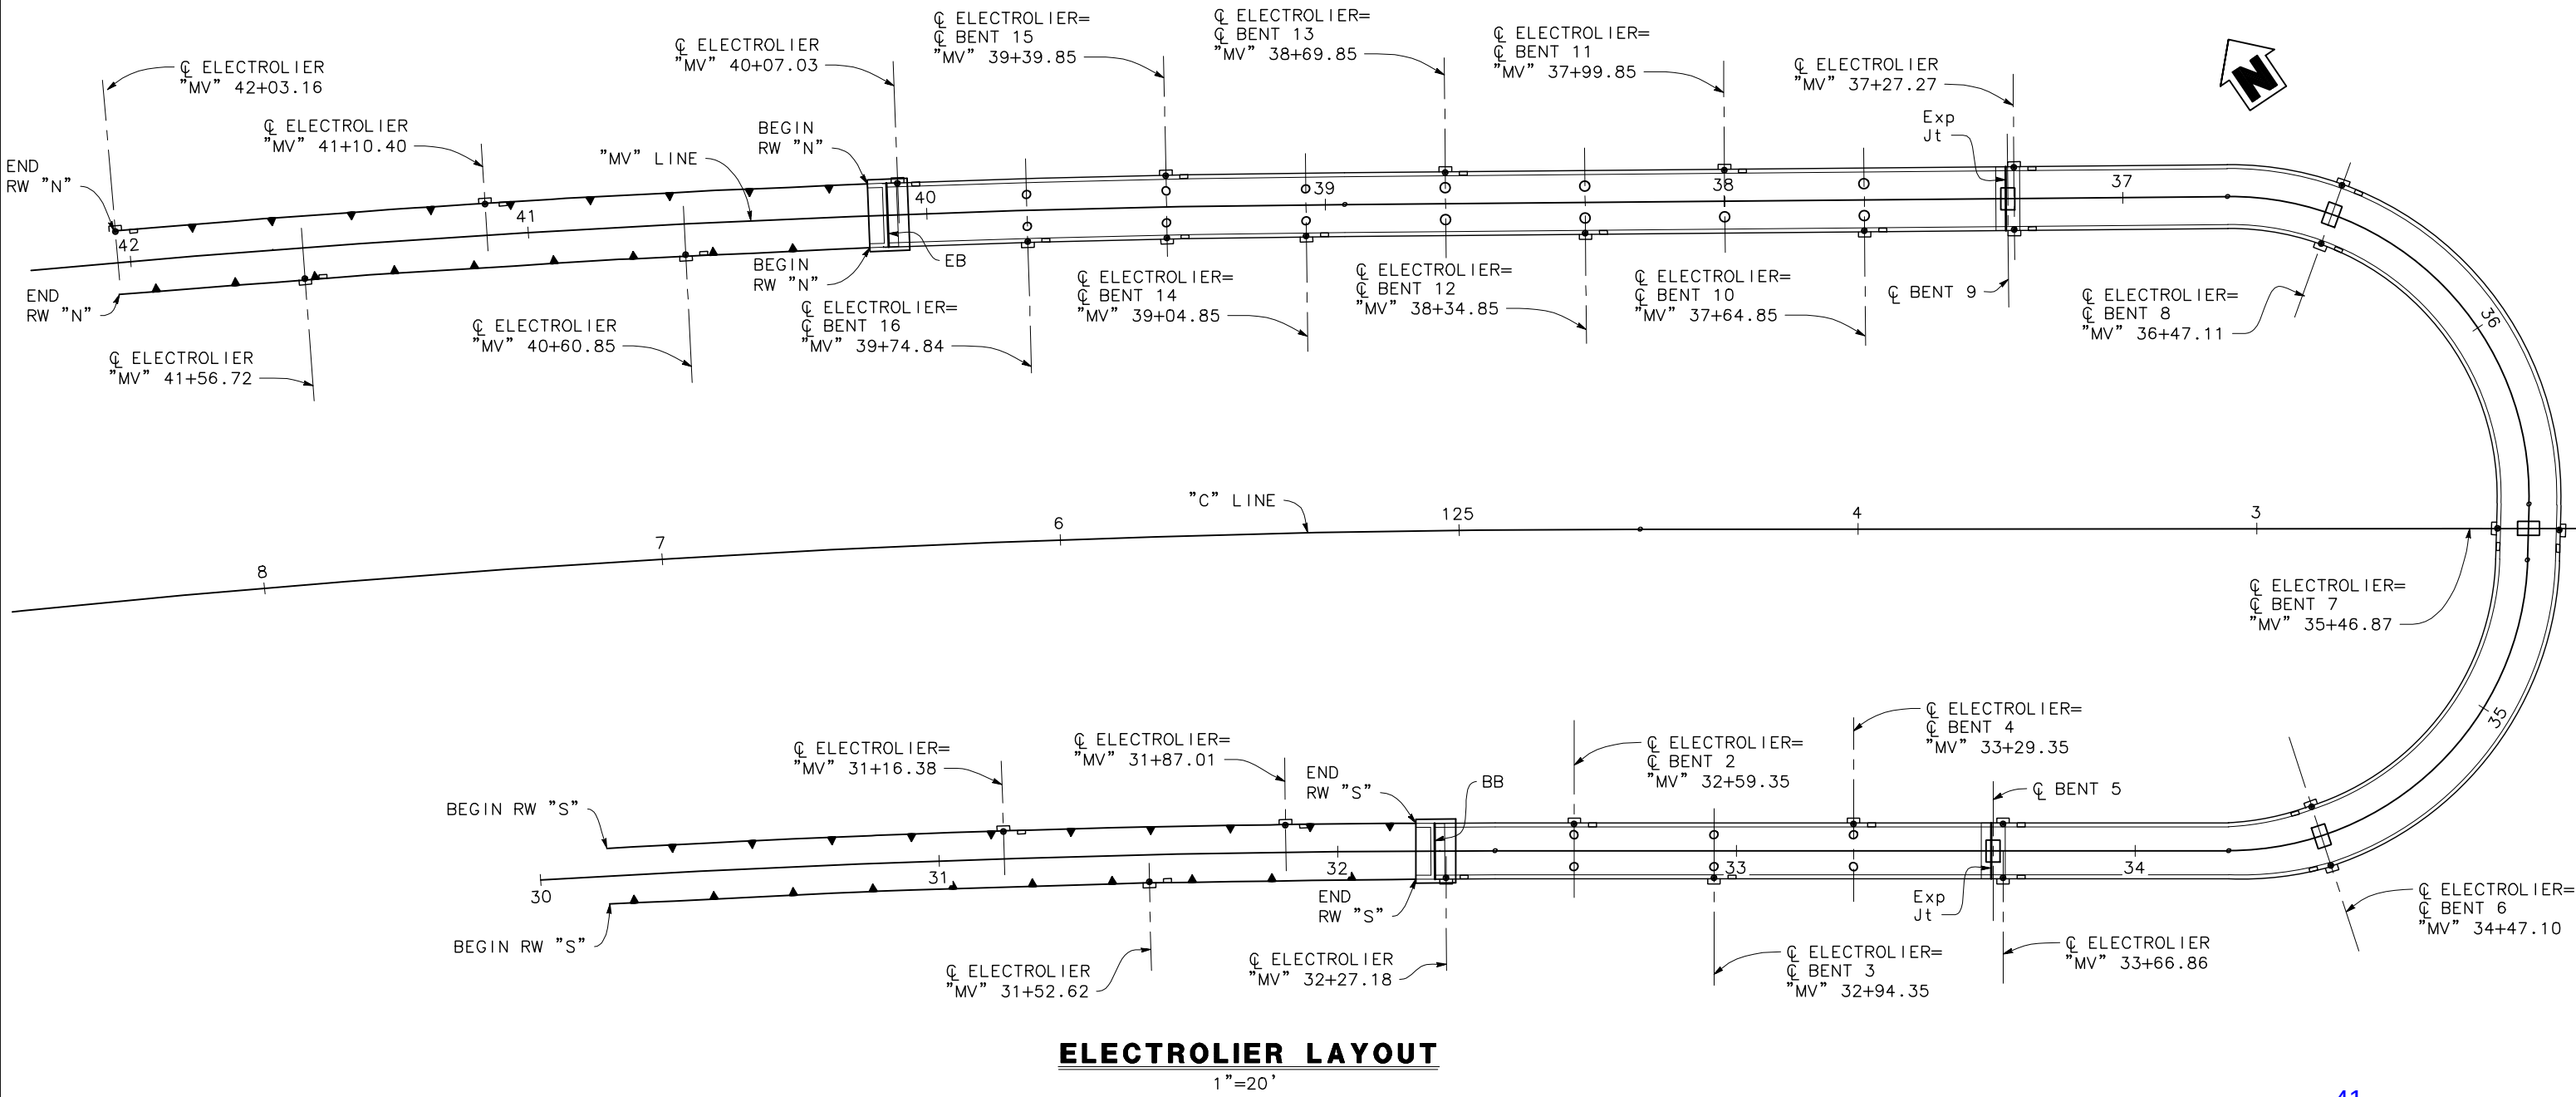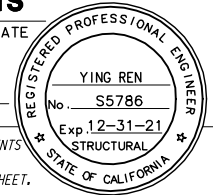

41

X
DESIGN OVERSIGHT
X
SIGN OFF DATE

DESIGN	BY Y. REN	CHECKED X
DETAILS	BY J. DOTY	CHECKED X
QUANTITIES	BY X	CHECKED X

PREPARED FOR THE
STATE OF CALIFORNIA
DEPARTMENT OF TRANSPORTATION

ERIC FREDRICKSON
PROJECT ENGINEER

BRIDGE No.
36-0128
POST MILE
10.87

MAR VISTA DRIVE POC
ELECTROLIER LAYOUT

DESIGN DETAIL SHEET
(ENGLISH) (REVISION 4/19/2018)

DATE PLOTTED => 11/15/2021
FILE => 39_MV_POC_EL.dwg

TIME PLOTTED => 9:31 AM
USERNAME => JDOTY

ORIGINAL SCALE
IN INCHES FOR
REDUCED PLANS

0 1 2 3

UNIT: X
PROJECT NUMBER & PHASE: 0518000116

CONTRACT No.: 05-0C7331

DISREGARD PRINTS BEARING
EARLIER REVISION DATES

REVISION DATES	SHEET	OF
6-18-21	39	38


NOTES:

STANDARD PENETRATION TEST SAMPLER: I.D. = 1.4"; O.D. = 2"
MODIFIED CALIFORNIA SAMPLER: I.D. = 2.5"; O.D. = 3"
HAMMER ASSEMBLY: A 140 LB HAMMER WITH
A 30" DROP (AUTOMATIC HAMMER)

THIS LOTB SHEET WAS PREPARED IN ACCORDANCE WITH THE
CALTRANS SOIL & ROCK, LOGGING, CLASSIFICATION, AND
PRESENTATION MANUAL (2010)

SEE CALTRANS 2018 STANDARD PLANS A10F, A10G FOR SOIL
LEGEND.

ALL DIMENSIONS ARE IN FEET UNLESS OTHERWISE SHOWN

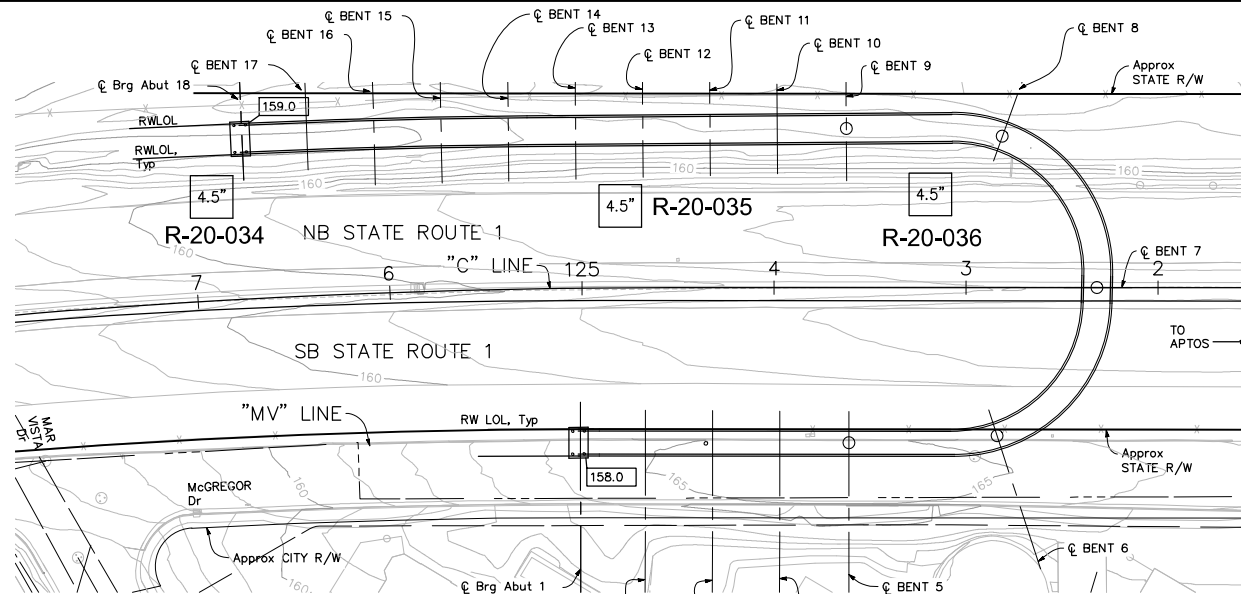

DRAFT

DIST	COUNTY	ROUTE	POST MILES TOTAL PROJECT	SHEET No	TOTAL SHEETS
05	SCr	1	10.54/13.44	452	453

REGISTERED STRUCTURAL ENGINEER	DATE
PLANS APPROVAL DATE	


The State of California or its officers or agents
shall not be responsible for the accuracy or
completeness of scanned copies of this plan sheet.

SCCRTC
1523 PACIFIC AVENUE
SANTA CRUZ, CA 95090

PARIKH CONSULTANTS, INC.
1497 N MILPITAS BLVD.
MILPITAS, CA 95035

BOREHOLE LOCATION TABLE

Hole ID	Alignment Name	Station and Offset
R-20-034	"C" Line	126+90 54' Rt.
R-20-035	"C" Line	124+80 43' Rt.
R-20-036	"C" Line	123+19 49' Rt.

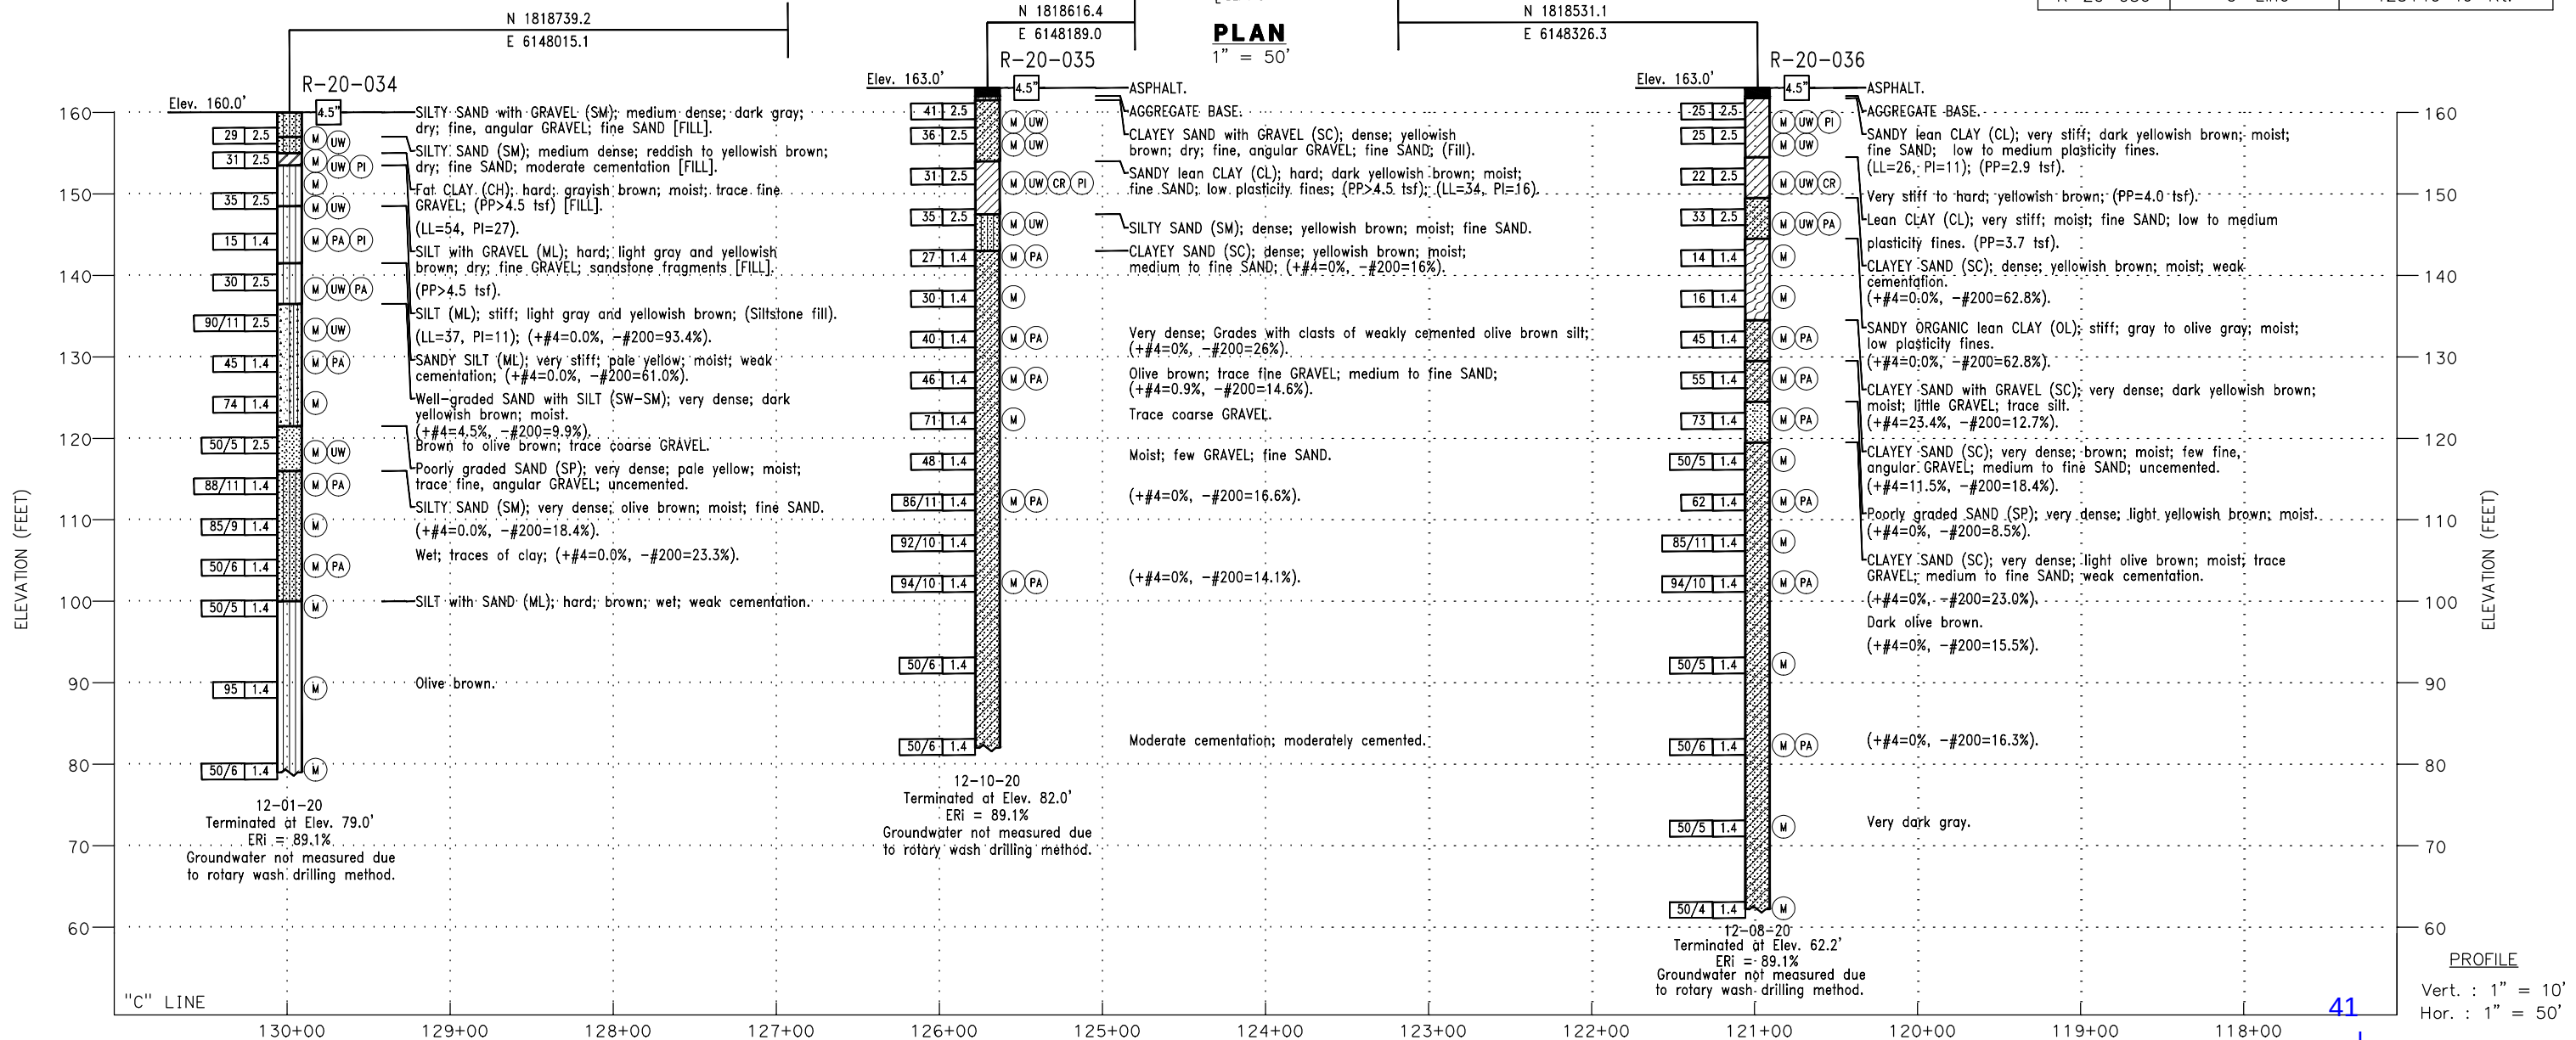

GEOTECHNICAL PROFESSIONAL APPROVAL DATE

SCALE: AS SHOWN	VERT.DATUM X	HORZ.DATUM X
PHOTOGRAMMETRY AS OF: X	ALIGNMENT TIES X	
SURVEYED BY X	DRAFTED BY K. OUYANG	
SIGN OFF DATE	FIELD CHECKED BY X	CHECKED BY G. PARIKH

DESIGN BY K. ADHIKARI	CHECKED
DETAILS BY	CHECKED
QUANTITIES BY	CHECKED

PREPARED FOR THE
STATE OF CALIFORNIA
DEPARTMENT OF TRANSPORTATION

K. SARAVANAPAVAN	BRIDGE NO.
PROJECT ENGINEER	36-0128
	POST MILES
	10.87

MAR VISTA DRIVE POC
LOG OF TEST BORINGS 1 OF 2

FOUNDATION PLAN SHEET (ENGLISH) (REV. 03/14/12)

ORIGINAL SCALE IN INCHES
FOR REDUCED PLANS

UNIT: X
PROJECT NUMBER & PHASE: 0518000116
CONTRACT NO.: 05-0C7331

DISREGARD PRINTS BEARING
EARLIER REVISION DATES

REVISION DATES	SHEET	OF
	37	38

TIME PLOTTED => 7:20 PM
USERNAME => SUGHERIA DATE PLOTTED => 14-Jun-21


STANDARD PENETRATION TEST SAMPLER: I.D. = 1.4"; O.D. = 2"
MODIFIED CALIFORNIA SAMPLER: I.D. = 2.5"; O.D. = 3"
HAMMER ASSEMBLY: A 140 LB HAMMER WITH
A 30" DROP (AUTOMATIC HAMMER)

SEE CALTRANS 2018 STANDARD PLANS A10F, A10G FOR SOIL
LEGEND.

ALL DIMENSIONS ARE IN FEET UNLESS OTHERWISE SHOWN



DRAFT

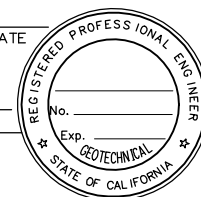
REGISTERED STRUCTURAL ENGINEER DATE _____

The State of California or its officers or agents shall not be responsible for the accuracy or completeness of scanned copies of this plan sheet

SCCRTC
1523 PACIFIC AVENUE
SANTA CRUZ, CA 95090

PARIKH CONSULTANTS, INC.
1497 N MILPITAS BLVD.
MILPITAS, CA 95035

Hole ID	Alignment Name	Station and Offset
R-20-037	"C" Line	123+25 88' Lt.
R-20-038	"C" Line	125+39 87' Lt.
R-20-039	"C" Line	127+47 86' Lt.

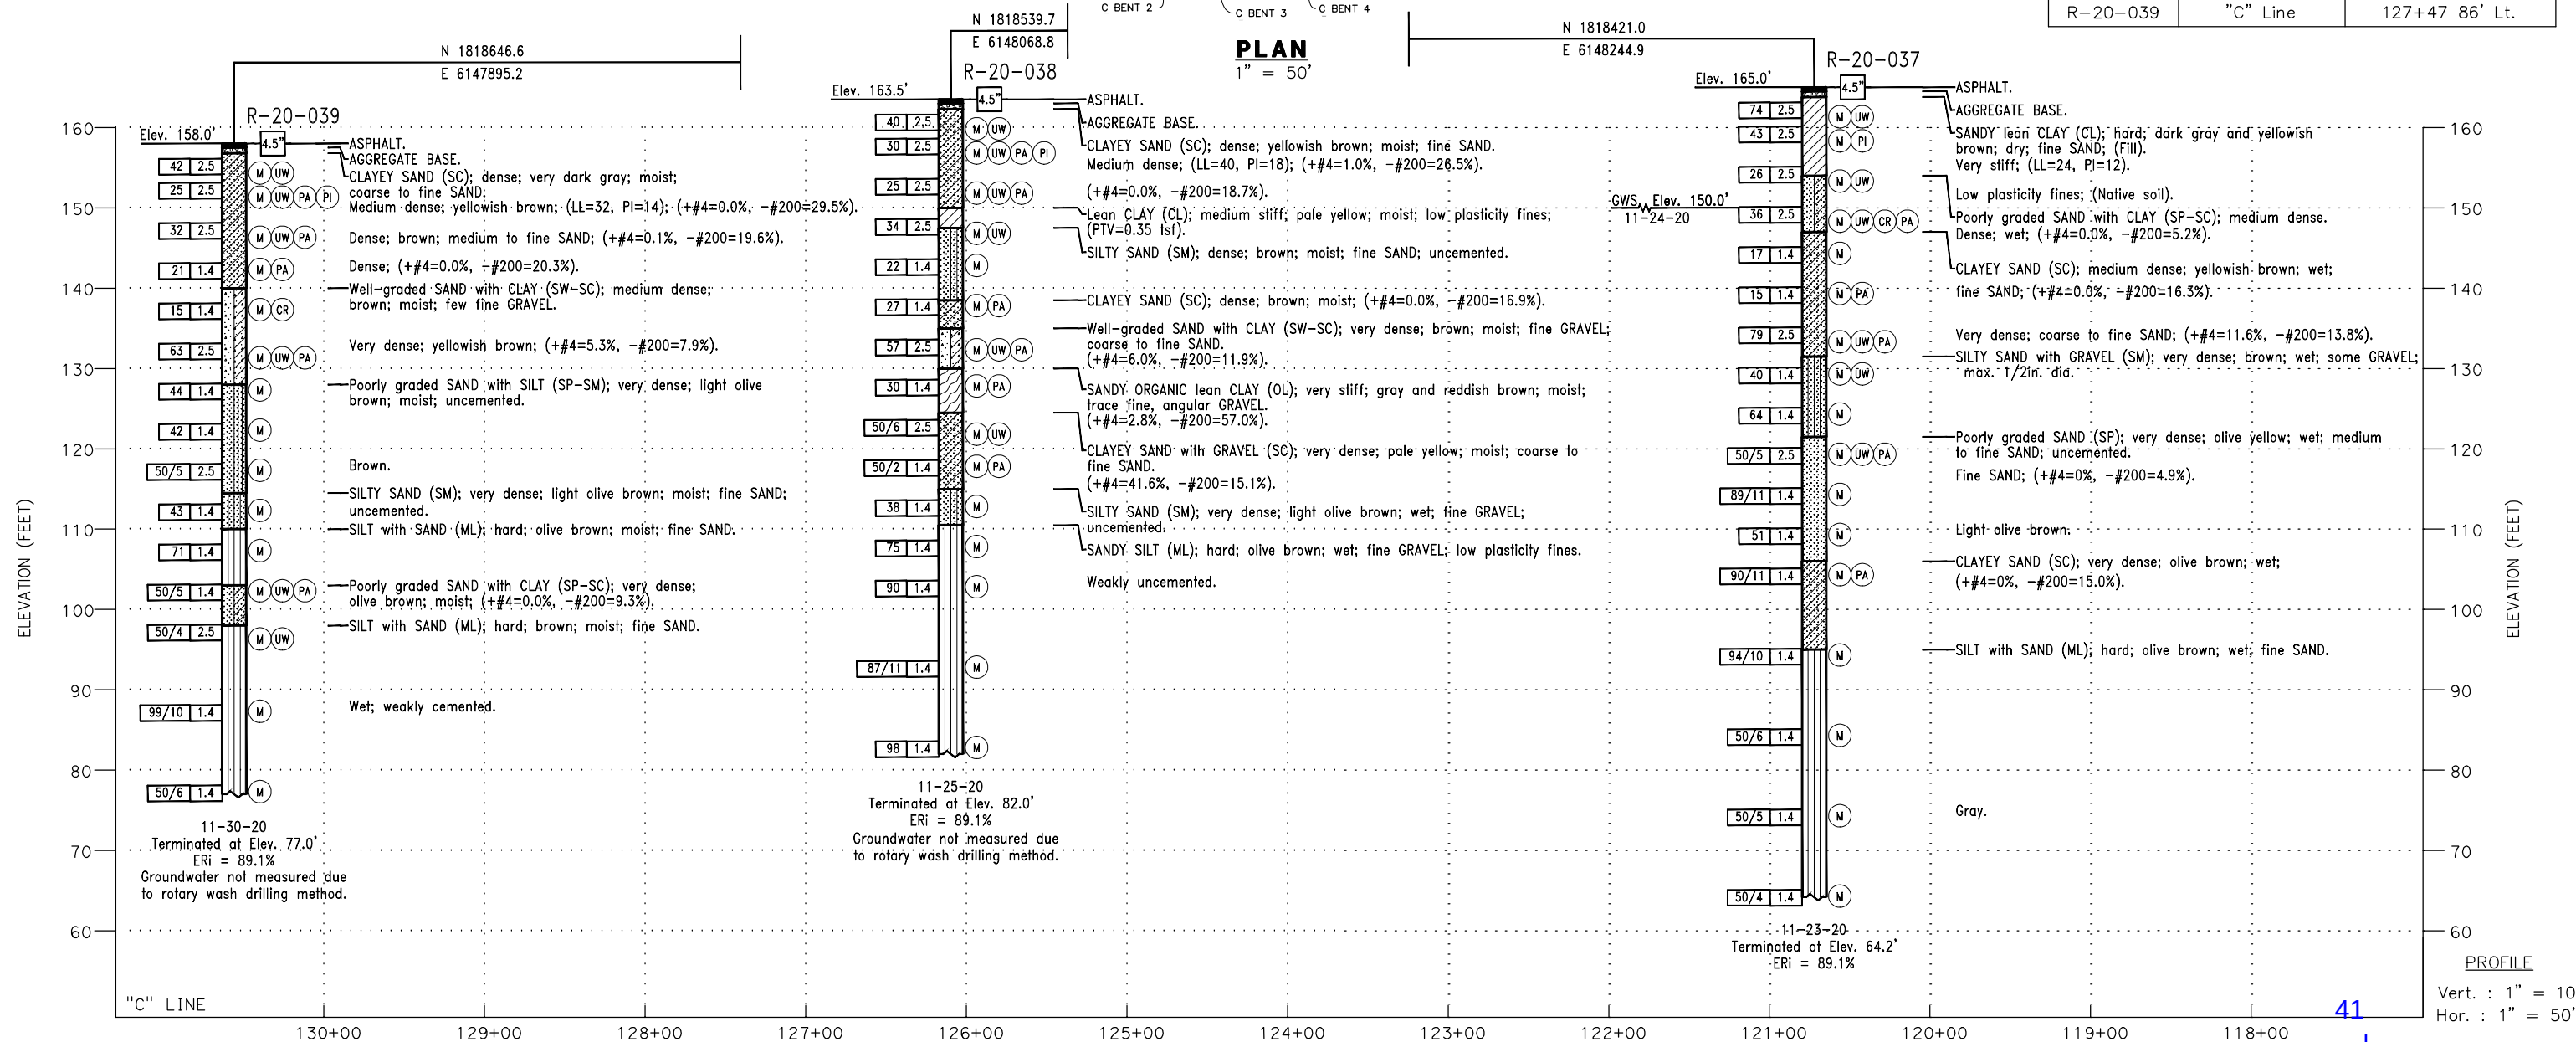

TIME PLATTED -> 7.06 PM

PERSONNEL	DATE	BY	OFFICE	14	1.5	21

	SCALE: AS SHOWN	VERT.DATUM X	HORZ.DATUM X
DESIGN OVERSIGHT	PHOTOGRAMMETRY AS OF: X		ALIGNMENT TIES X
	SURVEYED	BY X	DRAFTED BY K. OUYANG
SIGN OFF DATE	FIELD CHECKED	BY X	CHECKED BY G. PARIKH

DESIGN	BY K. ADHIKARI
DETAILS	BY
QUANTITIES	BY

PREPARED FOR THE
STATE OF CALIFORNIA
DEPARTMENT OF TRANSPORTATION

K. SARAVANAPAVAN PROJECT ENGINEER	BRIDGE NO.
	36-0128
	POST MILES
	10.87

MAR VISTA DRIVE POC
LOG OF TEST BORINGS 2 OF 2

FOUNDATION PLAN SHEET (ENGLISH) (REV. 03/14/12)

ORIGINAL SCALE IN INCHES
FOR REDUCED PLANS

UNIT:	X
PROJECT NUMBER & PHASE:	0518000116

CONTRACT NO.: 05-0C7331

DISREGARD PRINTS BEARING
EARLIER REVISION DATES

REVISION DATES				SHEET	OF
				38	38

```
FILE => MV POC_LOTB
```