



		4-22-2022	
REGISTERED STRUCTURAL ENGINEER		DATE	
PLANS APPROVAL DATE			
THE STATE OF CALIFORNIA OR ITS OFFICERS OR AGENTS SHALL NOT BE RESPONSIBLE FOR THE ACCURACY OR COMPLETENESS OF SCANNED COPIES OF THIS PLAN SHEET.			
MARK THOMAS 2121 ALTON PARKWAY, SUITE 210 IRVINE, CA 92606			
CITY OF TEMECULA 41000 MAIN STREET TEMECULA, CA 92590			

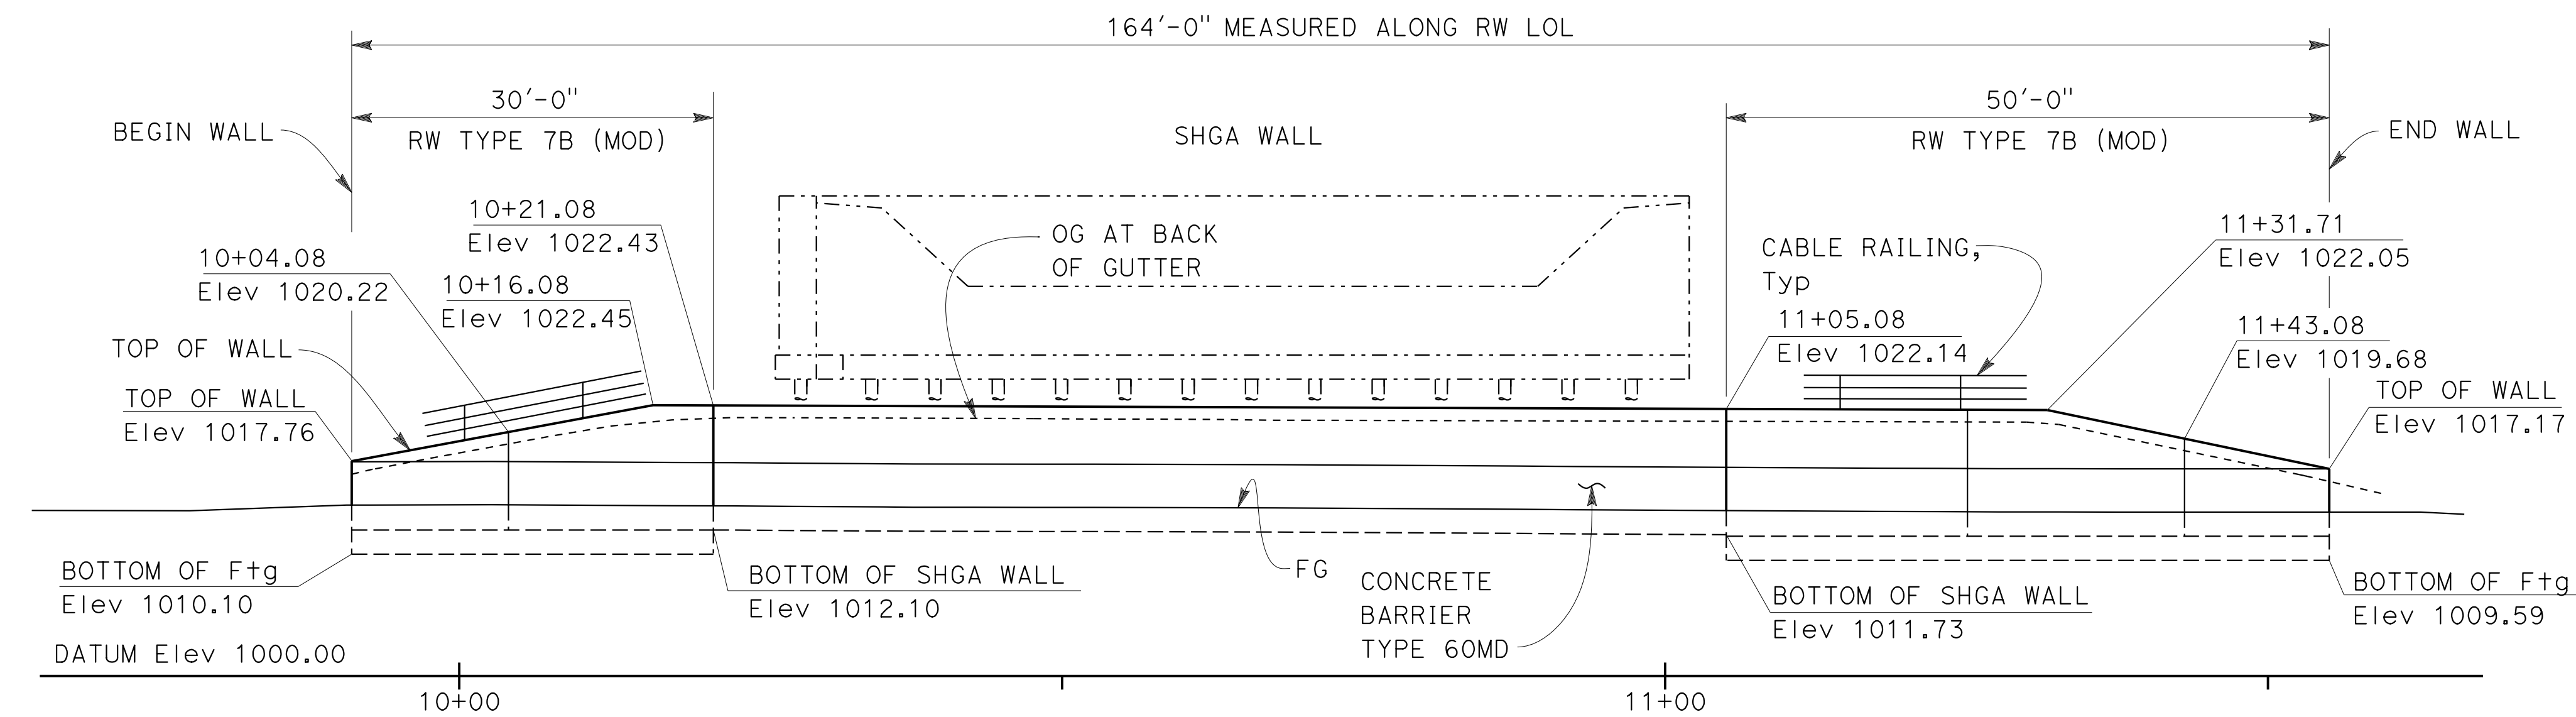

LEGEND:

-  Indicates Direction of Travel
 Indicates Retaining Wall
 Indicates Existing Structure
 SHGA Sub Horizontal Ground Anchor


MIRRORED ELEVATION
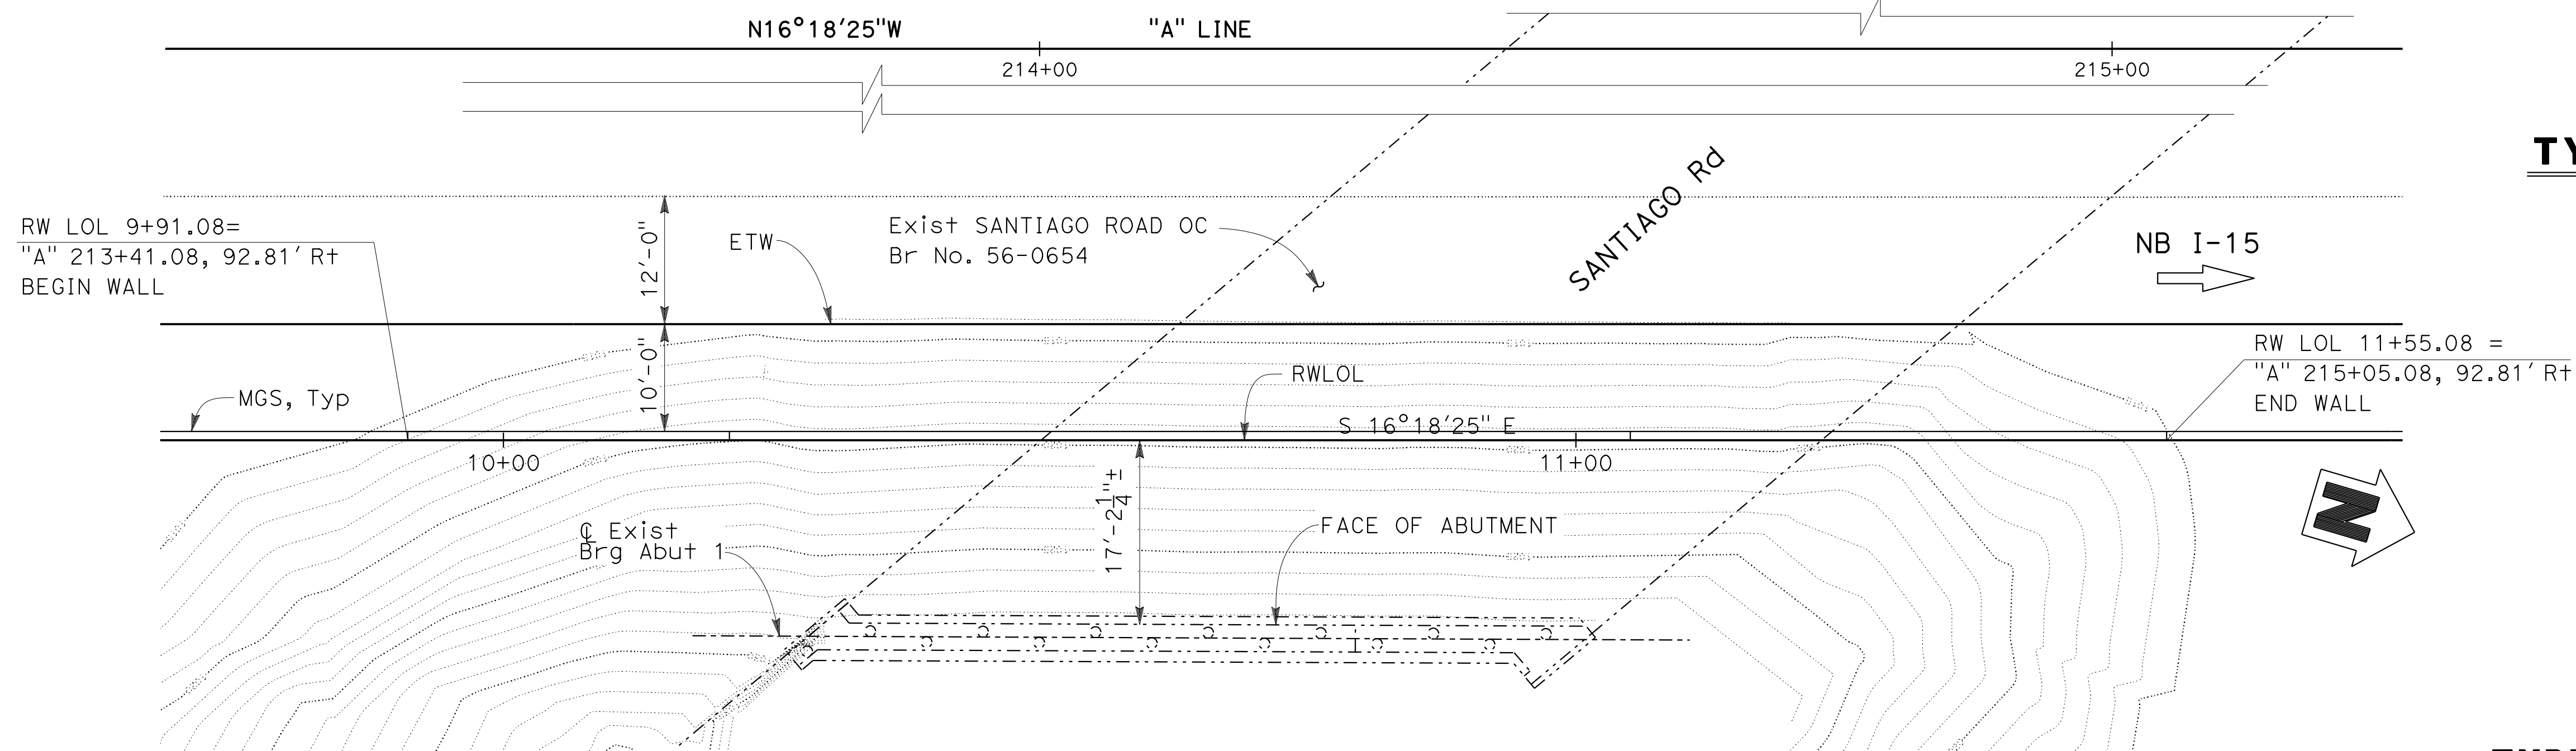
$$1'' = 10'$$


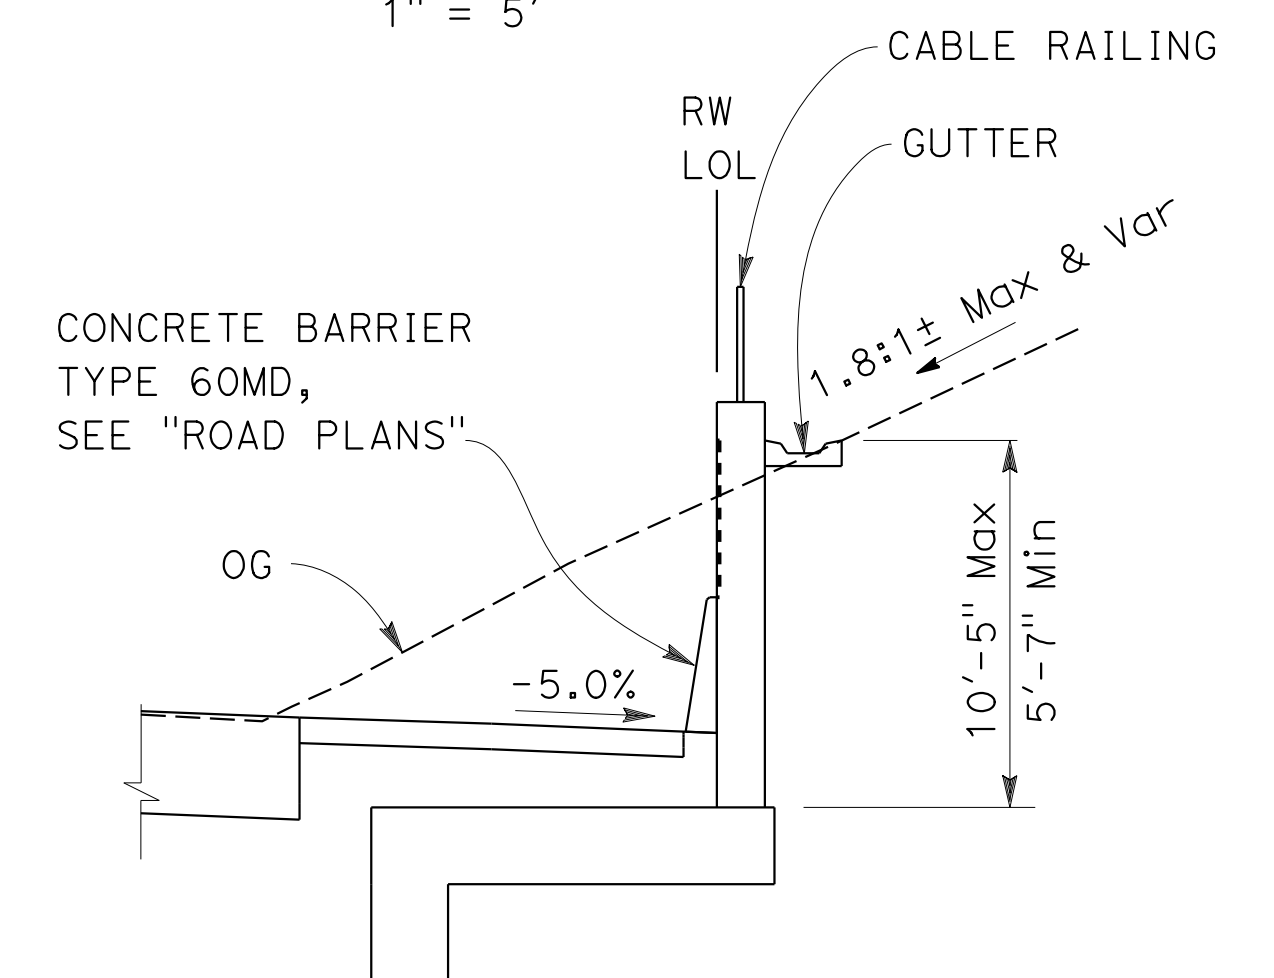
PLAN

$$\overline{1'' = 10'}_{84'-0''}$$

NOTE:
THE CONTRACTOR MUST VERIFY ALL
CONTROLLING FIELD DIMENSIONS BEFORE
ORDERING OR FABRICATING ANY MATERIAL.

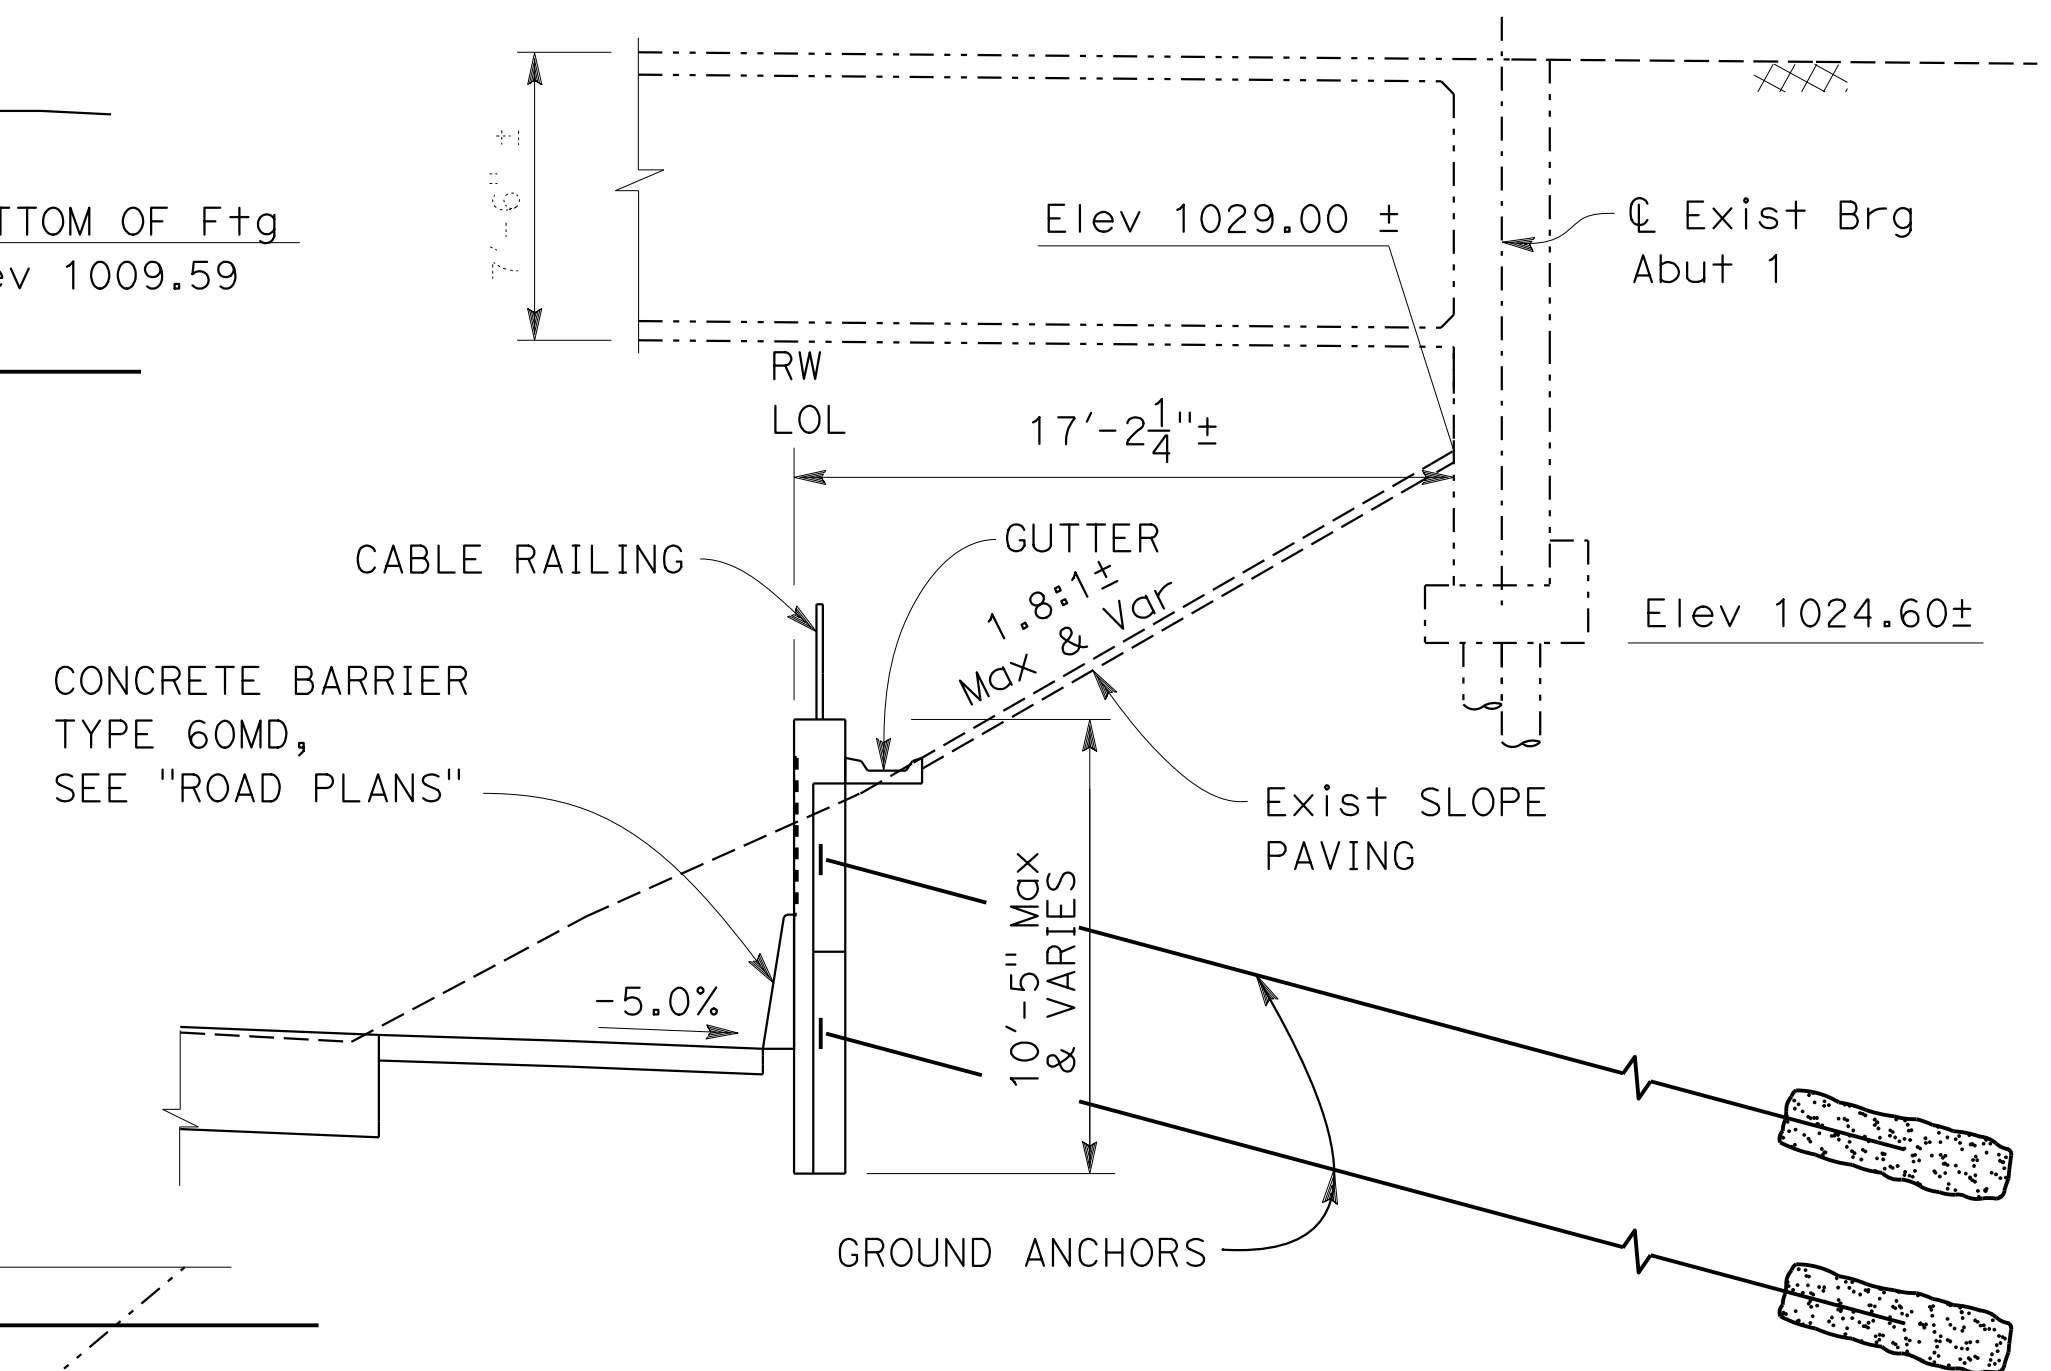

TYPICAL SECTION - SHGA WALL

$$1'' = 5'$$


TYPICAL SECTION - TYPE 7B (MOD) WALL

$$1'' = 5'$$

100% SUBMITTAL

DESIGN OVERSIGHT	DESIGN	BY Y. REN	CHECKED J. SAMPSON	LOAD & RESISTANCE FACTOR DESIGN		PREPARED FOR THE STATE OF CALIFORNIA DEPARTMENT OF TRANSPORTATION	JULIE PASSALACQUA PROJECT ENGINEER		BRIDGE No. 56E0210	SANTIAGO ROAD OC RETAINING WALL													
	DETAILS	BY G. BOYKO	CHECKED J. SAMPSON	LAYOUT	BY G. BOYKO		CHECKED Y. REN	POST MILE	GENERAL PLAN														
	QUANTITIES	BY K. WU	CHECKED A. CLUBB	SPECIFICATIONS	BY Y. REN		PLANS AND SPECS COMPARED	4.1															
SIGN OFF DATE																							
DESIGN GENERAL PLAN SHEET (ENGLISH) (REVISION 4/19/2018)				DATE PLOTTED => 15-FEB-2022 FILE => 01_TEM_RW-gp.dgn		TIME PLOTTED => 17:45 USERNAME => jvalenzuel		ORIGINAL SCALE IN INCHES FOR REDUCED PLANS		0 1 2 3		UNIT: PROJECT NUMBER & PHASE: 0820000074		CONTRACT No.: 08-1K402		DISREGARD PRINTS BEARING EARLIER REVISION DATES		REVISION DATES 3/30/20 7/14/20		SHEET 1		OF 11	

GENERAL NOTES - SHGA WALL

DESIGN: AASHTO LRFD Bridge Design Specifications, 8th Edition with California Amendments, preface dated April 2019.

SEISMIC: K_h = 0.19 K_v = 0.0

SOIL: ϕ = 34° γ = 120 pcf

SHOTCRETE: f_y = 60 ksi (Yield strength of reinforcement) f'c = 4.0 ksi (28 days Compressive strength) f'ci = 3.2 ksi (at time of stressing)

CONCRETE: f_y = 60 ksi f'c = 4.0 ksi n = 8

PRESTRESSING STEEL: See "SUB HORIZONTAL GROUND ANCHOR DETAILS" sheet.

FDL = 80.0 kips FTL = 80.0 kips LL = 53.3 kips

STRUCTURAL STEEL: f_y = 36 ksi (ASTM A709, Grade 36)

GENERAL NOTES TYPE 7B (MODIFIED) WALL

DESIGN: AASHTO LRFD Bridge Design Specifications, 8th edition with California Amendments, preface dated April 2019.

SEISMIC: K_h = 0.19 K_v = 0.0 Seismic Earth Pressure Increment = 25 pcf

SOIL: ϕ = 34° (Beneath Footing) Active Earth Pressure = 56 pcf

CONCRETE: f'c = 3.6 ksi f_y = 60 ksi

STANDARD PLANS DATED 2018

A3A - A3C A10A - A10E A10F & A10G B0-3 B3-6 B9-6 B11-47 RSP A76A ABBREVIATIONS LINES AND SYMBOLS LEGEND - SOIL BRIDGE DETAILS RETAINING WALL DETAILS No. 2 STRUCTURE APPROACH DRAINAGE DETAILS CABLE RAILING CONCRETE BARRIER TYPE 60MD



BENCHMARKS:

BASIS OF BEARING The Basis of Bearings for this survey is based on the California Coordinate System (CCS83), Zone VI, NAD83 (NSRS2007, Epoch 2007.00) as determined locally by a line between Continuous Global Positioning Stations (CGPS) "P477" and "BILL" being North 28°53'23" East as derived from coordinates published by the California Spatial Reference Center (CSRC) on 01/18/2007.

Station	Latitude	Longitude	Northing	Easting
P477	N33°30'10.06775"	W117°06'48.08654"	2127663.41	6298483.02
BILL	N33°34'41.66159"	W117°03'52.51146"	2154994.78	6313564.36


VERTICAL DATUM AND BENCHMARKS Elevations shown are based on the North American Vertical Datum of 1988 (NAVD88). The Cal Trans 6033-01 Control Datasheet elevation at the following Benchmark was used:

Designation	Elevation
RIV 79 -19.3	1001.16


Found Standard CADT Disk down 0.5' stamped "1998 BM RIV 79-19.3", 35' northerly of the curb flowline of the North bound Hwy 79, +/- 52' westerly of a culvert in a headwall, at approximate prod of Wabash Ln.

QUANTITIES

STRUCTURE EXCAVATION (RETAINING WALL)	448 CY
STRUCTURE EXCAVATION (GROUND ANCHOR WALL)	57 CY
STRUCTURE BACKFILL (RETAINING WALL)	261 CY
STRUCTURE BACKFILL (GROUND ANCHOR WALL)	6 CY
GROUND ANCHOR (SUBHORIZONTAL)	16 EA
GROUND ANCHOR (RETAINING WALL)	132 CY
-FRACTURED RIB TEXTURE	620 SQFT
BAR REINFORCING STEEL (RETAINING WALL)	25,505 LB
STRUCTURE SHOTCRETE	23 CY
MINOR CONCRETE (GUTTER)	164 LF
CABLE RAILING	164 LF

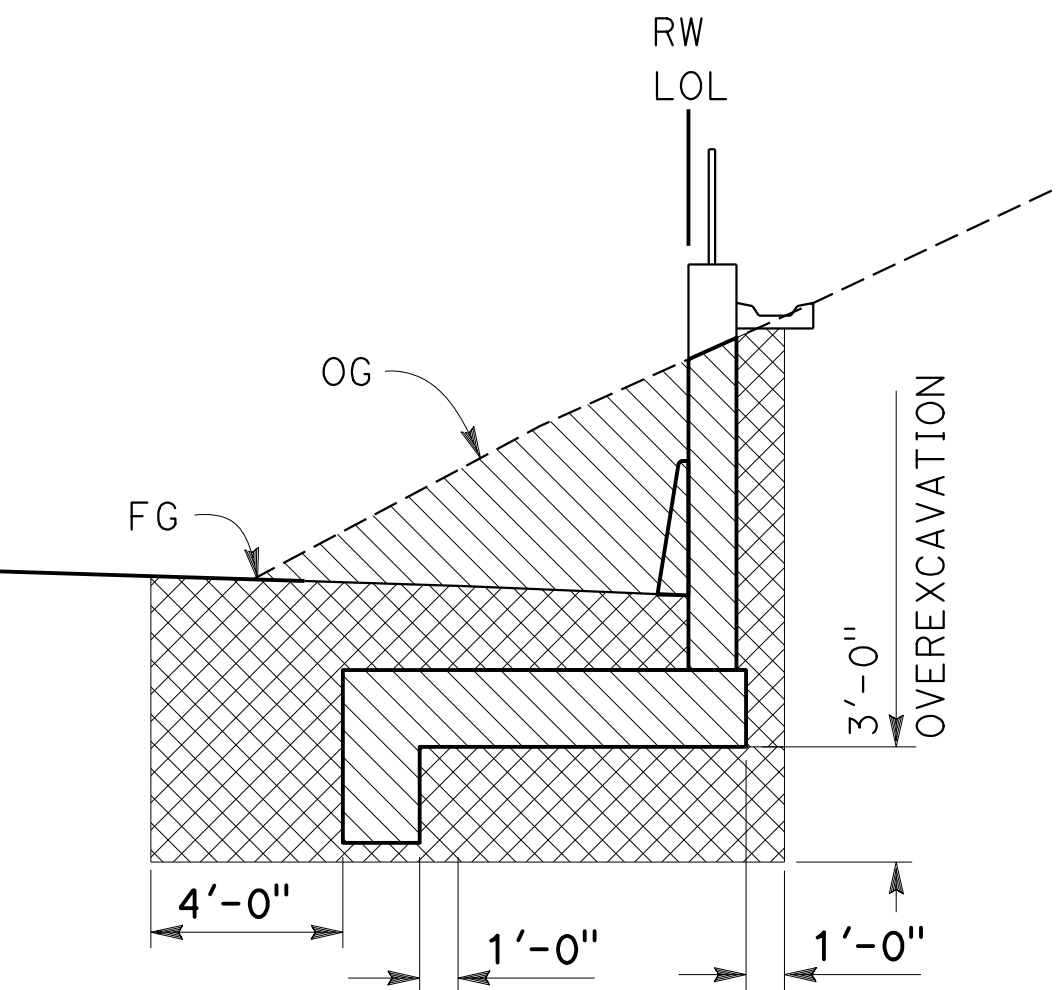


RW TYPE 7B (MOD) WALL

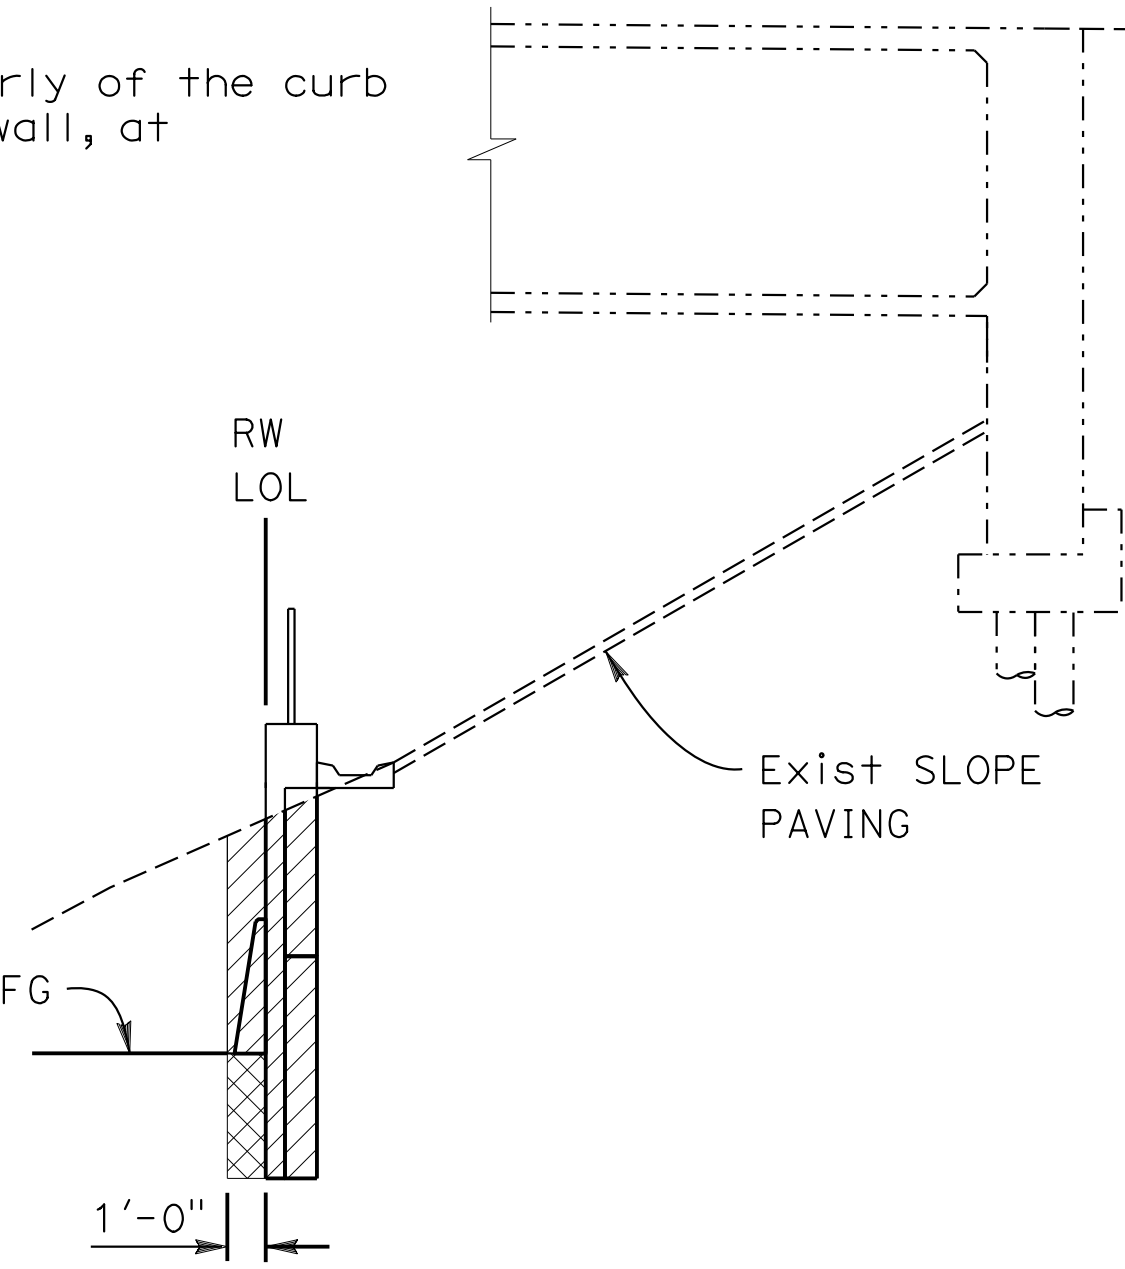

SHGA WALL

LIMITS OF PAYMENT FOR STRUCTURE EXCAVATION & BACKFILL

NO SCALE

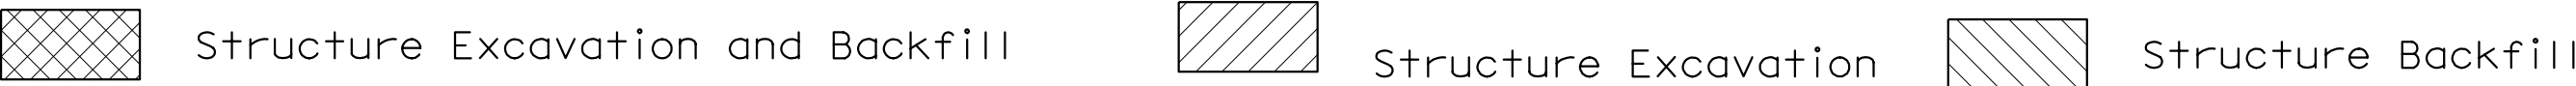


NOTE: THE CONTRACTOR MUST VERIFY ALL CONTROLLING DIMENSIONS BEFORE ORDERING OR FABRICATING ANY MATERIAL.

INDEX TO PLANS

SHEET NO.	TITLE
1	GENERAL PLAN
2	INDEX TO PLANS
3	STRUCTURE PLAN NO. 1
4	STRUCTURE PLAN NO. 2
5	RETAINING WALL DETAILS NO. 1
6	RETAINING WALL DETAILS NO. 2
7	SUB HORIZONTAL GROUND ANCHOR DETAILS
8	WALL DRAINAGE DETAILS
9	ARCHITECTURAL TREATMENT DETAIL
10	LOG OF TEST BORINGS 1 OF 2
11	LOG OF TEST BORINGS 2 OF 2


100% SUBMITTAL

DESIGN OVERSIGHT		DESIGN BY Y. REN CHECKED J. SAMPSON		PREPARED FOR THE STATE OF CALIFORNIA DEPARTMENT OF TRANSPORTATION		JULIE PASSALACQUA PROJECT ENGINEER		BRIDGE No. 56E0210		SANTIAGO ROAD OC RETAINING WALL																									
SIGN OFF DATE		DETAILS BY G. BOYKO CHECKED J. SAMPSON				POST MILE		INDEX TO PLANS																											
		QUANTITIES BY K. WU CHECKED A. CLUBB				4.1																													
DESIGN DETAIL SHEET (ENGLISH) (REVISION 4/19/2018)				DATE PLOTTED => 15-FEB-2022 FILE => 02_TEM_RW1-ip.dgn		TIME PLOTTED => 17:45 USERNAME => jvalenzuela		ORIGINAL SCALE IN INCHES FOR REDUCED PLANS		0		1		2		3		UNIT: PROJECT NUMBER & PHASE: 0820000074		CONTRACT No.: 08-1K402		DISREGARD PRINTS BEARING EARLIER REVISION DATES		7/07/20								SHEET 2		OF 11	

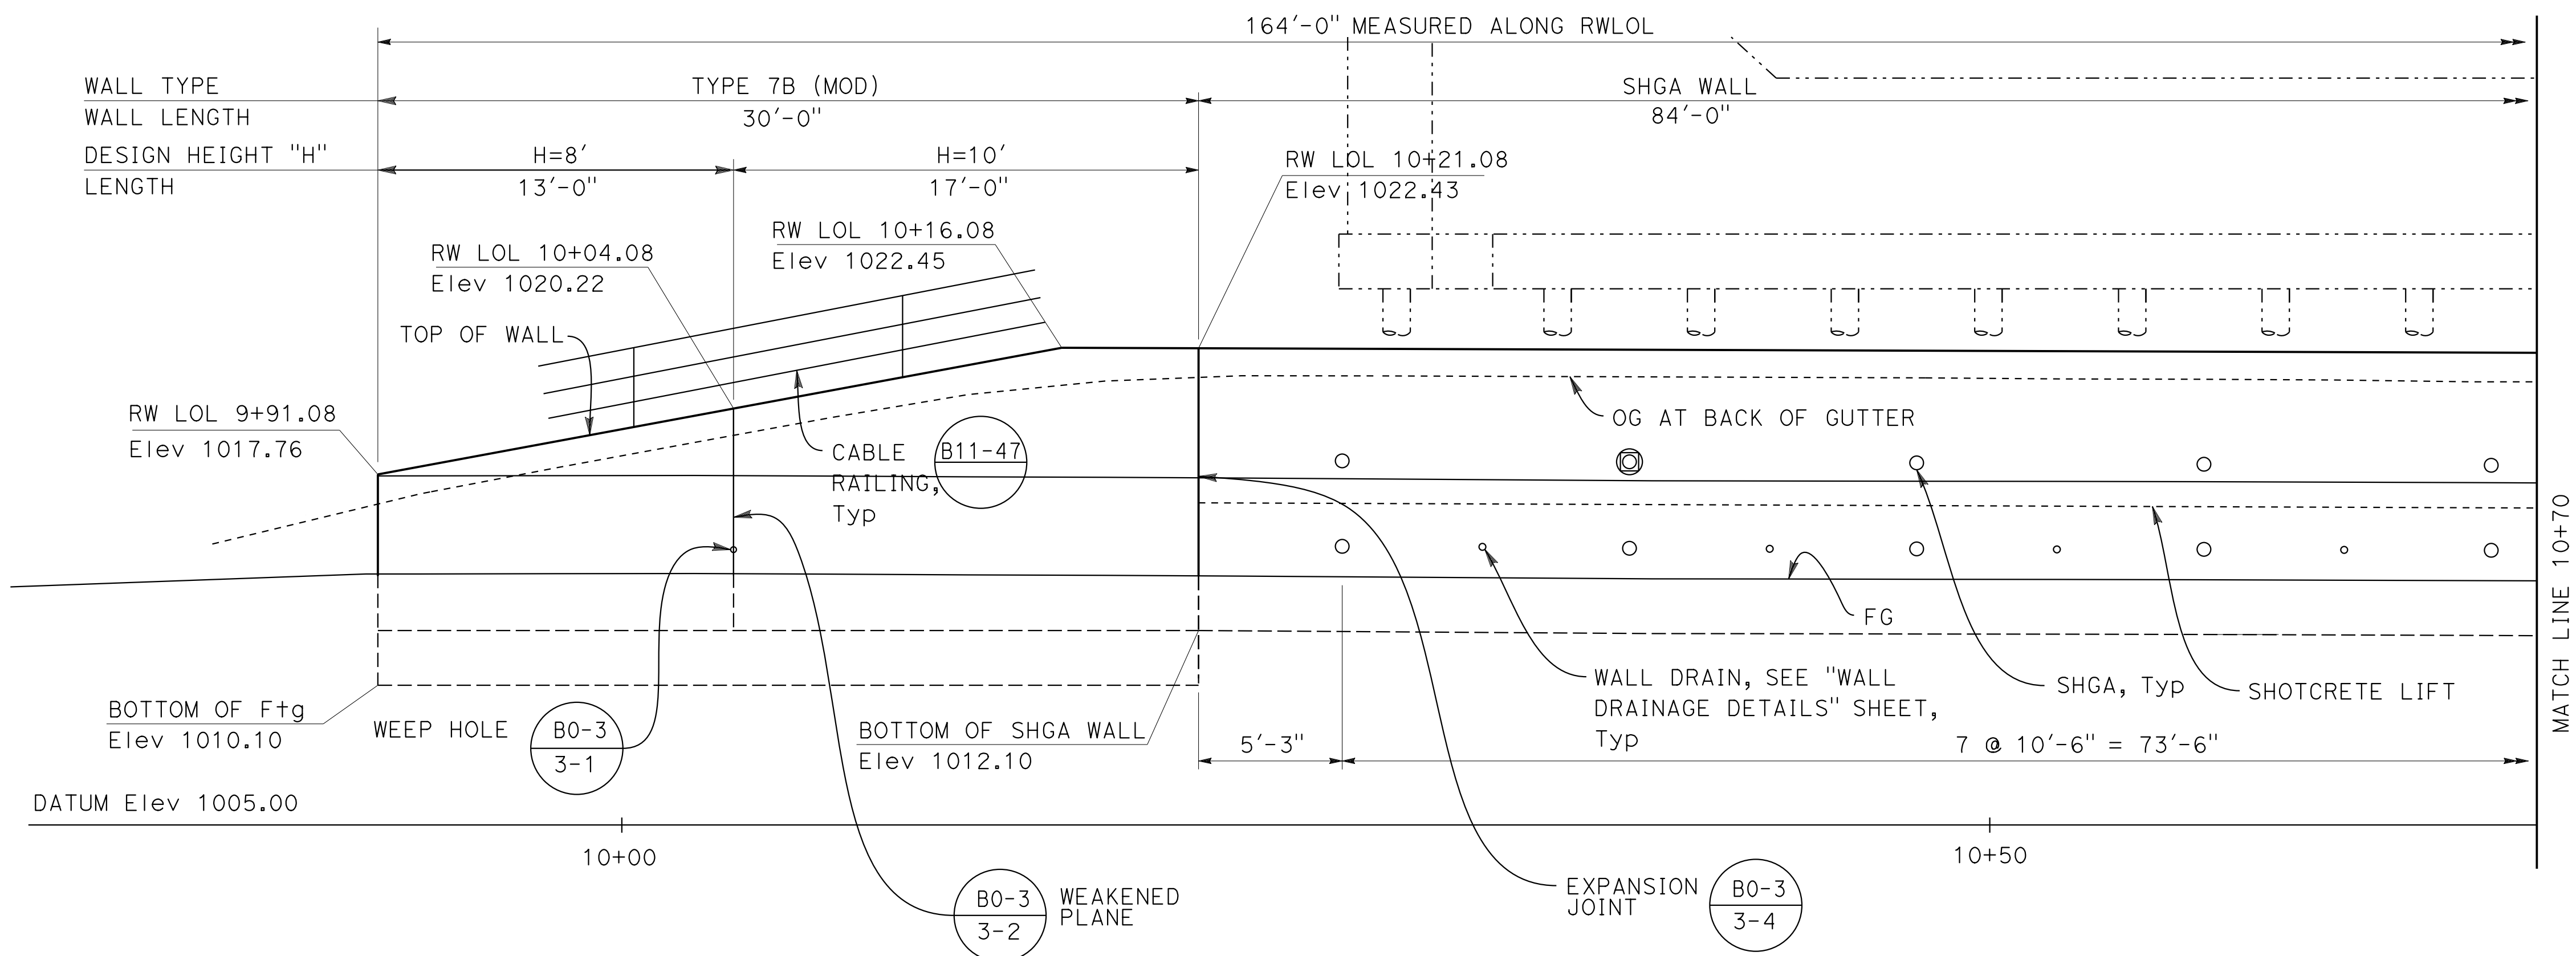

ELEVATION

1/4" = 1'-0"

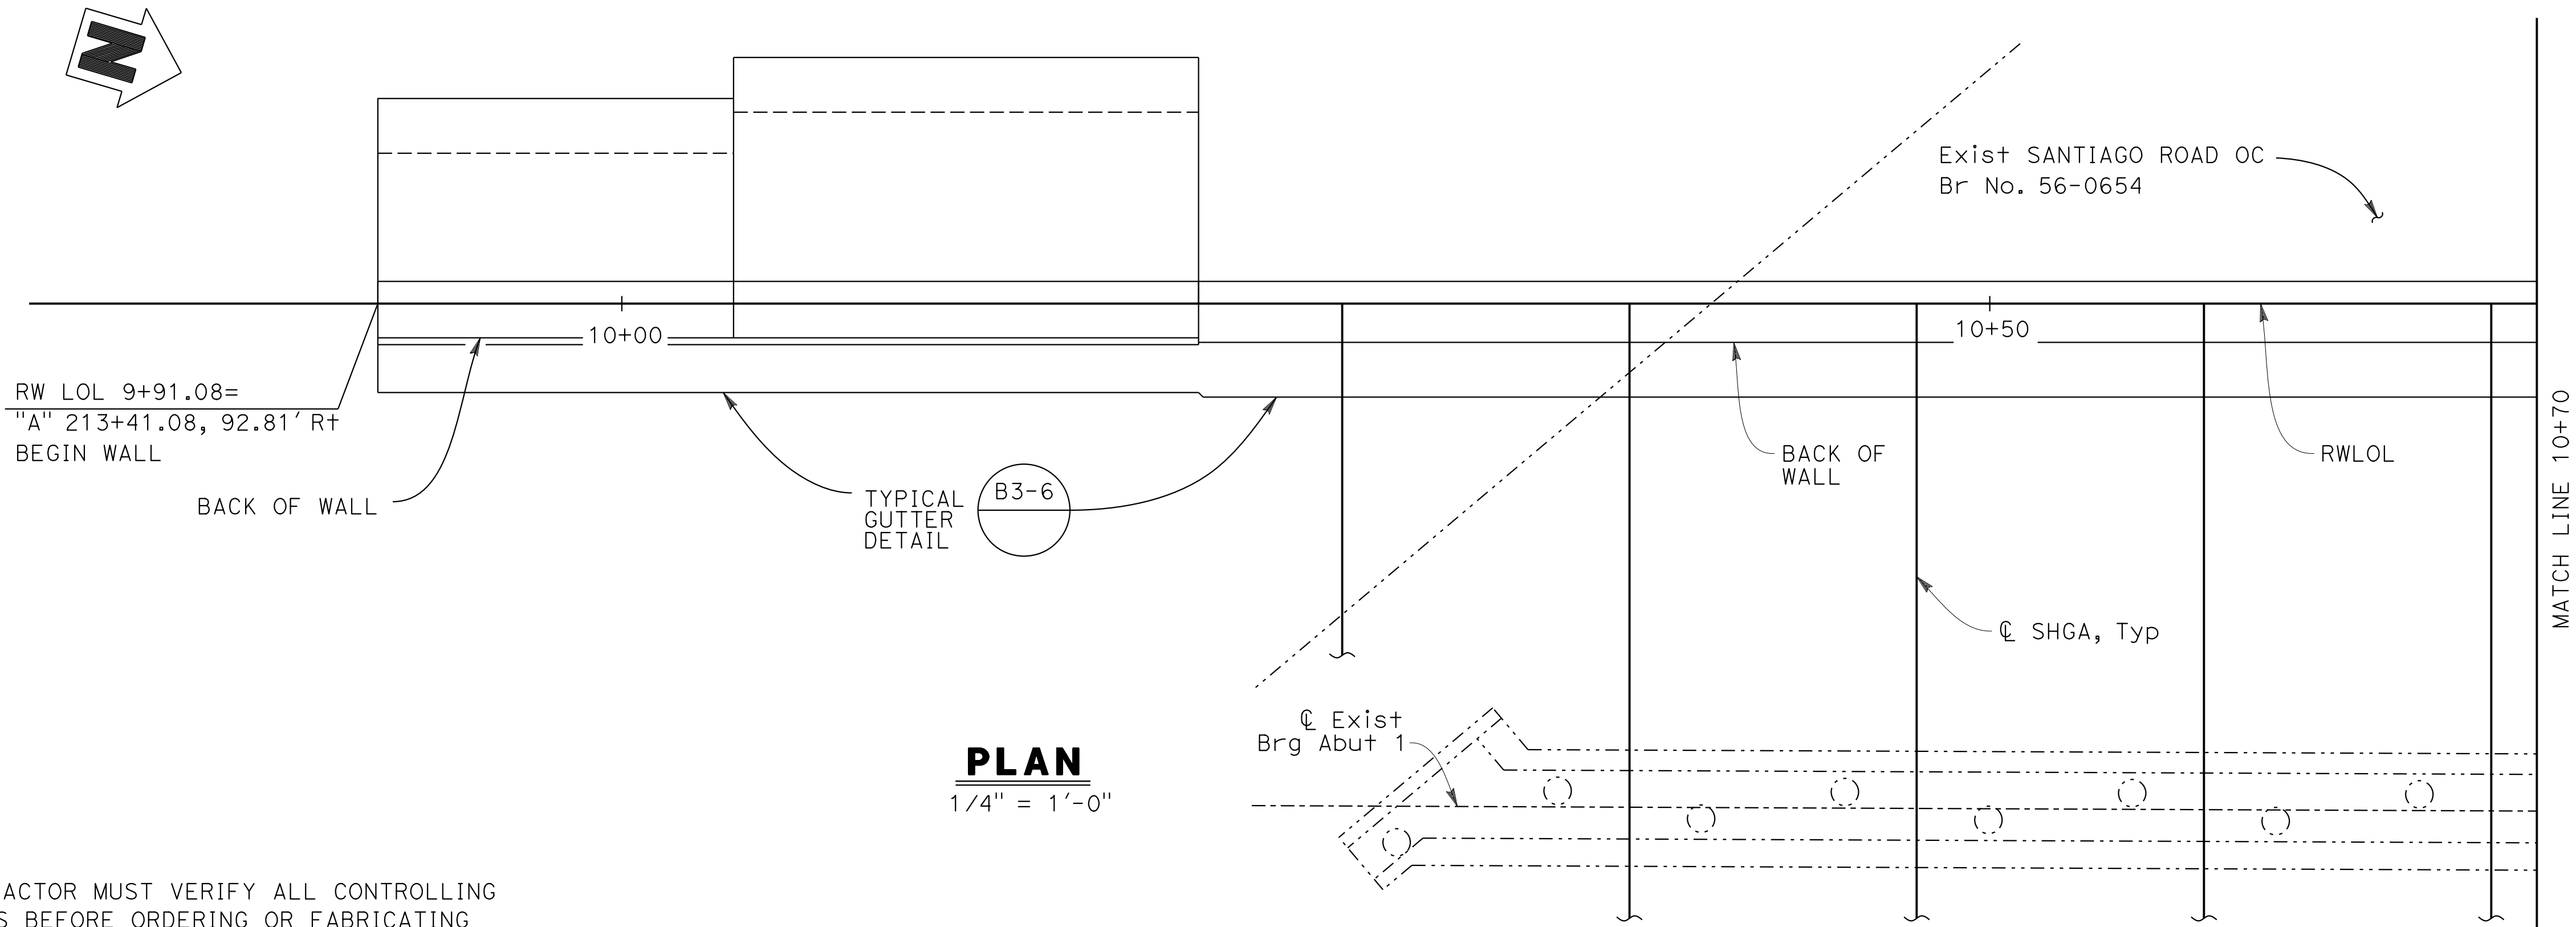

PLAN

1/4" = 1'-0"

NOTE:
THE CONTRACTOR MUST VERIFY ALL CONTROLLING
DIMENSIONS BEFORE ORDERING OR FABRICATING
ANY MATERIAL.

NOTES:

- All ground anchors must have a bearing to perpendicular RWLOL.
- For each row of ground anchors excavate no more than one-fifth of the total ground anchor wall length prior to drilling and tensioning ground anchor. Slot cut for smaller length of excavation may be needed for local stability. Maintain continuity of horizontal #7 bars in shotcrete by providing a 3'-6" lap length at construction joint.
- Location of existing piles shown are approximate. Contractor to verify location of existing piles prior to drilling ground anchor. Ground anchors may be adjusted to clear existing piles with approval of Engineer.



LEGEND:

- Indicates SHGA location
- Indicates Retaining Wall
- - - - - Indicates Existing Structure
- SHGA Sub Horizontal Ground Anchor
- ⊙ Indicates ground anchor to be performance tested

100% SUBMITTAL

DESIGN OVERSIGHT		DESIGN BY Y. REN	CHECKED J. SAMPSON	PREPARED FOR THE STATE OF CALIFORNIA DEPARTMENT OF TRANSPORTATION		BRIDGE No. 56E0210	SANTIAGO ROAD OC RETAINING WALL	
SIGN OFF DATE		DETAILS BY G. BOYKO	CHECKED J. SAMPSON	JULIE PASSALACQUA PROJECT ENGINEER		POST MILE 4.1	STRUCTURE PLAN No. 1	
DESIGN DETAIL SHEET (ENGLISH) (REVISION 4/19/2018)		QUANTITIES BY K. WU	CHECKED A. CLUBB	UNIT: PROJECT NUMBER & PHASE: 0820000074		CONTRACT No.: 08-1K402	DISREGARD PRINTS BEARING EARLIER REVISION DATES	REVISION DATES 7/07/20
DATE PLOTTED => 15-FEB-2022 FILE => 03_TEM_RW-w11.dgn		TIME PLOTTED => 17:45 USERNAME => jvalenzuela		ORIGINAL SCALE IN INCHES FOR REDUCED PLANS		0 1 2 3	SHEET 3	OF 11

Ying Ren		4-22-2022
REGISTERED STRUCTURAL ENGINEER		DATE
PLANS APPROVAL DATE		
THE STATE OF CALIFORNIA OR ITS OFFICERS OR AGENTS SHALL NOT BE RESPONSIBLE FOR THE ACCURACY OR COMPLETENESS OF SCANNED COPIES OF THIS PLAN SHEET.		
MARK THOMAS 2121 ALTON PARKWAY, SUITE 210 IRVINE, CA 92606		
CITY OF TEMECULA 41000 MAIN STREET TEMECULA, CA 92590		

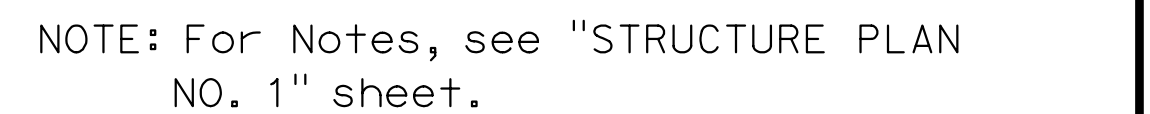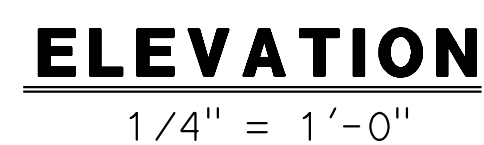

100% SUBMITTAL

DESIGN OVERSIGHT	BY Y. REN	CHECKED J. SAMPSON	PREPARED FOR THE STATE OF CALIFORNIA DEPARTMENT OF TRANSPORTATION	JULIE PASSALACQUA PROJECT ENGINEER	BRIDGE No.	SANTIAGO ROAD OC RETAINING WALL STRUCTURE PLAN No. 2				
					56E0210					
					POST MILE					
SIGN OFF DATE	BY G. BOYKO	CHECKED J. SAMPSON			4.1					
	BY K. WU	CHECKED A. CLUBB								
DESIGN DETAIL SHEET (ENGLISH) (REVISION 4/19/2018)	DATE PLOTTED => 15-FEB-2022 FILE => '04_TEM_RW-w12.dgn'	TIME PLOTTED => 17:45 USERNAME => jvalenzuel	ORIGINAL SCALE IN INCHES FOR REDUCED PLANS	0 1 2 3	UNIT: PROJECT NUMBER & PHASE: 0820000074	CONTRACT NO.: 08-1K402	DISREGARD PRINTS BEARING EARLIER REVISION DATES	REVISION DATES 7/07/20	SHEET 4	OF 11

Dist8COUNTYRivROUTE15POST MILES TOTAL PROJECT3.4/5.0SHEET No.8TOTAL SHEETS11

REGISTERED STRUCTURAL ENGINEER DATE4-22-2022

PLANS APPROVAL DATE

REGISTERED PROFESSIONAL ENGINEER

YING REN

No. 5786

Exp. 12-31-22

STRUCTURAL

STATE OF CALIFORNIA


MARK THOMAS
2121 ALTON PARKWAY, SUITE 210
IRVINE, CA 92606

CITY OF TEMECULA
41000 MAIN STREET
TEMECULA, CA 92590

TABLE OF WALL DIMENSIONS, REINFORCING STEEL AND BEARING STRESS DATA		
DESIGN H	8'	10'
W	9'-0"	10'-6"
C	7'-6"	9'-0"
B	1'-6"	1'-6"
F	2'-0"	2'-0"
D	1'-6"	2'-6"
© BARS	#7 @ 9"	#7 @ 6"
SER I: B'(ft), q ₀ (ksf)	5.8, 1.4	4.9, 1.9
STR Ia: B'(ft), q ₀ (ksf)	5.2, 2.0	4.9, 2.6
STR, Ib: B'(ft), q ₀ (ksf)	3.7, 2.3	2.6, 3.8
Ext I: B'(ft), q ₀ (ksf)	5.2, 1.3	3.7, 2.2
Ext II: B'(ft), q ₀ (ksf)	N/A	N/A

SER: service limit state
STR: strength limit state
EXT: extreme event limit state
B': effective footing width (ft)
q₀: net bearing stress (ksf)
q_g: gross uniform bearing stress (ksf)

NOTE:
THE CONTRACTOR MUST VERIFY ALL CONTROLLING
DIMENSIONS BEFORE ORDERING OR FABRICATING
ANY MATERIAL.

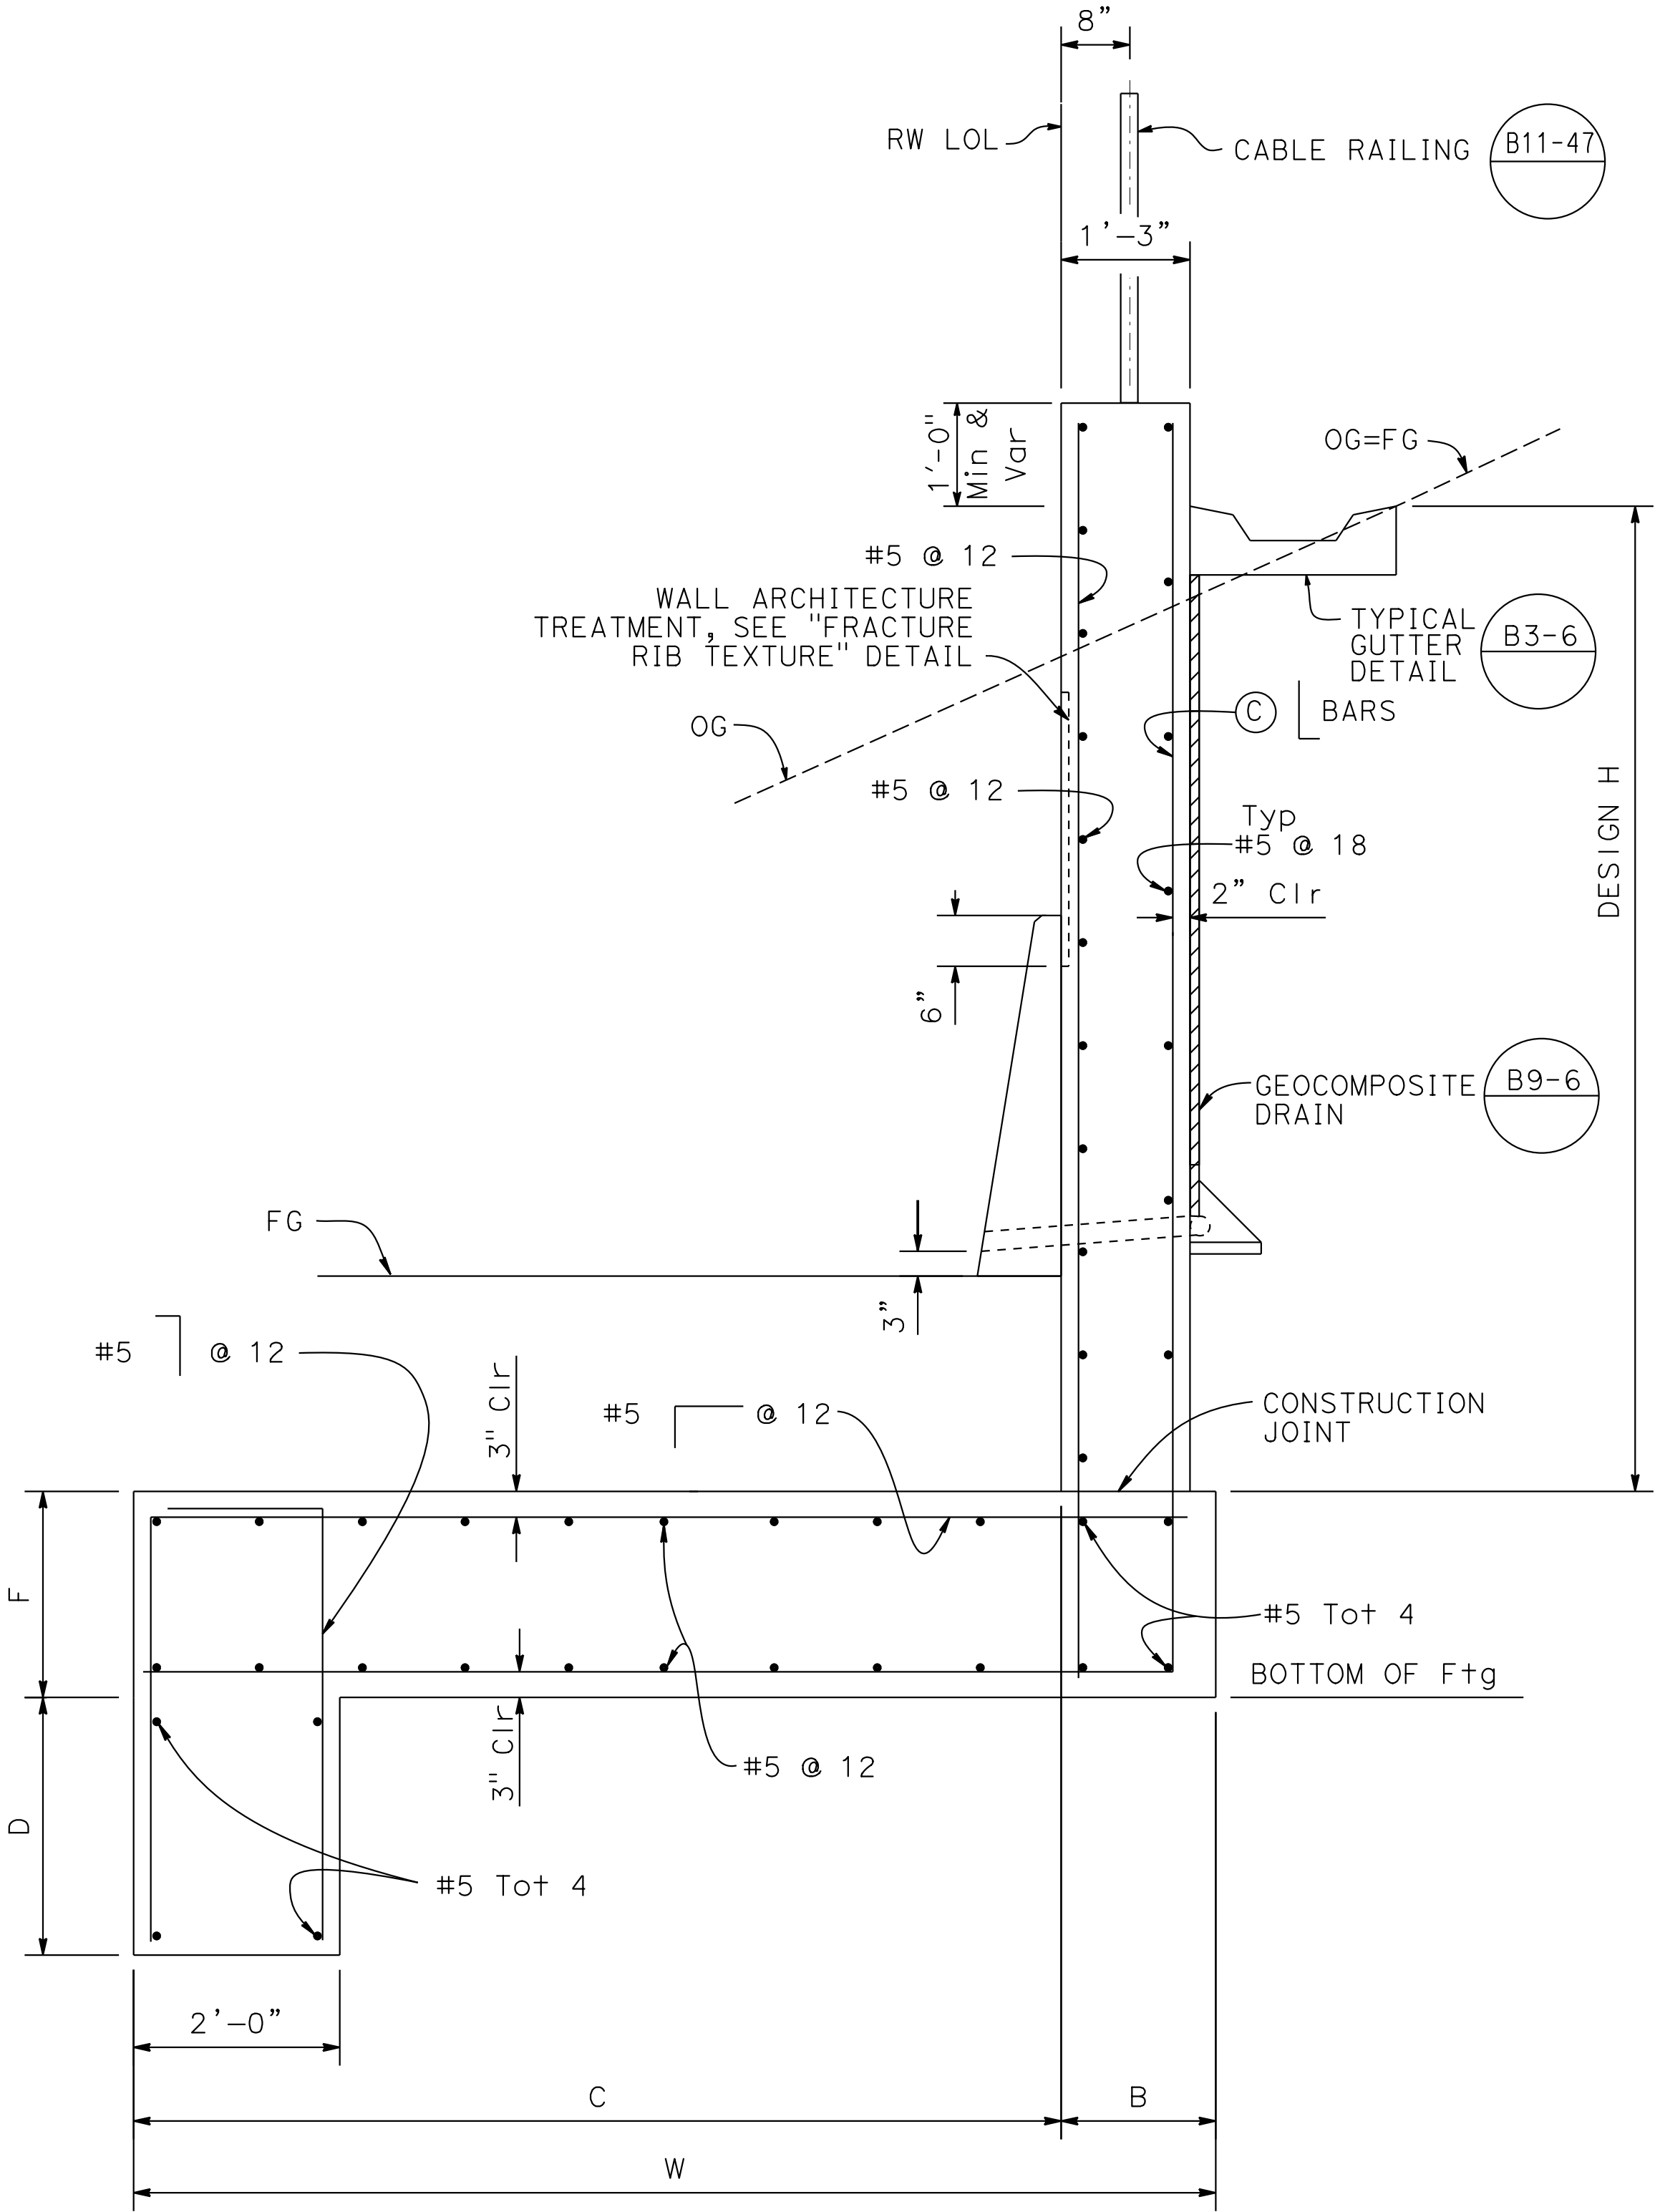

TYPICAL SECTION-TYPE 7B (MODIFIED)
3/4" = 1'-0"

NOTE: For details not shown and drainage notes see, (B3-5) and (B0-3 3-1)

100% SUBMITTAL

DESIGN OVERSIGHT				DESIGN	BY Y. REN	CHECKED J. SAMPSON	PREPARED FOR THE STATE OF CALIFORNIA DEPARTMENT OF TRANSPORTATION	JULIE PASSALACQUA PROJECT ENGINEER		BRIDGE No.	SANTIAGO ROAD OC RETAINING WALL																								
				DETAILS	BY G. BOYKO	CHECKED J. SAMPSON				56E0210	RETAINING WALL DETAILS NO. 1																								
				QUANTITIES	BY K. WU	CHECKED A. CLUBB				POST MILE																									
SIGN OFF DATE										4.1																									
DESIGN DETAIL SHEET (ENGLISH) (REVISION 4/19/2018)				DATE PLOTTED => 15-FEB-2022 FILE => 05_TEM_RW1-def1.dgn				TIME PLOTTED => 17:45 USERNAME => jvalenzuela				ORIGINAL SCALE IN INCHES FOR REDUCED PLANS				UNIT:		PROJECT NUMBER & PHASE: 0820000074				CONTRACT No.: 08-1K402		DISREGARD PRINTS BEARING EARLIER REVISION DATES				REVISION DATES				SHEET		OF	
												0 1 2 3												7/07/20						5		11			

Dist	COUNTY	ROUTE	POST MILES TOTAL PROJECT	SHEET No.	TOTAL SHEETS
8	Riv	15	3.4/5.0		

REGISTERED STRUCTURAL ENGINEER

DATE 4-22-2022

PLANS APPROVAL DATE

REGISTERED PROFESSIONAL ENGINEER

YING REN

No. 5786

Exp. 12-31-22

STRUCTURAL

STATE OF CALIFORNIA

THE STATE OF CALIFORNIA OR ITS OFFICERS OR AGENTS

SHALL NOT BE RESPONSIBLE FOR THE ACCURACY OR

COMPLETENESS OF SCANNED COPIES OF THIS PLAN SHEET.

MARK THOMAS





2121 ALTON PARKWAY, SUITE 210

IRVINE, CA 92606

CITY OF TEMECULA

41000 MAIN STREET

TEMECULA, CA 92590

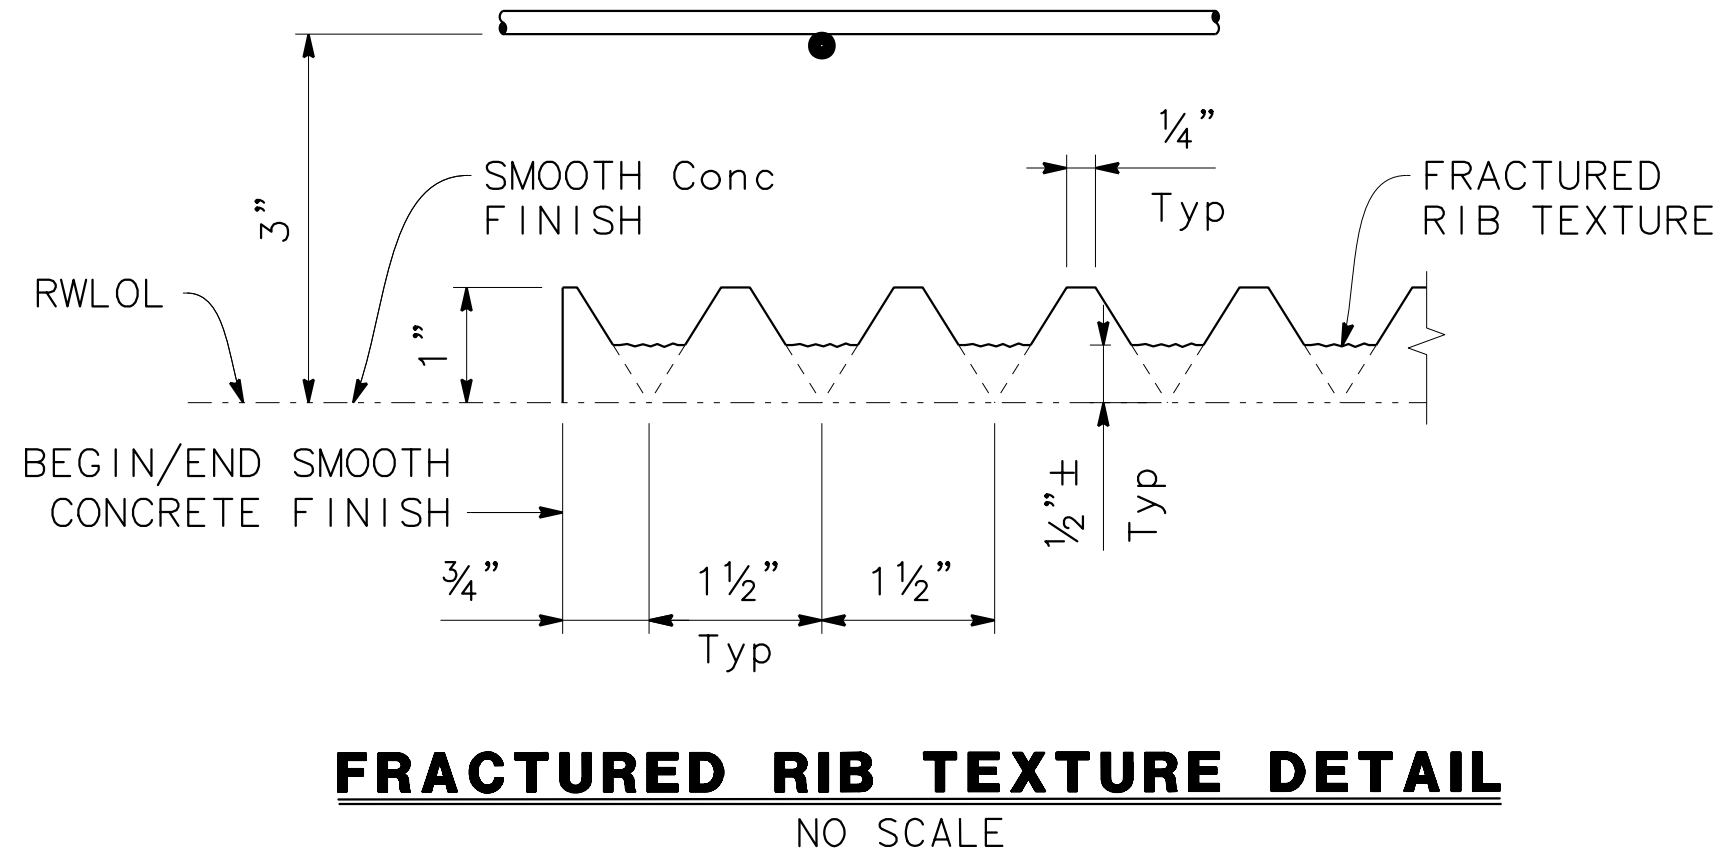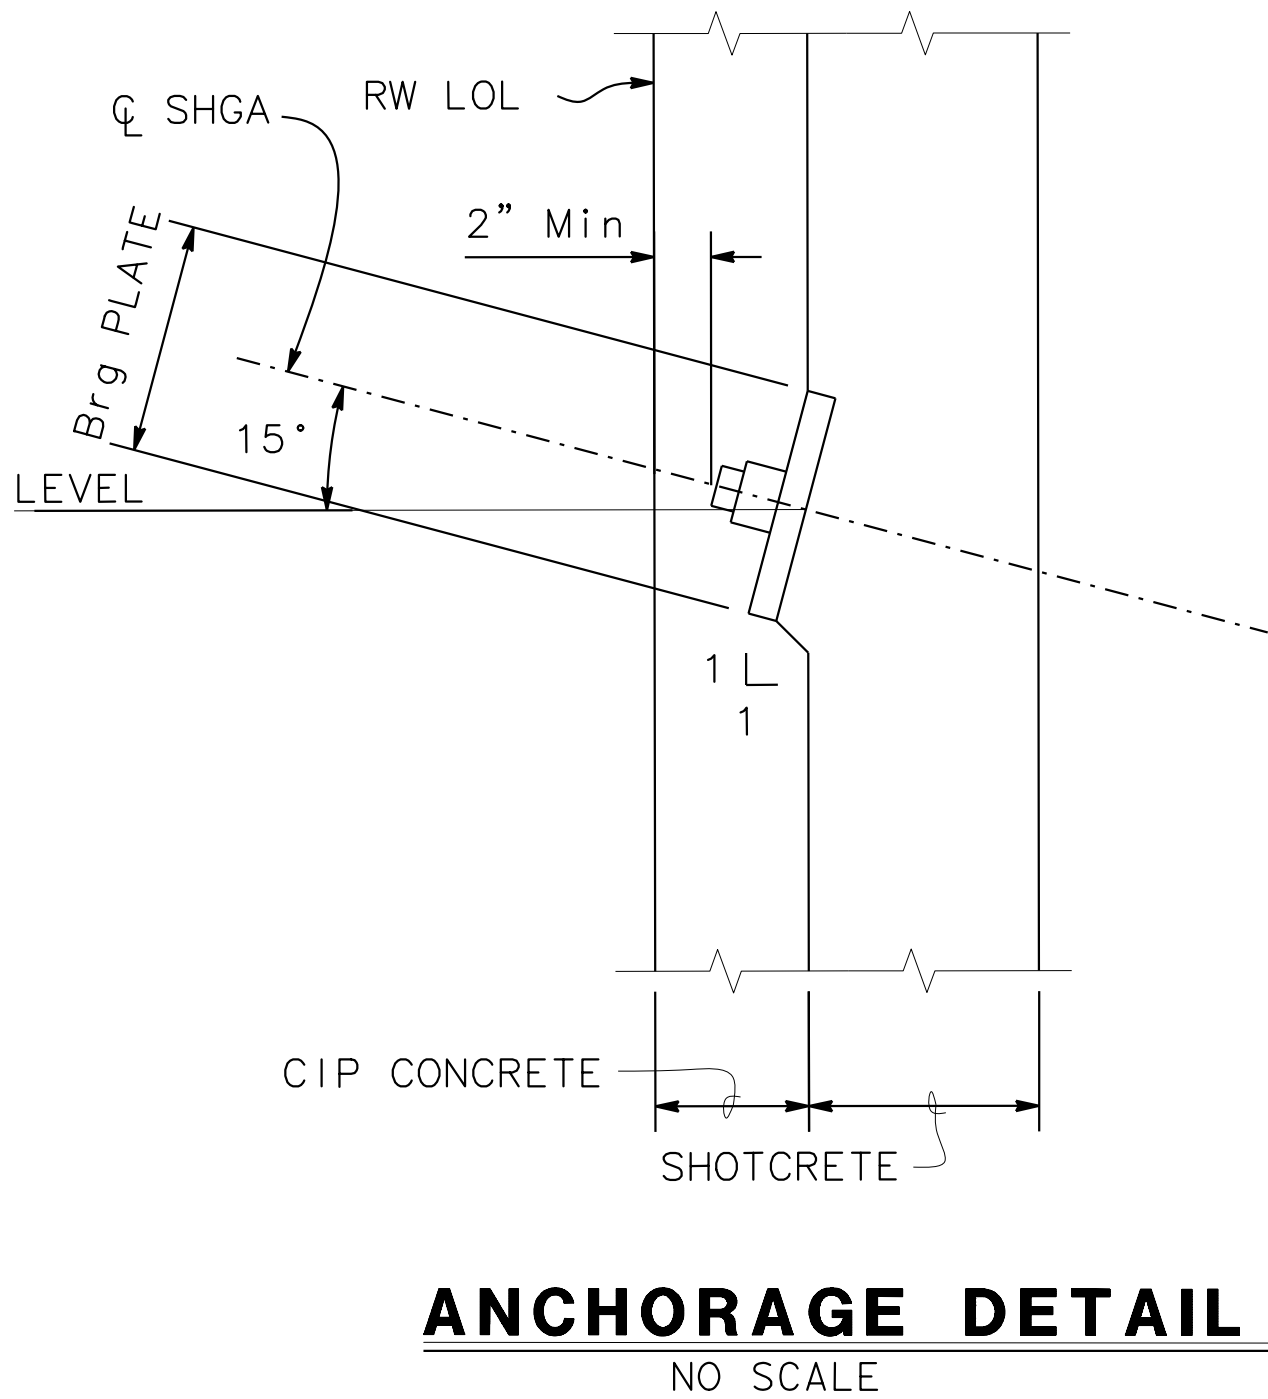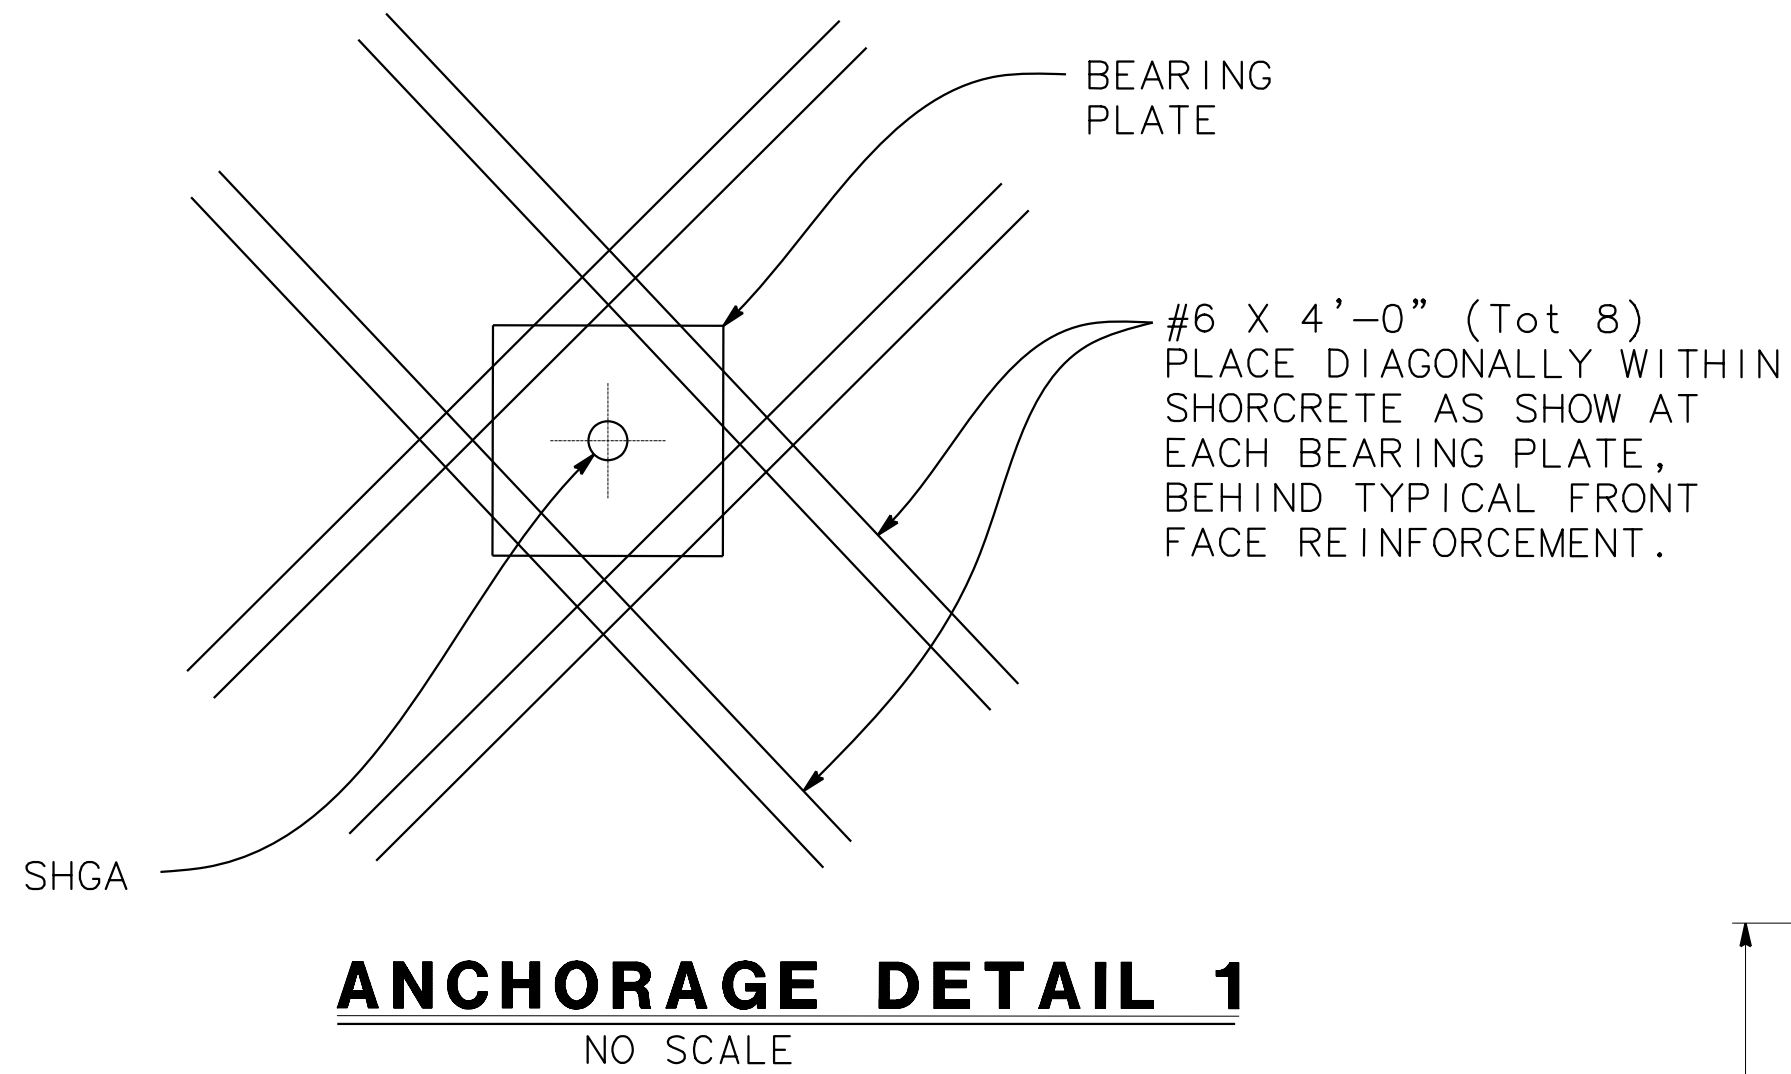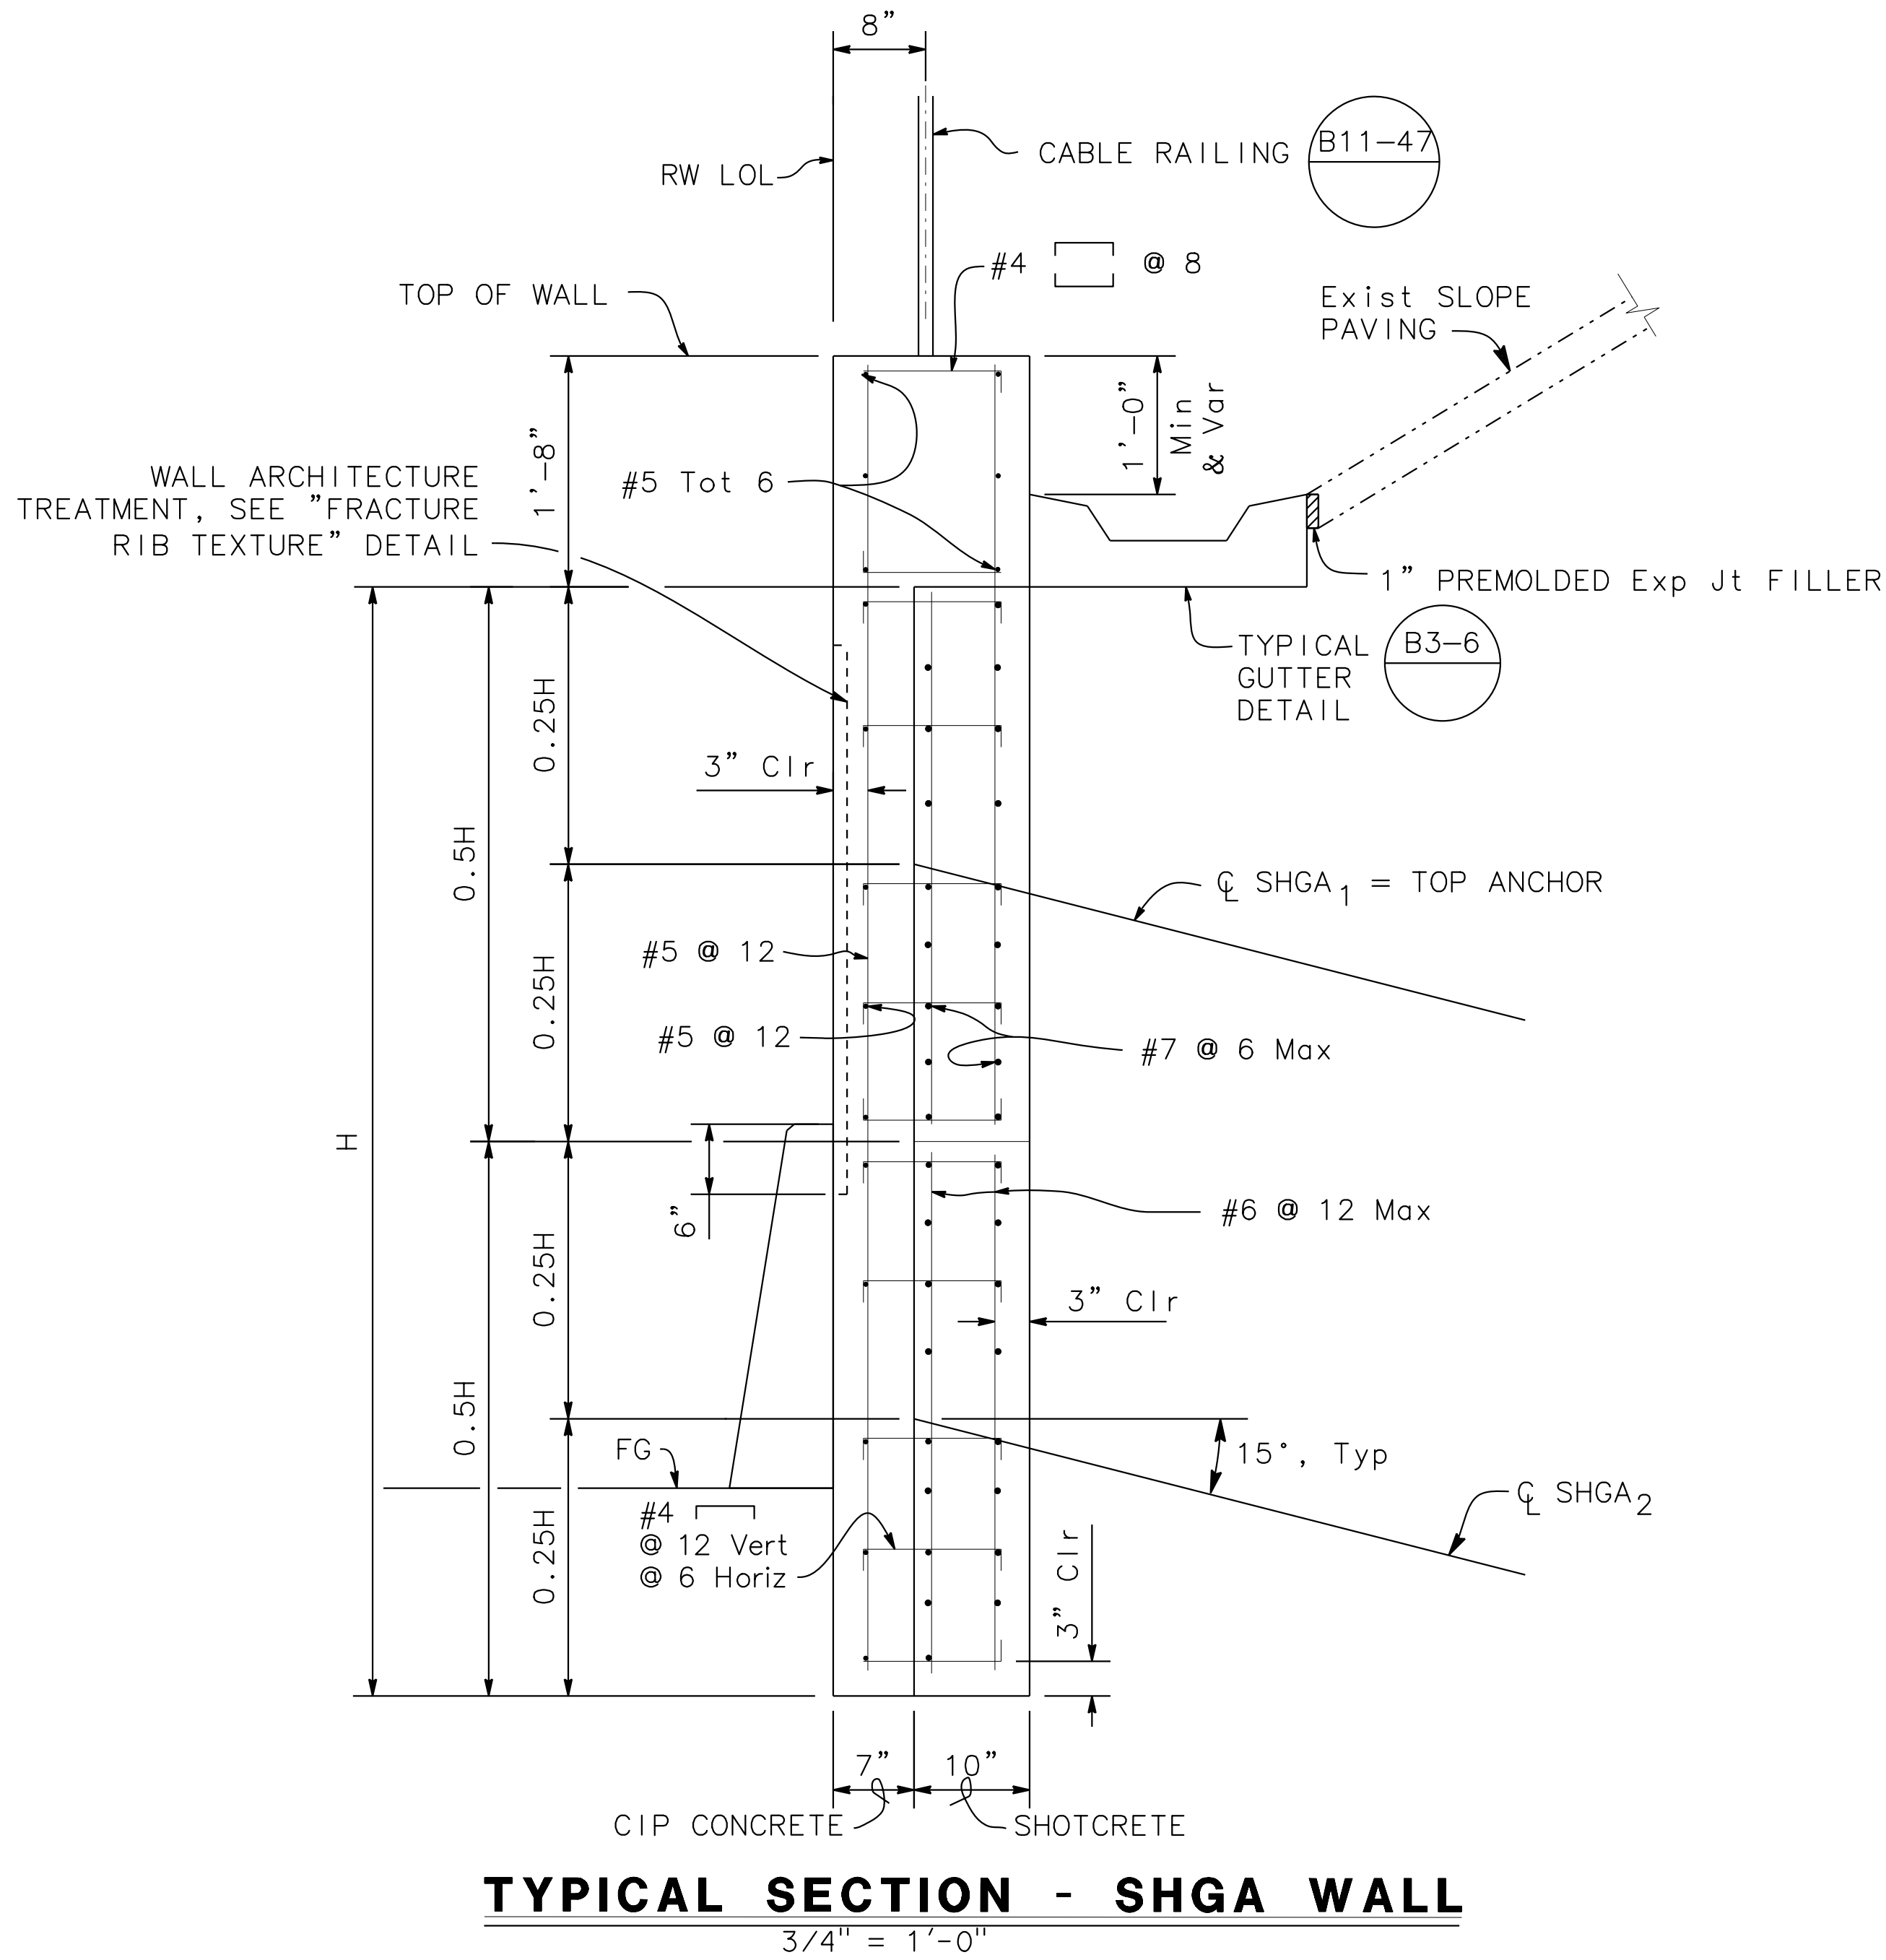

NOTE:
THE CONTRACTOR MUST VERIFY ALL CONTROLLING
DIMENSIONS BEFORE ORDERING OR FABRICATING
ANY MATERIAL.

100% SUBMITTAL

DESIGN OVERSIGHT		DESIGN	BY Y. REN	CHECKED J. SAMPSON	PREPARED FOR THE STATE OF CALIFORNIA DEPARTMENT OF TRANSPORTATION	JULIE PASSALACQUA PROJECT ENGINEER	BRIDGE No.	SANTIAGO ROAD OC RETAINING WALL							
		DETAILS	BY G. BOYKO	CHECKED J. SAMPSON			56E0210								
		QUANTITIES	BY K. WU	CHECKED A. CLUBB			POST MILE								
SIGN OFF DATE		DATE PLOTTED => 15-FEB-2022		TIME PLOTTED => 17:45	ORIGINAL SCALE IN INCHES FOR REDUCED PLANS		UNIT: PROJECT NUMBER & PHASE: 0820000074	CONTRACT No.: 08-1K402	DISREGARD PRINTS BEARING EARLIER REVISION DATES	REVISION DATES		SHEET	OF		
DESIGN DETAIL SHEET (ENGLISH) (REVISION 4/19/2018)		FILE => 06_TEM_RW1-det2.dgn		USERNAME => jvalenzuela		0 1 2 3				7/07/20				6	11

GENERAL NOTES

DESIGN:
AASHTO LRFD Bridge Design Specifications,
8th Edition with California Amendments.

PRESTRESSING STEEL:

Bars - ASTM Designation: A722 Type II (150 ksi)

Strand Tendons-ASTM Designation: A416
(270 Ksi Low Relaxation steel)


FTL = Factored Test Load per anchor (Kips)

f_{pu} = Minimum tensile strength of prestressing steel


As = Minimum cross sectional area of prestressing steel in ground anchor (square inch)

$$A_s(\text{Min}) = \frac{1.0 \text{ FTL}}{0.75 f_{pu}} \quad (\text{Strands})$$

$$A_s(\text{Min}) = \frac{1.0 \text{ FTL}}{0.80 f_{pu}} \text{ (Bars)}$$

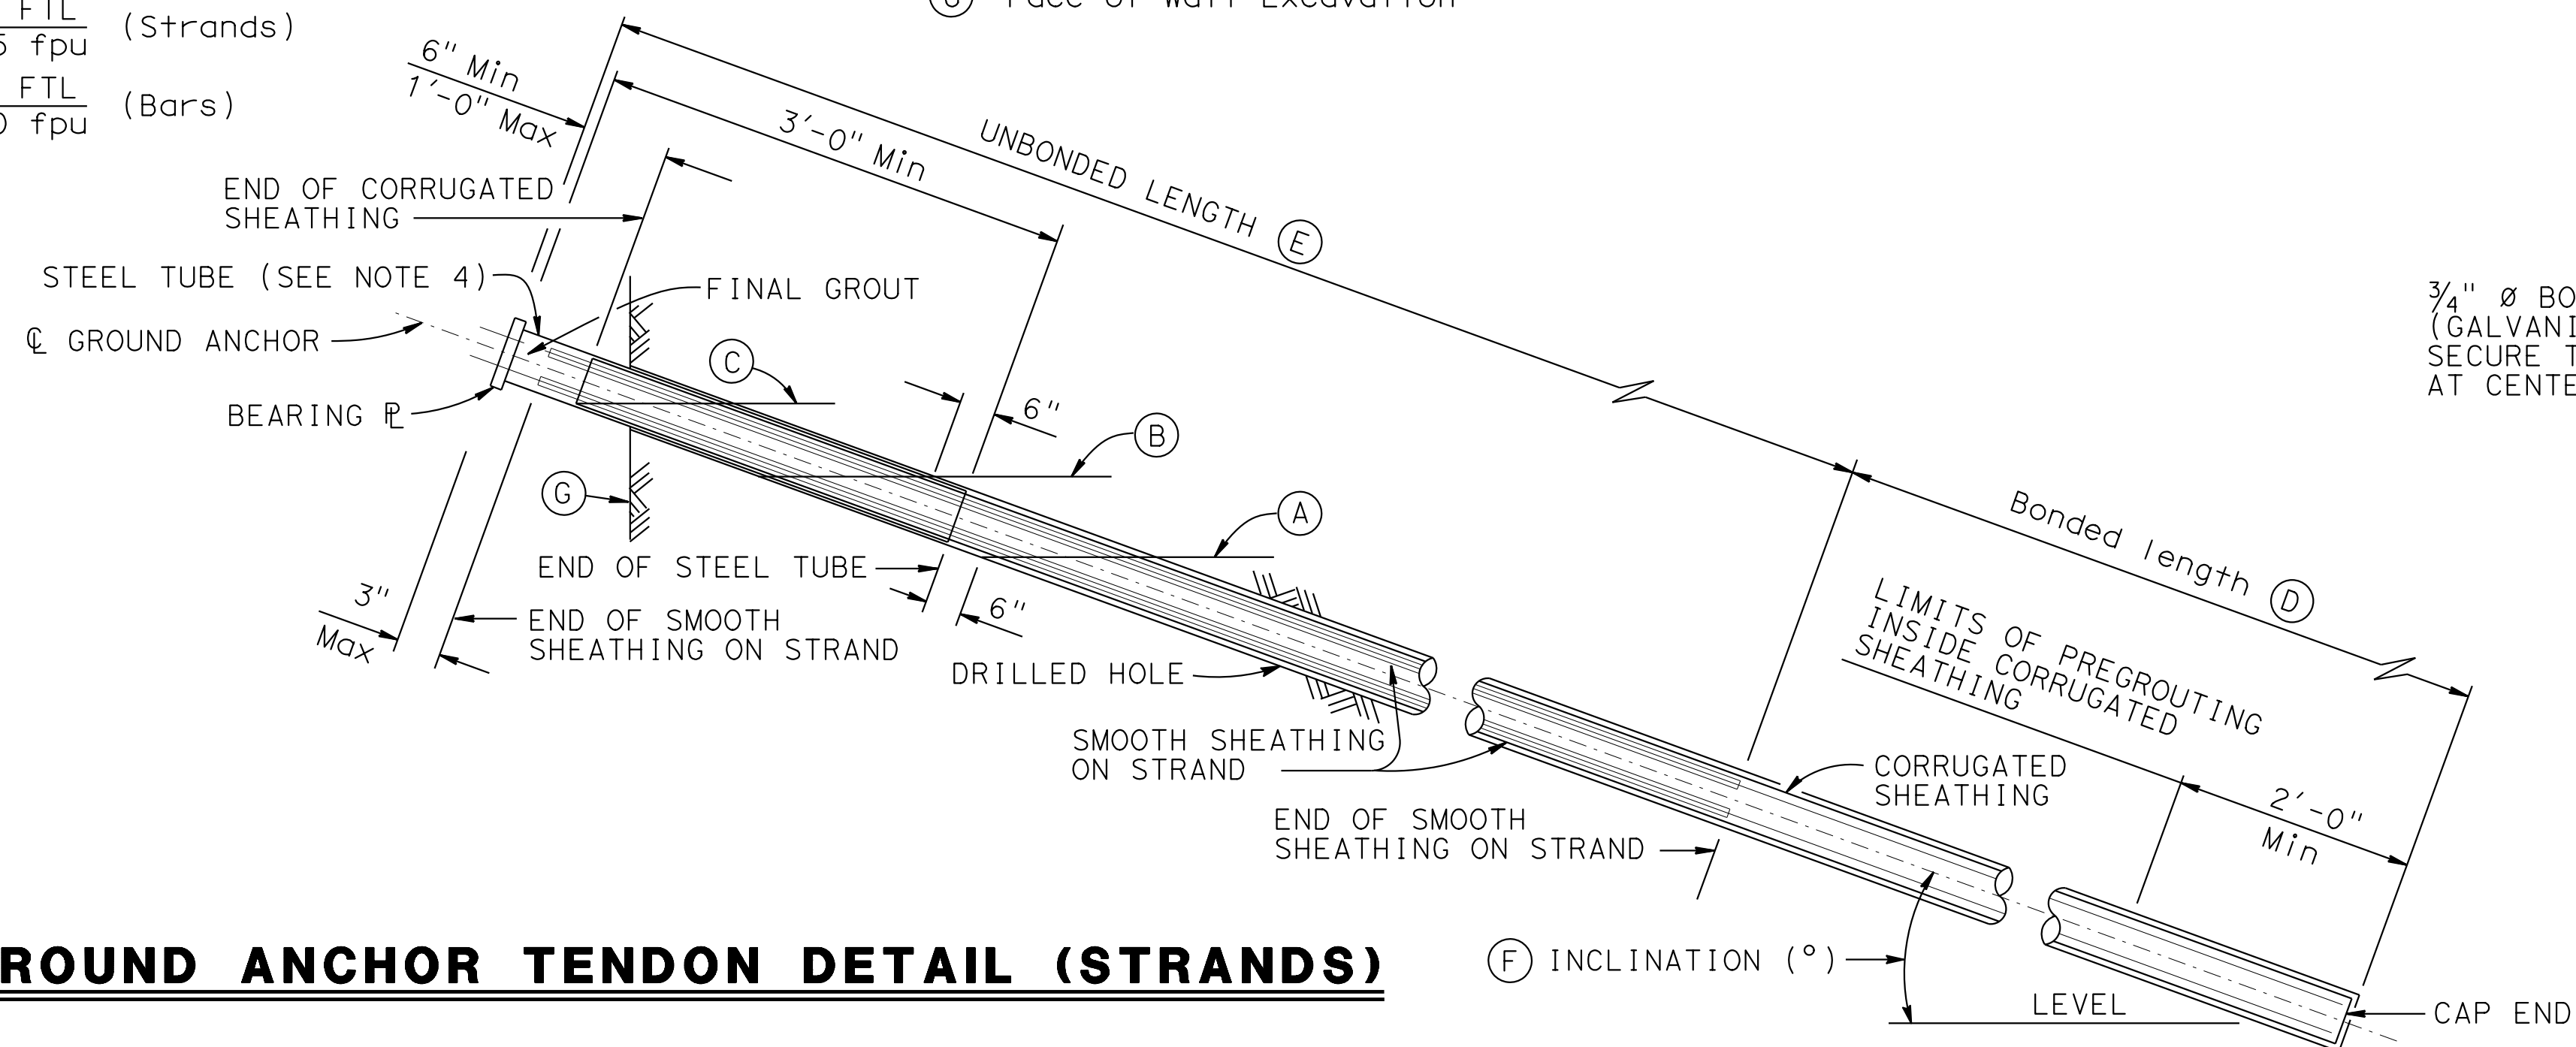

GROUND ANCHOR TENDON DETAIL (STRANDS)

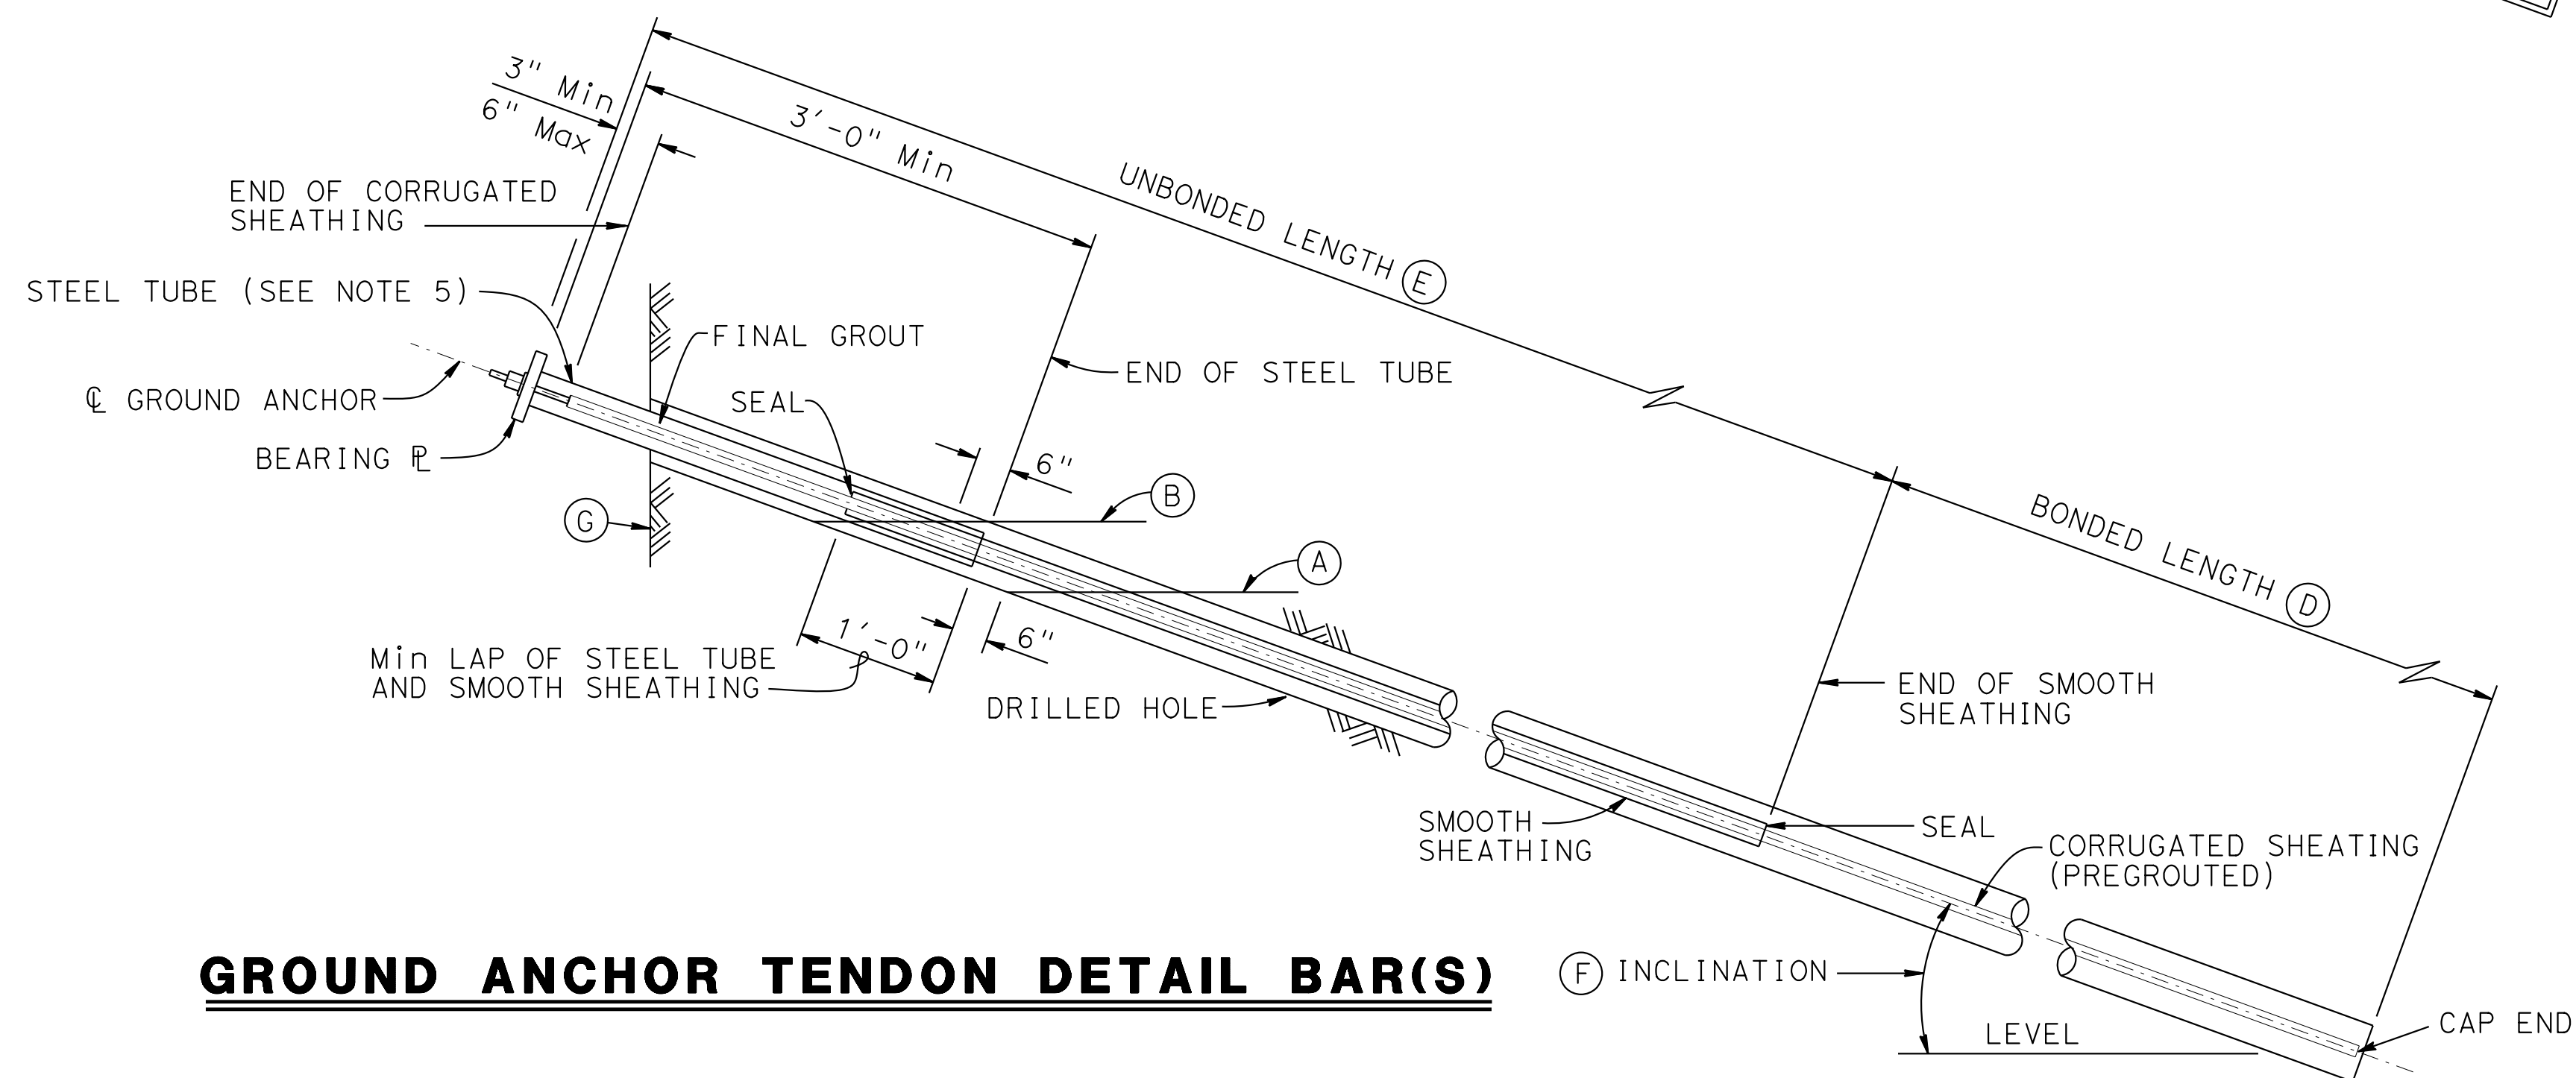


GROUND ANCHOR TENDON DETAIL BAR(S)

NOTES:


- (A) Level of initial grouting for drilled hole 6" in diameter or smaller
- (B) Level of secondary grouting
- (C) Level of initial grouting inside corrugated sheathing
- ① (D) Bonded length is 15'-0" minimum, to be determined by the contractor
- ① (E) Unbonded length = 27'-0"
- (F) For inclination, see PROJECT PLANS
- (G) Face of Wall Excavation

NOTES:

- ~~② 1. Anchorage enclosure shall only be used when anchor head assembly is not enclosed in concrete.~~
- ~~② 2. Anchorage enclosure shall have provisions to allow injecting grout at low end and venting at high end. Galvanize after fabrication.~~
- ~~② 3. Silicone sealant to cover full width of flange.~~
4. Steel tube (Min thickness = $\frac{1}{4}$ ") welded to bearing plate. Galvanize assembly after fabrication
5. Steel tube welded to bearing plate. Inside diameter of steel tube (Min thickness = $\frac{1}{4}$ ") to be 1" greater than outside diameter of smooth sheathing.
6. Galvanize assembly after fabrication.
7. For other wall details, see PROJECT PLANS.

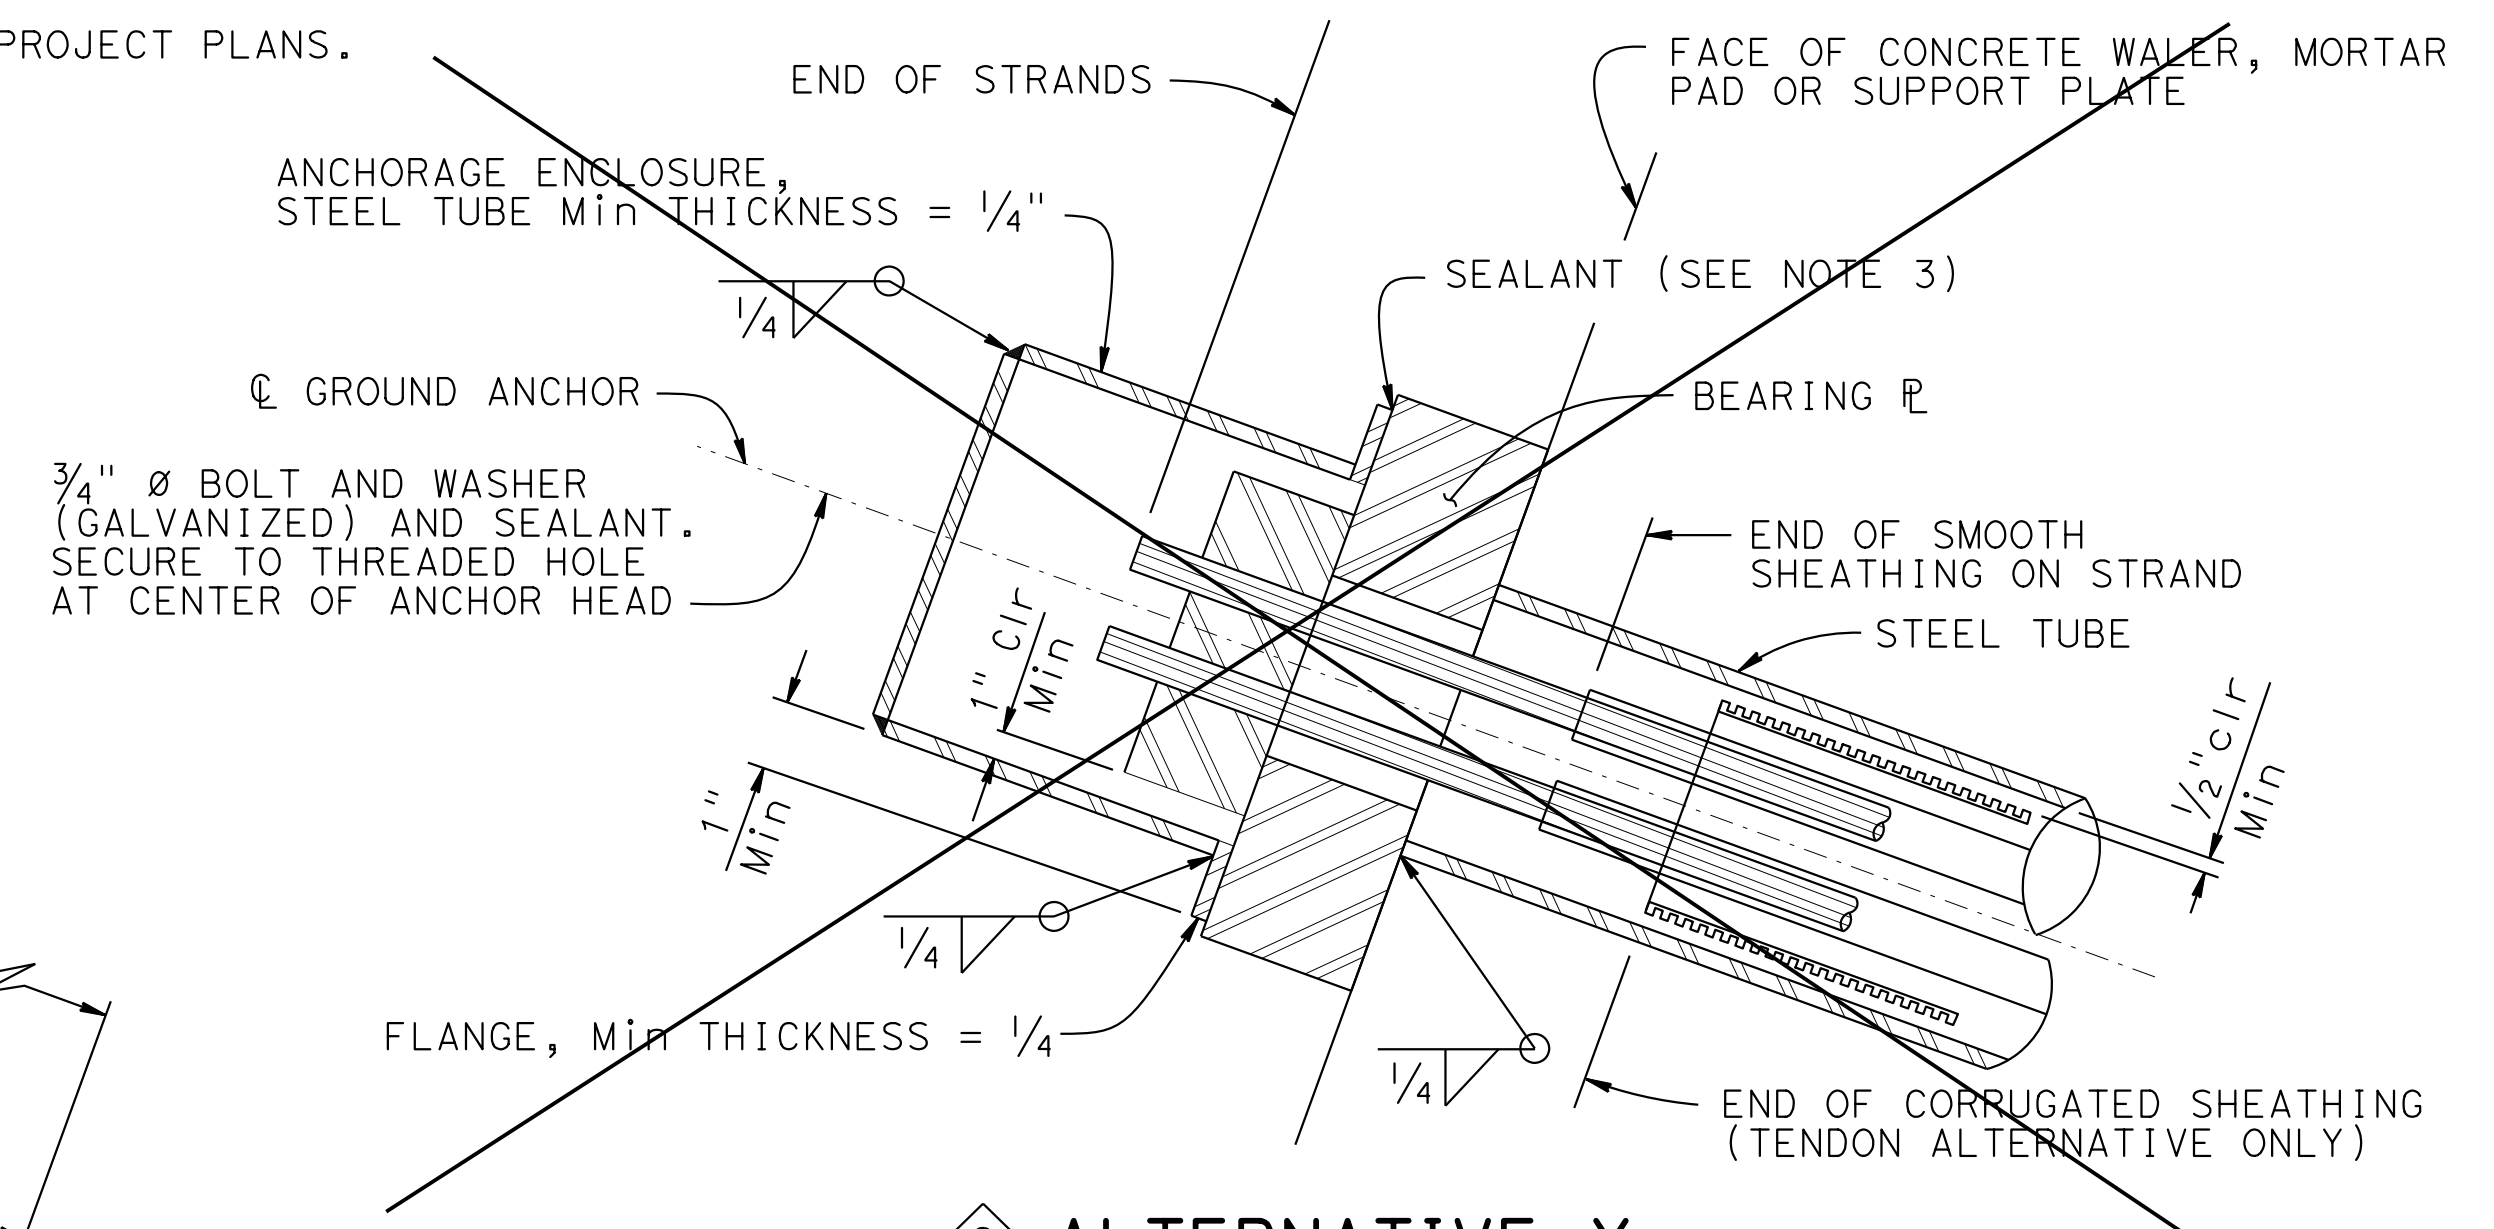

2 ALTERNATIVE X

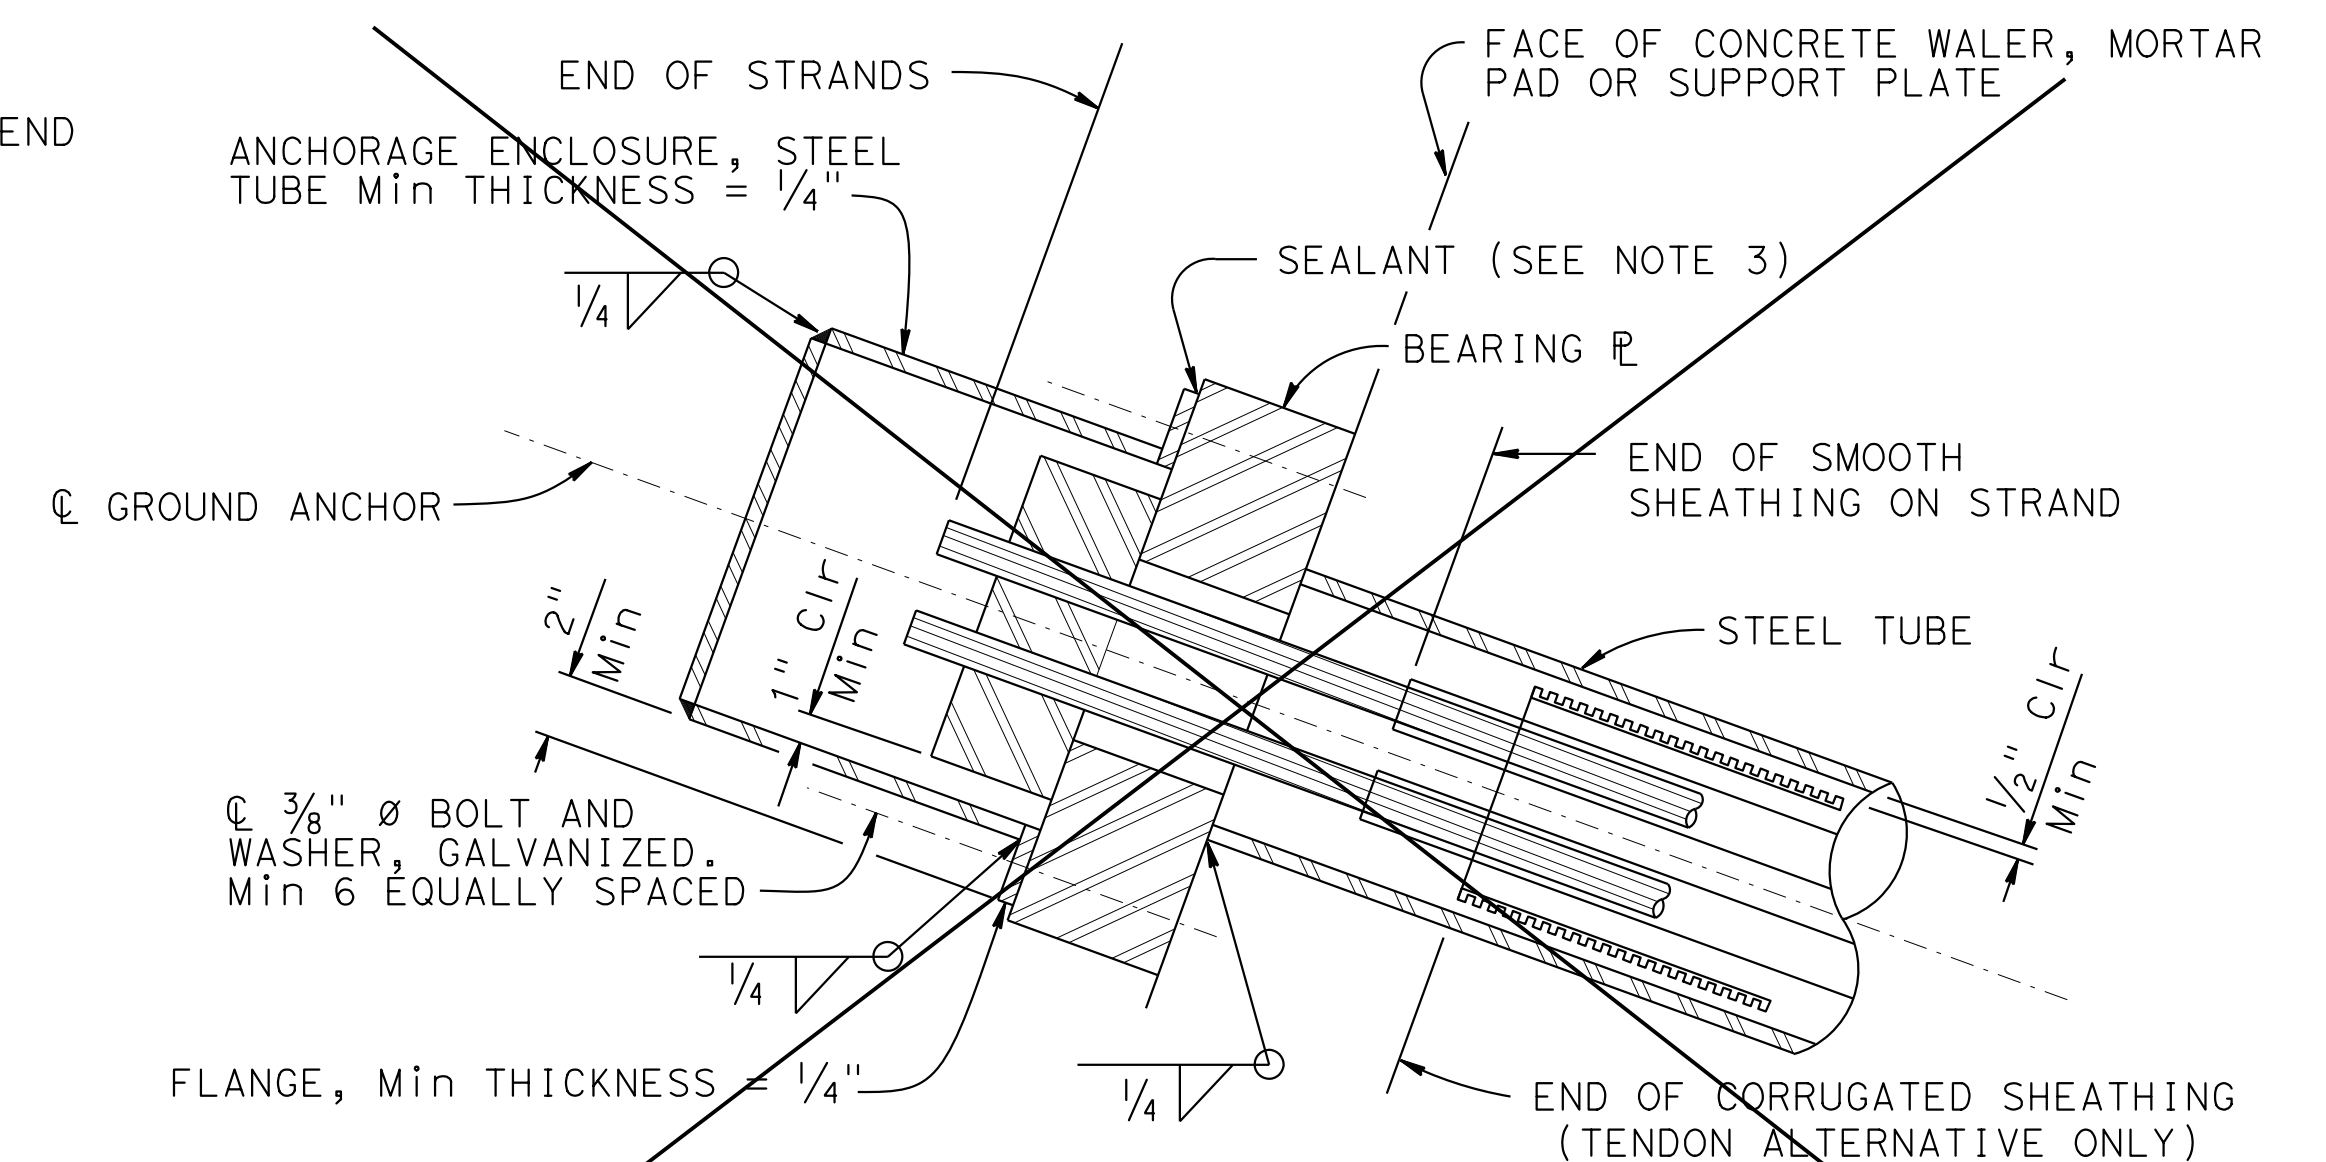

ALTERNATIVE Y

ANCHORAGE ENCLOSURE DETAILS

NO SCALE

100% SUBMITTAL

SPECIAL DETAILS

SANTIAGO ROAD OC RETAINING WALL

SUB HORIZONTAL GROUND ANCHOR DETAILS	
--------------------------------------	--

BRIDGE STANDARD DETAILS			MODIFICATION SHOWN:			STATE OF CALIFORNIA		DIVISION OF ENGINEERING SERVICES		SANTIAGO ROAD OC RETAINING WALL	
xs12-040		July 2014	The components of the Bridge Standard Details have been prepared under the responsible charge of the technical owner, a registered civil engineer in the State of California	① REVISED NOTE	② DOES NOT APPLY	DEPARTMENT OF TRANSPORTATION		BRIDGE NO.	56-NEW	SUB HORIZONTAL GROUND ANCHOR DETAILS	
FILE NO.	APPROVAL DATE	POST MILE		4.1							
Refer to: http://www.dot.ca.gov/hq/esc/techpubs/manual/bridgemanuals/bridge-standard-detail-sheets/index.html			FILE => 07_xs12-040.dgn USERNAME => jvalenzuela TIME PLOTTED => 17:45 DATE PLOTTED => 15-FEB-2022			ORIGINAL SCALE IN INCHES FOR REDUCED PLANS 0 1 2 3		UNIT: PROJECT NUMBER & PHASE: 0820000074		CONTRACT NO.: 08-1K402	
								DISREGARD PRINTS BEARING EARLIER REVISION DATES		REVISION DATES 6-24-14 7-18-16 7-23-21	
										SHEET	OF
										7	10

Dist	COUNTY	ROUTE	POST MILES TOTAL PROJECT	SHEET No.	TOTAL SHEETS
8	Riv	15	3.4/5.0		

REGISTERED STRUCTURAL ENGINEER DATE 4-22-2022


YING REN
No. 5786
Exp. 12-31-22
STRUCTURAL
STATE OF CALIFORNIA

PLANS APPROVAL DATE



THE STATE OF CALIFORNIA OR ITS OFFICERS OR AGENTS
SHALL NOT BE RESPONSIBLE FOR THE ACCURACY OR
COMPLETENESS OF SCANNED COPIES OF THIS PLAN SHEET.

MARK THOMAS
2121 ALTON PARKWAY, SUITE 210
IRVINE, CA 92606


CITY OF TEMECULA
41000 MAIN STREET
TEMECULA, CA 92590

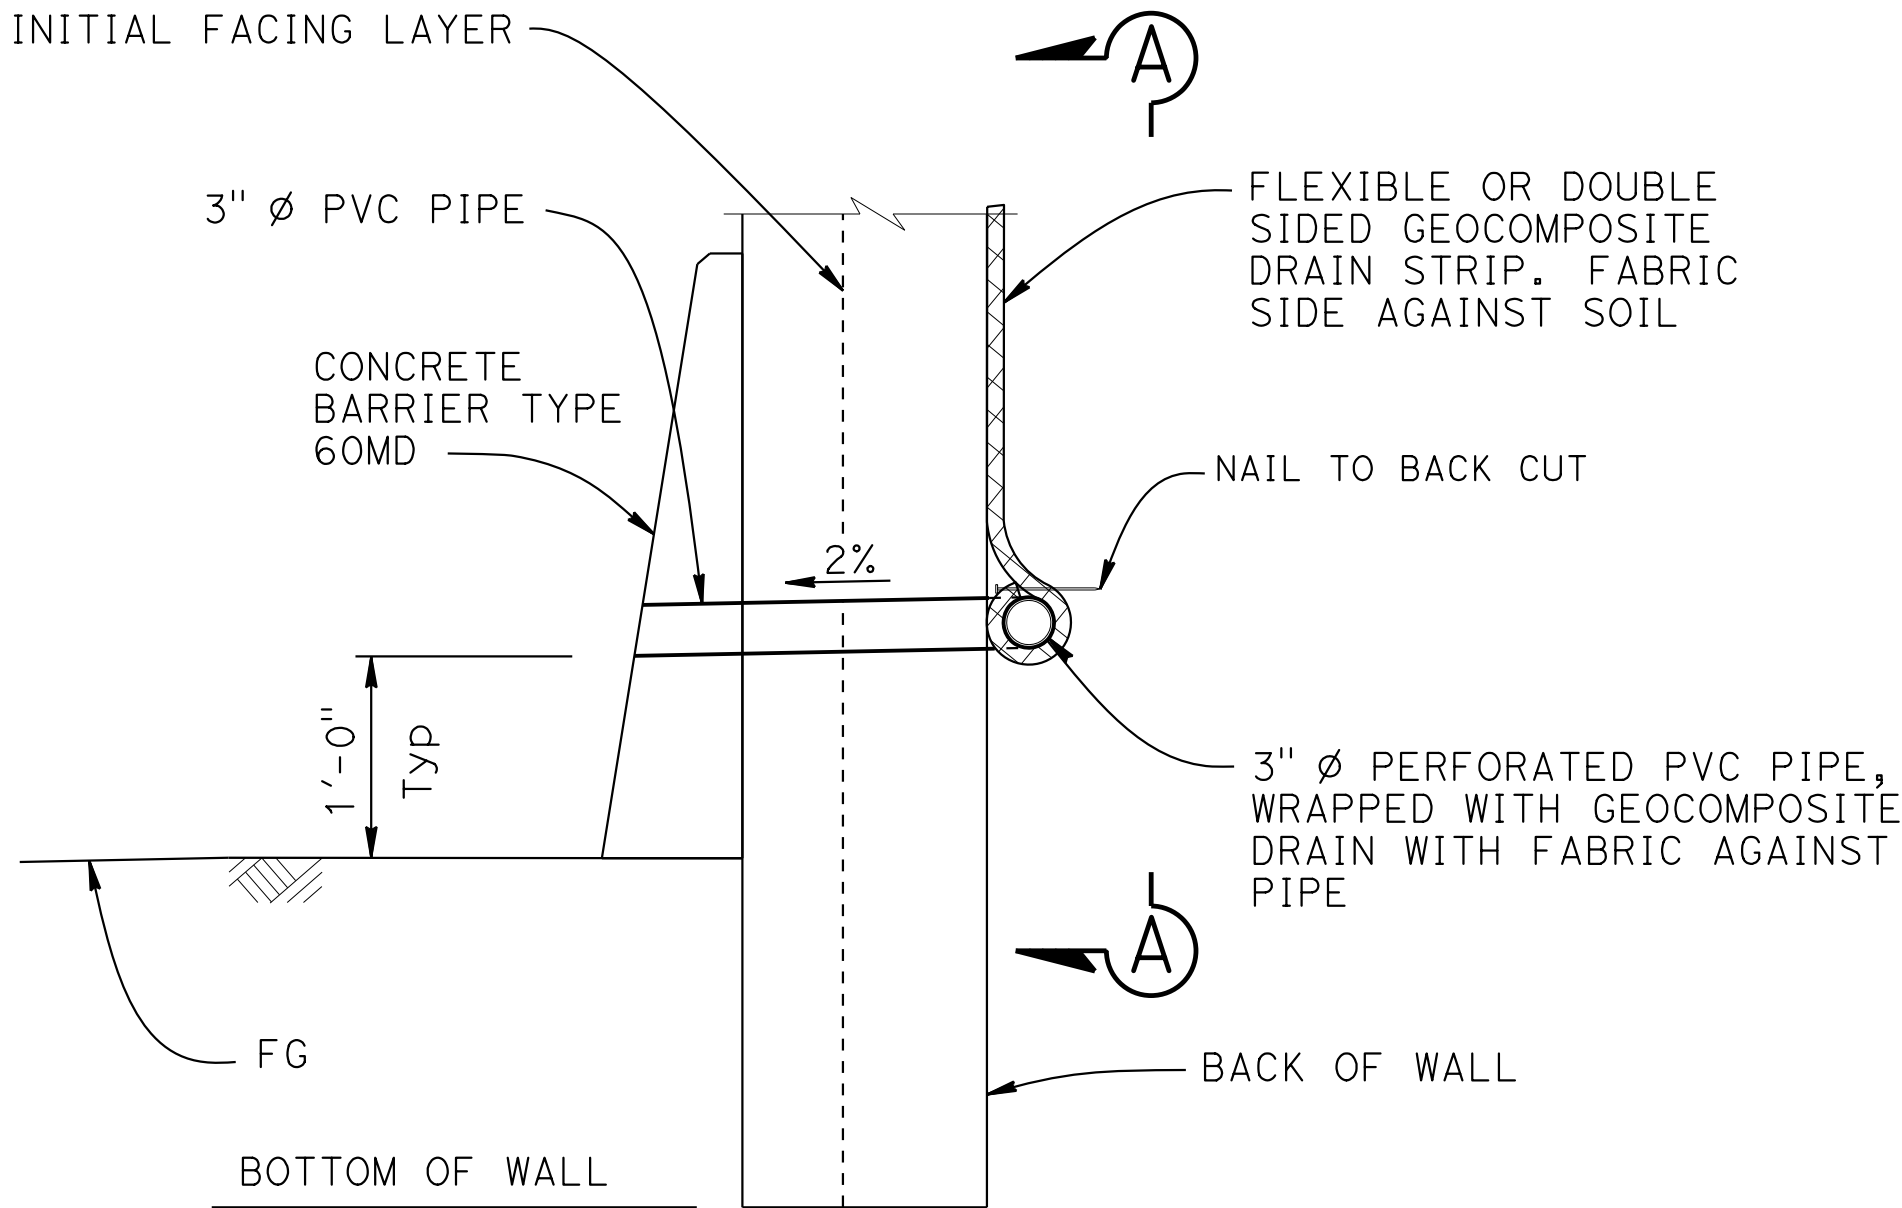


WALL DRAIN DETAIL AT WEEPHOLE
OPTION A
NO SCALE

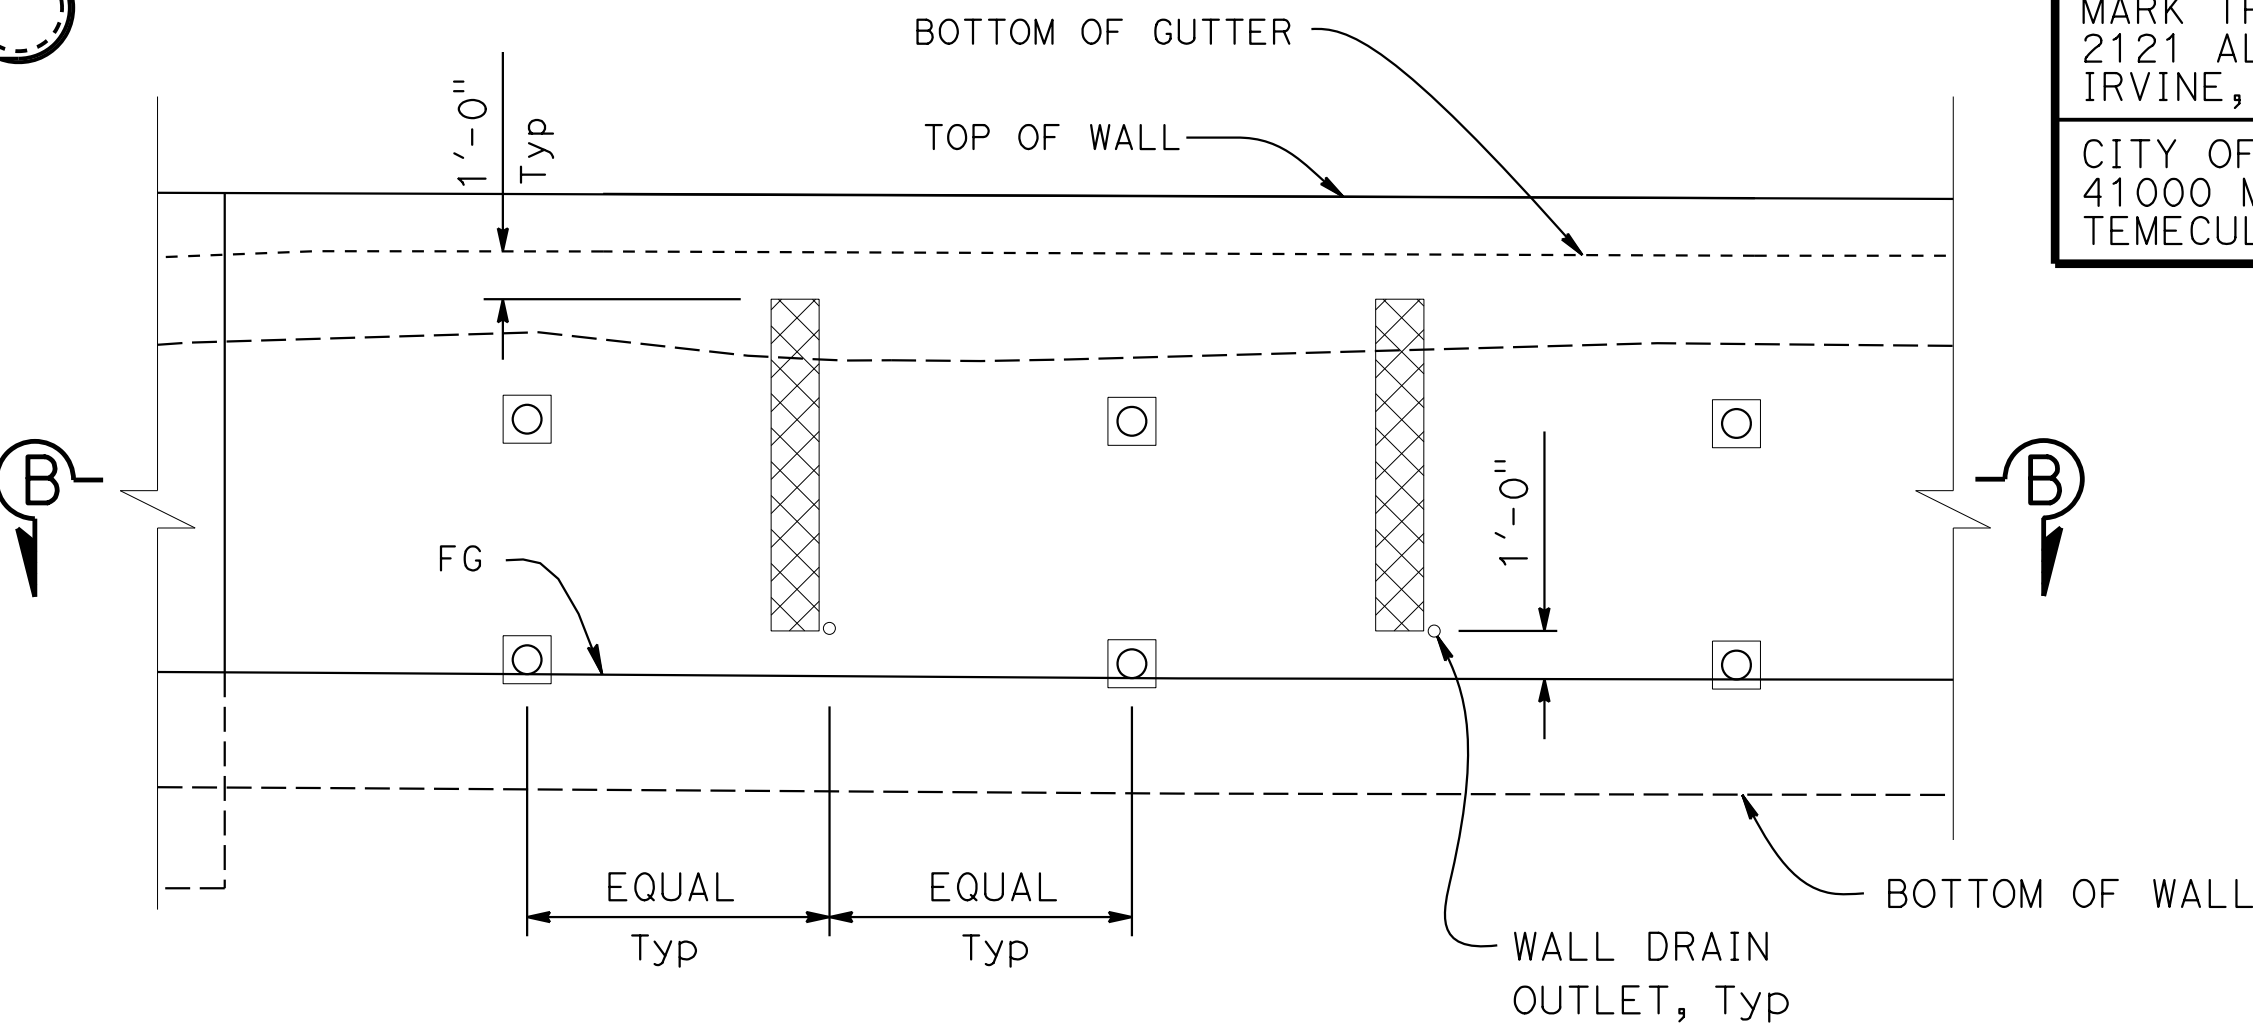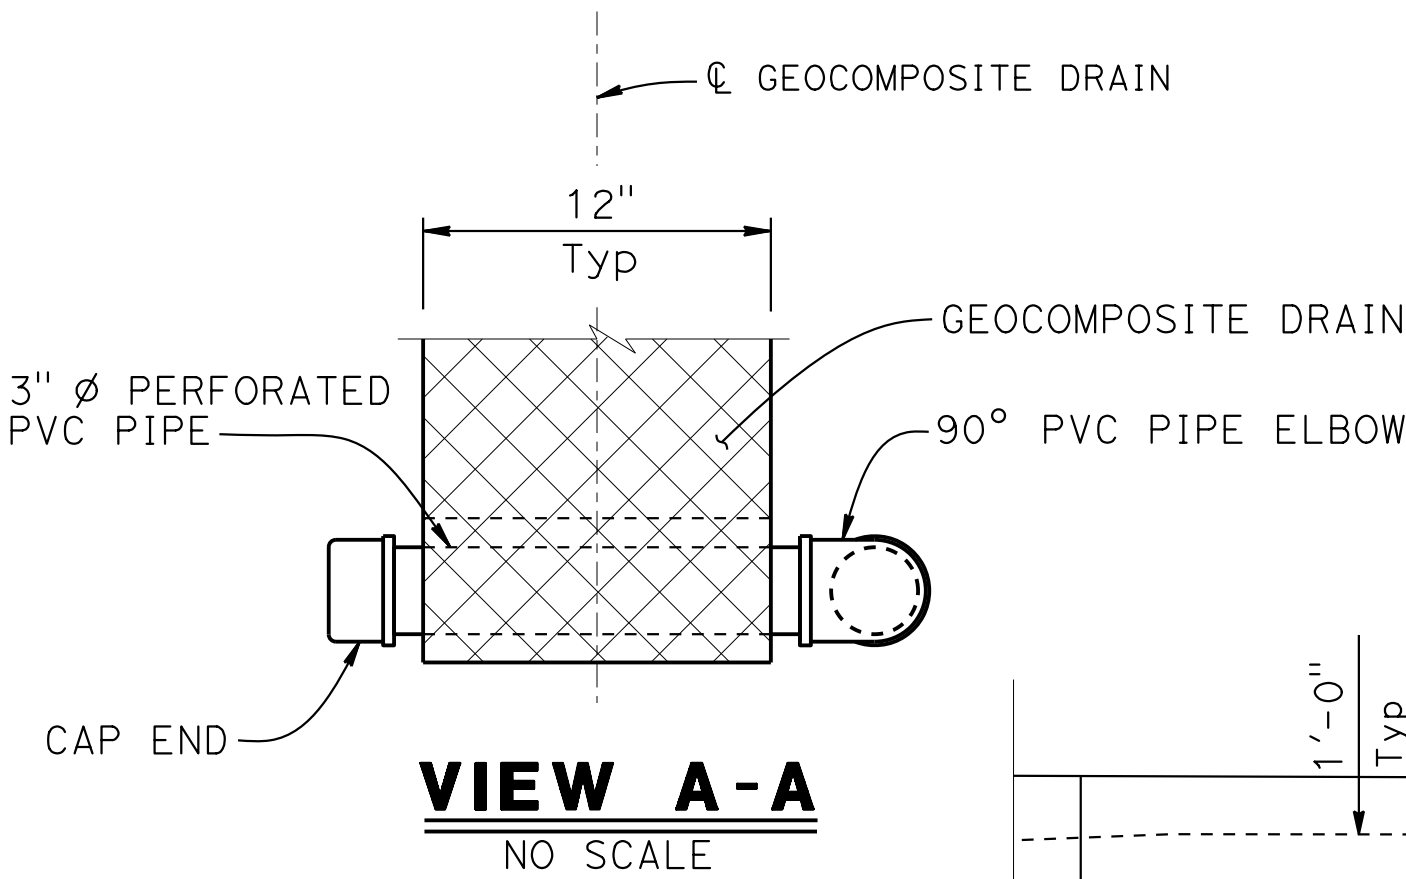

PART RETAINING WALL ELEVATION
1/4" = 1'-0"

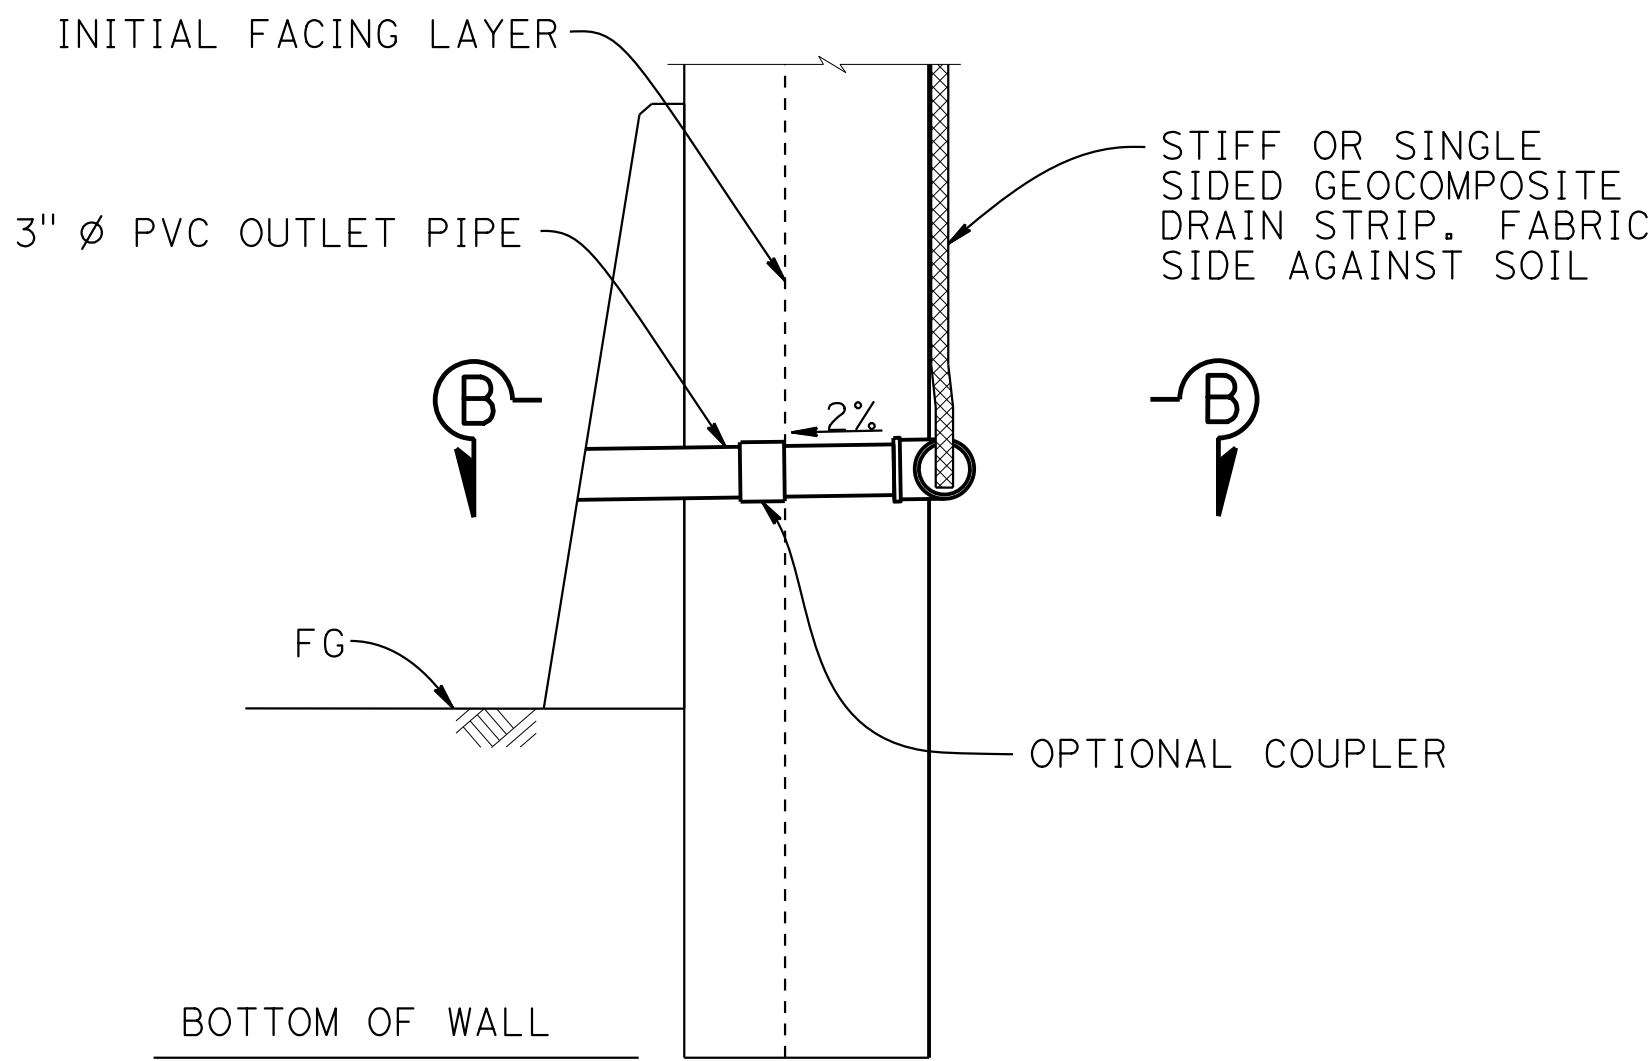

WALL DRAIN DETAIL AT WEEPHOLE
OPTION B
NO SCALE

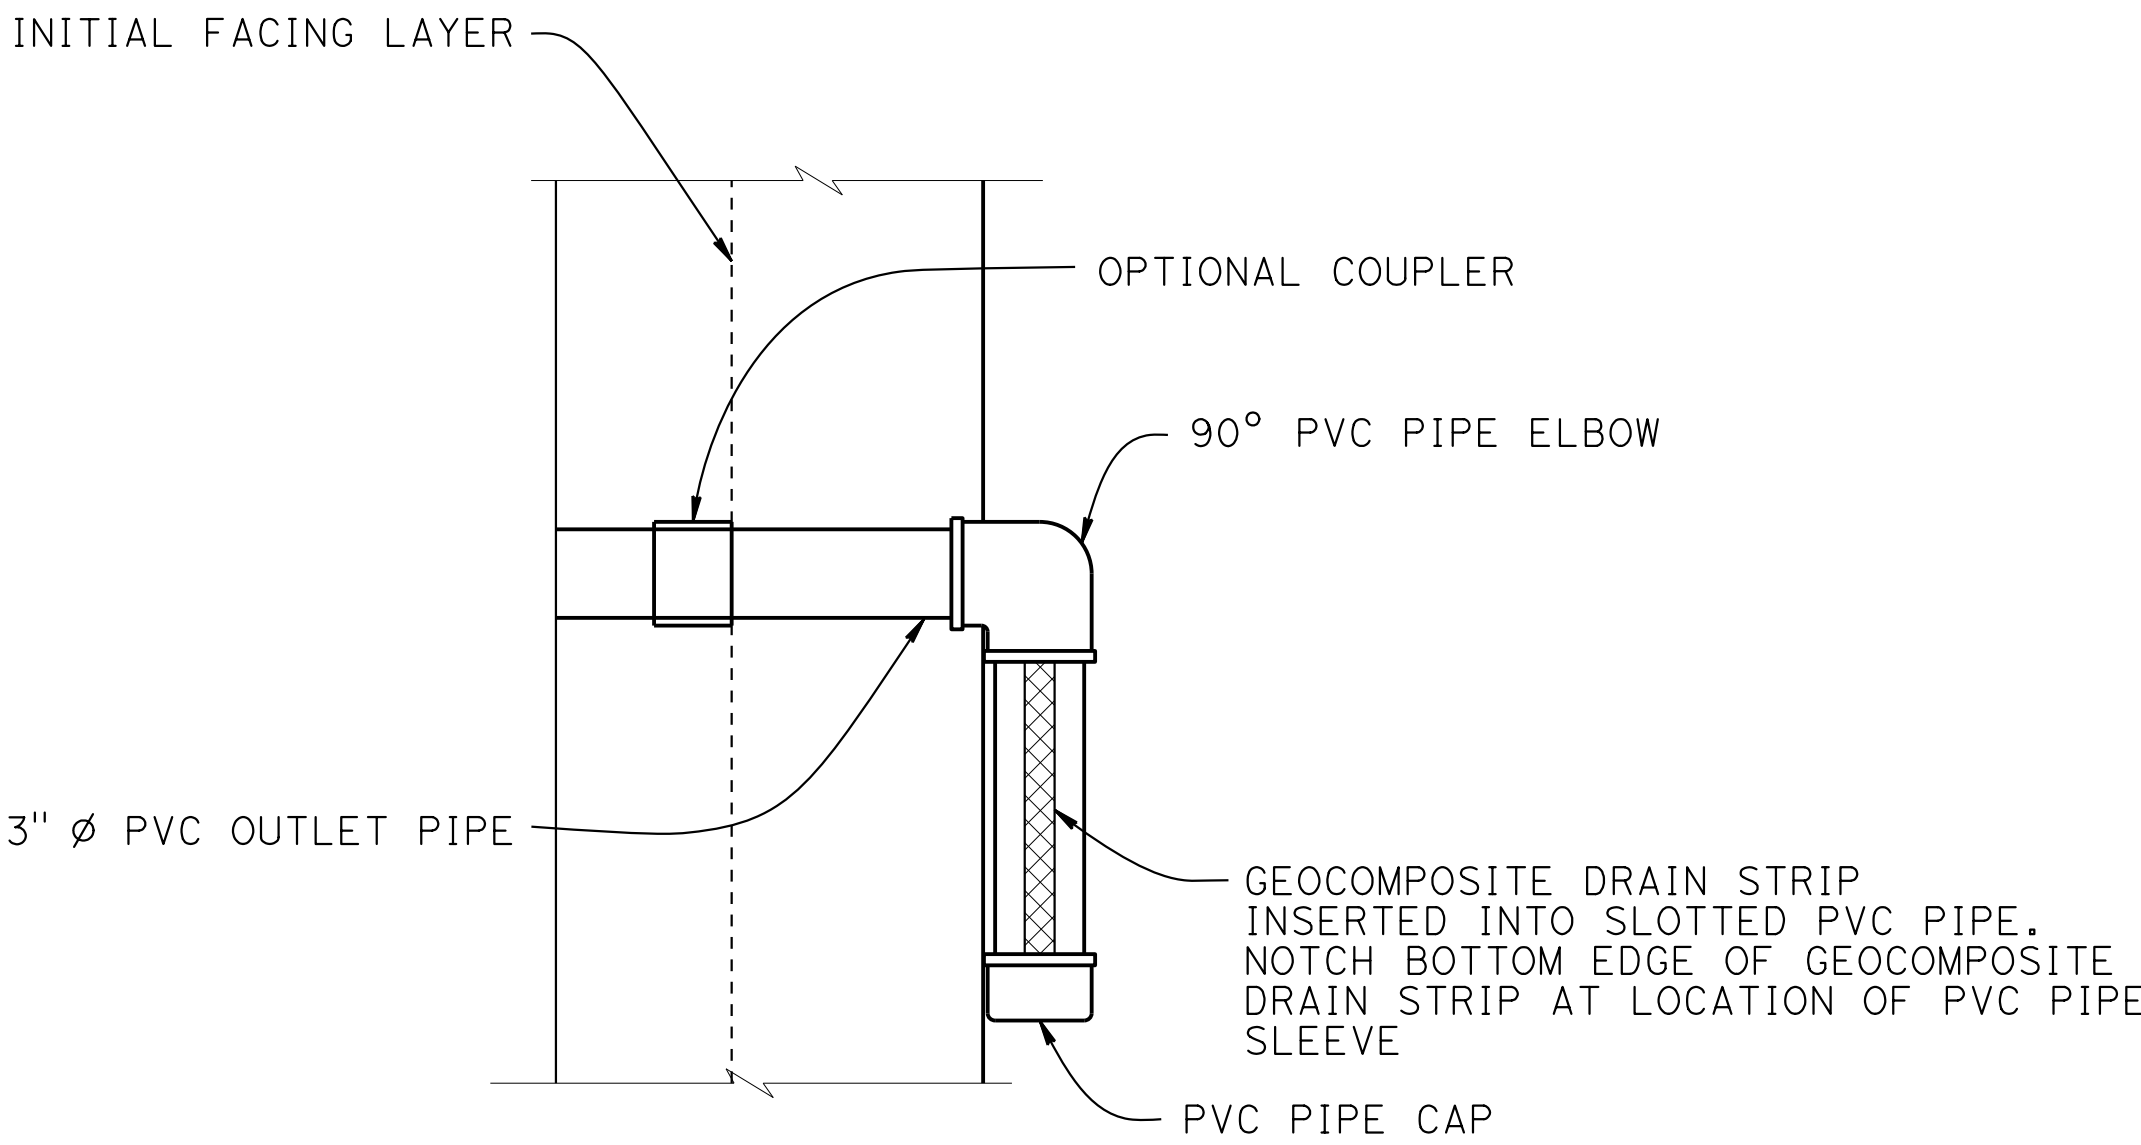

SECTION B-B
NO SCALE

NOTE:
THE CONTRACTOR MUST VERIFY ALL CONTROLLING
DIMENSIONS BEFORE ORDERING OR FABRICATING
ANY MATERIAL.

100% SUBMITTAL

		DESIGN		BY Y. REN	CHECKED J. SAMPSON	PREPARED FOR THE STATE OF CALIFORNIA DEPARTMENT OF TRANSPORTATION		JULIE PASSALACQUA PROJECT ENGINEER		BRIDGE No. 56E0210		SANTIAGO ROAD OC RETAINING WALL WALL DRAINAGE DETAILS											
DESIGN OVERSIGHT		DETAILS		BY G. BOYKO	CHECKED J. SAMPSON					POST MILE 4.1													
SIGN OFF DATE		QUANTITIES		BY K. WU	CHECKED A. CLUBB																		
DESIGN DETAIL SHEET (ENGLISH) (REVISION 4/19/2018)		DATE PLOTTED => 15-FEB-2022 FILE => 08_TEM_RW1-wd01.dgn		TIME PLOTTED => 17:45 USERNAME => jvalenzuela		ORIGINAL SCALE IN INCHES FOR REDUCED PLANS		0	1	2	3	UNIT: PROJECT NUMBER & PHASE: 0820000074		CONTRACT No.: 08-1K402		DISREGARD PRINTS BEARING EARLIER REVISION DATES		REVISION DATES		SHEET 8		OF 11	
																7/07/20							

Dist	COUNTY	ROUTE	POST MILES TOTAL PROJECT	SHEET No.	TOTAL SHEETS
8	Riv	15	3.4/5.0		



4-22-2022



REGISTERED STRUCTURAL ENGINEER DATE _____

PLANS APPROVAL DATE _____

YING REN

No. 5786

Exp. 12-31-22


STRUCTURAL

STATE OF CALIFORNIA

THE STATE OF CALIFORNIA OR ITS OFFICERS OR AGENTS
SHALL NOT BE RESPONSIBLE FOR THE ACCURACY OR
COMPLETENESS OF SCANNED COPIES OF THIS PLAN SHEET.

MARK THOMAS
2121 ALTON PARKWAY, SUITE 210
IRVINE, CA 92606

CITY OF TEMECULA
41000 MAIN STREET
TEMECULA, CA 92590

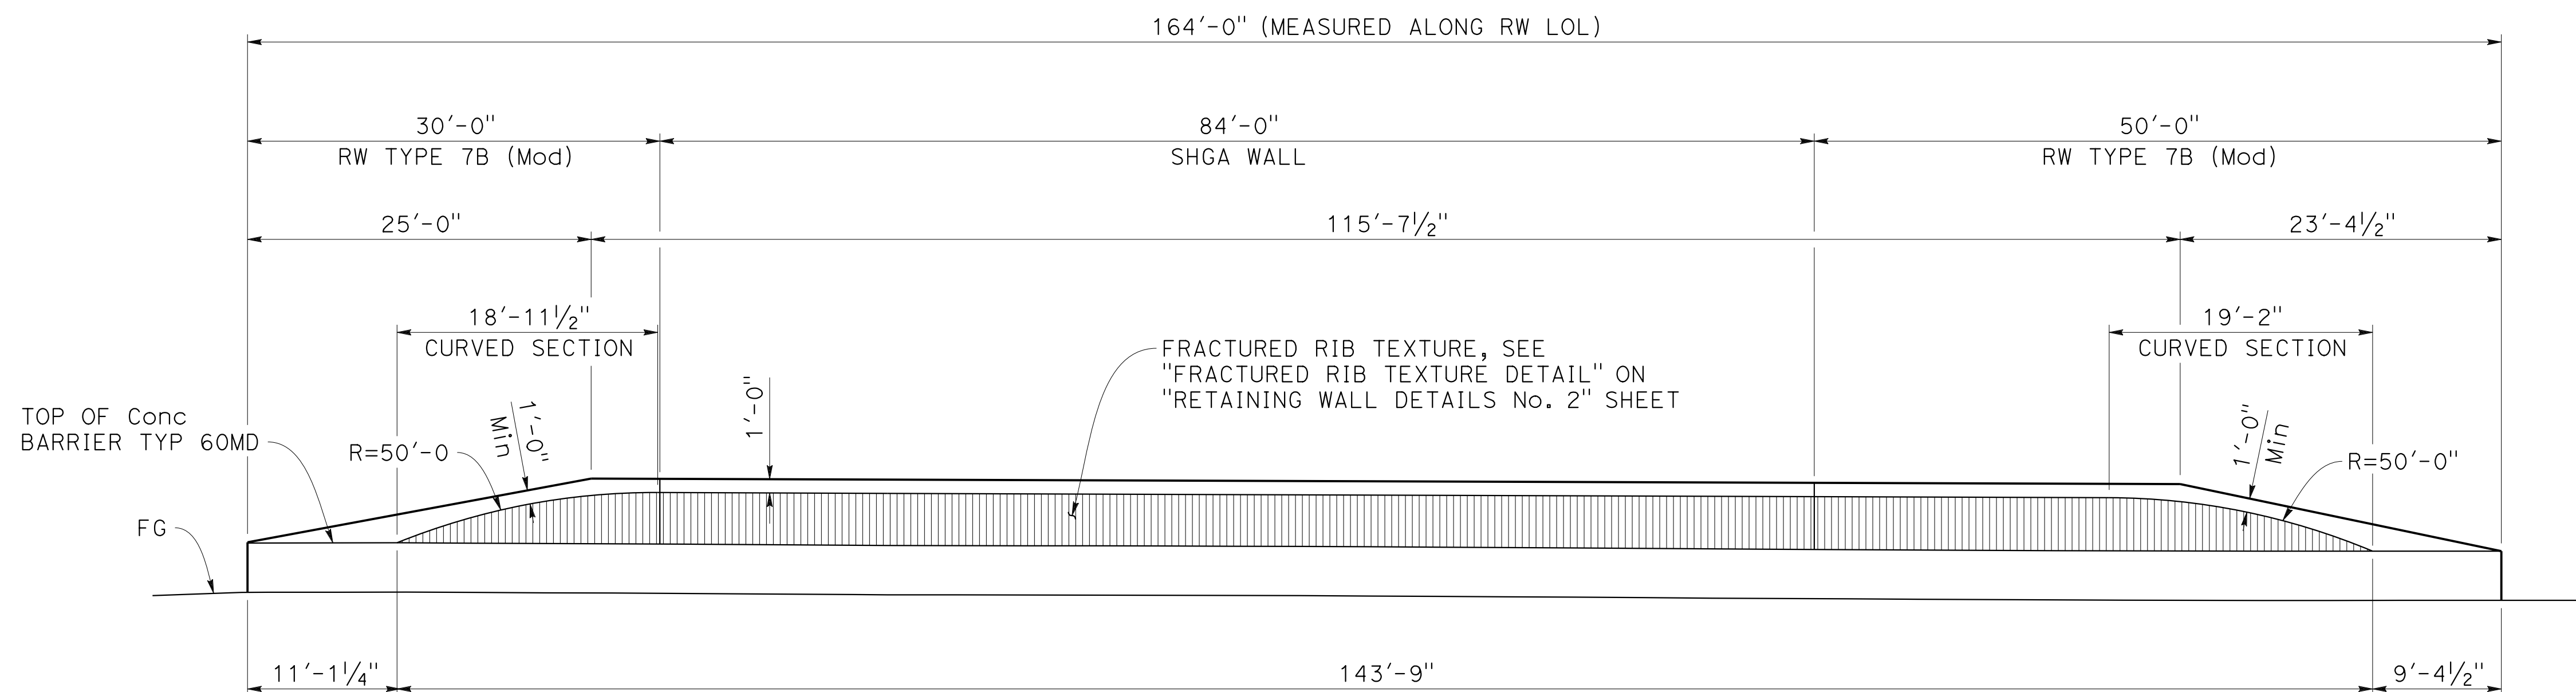

ELEVATION - ARCHITECTURAL TREATMENT

$$\frac{1}{8}'' = 1' - 0''$$

NOTE:
THE CONTRACTOR MUST VERIFY ALL CONTROLLING
DIMENSIONS BEFORE ORDERING OR FABRICATING
ANY MATERIAL.

100% SUBMITTAL

DESIGN OVERSIGHT		DESIGN BY Y. REN	CHECKED J. SAMPSON	PREPARED FOR THE STATE OF CALIFORNIA DEPARTMENT OF TRANSPORTATION		JULIE PASSALACQUA PROJECT ENGINEER		BRIDGE No. 56E0210	SANTIAGO ROAD OC RETAINING WALL																						
		DETAILS BY G. BOYKO	CHECKED J. SAMPSON					POST MILE 4.1	ARCHITECTURAL TREATMENT DETAIL																						
SIGN OFF DATE		QUANTITIES BY K. WU	CHECKED A. CLUBB																												
DESIGN DETAIL SHEET (ENGLISH) (REVISION 4/19/2018)				DATE PLOTTED => 15-FEB-2022 FILE => 09_TEM_RW1-miscdt01.dgn		TIME PLOTTED => 17:45 USERNAME => jvalenzuela		ORIGINAL SCALE IN INCHES FOR REDUCED PLANS		0		1		2		3		UNIT: PROJECT NUMBER & PHASE: 0820000074		CONTRACT No.: 08-1K402		DISREGARD PRINTS BEARING EARLIER REVISION DATES		7/07/20		REVISION DATES		SHEET 9		OF 11	

BENCH MARK:

Elevations shown are based on the North American Vertical Datum of 1988 (NAVD88).
The Caltrans 6033-01 Control Datasheet elevation at the following Benchmark was used:

Designation	Elevation
RIV 79 -19.3	1001.16

The Basis of Bearings for this survey is based on the California Coordinate System (CCS83), Zone VI, NAD83 (NSRS2007, Epoch 2007.00)

NOTES:

- (1) This LOTB sheet (Boring Record) was prepared in accordance with Caltrans Soil and Rock Logging, Classification and Presentation Manual (2010).
- (2) 1.4" samples were taken using a Standard Penetration Sampler and 2.4" samples were taken using a California Modified Sampler.
- (3) An automatic trip hammer system consisting of a hammer weight of 140 lbs falling a distance of 30" was used to advance the samplers.
- (4) For Soil Legend, see Caltrans Standard Plans A100 and A100.

RW LOL 9+91.08=
92.81' R+ "A" 213+41.08 BEGIN RW

A-20-003

8

8


A-20-002

PLAN

1"=20'

A-20-002

A-20-001

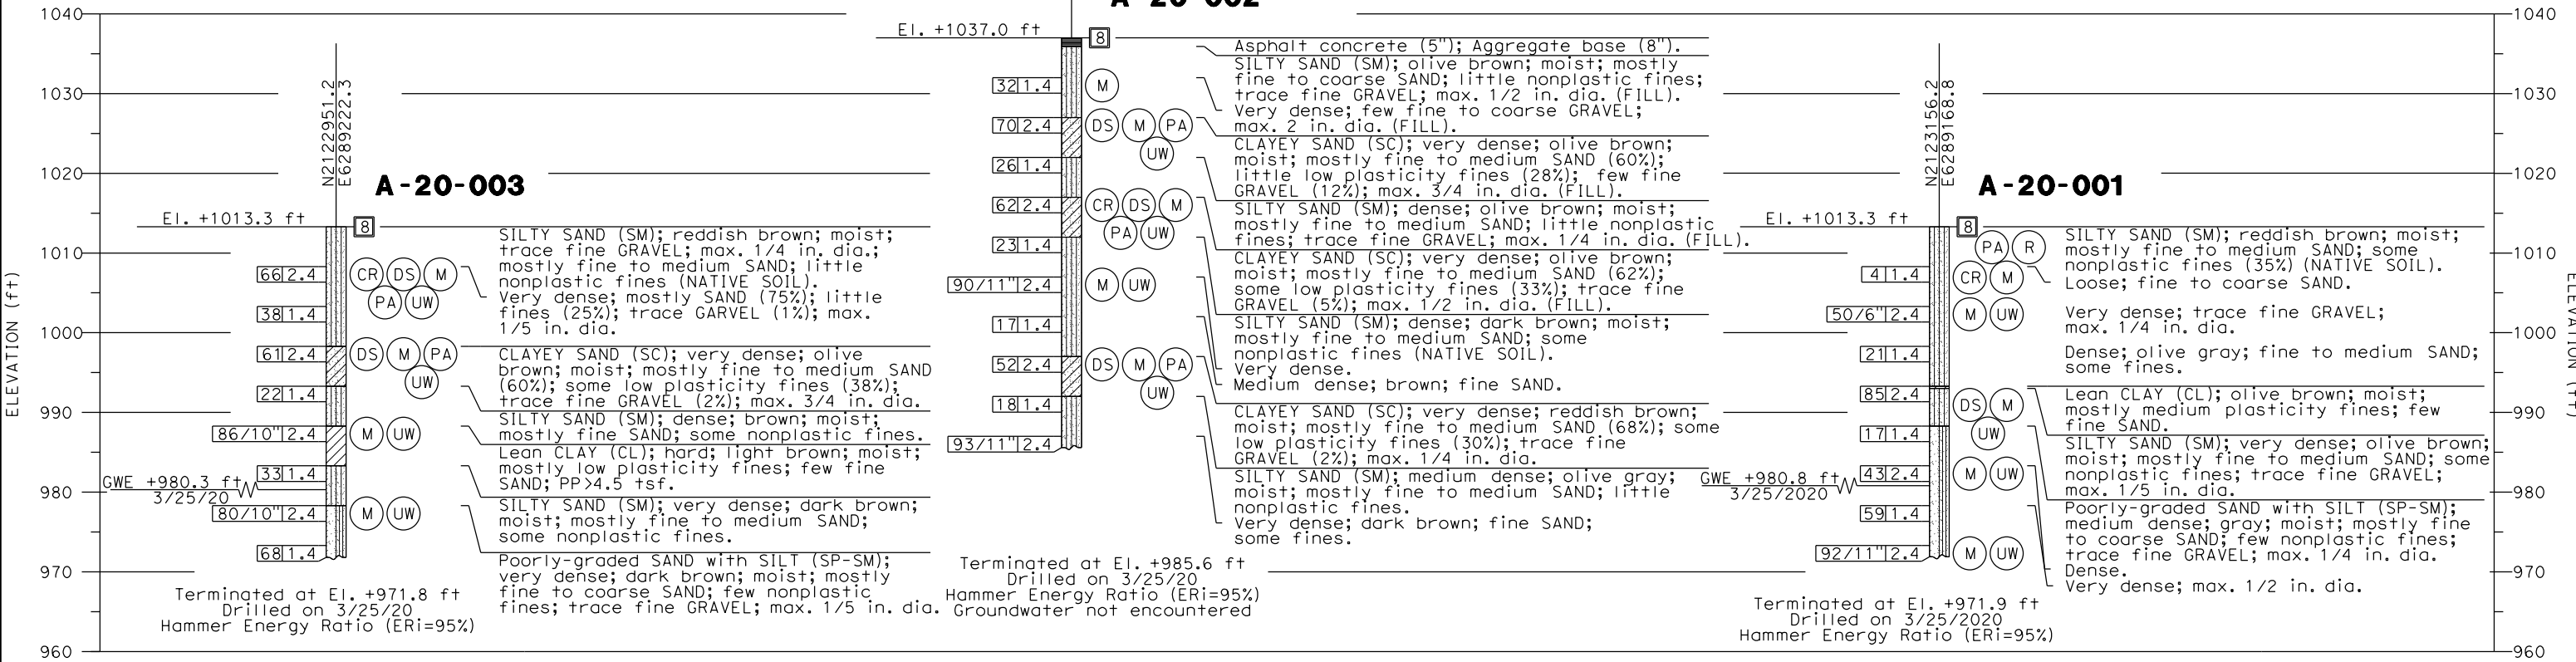


X DESIGN OVERSIGHT		DRAWN P.RAGAVAN	BY P.RAGAVAN FIELD INVESTIGATOR	PREPARED FOR THE STATE OF CALIFORNIA DEPARTMENT OF TRANSPORTATION		BRIDGE No. 56-XXXX	SANTIAGO ROAD OC RETAINING WALL					
X SIGN OFF DATE		CHECKED A.THURAIRAJAH	DATE 3/25/2020	PROJECT ENGINEER (ALAHESH) A. THURAIRAJAH, GE		POST MILE 4.1	LOG OF TEST BORINGS 1 OF 2					
GS GEOTECHNICAL LOG OF TEST BORINGS SHEET (ENGLISH) (REVISION 4/19/2018)				DATE PLOTTED => \$DATE FILE => \$REQUEST	TIME PLOTTED => \$TIME USERNAME => \$USER	ORIGINAL SCALE IN INCHES FOR REDUCED PLANS	UNIT: X PROJECT NUMBER & PHASE: 0820000074	CONTRACT No.: X	DISREGARD PRINTS BEARING EARLIER REVISION DATES	REVISION DATES	SHEET 10	OF 11


FIELD STUDY	By J.E. K. 11/13/70
DRAWN	By J.E. K. 11/13/70
CHECKED	By J.E. K. 11/13/70
APPROVED	By J.E. K. 11/13/70

BRIDGE DEPARTMENT
ENGINEERING GEOLOGY SECTION


LEGEND OF EARTH MATERIALS	
GRAVEL	SILTY CLAY OR CLAYEY SILT
SAND	PEAT AND/OR ORGANIC MATTER
SILT	FILL MATERIAL
CLAY	IGNEOUS ROCK
SANDY CLAY OR CLAYEY SAND	SEDIMENTARY ROCK
SANDY SILT OR SILTY SAND	METAMORPHIC ROCK

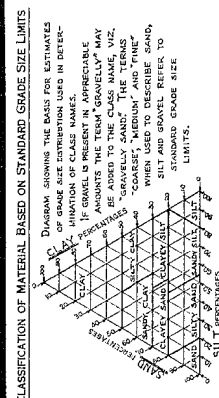

NOTE: Classification of earth material as shown on this sheet is based upon field inspection and is not to be construed to imply mechanical analysis.

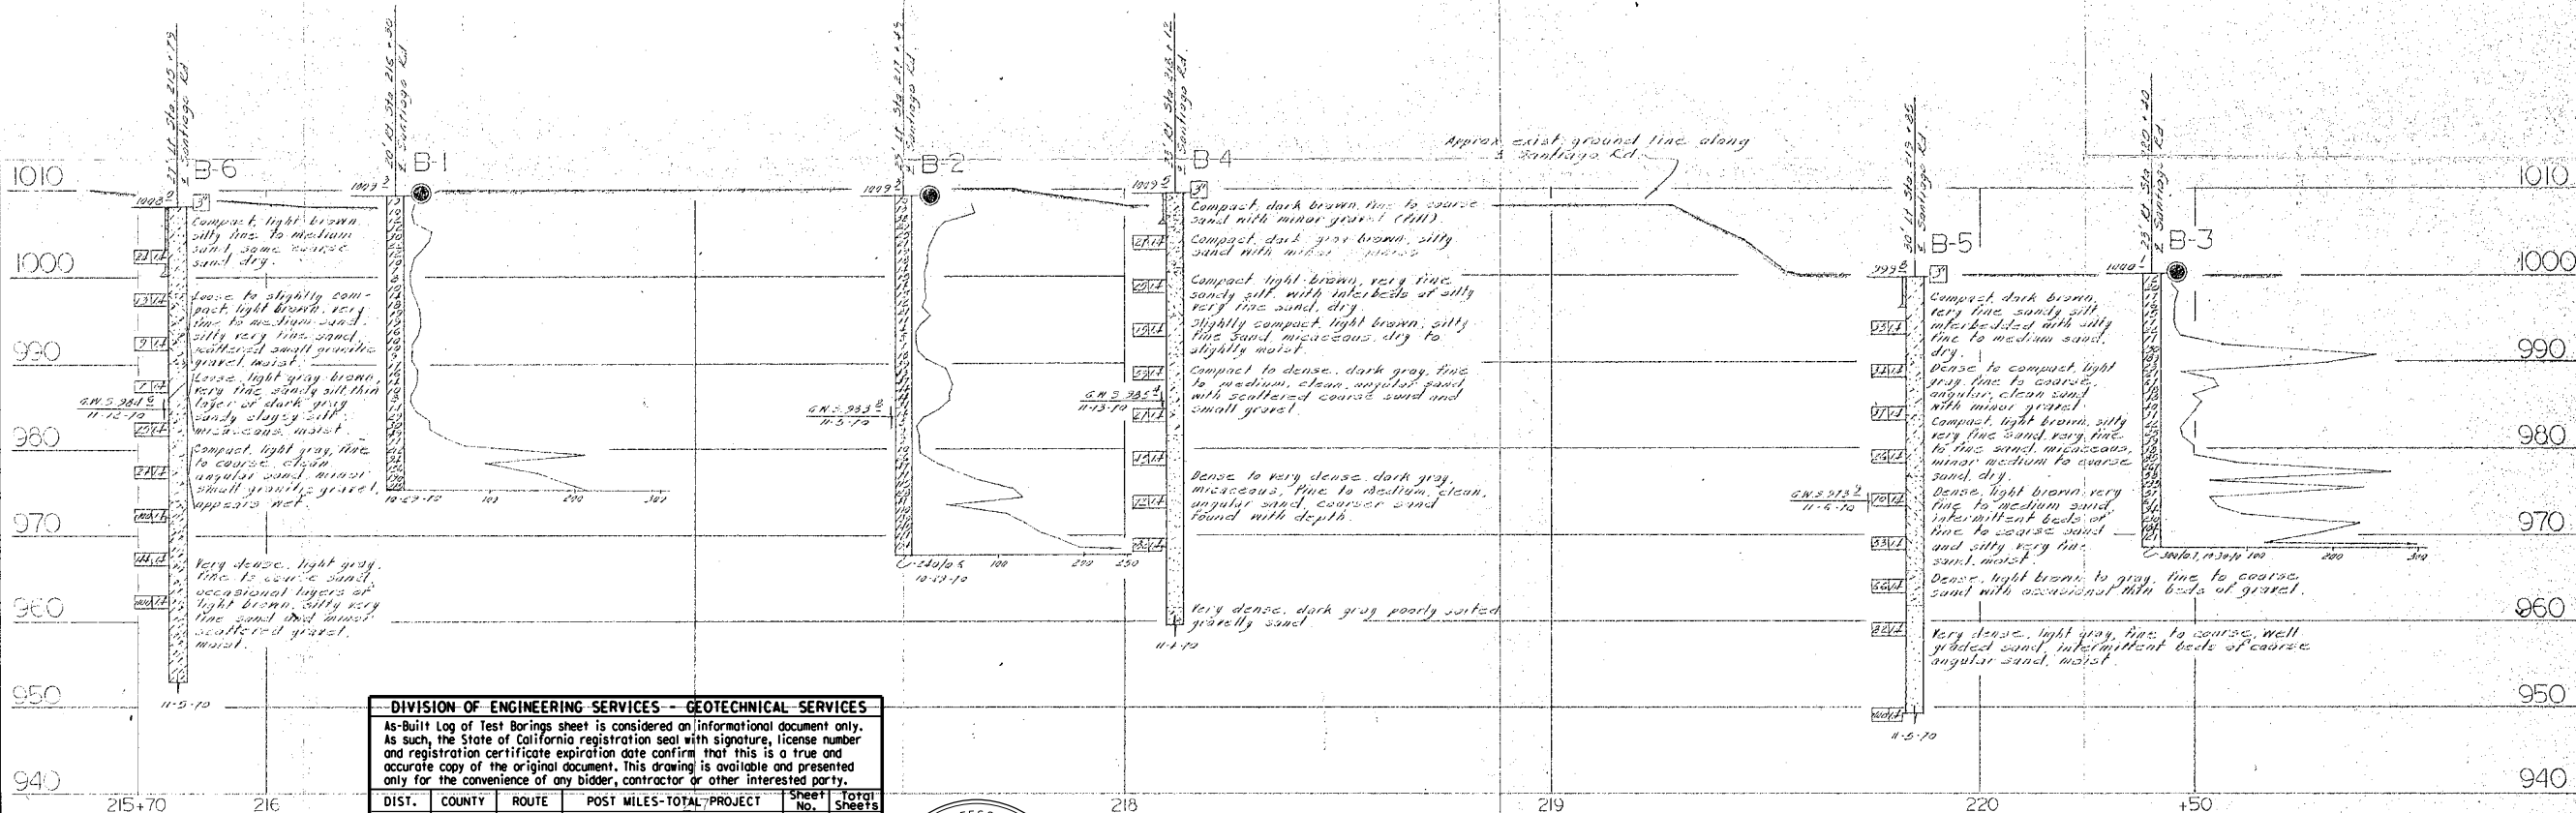

DIVISION OF ENGINEERING SERVICES - GEOTECHNICAL SERVICES					
As-Built Log of Test Borings sheet is considered an informational document only. As such, the State of California registration seal with signature, license number and registration certificate expiration date confirm that this is a true and accurate copy of the original document. This drawing is available and presented only for the convenience of any bidder, contractor or other interested party.					
DIST.	COUNTY	ROUTE	POST MILES-TOTAL PROJECT	Sheet No.	Total Sheets
8	RIV	15	R3.4/5.0		
GEOTECHNICAL PROFESSIONAL			DATE		
SANTIAGO ROAD OC RETAINING WALL			LOG OF TEST BORINGS 2 OF 2		
NOTE: A COPY OF THIS LOG OF TEST BORINGS IS AVAILABLE AT OFFICE OF STRUCTURE MAINTENANCE AND INVESTIGATIONS, SACRAMENTO, CALIFORNIA					
UNIT: X			PROJECT NUMBER & PHASE: 0820000074		
BRIDGE No.	Sheet	of			
56-XXXX	11	11			

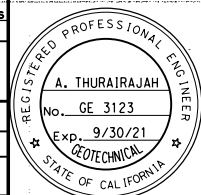

STATE OF CALIFORNIA TRANSPORTATION AGENCY DEPARTMENT OF PUBLIC WORKS DIVISION OF HIGHWAYS			
SANTIAGO ROAD OVERCROSSING			
LOG OF TEST BORINGS			
BRIDGE NO.	POST MILE	DRAWING NO.	SHEET OF
56-654	40		11
REVISION DATES (PRELIMINARY STAGE ONLY)			

WO 133201
CU 08203

Discard prints bearing earlier revision dates