


ELEVATION ALONG "SR" LINE
1" = 20'

LEGEND:

 Indicates pedestrian walkway on platform around stairs and ramps

NOTE:
For "SECTION A-A" and "SECTION B-B"
see "TUNNEL PLATFORM GP No. 2" sheet.

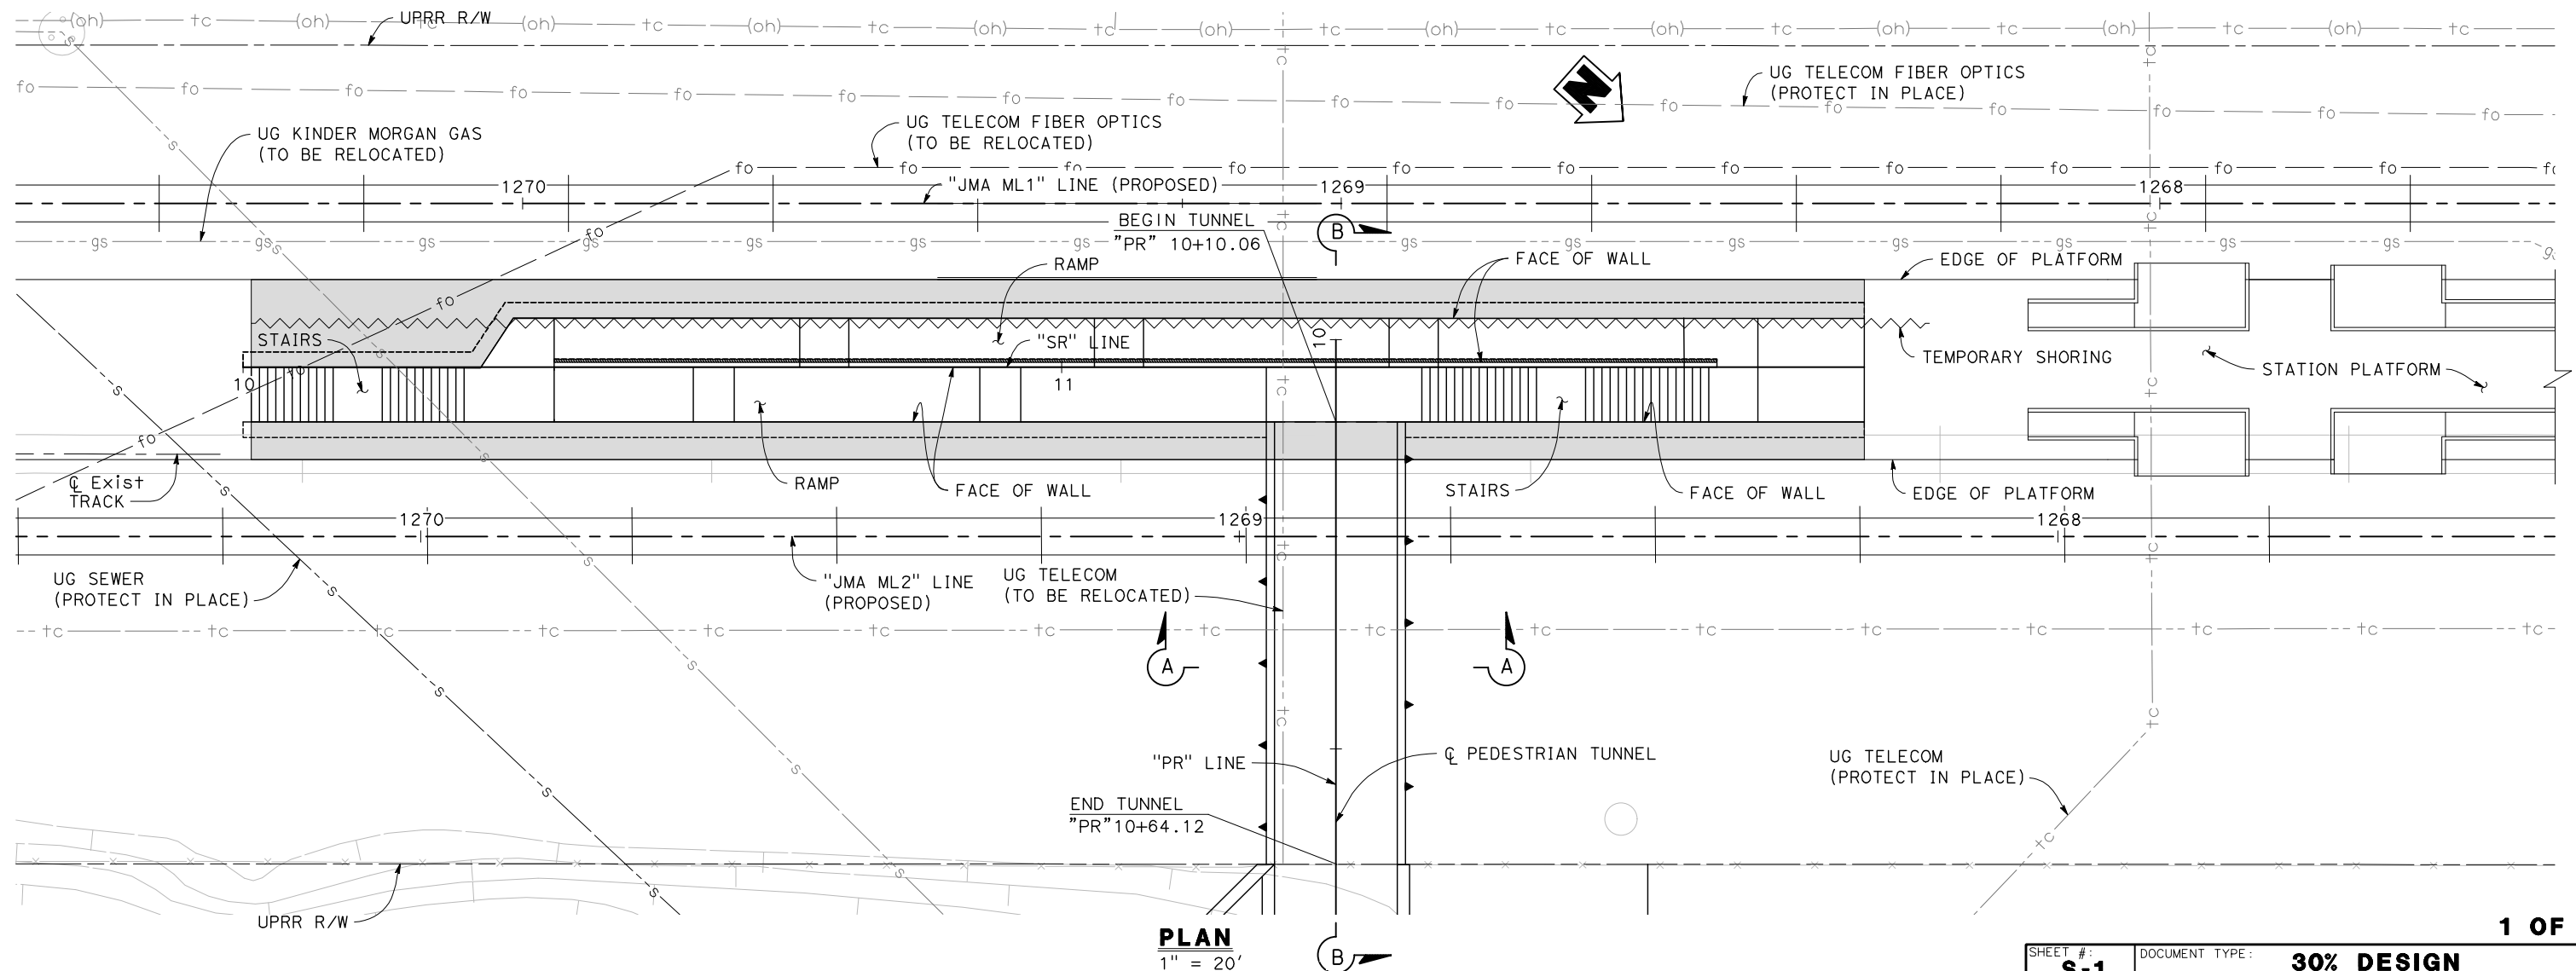


PLAN
1" = 20'

1 OF 3


REV. #	BY	DATE	DESCRIPTION




SHEET #: S-1	DOCUMENT TYPE: 30% DESIGN
DRAWN BY: JD	UNION PACIFIC RAILROAD For Use in Agreement with: ACE
CHECKED BY: EF/YR	LOCATION & DESCRIPTION: Ceres, Stanislaus County, CA - Fresno Sub MP 114 to 117 ACE Track Improvement And Ceres Station Project Latitude: 37°35'27"W; Longitude: 120°57'24"W
DATE: 12/14/21	SHEET TITLE: TUNNEL AND PLATFORM GP No. 1
PAGE NUMBER of XX	

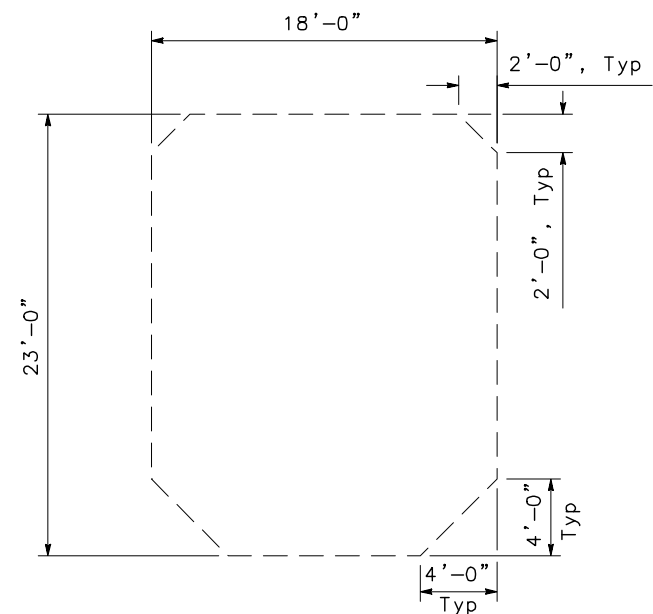

PERMANENT CLEARANCE ZONE
NO SCALE

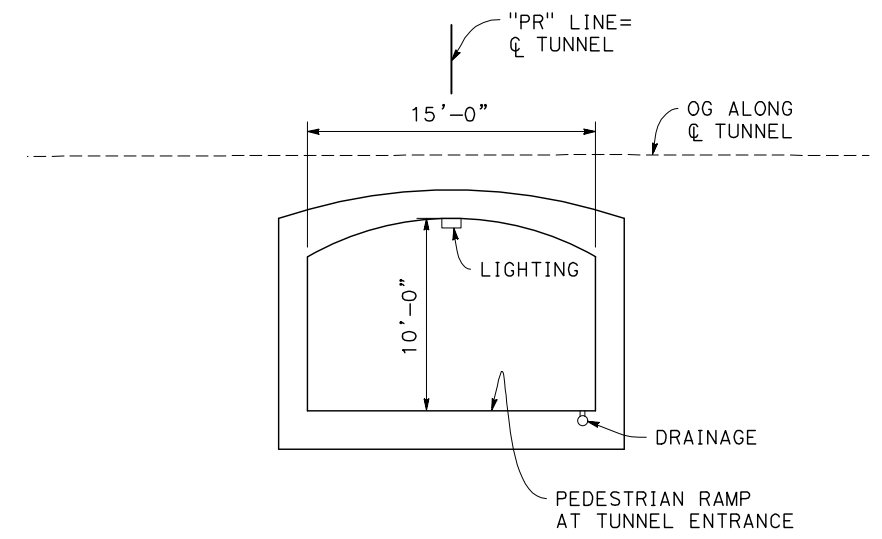

SECTION A-A
1" = 5'

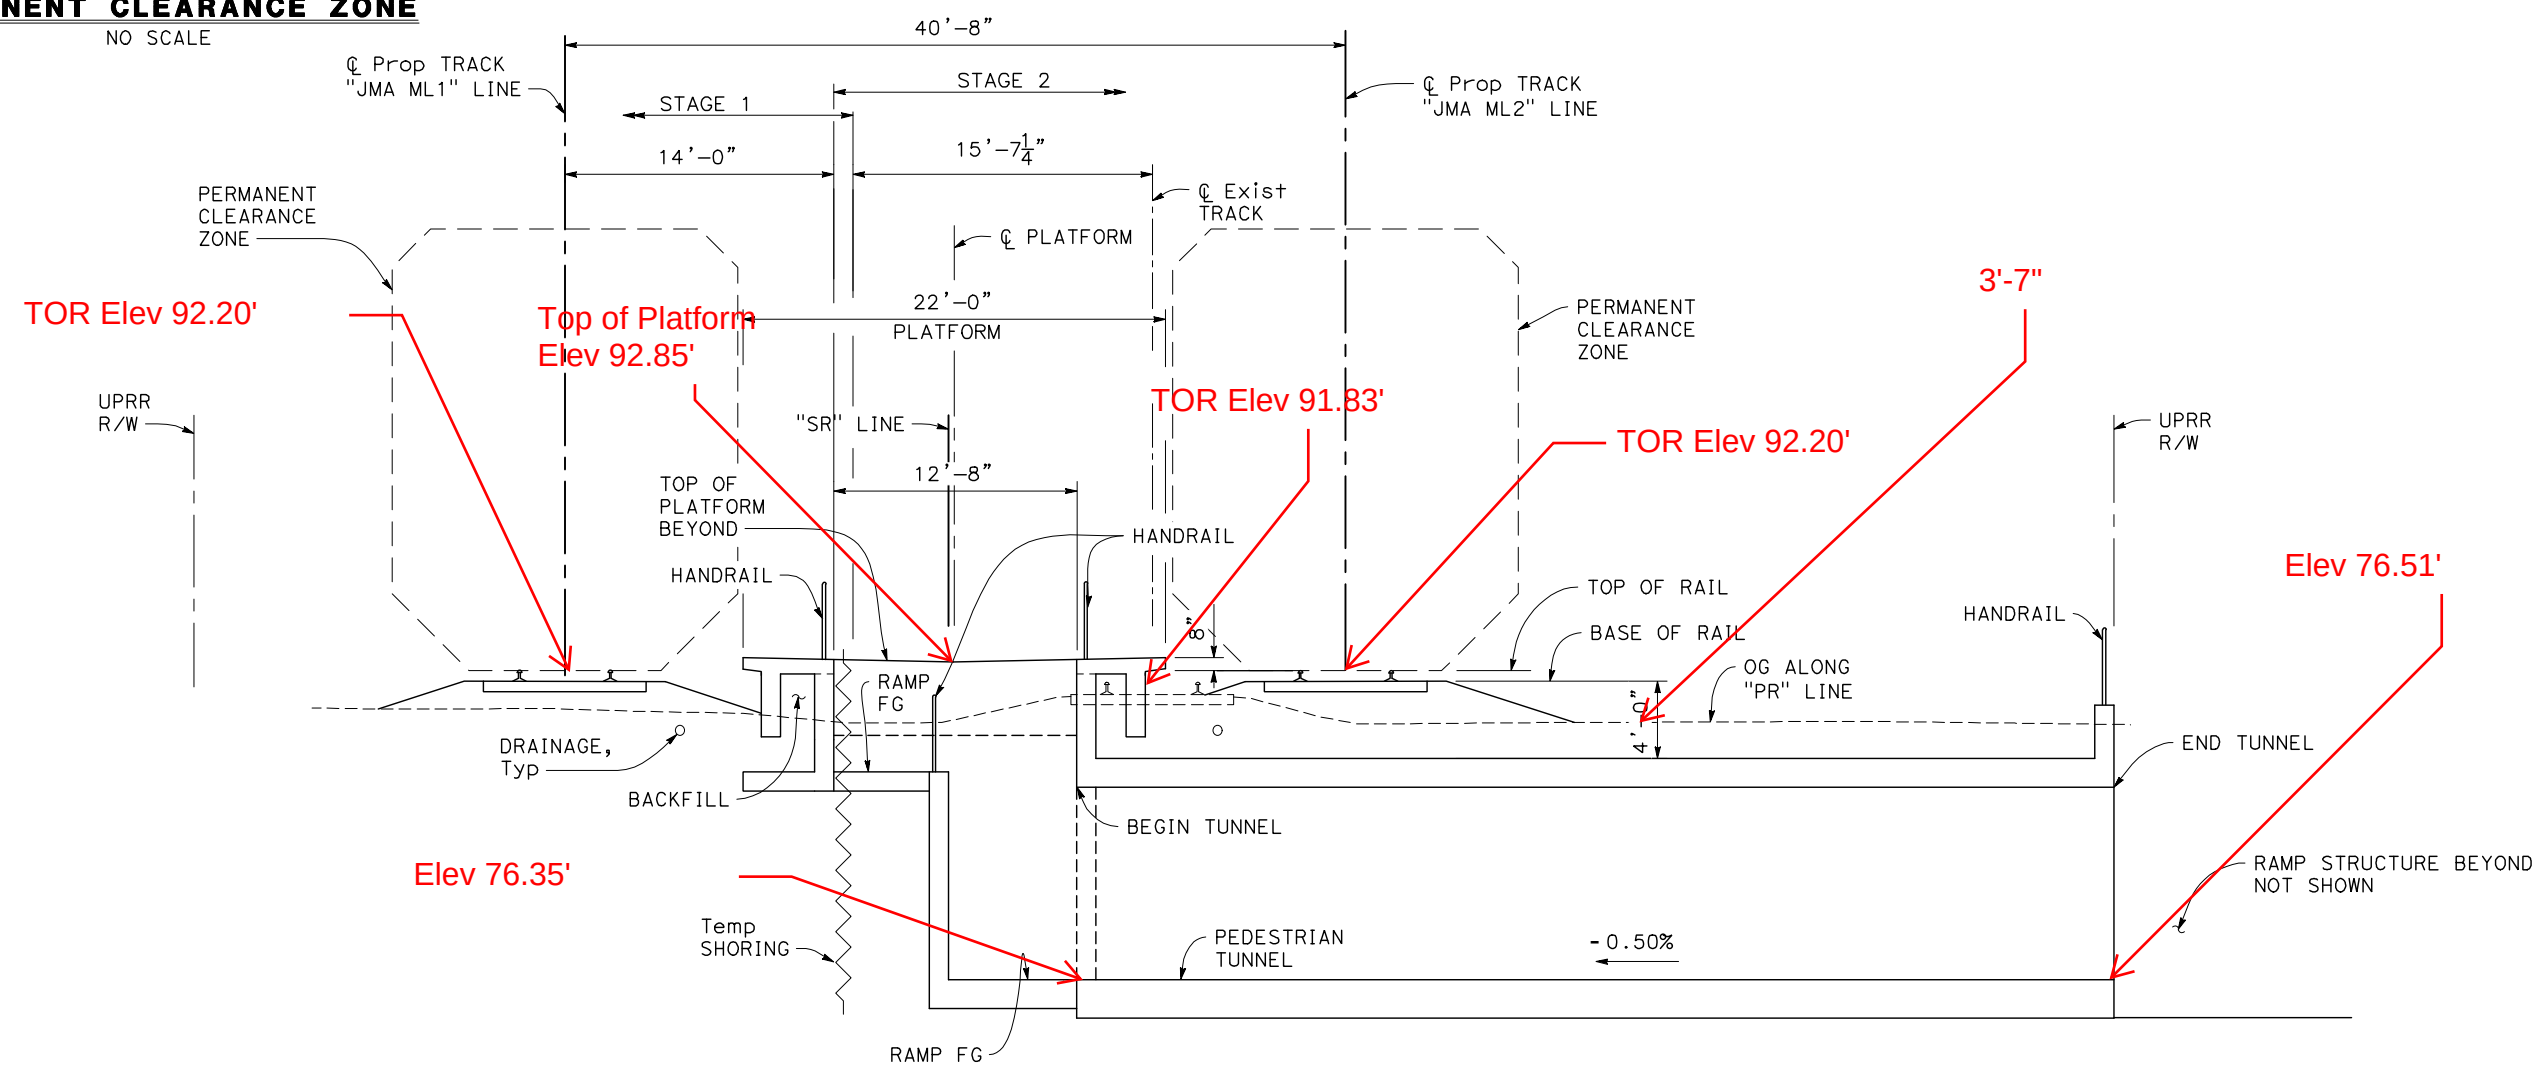

SECTION B-B
1" = 5'

REV. #	BY	DATE	DESCRIPTION



CALL BEFORE YOU DIG



CAUTION
Overhead
Power
Lines



ALTAHONT CORRIDOR EXPRESS



MARK THOMAS



SHEET #:	S-2	DOCUMENT TYPE:	30% DESIGN
DRAWN BY:	JD	UNION PACIFIC RAILROAD For Use in Agreement with: ACE	
CHECKED BY:	EF/YR	LOCATION & DESCRIPTION: Ceres, Stanislaus County, CA – Fresno Sub MP 114 to 117 ACE Track Improvement And Ceres Station Project Latitude: 37°35'27"W; Longitude: 120°57'24"W	
DATE:	12/14/21	SHEET TITLE: TUNNEL AND PLATFORM GP No. 2	
PAGE NUMBER	of XX		

GENERAL NOTES

1. Railroad requires review and approval of all submittals for shoring, demolition, erection and falsework. No work shall be allowed prior to written railroad approval. Allow a minimum of 45 days for the review and approval of each submittal unless specified otherwise in the contract special provisions.
2. The elevation of the existing top-of-rail profile shall be verified before beginning construction. All discrepancies shall be brought to the railroad authority for approval prior to beginning any construction activities.
3. The contractor must submit a proposed method of erosion and sediment control within the railroad Right-Of-Way and have the method approved by the railroad.
4. All shoring systems that impact the Railroad's operations and/or support the railroad's embankment shall be designed and constructed per current Railroad Guidelines for Temporary shoring.
5. All demolitions within the railroad Right-Of-Way and/or demolition that may impact the railroad's tracks or operations shall be in compliance wit the Railroad's Demolition Guidelines.
6. All construction phases that may impact the railroad's normal operation shall be designed to cause no interruption to the railroad operation. Any train traffic interruption closure shall require prior railroad approval in writing.
7. All permanent clearances shall be verified prior to completion of the project.
8. For all railroad coordination during construction refer to the railroad's special provisions within the Contract Special Provisions documents and the approved Construction and Maintenance (C & M) Agreement.
9. Railroad requirements do not allow work within 50 feet of track centerline when a train passes the work site and all personnel must clear the area within 25 feet of the track centerline and secure all equipment.
10. UPRR Monitoring Program and Contingency Plans must be submitted and approved prior to work.

CALTRANS STANDARD PLANS DATED 2018 EDITION

TBD

STANDARD PLAN SHEET No.

DETAIL No.

PLAN SYMBOLS

A

Indicates Section Identification

Indicates Temporary Shoring

ABBREVIATIONS

- Embed – Embedment
- UPRR – Union Pacific Railroad
- T/R – Top of Rail
- TOC – Top of Curb

GENERAL NOTES
LOAD AND RESISTANCE FACTOR DESIGN

DESIGN: AREMA Manual for Railway Engineering, 2019
UPRR-BNSF Guidelines for Railroad Grade Separation Projects, 2015
UPRR-BNSF Guidelines for Temporary Shoring, 2004

AASHTO LRFD Bridge Design Specifications, 8th Edition with California Amendments, preface dated April 2019.

LIVE LOADING: COOPER E-80

REINFORCED CONCRETE: $f_y = 60 \text{ ksi}$
 $f'_c = 4.0 \text{ ksi}$

UPRR-BNSF Guidelines for Railroad Grade Separation Projects, Section 6.2

BACKFILL: AREMA Manual for Railway Engineering, Chapter 8, Art. 16.2.3

CONSTRUCTION: AREMA Manual for Railway Engineering, Chapter 8, Art. 16.7


SHORING: Temporary shoring shall be in compliance with UPRR-BNSF Guidelines for Temporary Shoring, 2004, with updated shoring zone diagram including design variance.

INDEX TO PLANS

- S-1 TUNNEL & PLATFORM GP No. 1
- S-2 TUNNEL & PLATFORM GP No. 2
- S-3 INDEX TO PLANS

TOP OF RAIL ELEVATIONS

STATION	ELEVATIONS	
	JMA ML1	JMA ML2

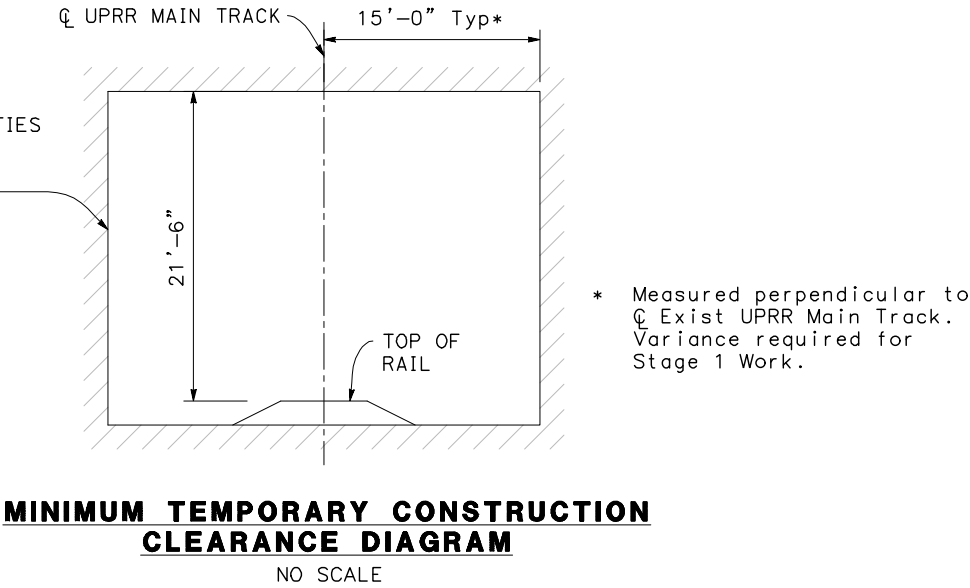

MINIMUM TEMPORARY CONSTRUCTION
CLEARANCE DIAGRAM

NO SCALE

REV. #	BY	DATE	DESCRIPTION

811

CALL BEFORE YOU DIG

CAUTION
Overhead
Power
Lines

ACE

ALTAMONT CORRIDOR EXPRESS

MARK THOMAS

UNION PACIFIC

SHEET #: S-2

DOCUMENT TYPE: 30% DESIGN

DRAWN BY: JD

CHECKED BY: EF/YR

DATE: 12/14/21

PAGE NUMBER of XX

UNION PACIFIC RAILROAD

For Use in Agreement with: ACE

LOCATION & DESCRIPTION:
Ceres, Stanislaus County, CA – Fresno Sub MP 114 to 117
ACE Track Improvement And Ceres Station Project
Latitude: 37°35'27"W; Longitude: 120°57'24"W

SHEET TITLE: INDEX TO PLANS